


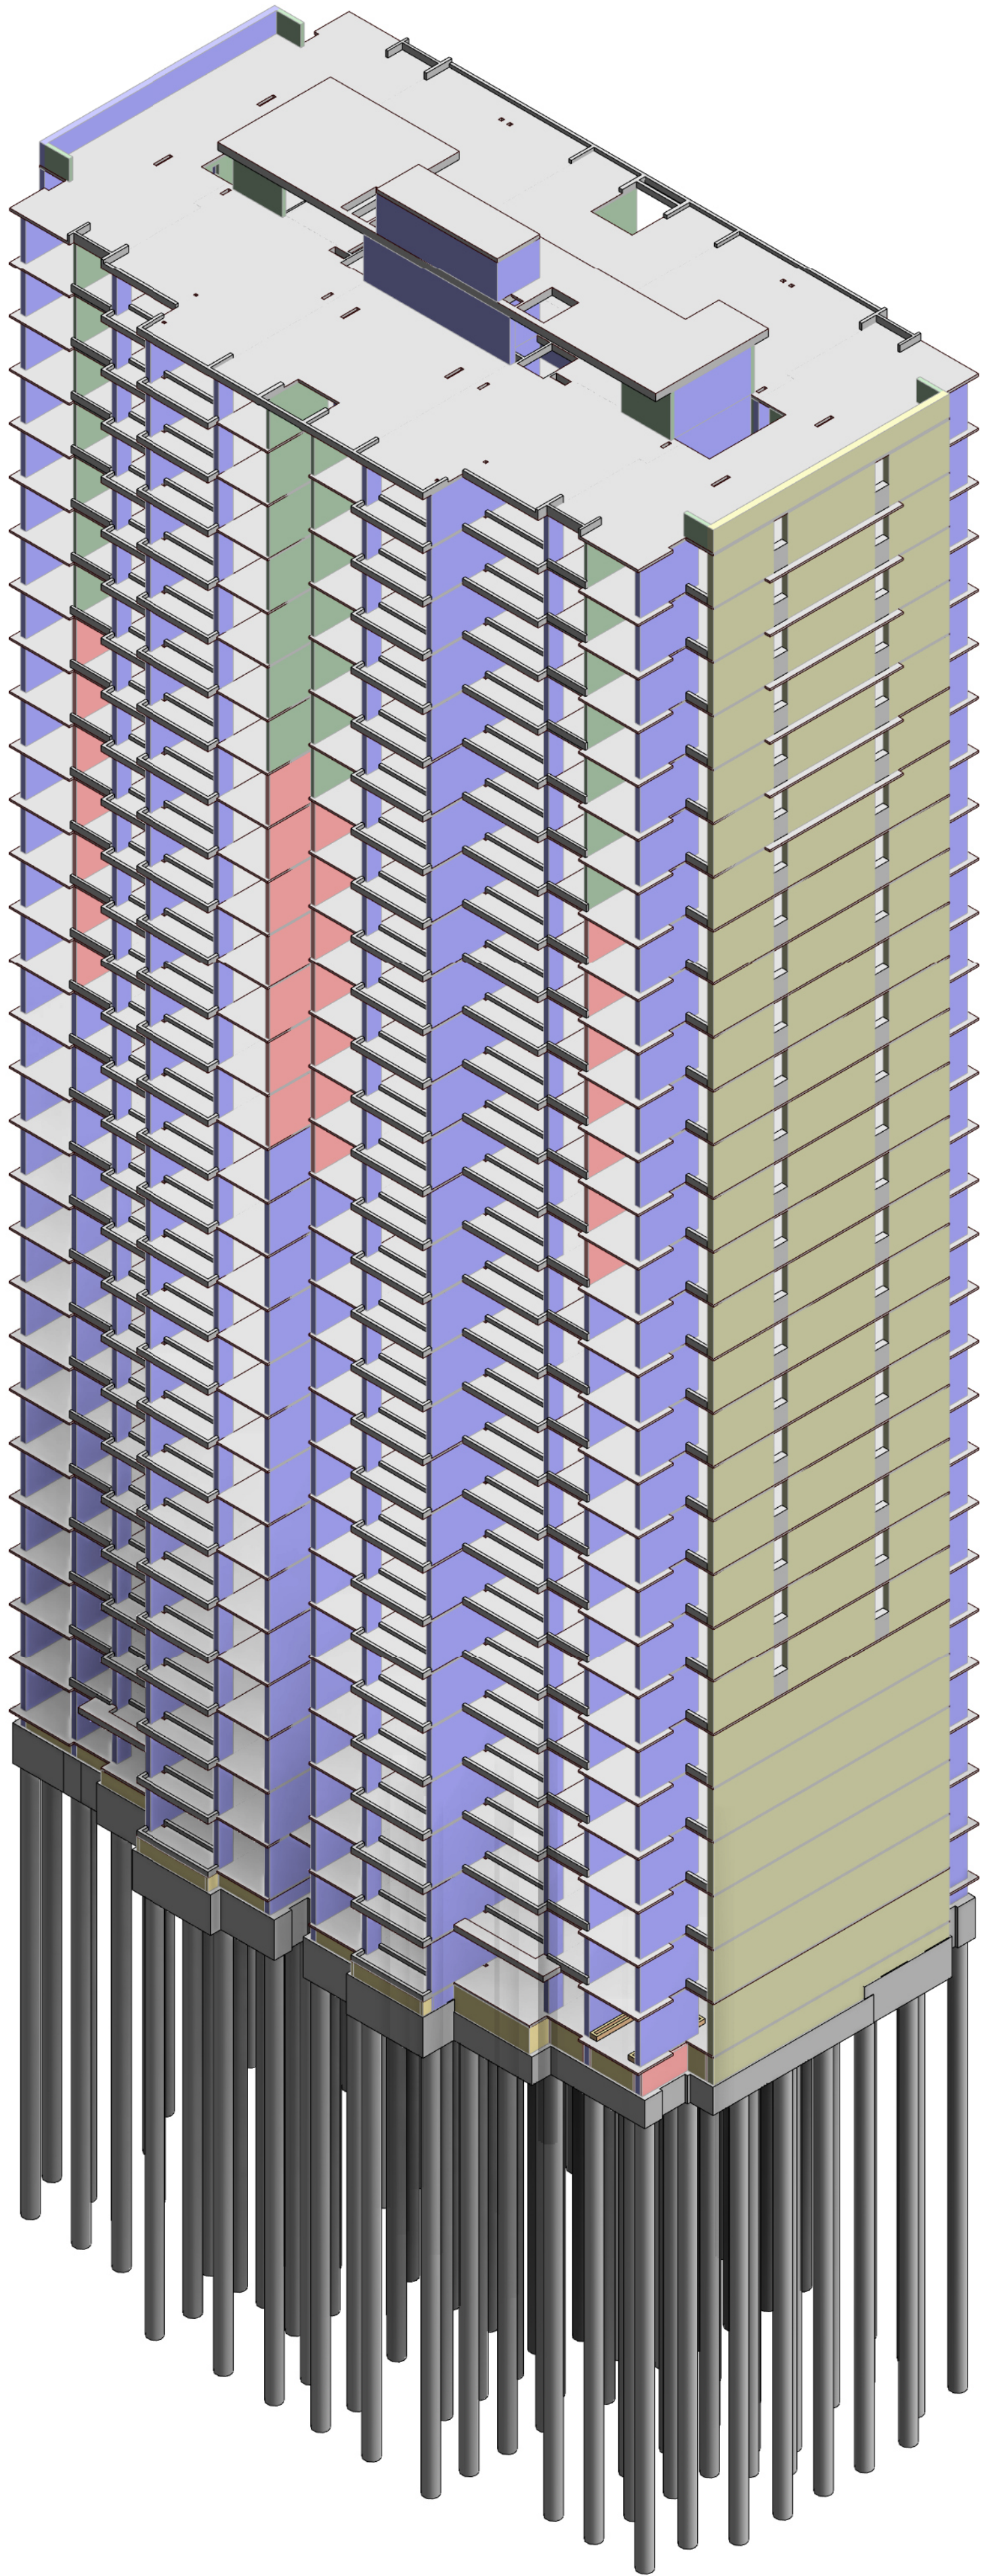

ESQUEMA 3D
Sin escala

ÍNDICE DE PLANOS ESTRUCTURALES			
PLANO N°	ARCHIVO DIGITAL	CONTENIDO	VERSIÓN
01.00	LA SCALA_EST_TOR-1_01.00_IND	ÍNDICE DE PLANOS	9
01.01	LA SCALA_EST_TOR-1_01.01_IND	CORTE LONGITUDINAL Y CUADRO DE ESPECIFICACIONES	2
01.02	LA SCALA_EST_TOR-1_01.02_DT-GEN	DETALLES GENERALES	2
02.00	LA SCALA_EST_TOR-1_02.00_LPL	PLANTA DE LOCALIZACIÓN DE PILOTES	6
02.01	LA SCALA_EST_TOR-1_02.01_DT-PL	DETALLES Y CUADRO DE PILOTES	3
03.00	LA SCALA_EST_TOR-1_03.00_LCM-CIM	PLANTA DE LOCALIZACIÓN DE MUROS CIMENTACIÓN	3
03.01	LA SCALA_EST_TOR-1_03.01_CIM	PLANTA DE CIMENTACIÓN	4
03.02	LA SCALA_EST_TOR-1_03.02_DT-CIM	CORTES Y DETALLES DE CIMENTACIÓN	3
03.03	LA SCALA_EST_TOR-1_03.03_LDAD	PLANTA DE LOCALIZACIÓN DE DADOS Y DETALLES	4
03.04	LA SCALA_EST_TOR-1_03.04_DT-FS	DESPIECE FOSO DE ASCENSORES	2
03.05	LA SCALA_EST_TOR-1_03.05_CIM-D1	DESPIECE VIGAS DE CIMENTACIÓN	3
03.06	LA SCALA_EST_TOR-1_03.06_CIM-D2	DESPIECE VIGAS DE CIMENTACIÓN	3
03.07	LA SCALA_EST_TOR-1_03.07_CIM-D3	DESPIECE VIGAS DE CIMENTACIÓN	4
04.00	LA SCALA_EST_TOR-1_04.00_LCM-P1	PLANTA LOCALIZACIÓN DE MUROS PISO 1	2
04.01	LA SCALA_EST_TOR-1_04.01_LDINT-P1	PLANTA LOCALIZACIÓN E IDENTIFICACIÓN DE DINTELES PISO 1	2
04.02	LA SCALA_EST_TOR-1_04.02_P1-RADC	PLANTA DE REFUERZO ADICIONAL PISO 1	2
04.03	LA SCALA_EST_TOR-1_04.03_P1-RINF	PLANTA DE REFUERZO INFERIOR PISO 1	2
04.04	LA SCALA_EST_TOR-1_04.04_P1-RSUP	PLANTA DE REFUERZO SUPERIOR PISO 1	2
05.00	LA SCALA_EST_TOR-1_05.00_LCM-P2	PLANTA LOCALIZACIÓN DE MUROS PISO 2	2
05.01	LA SCALA_EST_TOR-1_05.01_LDINT-P2	PLANTA LOCALIZACIÓN E IDENTIFICACIÓN DE DINTELES PISO 2	2
05.02	LA SCALA_EST_TOR-1_05.02_P2-RADC	PLANTA DE REFUERZO ADICIONAL PISO 2	2
05.03	LA SCALA_EST_TOR-1_05.03_P2-RINF	PLANTA DE REFUERZO INFERIOR PISO 2	2
05.04	LA SCALA_EST_TOR-1_05.04_P2-RSUP	PLANTA DE REFUERZO SUPERIOR PISO 2	2
06.00	LA SCALA_EST_TOR-1_06.00_LCM-PT1	PLANTA LOCALIZACIÓN DE MUROS PISO TIPO 1	2
06.01	LA SCALA_EST_TOR-1_06.01_LDINT-PT1	PLANTA LOCALIZACIÓN E IDENTIFICACIÓN DE DINTELES PISO TIPO 1 (PISO 3 A PISO 15)	2
06.02	LA SCALA_EST_TOR-1_06.02_PT1-RADC	PLANTA DE REFUERZO ADICIONAL PISO TIPO 1 (PISO 3 A 15)	2
06.03	LA SCALA_EST_TOR-1_06.03_PT1-RINF	PLANTA DE REFUERZO INFERIOR PISO TIPO 1 (PISO 3 A PISO 15)	2
06.04	LA SCALA_EST_TOR-1_06.04_PT1-RSUP	PLANTA DE REFUERZO SUPERIOR PISO TIPO 1 (PISO 3 A PISO 15)	2
07.00	LA SCALA_EST_TOR-1_07.00_LCM-PT2	PLANTA LOCALIZACIÓN DE MUROS PISO TIPO 2 (PISO 16 A PISO 21)	2
07.01	LA SCALA_EST_TOR-1_07.01_LDINT-PT2	PLANTA LOCALIZACIÓN E IDENTIFICACIÓN DE DINTELES PISO TIPO 2 (PISO 16 A PISO 22)	2
07.02	LA SCALA_EST_TOR-1_07.02_PT2-RADC	PLANTA DE REFUERZO ADICIONAL PISO TIPO 2 (PISO 16 A 22)	2
07.03	LA SCALA_EST_TOR-1_07.03_PT2-RINF	PLANTA DE REFUERZO INFERIOR PISO TIPO 2 (PISO 16 A PISO 22)	2
07.04	LA SCALA_EST_TOR-1_07.04_PT2-RSUP	PLANTA DE REFUERZO SUPERIOR PISO TIPO 2 (PISO 16 A PISO 22)	3
08.00	LA SCALA_EST_TOR-1_08.00_LCM-PT3	PLANTA LOCALIZACIÓN DE MUROS PISO TIPO 3 (PISO 22 A PISO PISO 28)	2
08.01	LA SCALA_EST_TOR-1_08.01_LDINT-PT3	PLANTA LOCALIZACIÓN E IDENTIFICACIÓN DE DINTELES PISO TIPO 3 (PISO 23 A PISO 28)	2
08.02	LA SCALA_EST_TOR-1_08.02_PT3-RADC	PLANTA DE REFUERZO ADICIONAL PISO TIPO 3 (PISO 23 A 28)	2
08.03	LA SCALA_EST_TOR-1_08.03_PT3-RINF	PLANTA DE REFUERZO INFERIOR PISO TIPO 3 (PISO 23 A PISO 28)	2
08.04	LA SCALA_EST_TOR-1_08.04_PT3-RSUP	PLANTA DE REFUERZO SUPERIOR PISO TIPO 3 (PISO 23 A PISO 28)	3
09.00	LA SCALA_EST_TOR-1_09.00_LCM-CUB	PLANTA LOCALIZACIÓN DE MUROS DE CUBIERTA	2
09.01	LA SCALA_EST_TOR-1_09.01_LDINT-CUB	PLANTA LOCALIZACIÓN E IDENTIFICACIÓN DE DINTELES DE CUBIERTA	2
09.02	LA SCALA_EST_TOR-1_09.02_CUB-RADC	PLANTA DE REFUERZO ADICIONAL CUBIERTA	2
09.03	LA SCALA_EST_TOR-1_09.03_CUB-RINF	PLANTA DE REFUERZO INFERIOR CUBIERTA	2
09.04	LA SCALA_EST_TOR-1_09.04_CUB-RSUP	PLANTA DE REFUERZO SUPERIOR- CUBIERTA N.E. 74 20	2
09.05	LA SCALA_EST_TOR-1_09.05_CUB-MAQ	PLANTA DE CUBIERTA ASCENSOR Y CUBIERTA DE ESCALERAS	2
10.00	LA SCALA_EST_TOR-1_10.00_DINT-D1	DESPIECE DE DINTELES	2
10.01	LA SCALA_EST_TOR-1_10.01_DINT-D2	DESPIECE DE DINTELES	2
10.02	LA SCALA_EST_TOR-1_10.02_DINT-D3	DESPIECE DE DINTELES	2
10.03	LA SCALA_EST_TOR-1_10.03_DINT-D4	DESPIECE DE DINTELES	2
10.04	LA SCALA_EST_TOR-1_10.04_DINT-D5	DESPIECE DE DINTELES	2
11.00	LA SCALA_EST_TOR-1_11.00_MUR-D1	DESPIECE DE MUROS	3
11.01	LA SCALA_EST_TOR-1_11.01_MUR-D2	DESPIECE DE MUROS	3
11.02	LA SCALA_EST_TOR-1_11.02_MUR-D3	DESPIECE DE MUROS	4
11.03	LA SCALA_EST_TOR-1_11.03_MUR-D4	DESPIECE DE MUROS	4
11.04	LA SCALA_EST_TOR-1_11.04_MUR-D5	DESPIECE DE MUROS	3
11.05	LA SCALA_EST_TOR-1_11.05_MUR-D6	DESPIECE DE MUROS	3
11.06	LA SCALA_EST_TOR-1_11.06_MUR-D7	DESPIECE DE MUROS	3
11.07	LA SCALA_EST_TOR-1_11.07_MUR-D8	DESPIECE DE MUROS	3
11.08	LA SCALA_EST_TOR-1_11.08_MUR-D9	DESPIECE DE MUROS	3
11.09	LA SCALA_EST_TOR-1_11.09_MUR-D10	DESPIECE DE MUROS	3
11.10	LA SCALA_EST_TOR-1_11.10_MUR-D11	DESPIECE DE MUROS	3
11.11	LA SCALA_EST_TOR-1_11.11_MUR-D12	DESPIECE DE MUROS	3
11.12	LA SCALA_EST_TOR-1_11.12_MUR-D13	DESPIECE DE MUROS	3
11.13	LA SCALA_EST_TOR-1_11.13_MUR-D14	DESPIECE DE MUROS	3
11.14	LA SCALA_EST_TOR-1_11.14_MUR-D15	DESPIECE DE MUROS	4
11.15	LA SCALA_EST_TOR-1_11.15_MUR-D16	DESPIECE DE MUROS	3
11.16	LA SCALA_EST_TOR-1_11.16_MUR-D17	DESPIECE DE MUROS	3
11.17	LA SCALA_EST_TOR-1_11.17_MUR-D18	DESPIECE DE MUROS	3
11.18	LA SCALA_EST_TOR-1_11.18_MUR-D19	DESPIECE DE MUROS	3
11.19	LA SCALA_EST_TOR-1_11.19_MUR-D20	DESPIECE DE MUROS	3
11.20	LA SCALA_EST_TOR-1_11.20_MUR-D21	DESPIECE DE MUROS	3
11.21	LA SCALA_EST_TOR-1_11.21_MUR-D22	DESPIECE DE MUROS	3
11.22	LA SCALA_EST_TOR-1_11.22_DT-MUR	DETALLES DE MUROS	1
12.00	LA SCALA_EST_TOR-1_12.00_ESC-2	DESPIECE ESCALERA TIPO 1 (PISO 1 A 2)	2
12.01	LA SCALA_EST_TOR-1_12.01_ESC-2	DESPIECE ESCALERA TIPO 2 (PISO 1 A 2)	2
12.02	LA SCALA_EST_TOR-1_12.02_ESC-1	DESPIECE ESCALERAS TIPO 1 Y 2 (PISO 3 A 28)	2
12.03	LA SCALA_EST_TOR-1_12.03_ESC-1	DESPIECE ESCALERA TIPO 1 Y 2 (PISO 28 A CUBIERTA)	2
13.00	LA SCALA_EST_TOR-1_13.00_DT-NOES	DETALLES NOES	1



GERENTE DE PROYECTO

ROBERTO AYCARDI F.
MAT. 2520257258 CND

INGENIERO

CARLOS ANDRÉS WILCHES C.

MODELADOR

DANIEL CASTELLANOS

MODIFICACIONES	FECHA
Se actualiza índice de planos	31-07-2025
Se actualiza índice de planos	03-10-2025
Se actualiza índice de planos	04-11-2025
Se actualiza índice de planos	29-01-2026
Se actualiza índice de planos	16-02-2026
Se actualiza índice de planos	26-02-2026
Se actualiza índice de planos	18-06-2026



LA SCALA

LA SCALA_EST_TOR-1

TORRE 1

CALLE 170 CON AV. BOYACA

ÍNDICE DE PLANOS

LA SCALA_EST_TOR-1_01.00_IND

REVISOR ESTRUCTURAL

RAMÓN ÁNDRES ALVAREZ MANTILLA
MAT. 25202-346546 CND.