



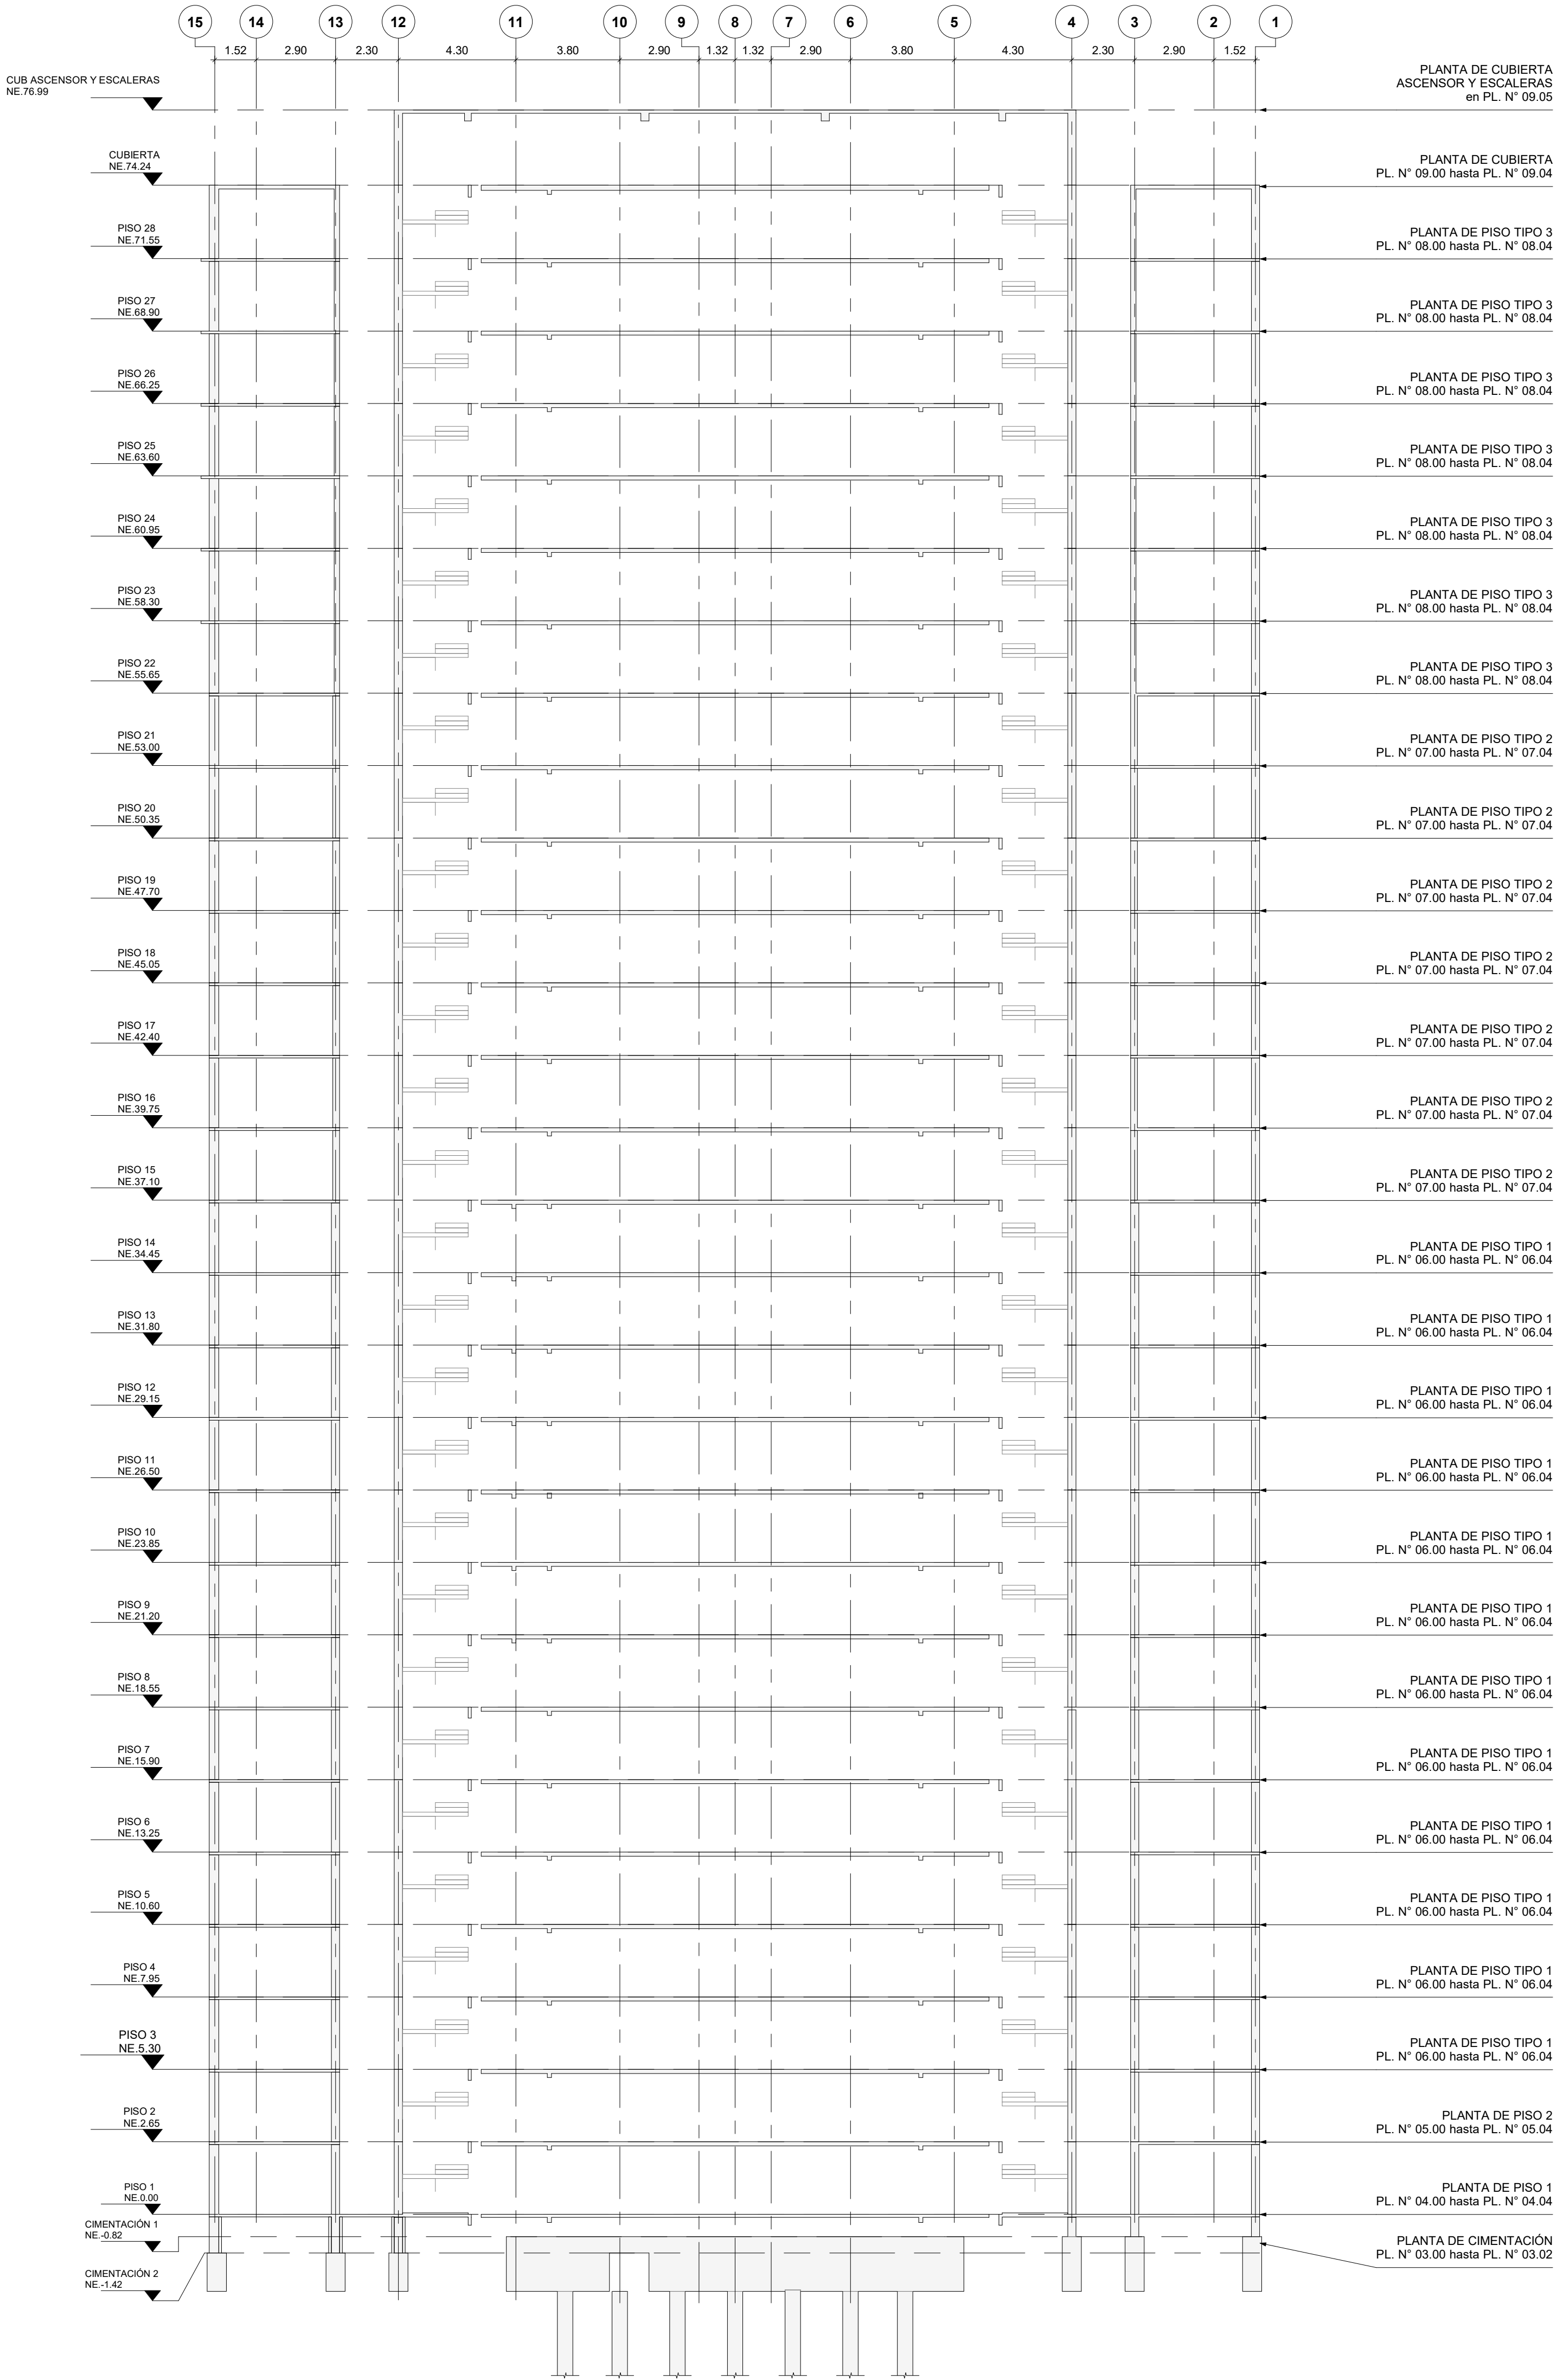

CORTE LONGITUDINAL
Escala 1 : 150

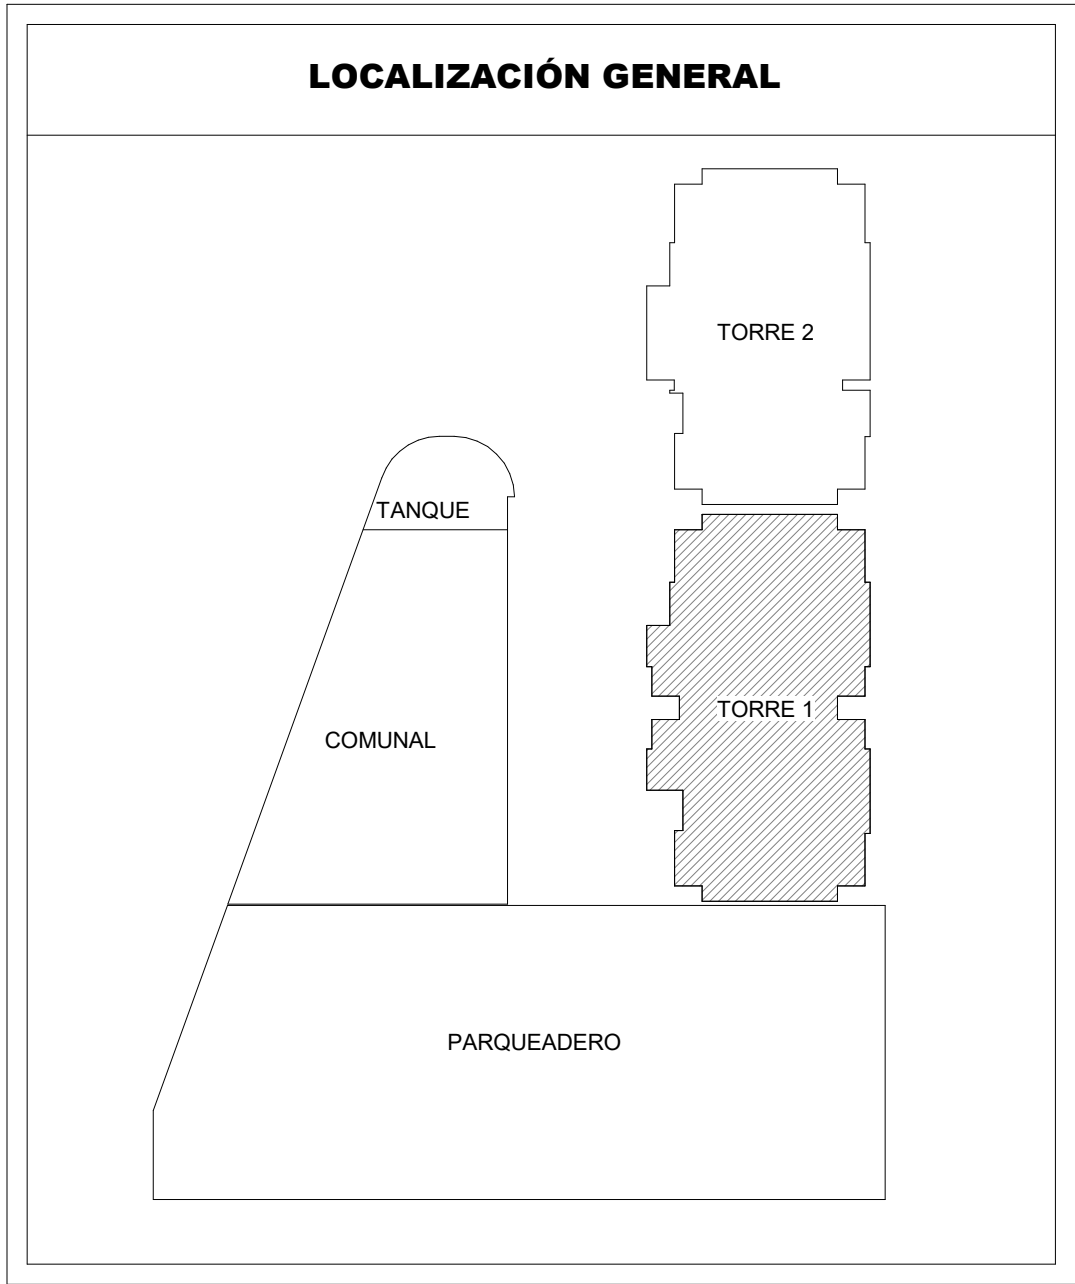

CUADRO DE ESPECIFICACIONES			
MATERIALES:		CARGAS:	
f'c= 280 kg/cm²	28 MPa Pilotes	MUERTAS:	
f'c= 350 kg/cm²	35 MPa Vigas de Cimentación	Acabados - Piso 1 a Cubierta	100 kg/m² 1.0 kN/m²
f'c= 210 kg/cm²	21 MPa Muretes	Muros no estructurales - Piso 1	131 kg/m² 1.3 kN/m²
		Muros no estructurales - Piso 2 a Piso 28	121 kg/m² 1.2 kN/m²
		Muros no estructurales - Cubierta	26 kg/m² 0.3 kN/m²
f'c= 350 kg/cm²	35 MPa Losas y dinteles de Piso 1 a Piso 8	VIVAS:	
f'c= 315 kg/cm²	32 MPa Losas y dinteles de Piso 9 a Piso 15	Residencial - Cuartos privados y sus corredores	180 kg/m² 1.8 kN/m²
f'c= 245 kg/cm²	25 MPa Losas y dinteles de Piso 16 a Piso 22	Cubierta con acceso al público	500 kg/m² 5.0 kN/m²
f'c= 210 kg/cm²	21 MPa Losas y dinteles de Piso 23 a Cubierta del ascensor y escaleras	Cubierta - Con acceso limitado	180 kg/m² 1.8 kN/m²
		Residencial -Escaleras	300 kg/m² 3.0 kN/m²
		Balcones	500 kg/m² 5.0 kN/m²
f'c= 490 kg/cm²	49 MPa Muros y vigas de acople de Cimentación a Piso 8		
f'c= 420 kg/cm²	42 MPa Muros y vigas de acople de Piso 8 a Piso 15		
f'c= 350 kg/cm²	35 MPa Muros y vigas de acople de Piso 15 a Piso 22		
f'c= 280 kg/cm²	28 MPa Muros y vigas de acople de Piso 22 a Cubierta del ascensor y escaleras		
f'c= 210 kg/cm²	21 MPa Escaleras		
fy= 4200 kg/cm²	420 MPa Varillas de refuerzo (NTC 2289)		
fy= 4200 kg/cm²	420 MPa Malla electrosoldada placas (NTC 5806)		
SISTEMA DE RESISTENCIA SÍSMICA:		GRUPO DE USO:	
MUROS DE CONCRETO (DES)	R _o = 5.0 (Según NSR-10)	GRUPO DE USO	I I = 1.0
IRREGULARIDAD EN PLANTA	R= 5.0		
IRREGULARIDAD EN ALTURA	Ø _p = 1.00		
AUSENCIA DE REDUNDANCIA	Ø _a = 1.00		
	Ø _r = 1.00		
ZONA DE AMENAZA SÍSMICA:	INTERMEDIA	PROTECCIÓN CONTRA FUEGO NSR-10	
MICROZONIFICACIÓN SÍSMICA DE BOGOTÁ (PROMEDIO) :	PIEDEMONTA A	CLASIFICACIÓN:	R1 De acuerdo con K.2.1-1
		CATEGORIZACIÓN:	I De acuerdo con J.3.3-1
		RESISTENCIA AL FUEGO:	1 Hora De acuerdo con J.3.4-4
A _a = 0.15	F _a = 1.65		
A _v = 0.20	F _v = 2.00		
	T _C = 0.78		
	T _L = 3.00		
	LACUSTRE 50		
A _a = 0.15	F _a = 1.40		
A _v = 0.20	F _v = 2.90		
	T _C = 1.33		
	T _L = 4.00		
CARACTERÍSTICAS DE LA ESTRUCTURA:		ESTUDIO DE SUELOS:	
TIPO DE CIMENTACIÓN	PILOTES PRE-EXCAVADOS Y FUNDICIÓN IN SITU	LA CIMENTACIÓN SIGUE LAS RECOMENDACIONES DE LA FIRMA	Alfonso Uribe S. y Cia. S.A.
PLACA ENTREPISOS	LOSA MACIZA	N° ESTUDIO DE SUELOS	AUS-13071-7-1
SISTEMA ESTRUCTURAL	MUROS DE CONCRETO (DES)		
		TIPO DE SUELO:	
		Suelo caracterizado como tipo: (Según estudio de suelos)	F (Según NSR-10)

MODIFICACIONES		FECHA
Emisión Inicial	Actualización cuadro de especificaciones	28-02-2025 03-10-2025



LA SCALA

LA SCALA_EST_TOR-1

TORRE 1

CALLE 170 CON AV. BOYACA

CORTE LONGITUDINAL Y CUADRO DE ESPECIFICACIONES

LA SCALA_EST_TOR-1_01.01_IND

REVISOR ESTRUCTURAL
RAMÓN ÁNDRES ALVAREZ MANTILLA
MAT. 25202-346546 CND.

PLANO N° VERSIÓN :

01.01

2

PLANO N° 01.01

VERSIÓN : 2



GERENTE DE PROYECTO
ROBERTO AYCARDI F.
MAT. 2520257258 CND

INGENIERO
CARLOS ANDRÉS WILCHES C.

MODELADOR
DANIEL CASTELLANOS