


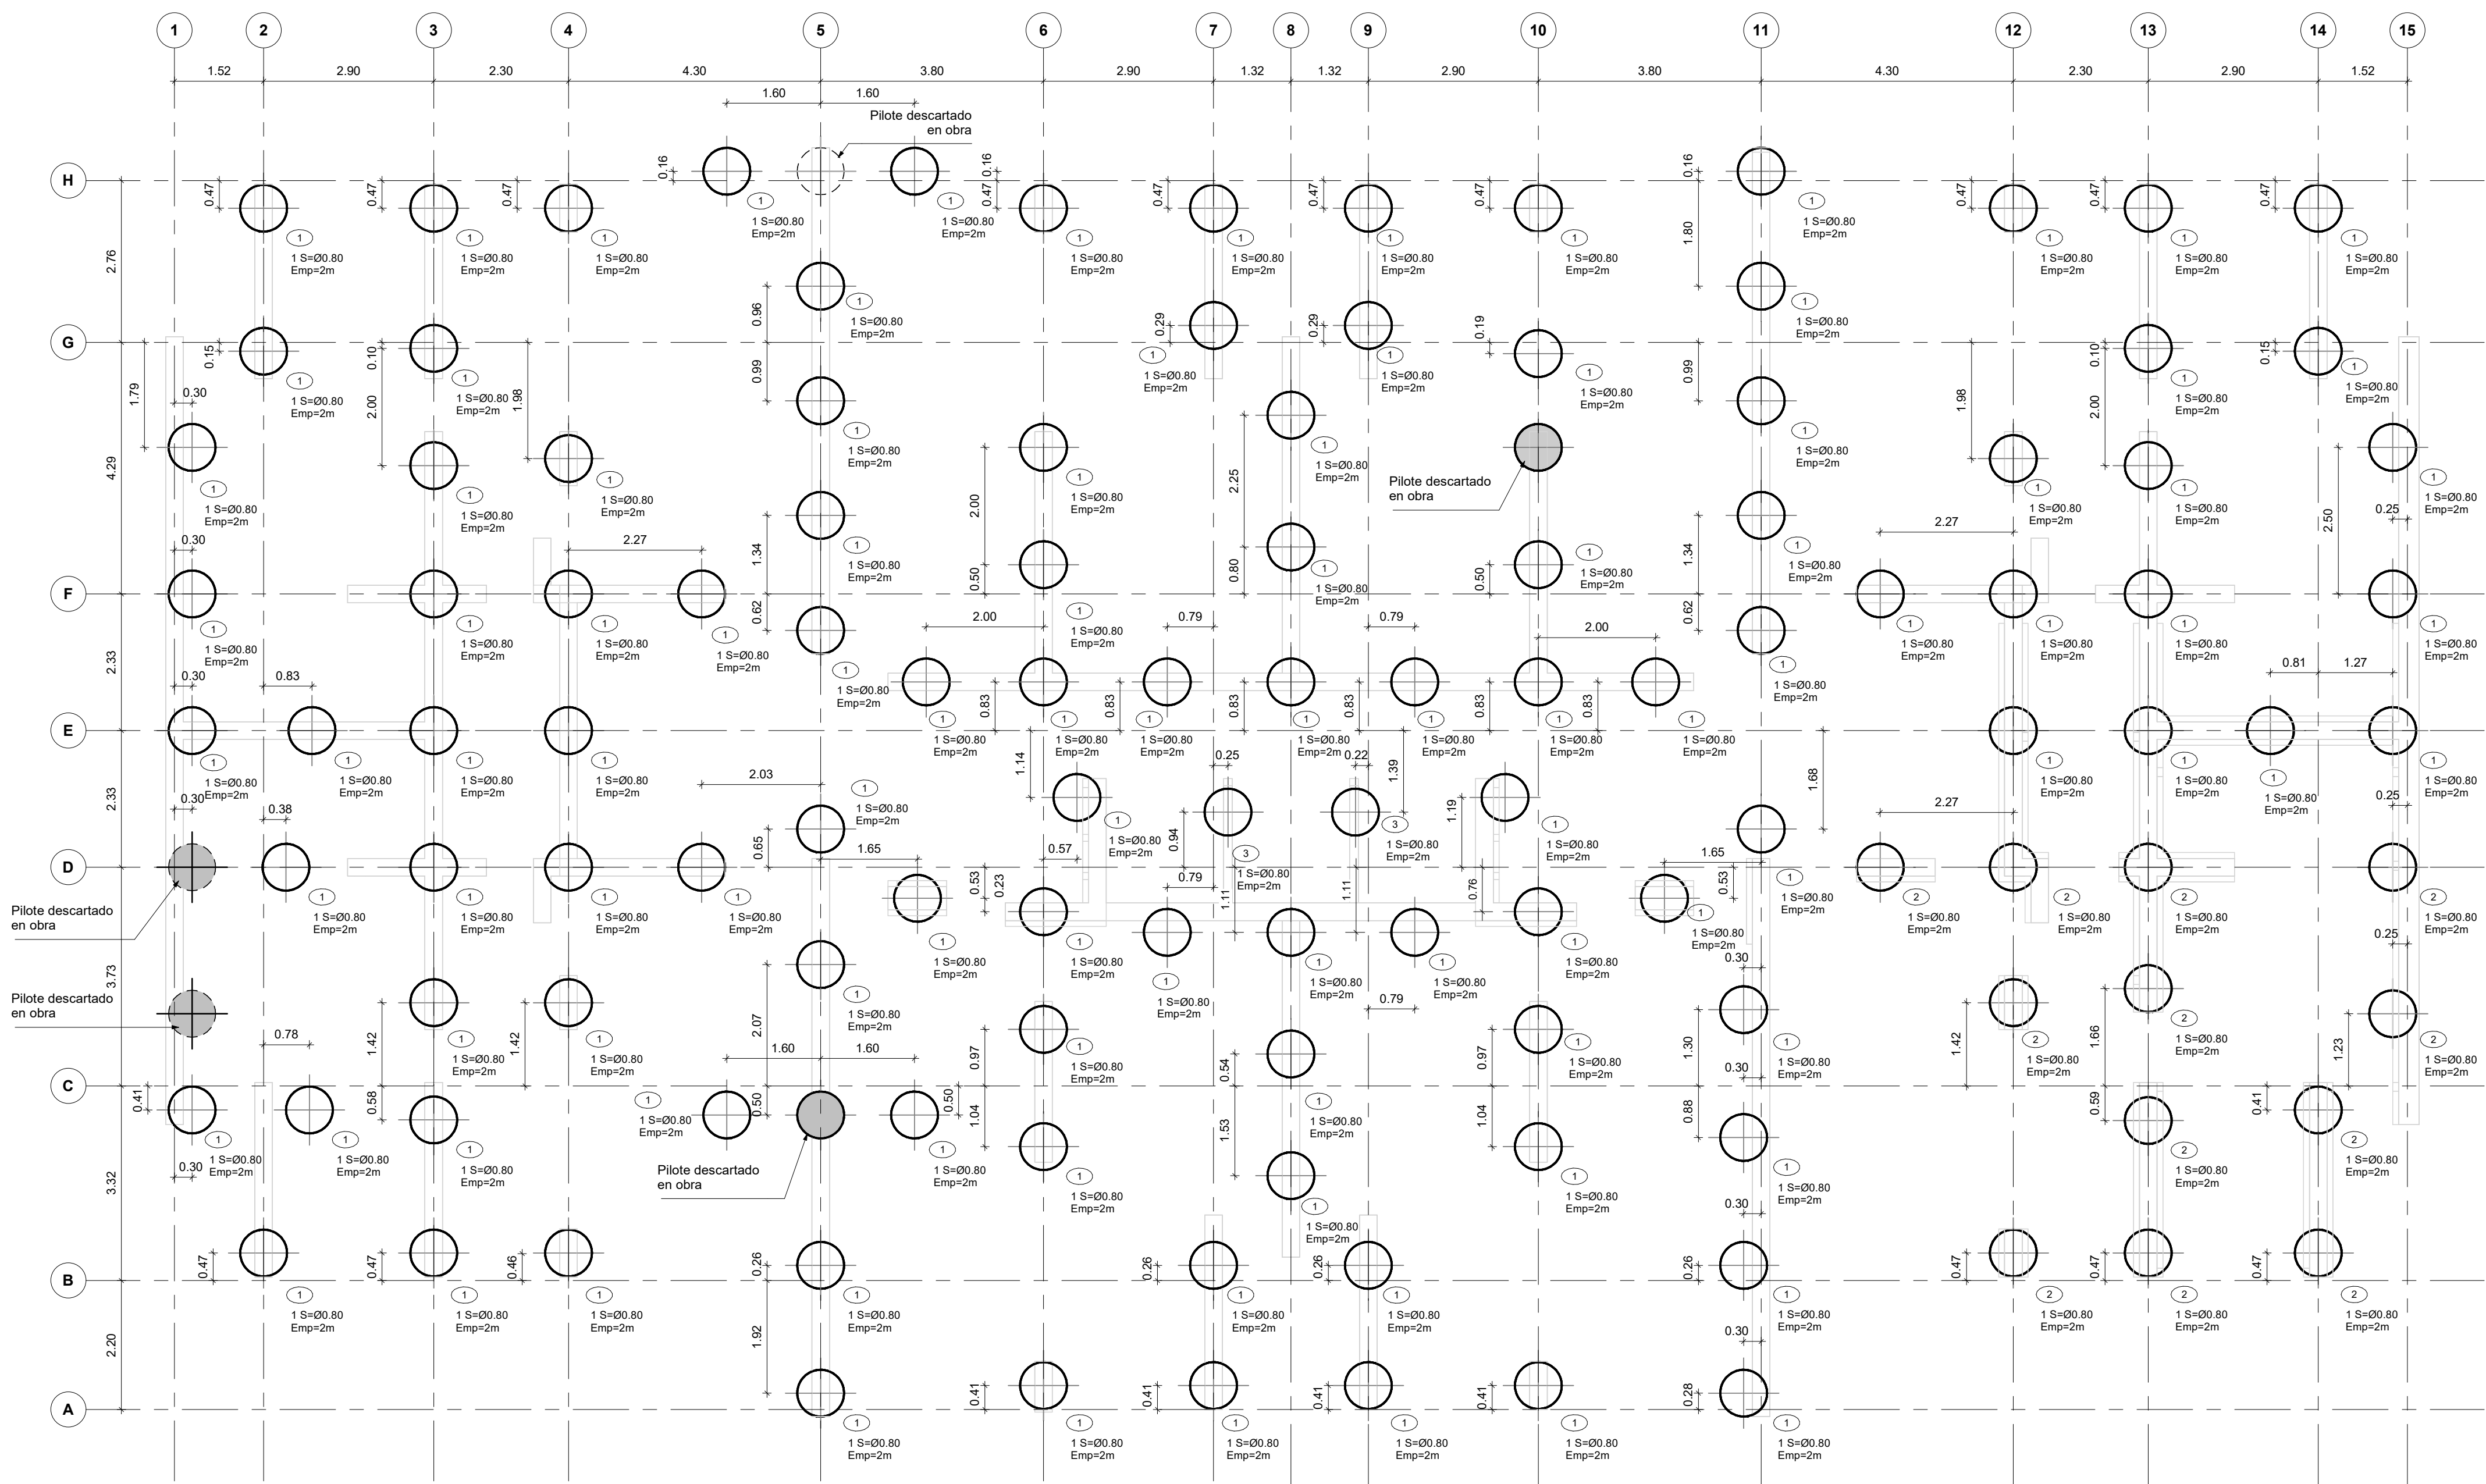

PLANTA DE LOCALIZACIÓN PILOTES  
Escala 1 : 75

**NOTA:**  
La longitud ó profundidad del pilote deberá ser revisada y aprobada en obra por el Ingeniero de Suelos para garantizar que la capacidad del elemento sea la establecida en el estudio de suelos.

**VºBº INGENIERO DE SUELOS**

**CONCRETO**  
**f'c=28 MPa**  
**f'c=280 kg/cm²**  
**f'c=4000 psi**

**CONVENCIONES**  
# Indica Tipo de Pilote  
Emp= Indica profundidad de empotramiento mínimo en el estrato de fundación de acuerdo con el estudio de suelos AUS-13071-7-3

**NOTAS**  
1. Ver detalles generales en el PL. N° 01.02  
2. Ver detalles y cuadro de pilotes en PL. N° 02.01

GERENTE DE PROYECTO  
ROBERTO AYCARDI F.  
MAT. 2520257258 CND

INGENIERO  
CARLOS ANDRÉS WILCHES C.

MODELADOR  
DANIEL CASTELLANOS

| MODIFICACIONES                                     | FECHA      |
|----------------------------------------------------|------------|
| Emisión Inicial                                    | 24-01-2025 |
| Se ajusta posición de pilote sobre eje 14-G y 14-B | 20-02-2025 |
| Se incluyen pilotes tipo 1 en eje 5 - H            | 31-07-2025 |
| Se incluyen pilotes ejes C-1 y D-2                 | 29-01-2026 |
| Se incluye pilotes entre ejes C-5                  | 16-02-2026 |
| Adición pilote en eje 10 - G                       | 18-06-2026 |



LA SCALA

LA SCALA\_EST\_TOR-1

TORRE 1

CALLE 170 CON AV. BOYACA

PLANTA DE LOCALIZACIÓN DE PILOTES

LA SCALA\_EST\_TOR-1\_02.00\_LPIL

REVISOR ESTRUCTURAL  
RAMÓN ANDRÉS ALVAREZ MANTILLA  
MAT. 25202-346546 CND.