


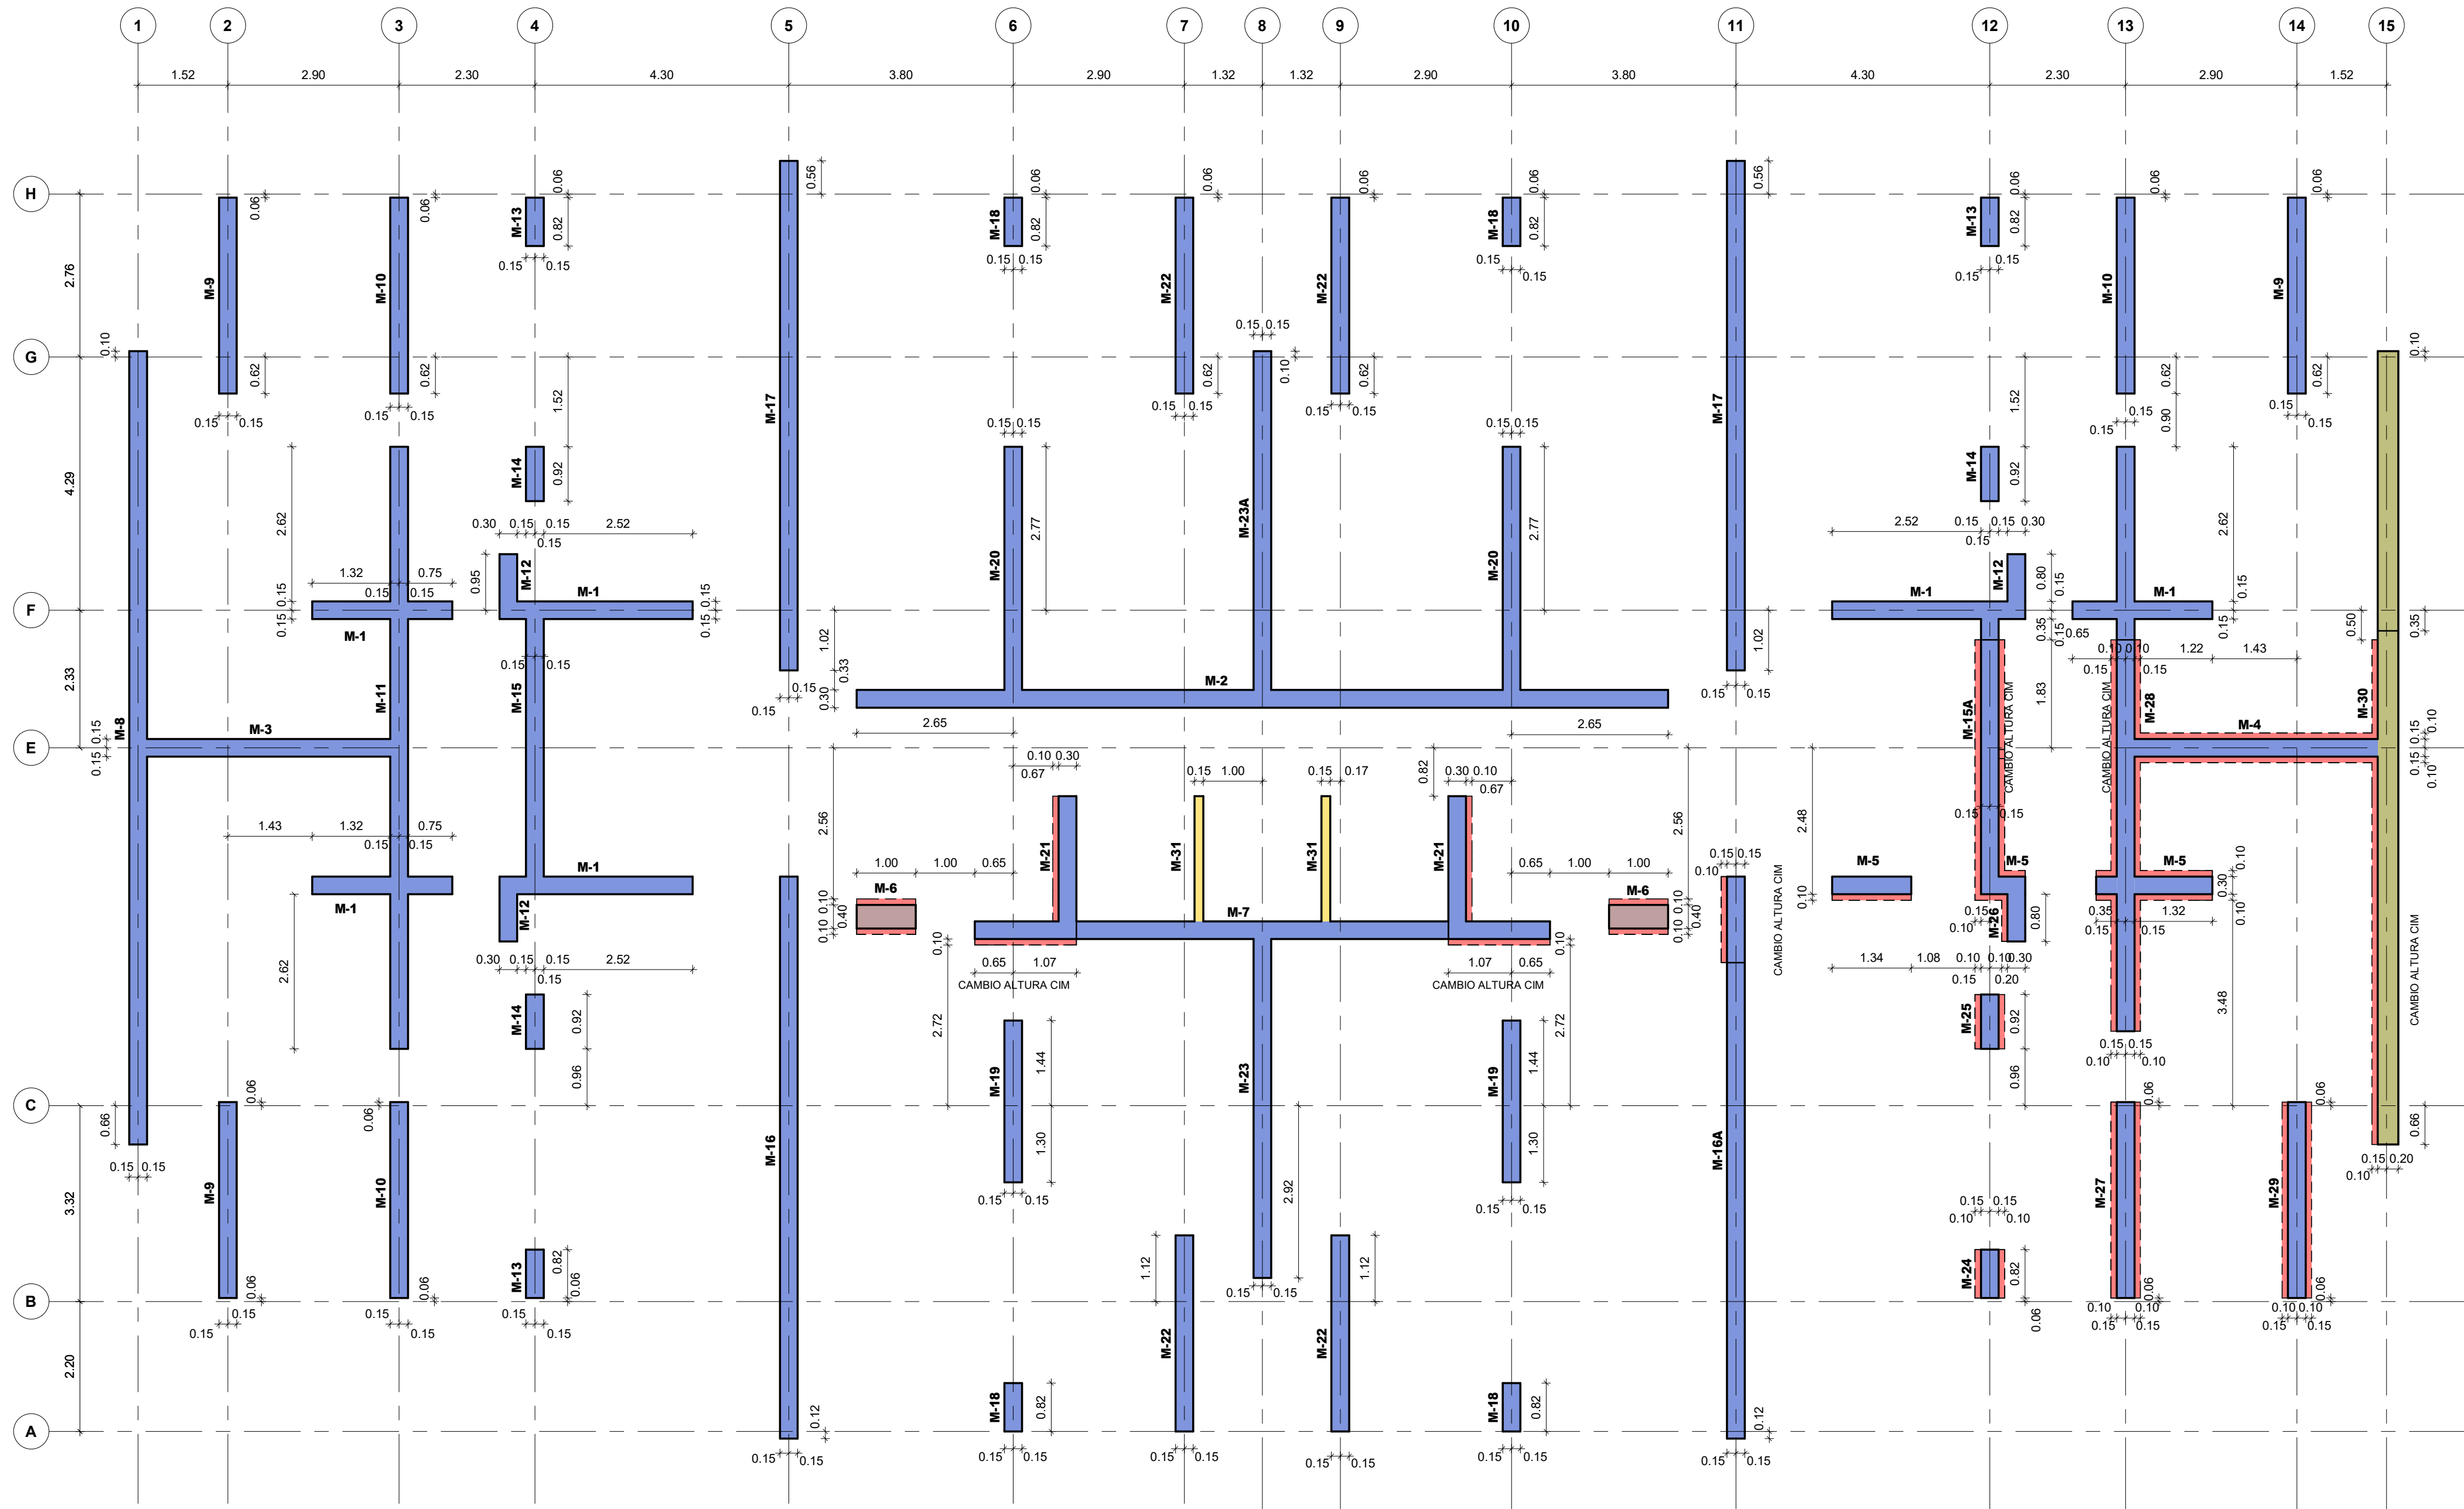

PLANTA LOCALIZACIÓN DE MUROS CIMENTACIÓN N.E -0.82 Y N.E -1.42
Escala 1 : 75

CONCRETO:			
MUROS			
* DE CIMENTACIÓN A PISO 8	* DE PISO 8 A PISO 15	* DE PISO 15 A PISO 22	* DE PISO 22 A CUBIERTA ASCENSOR Y ESCALERAS
f_c=49 MPa	f_c=42 MPa	f_c=35 MPa	f_c=28 MPa
f_c=490 kg/cm²	f_c=420 kg/cm²	f_c=350 kg/cm²	f_c=280 kg/cm²
f_c=7000 psi	f_c=6000 psi	f_c=5000 psi	f_c=4000 psi

CONVENCIONES	
M-#	Indica N° de Muro
	Indica muro e=0.15
	Indica muro e=0.30
	Indica muro e=0.35
	Indica muro e=0.40
	Indica sobrehanco e=0.10
NOTAS	
1. Ver detalles generales en PL. N°01.02	
2. Ver despieces de muros en PL. N° 11.00 a PL N°11.21	
3. Ver detalles de muros en PL. N° 11.22	

VERSIÓN :

3

PLANO N° 03.00



GERENTE DE PROYECTO
ROBERTO AYCARDI F.
MAT. 2520257258 CND

INGENIERO
CARLOS ANDRÉS WILCHES C.

MODELADOR
DANIEL CASTELLANOS

MODIFICACIONES		FECHA
Emisión Inicial	Se incluye sobrehanco de muros	20-02-2025
	Se actualiza longitud de muro M-19	03-10-2025
		04-11-2025



LA SCALA

LA SCALA_EST_TOR-1

TORRE 1

CALLE 170 CON AV. BOYACA

PLANTA DE LOCALIZACIÓN DE MUROS
CIMENTACIÓN

LA SCALA_EST_TOR-1_03.00_LCM-CIM

REVISOR ESTRUCTURAL

RAMÓN ÁNDRES ALVAREZ MANTILLA
MAT. 25202-346546 CND.

PLANO N°

03.00

VERSIÓN :

3