


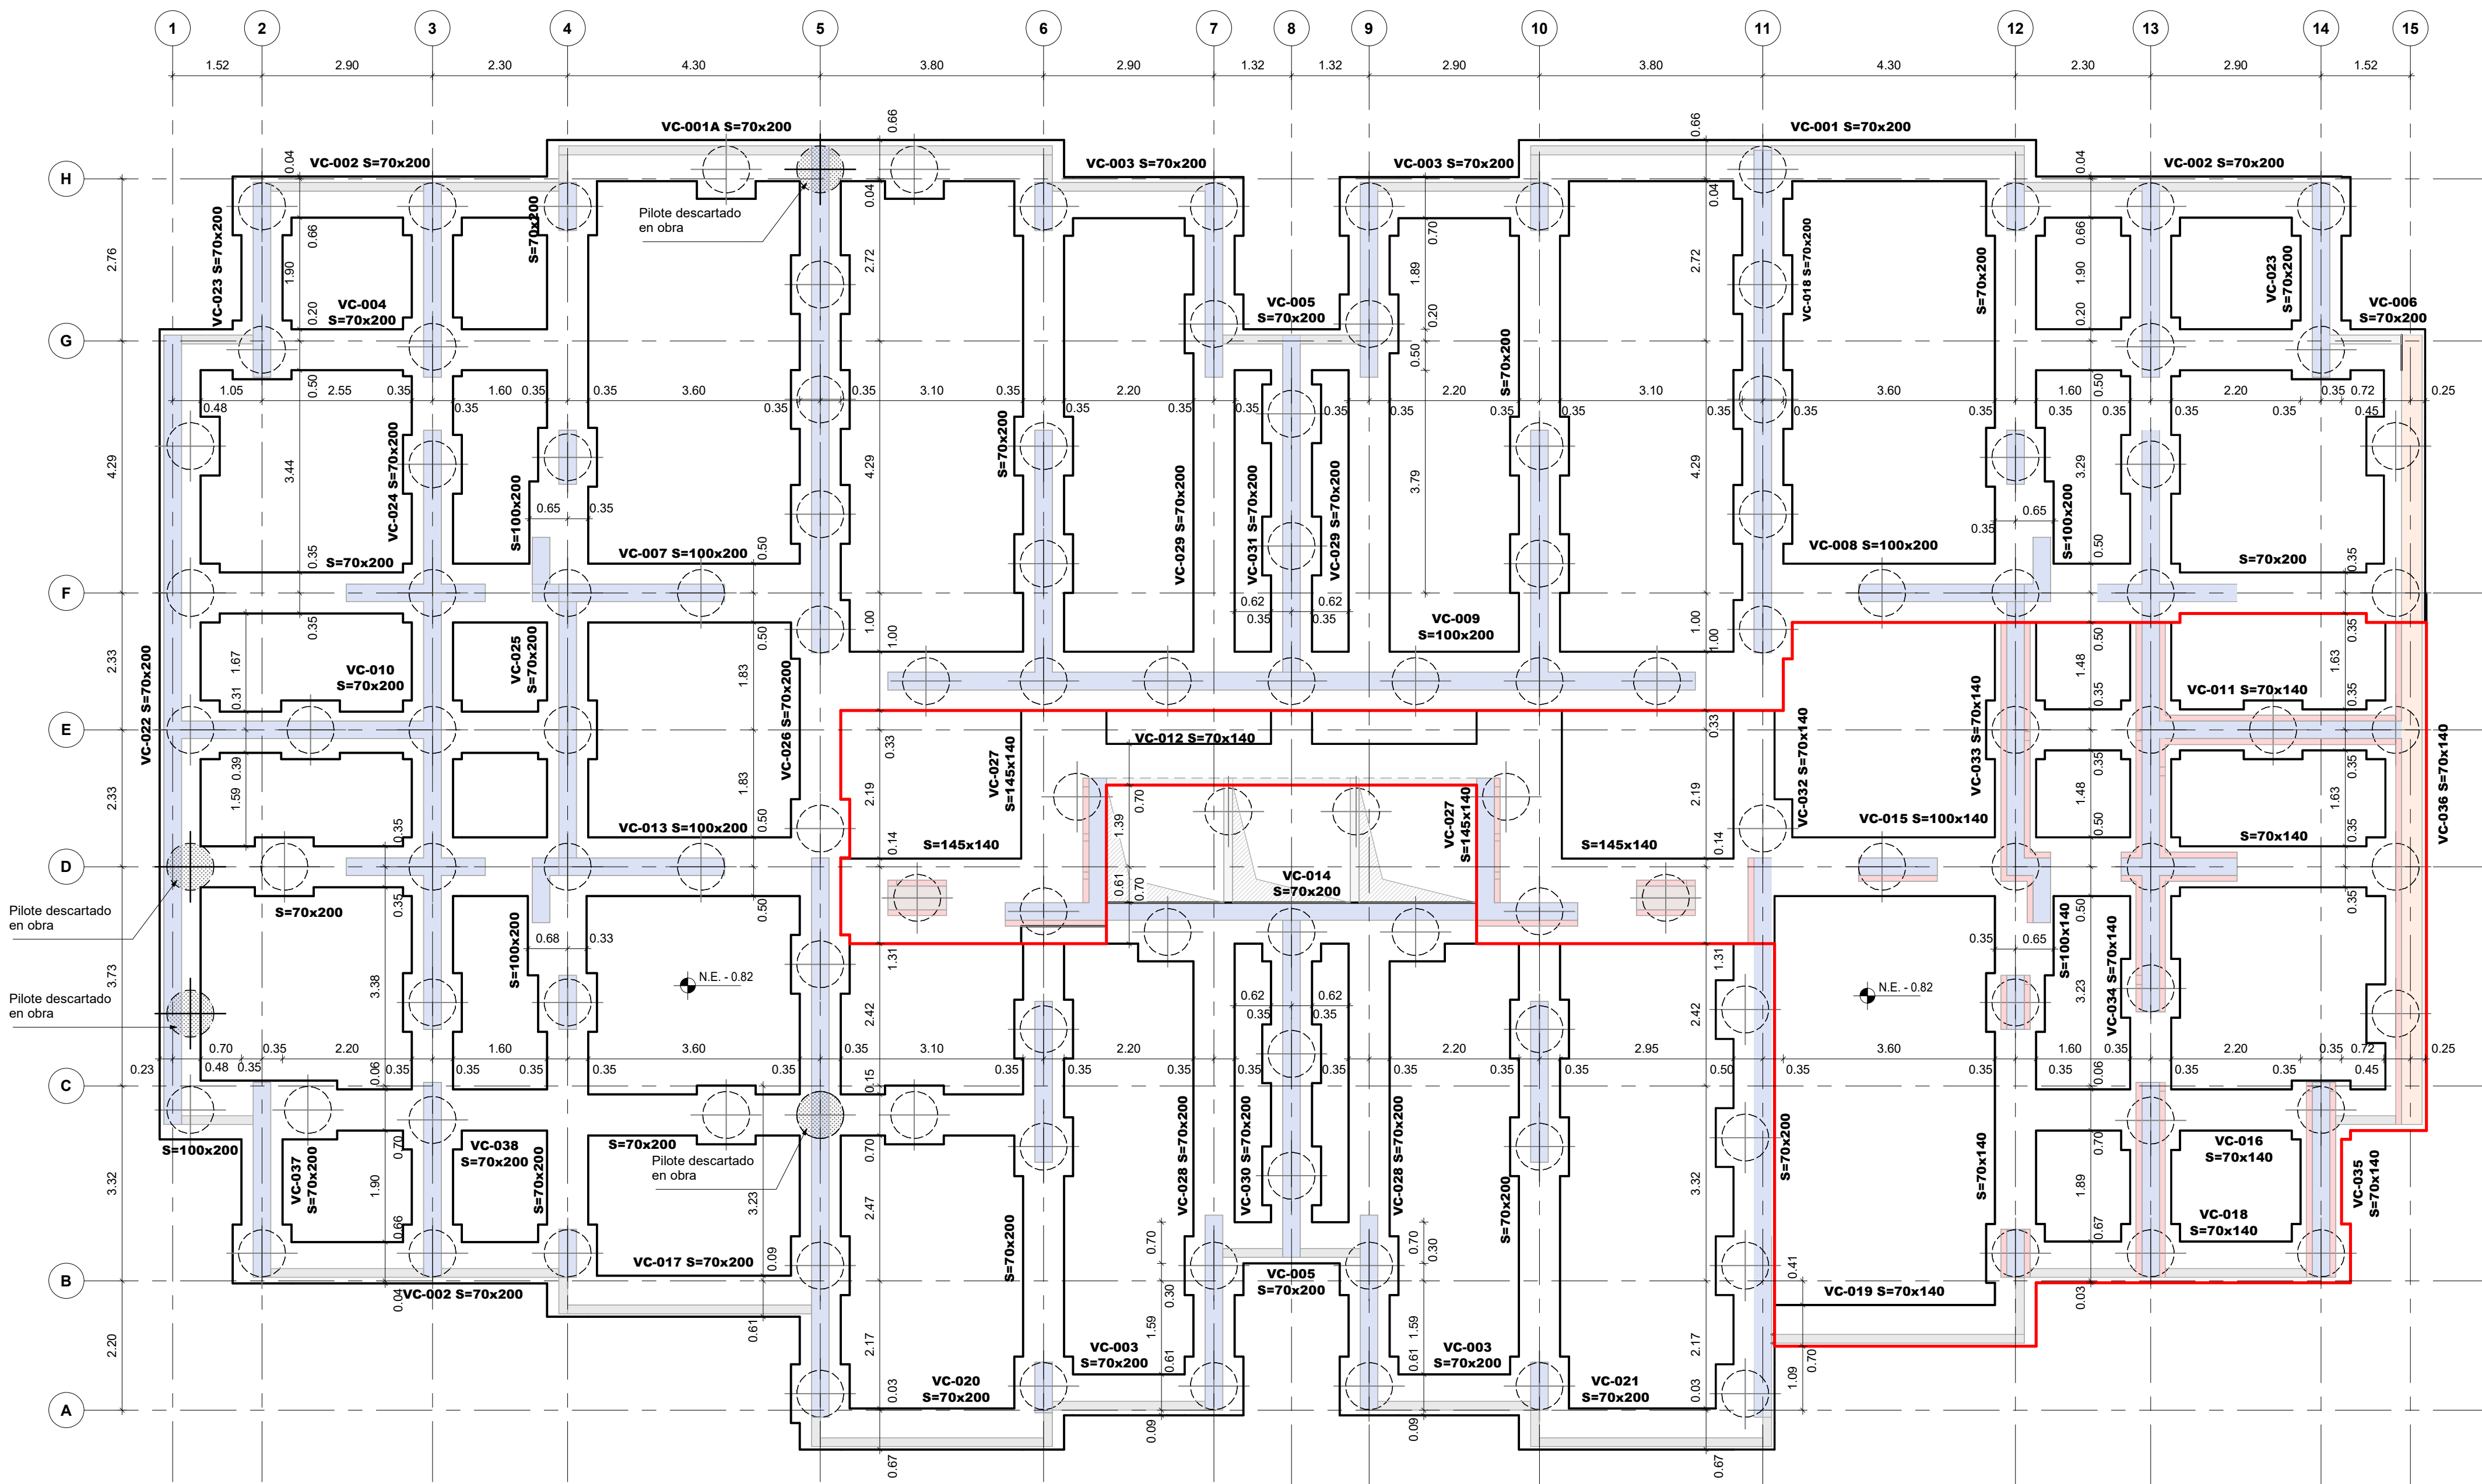

PLANTA DE CIMENTACIÓN N.E -0.82 Y N.E -1.42
Escala 1 : 75

CONVENCIONES	
	Indica muro e=0.15
	Indica muro e=0.30
	Indica muro e=0.35
	Indica muro e=0.40
	Indica muretes
	Indica sobreancho e=0.10
	Indica zona cambio de profundidad

CONCRETO	
f_c=35 MPa	
f_c=350 kg/cm²	
f_c=5000 psi	

NOTAS	
1. Ver plano de detalles generales en PL. N° 01.02	
2. Ver plano de localización de pilotes en PL. N° 02.00	
3. Ver corte y detalles de cimentación en PL. N° 03.02	
4. Ver planta y detalles de dados en PL. N° 03.03	
5. Ver despiece de vigas de cimentación desde PL. N° 03.05 hasta PL. N° 03.07	
6. Ver planta y detalles foso de ascensor en PL. N° 03.04	

NOTA:
Este plano debe ser revisado y aprobado por el Ingeniero de suelos.

V°B° INGENIERO DE SUELOS

PLANO N° 03.01

VERSIÓN : 4

GERENTE DE PROYECTO
ROBERTO AYCARDI F.
MAT. 2520257258 CND

INGENIERO
CARLOS ANDRÉS WILCHES C.

MODELADOR
DANIEL CASTELLANOS

MODIFICACIONES	FECHA
Emisión Inicial	20-02-2025
Se incluyen muretes perimetrales y dados en eje H-4-6	03-10-2025
Se incluyen vigas VC-037 y VC-038	29-01-2026
Se actualiza viga VC-038	26-02-2026



LA SCALA

LA SCALA_EST_TOR-1

TORRE 1

CALLE 170 CON AV. BOYACA

PLANTA DE CIMENTACIÓN

LA SCALA_EST_TOR-1_03.01_CIM

REVISOR ESTRUCTURAL
RAMÓN ANDRÉS ALVAREZ MANTILLA
MAT. 25202-346546 CND.

PLANO N°

03.01

VERSIÓN :

4