




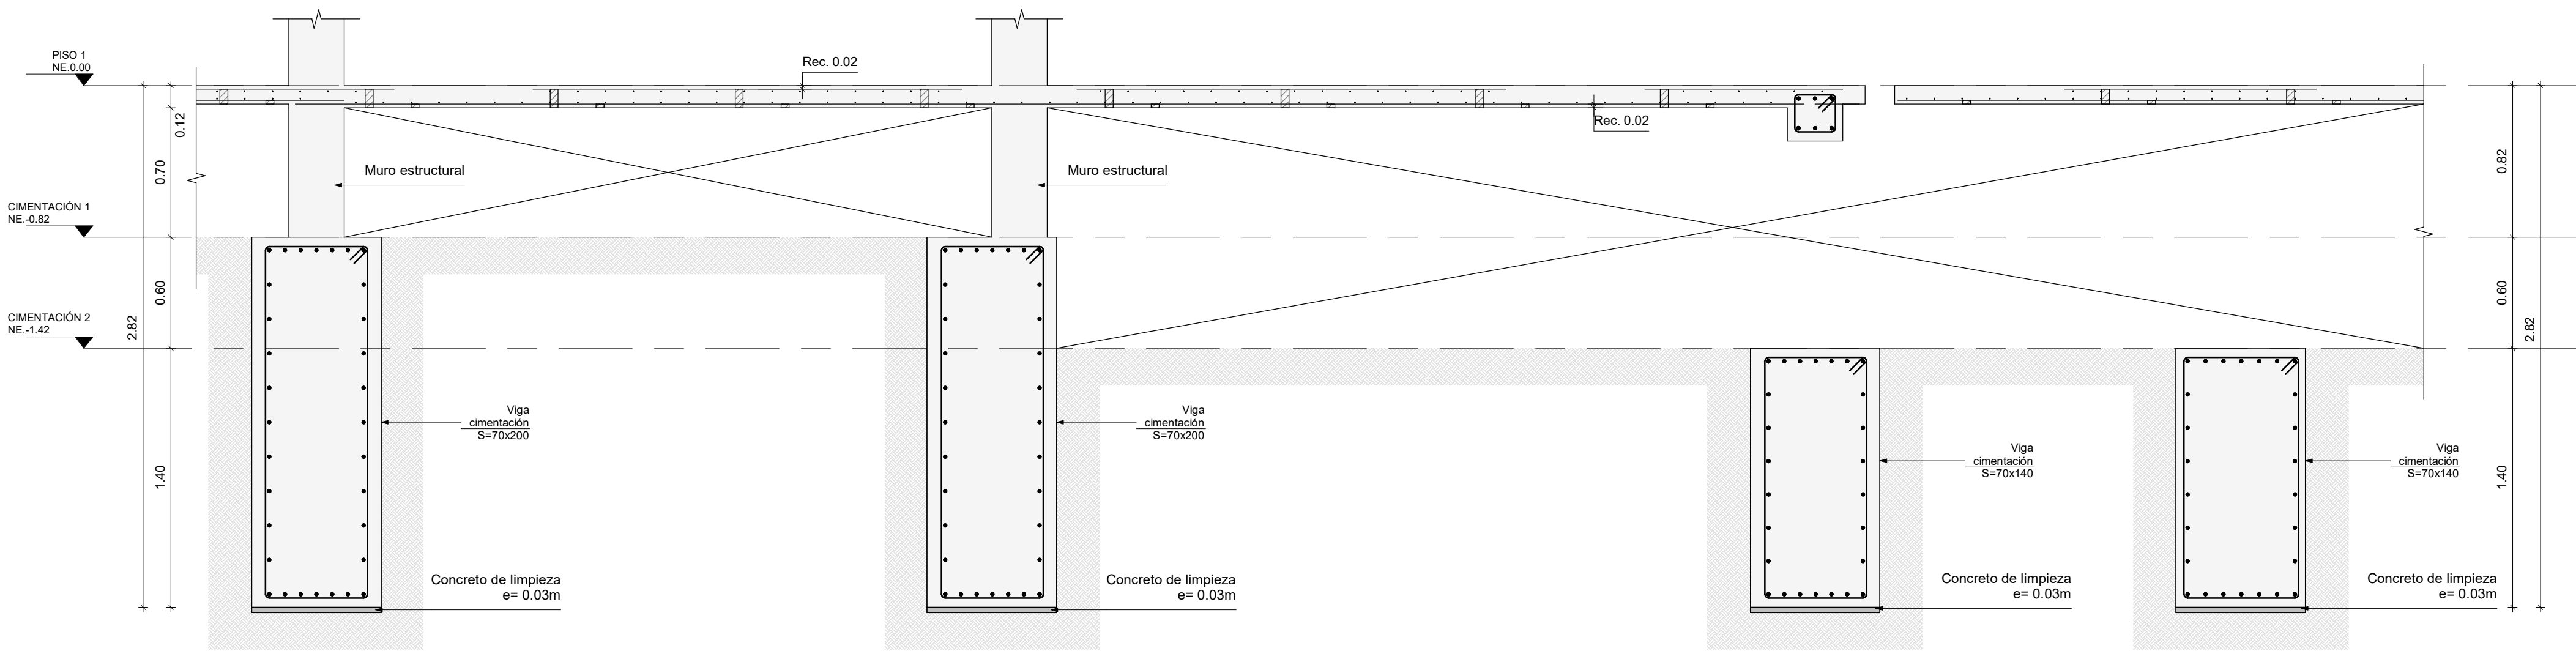


CORTE CIMENTACIÓN
Escala 1 : 25

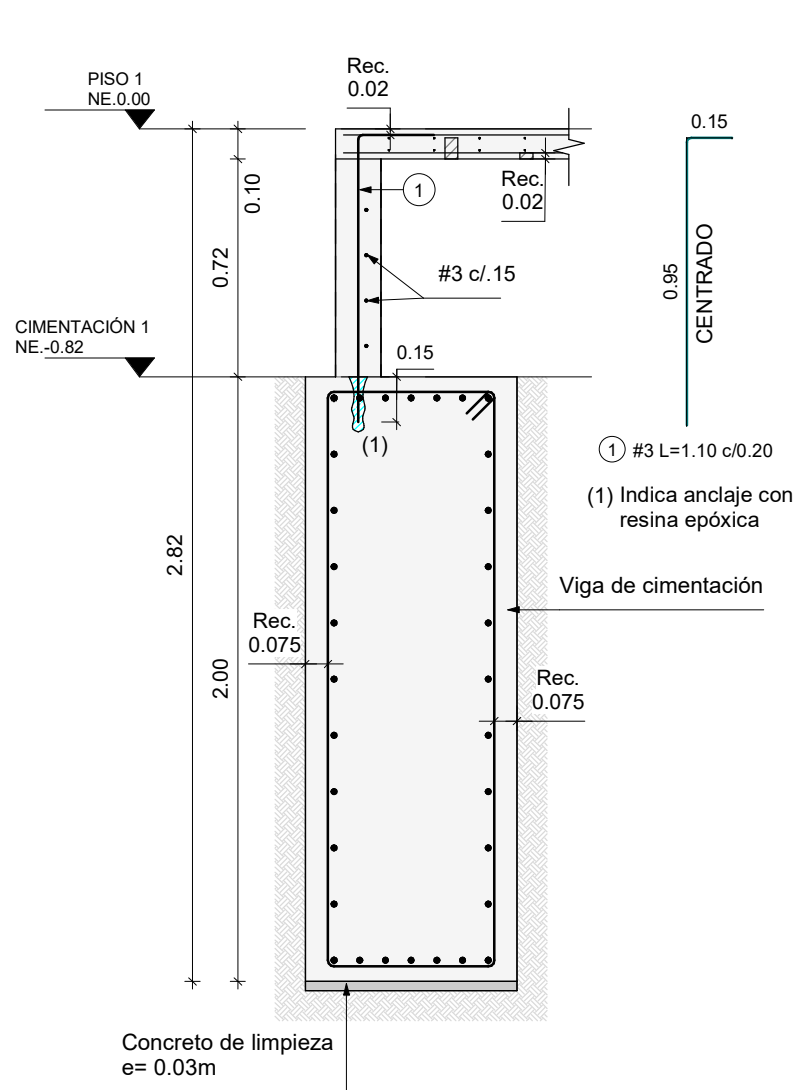


DETALLE MURETE EN CONCRETO TIPO 1
Escala 1 : 25

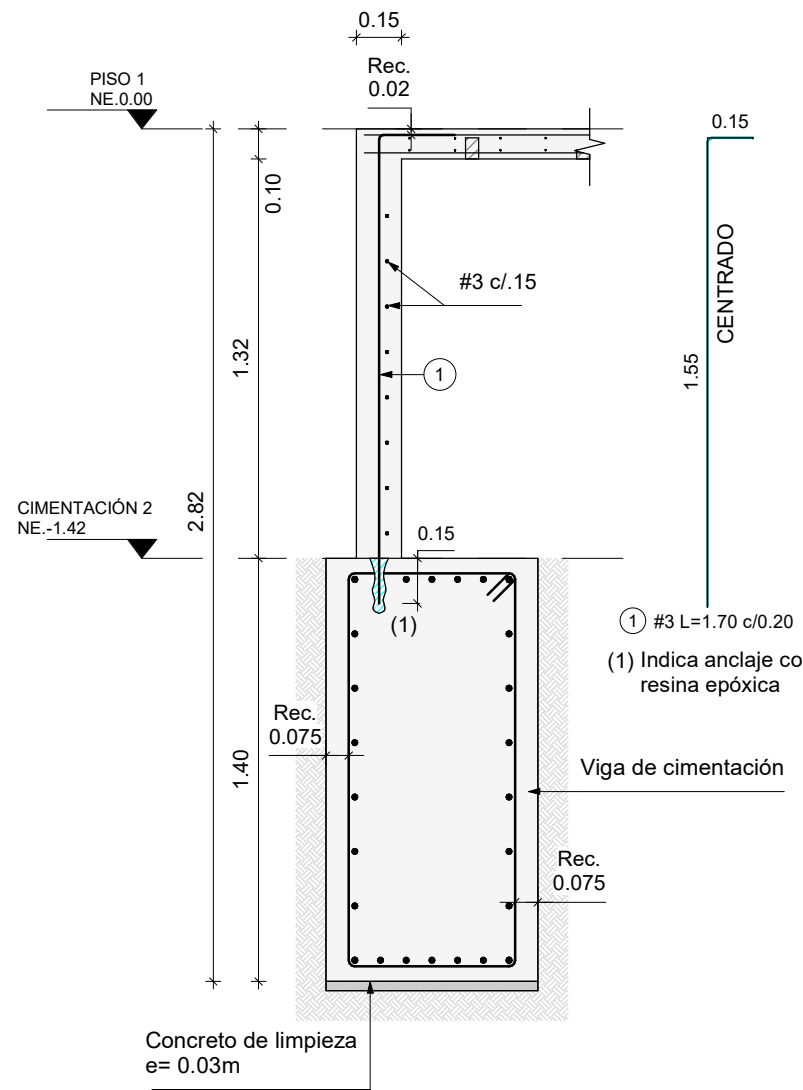


DETALLE MURETE EN CONCRETO TIPO 2
Escala 1 : 25

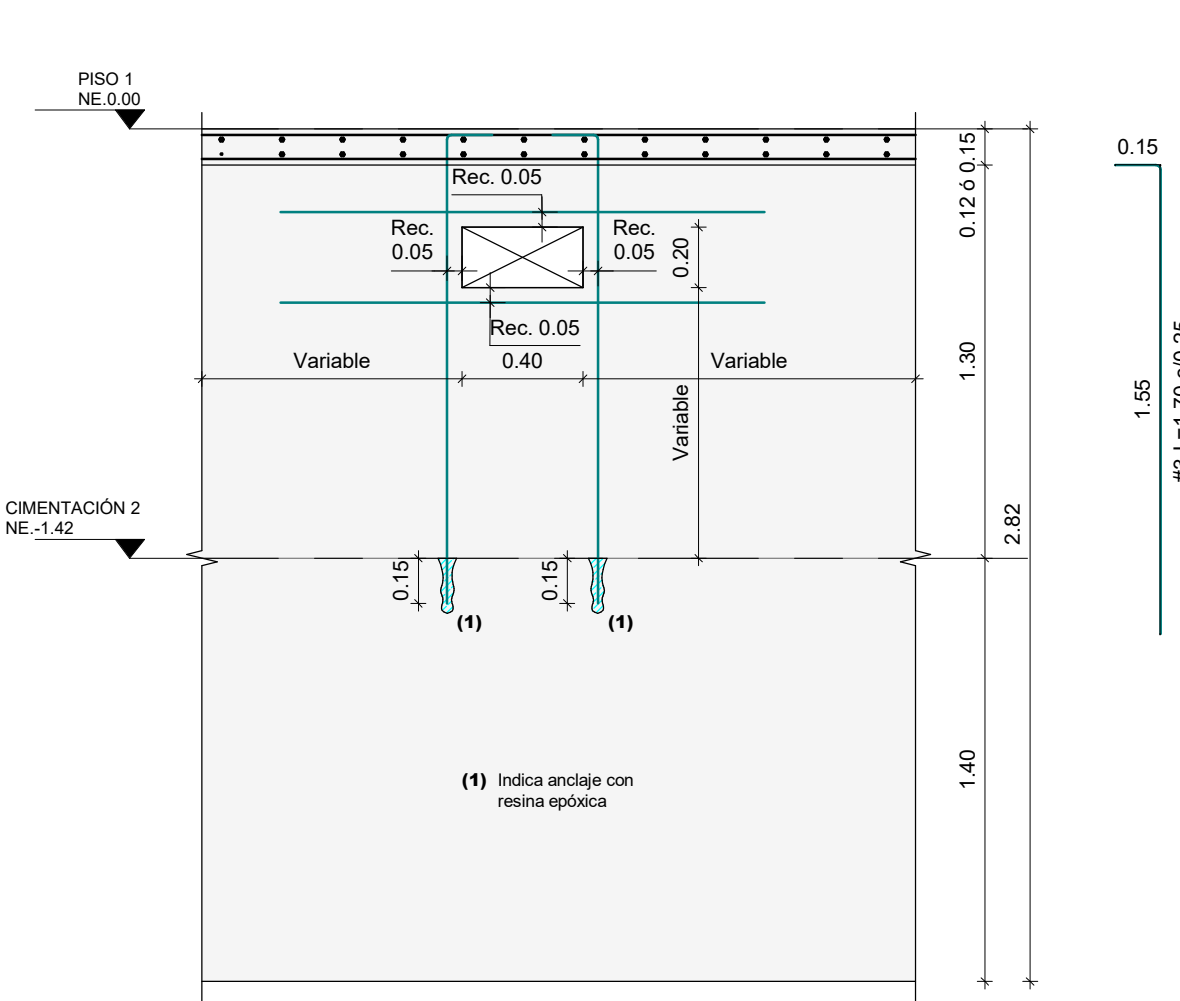

DETALLE PASES DE TUBERÍAS EN MURETES
Escala 1 : 25

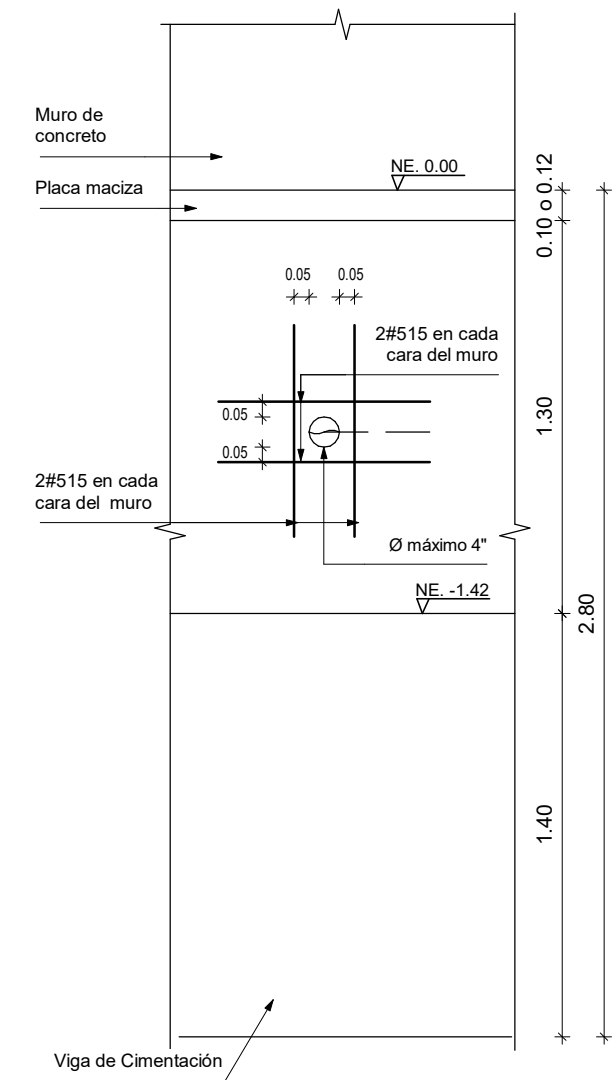

DETALLE PASE MURO
Escala 1 : 25

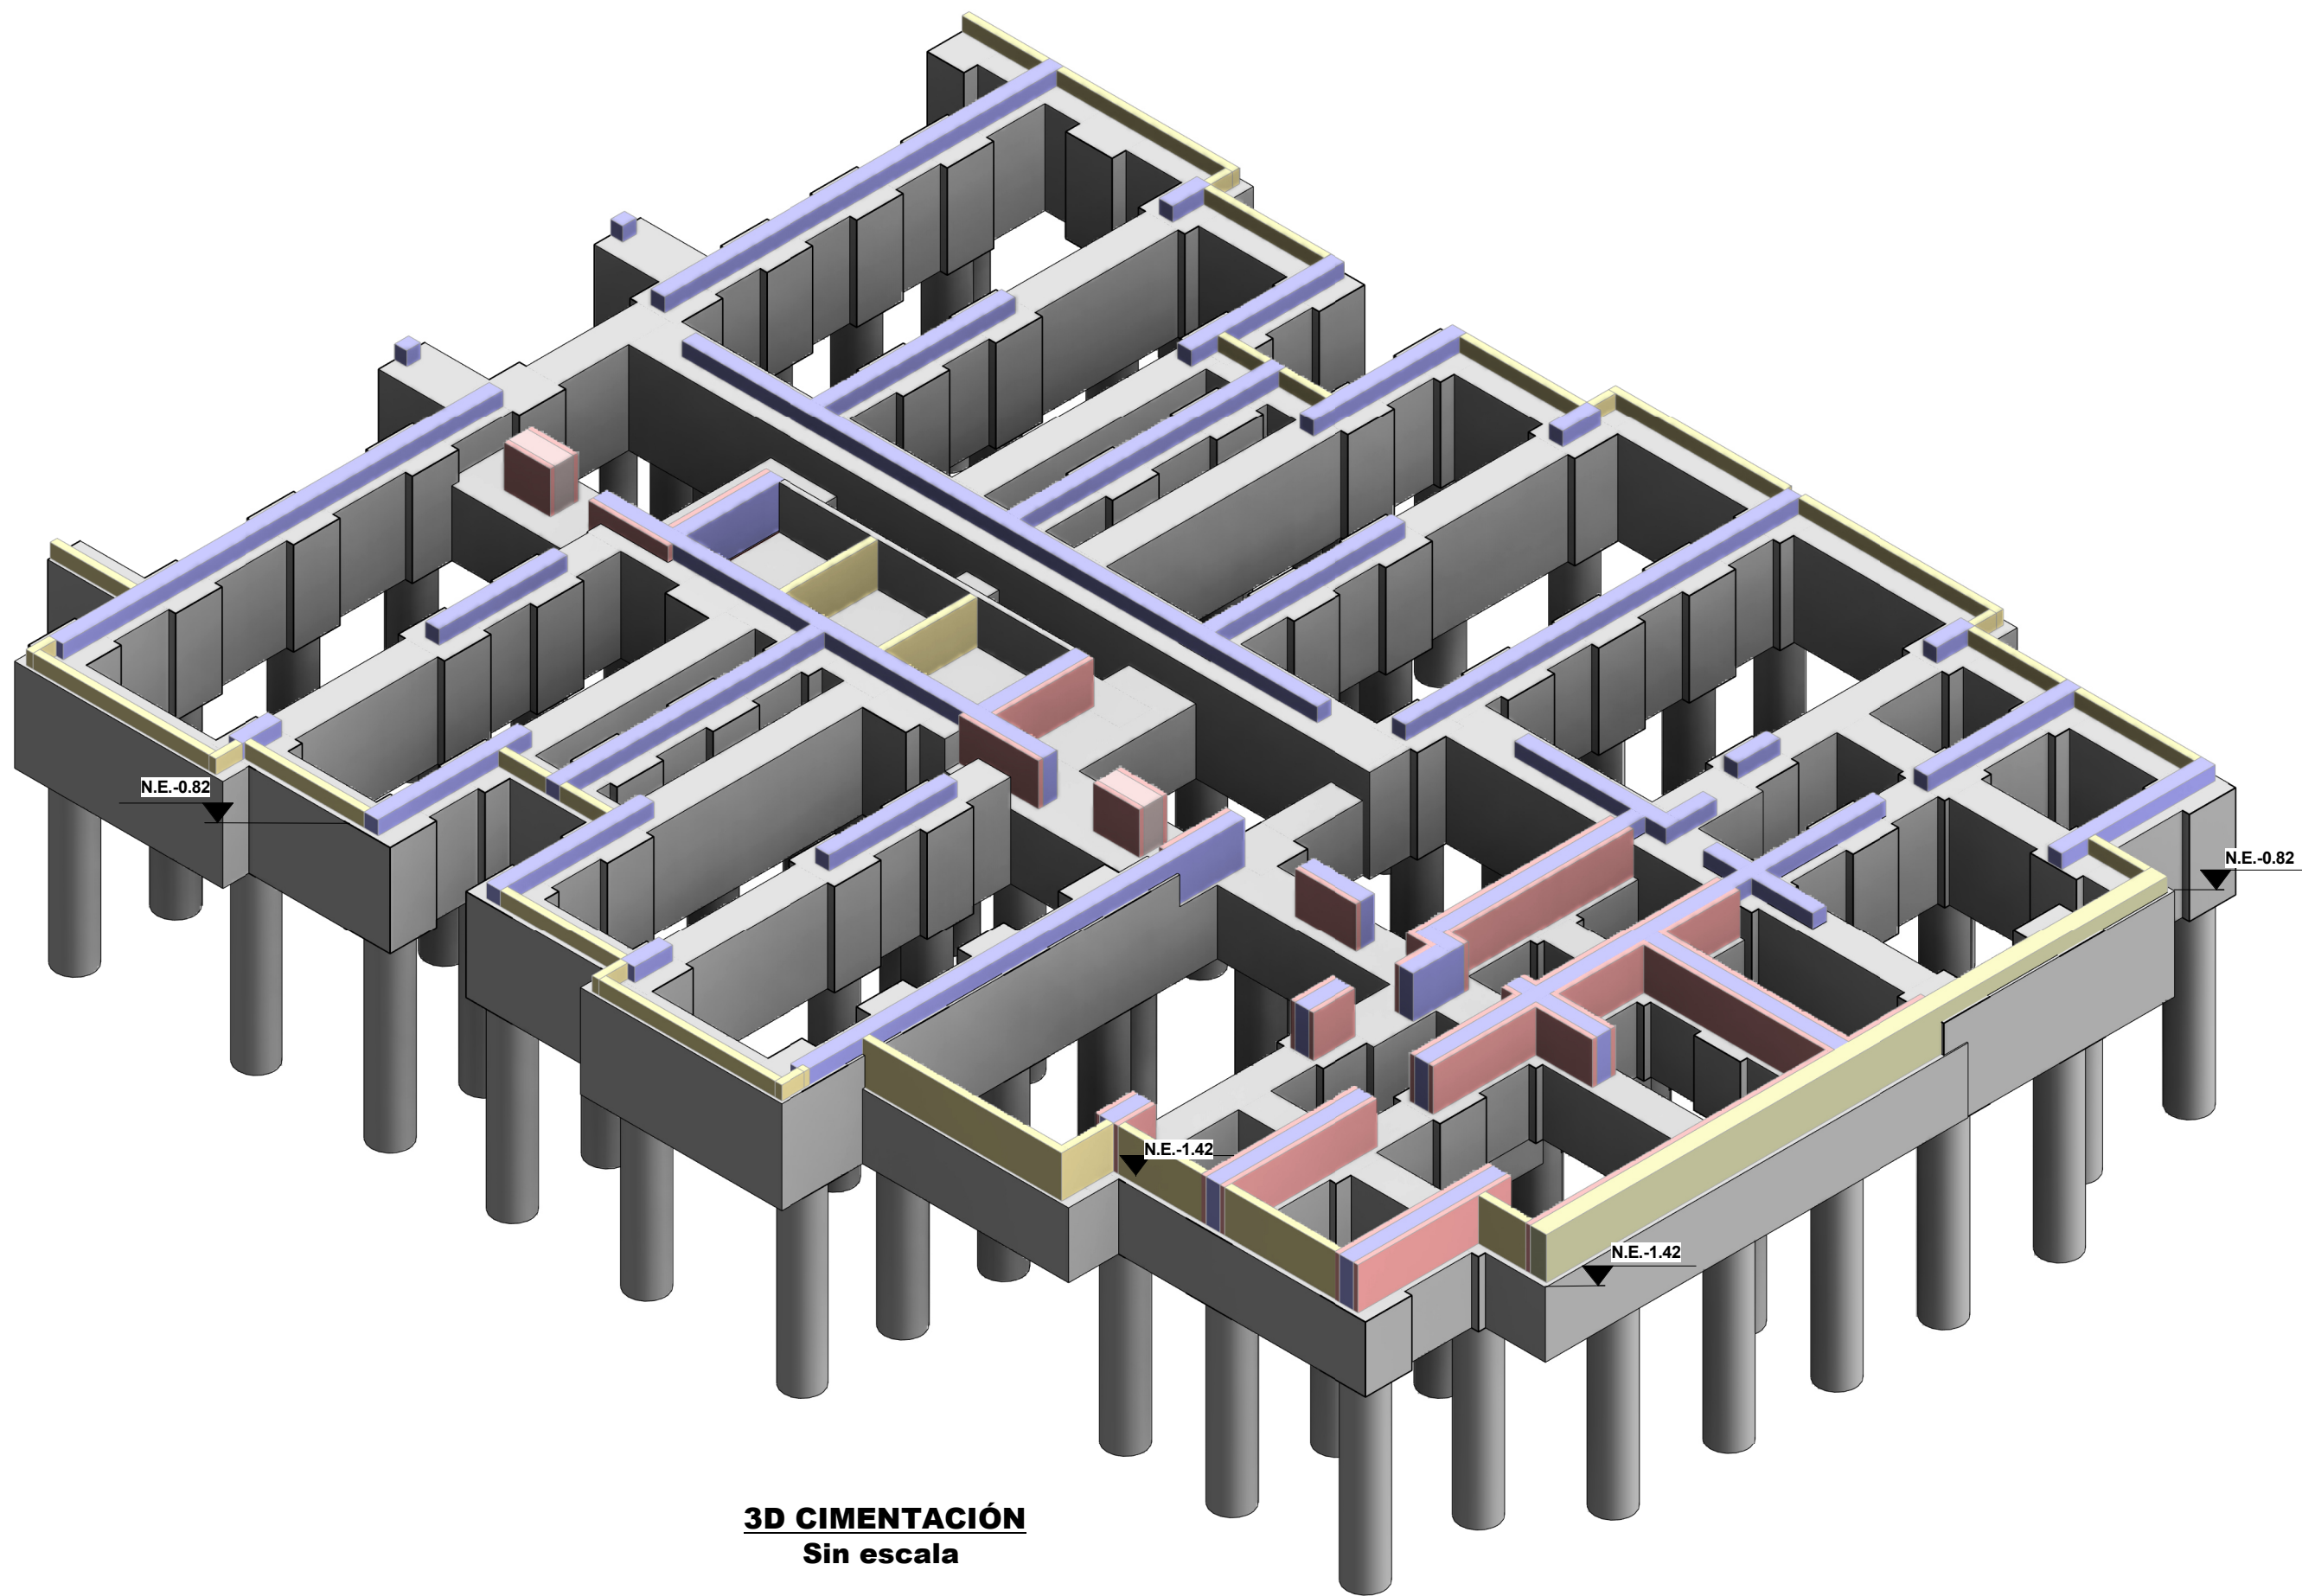

3D CIMENTACIÓN
Sin escala

NOTA:
Este plano debe ser revisado y aprobado por el Ingeniero de suelos.

V°B° INGENIERO DE SUELOS

CONCRETO
f_c=35 MPa
f_c=350 kg/cm²
f_c=5000 psi

NOTAS

1. Ver plano de detalles generales en PL. N° 01.02
2. Ver planta de cimentación en PL. N° 03.01
3. Ver planta y detalles de dados en PL. N° 03.03
4. Ver desplce de vigas de cimentación desde PL. N° 03.05 hasta PL. N° 03.06
5. Ver planta y detalles foso de ascensor en PL. N° 03.04

VERSIÓN :

3

PLANO N° 03.02

Aycardi
Estructural

GERENTE DE PROYECTO
ROBERTO AYCARDI F.
MAT. 2520257258 CND

INGENIERO
CARLOS ANDRÉS WILCHES C.

MODELADOR
DANIEL CASTELLANOS

MODIFICACIONES	FECHA
Emisión Inicial	20-02-2025
Se agregan detalles	26-02-2025
Se incluyen muretes perimetrales	03-10-2025



LA SCALA

LA SCALA_EST_TOR-1

TORRE 1

CALLE 170 CON AV. BOYACA

CORTES Y DETALLES DE CIMENTACIÓN

LA SCALA_EST_TOR-1_03.02_DT-CIM

REVISOR ESTRUCTURAL

RAMÓN ÁNDRES ALVAREZ MANTILLA
MAT. 25202-346546 CND.

PLANO N°

03.02

VERSIÓN :

3