




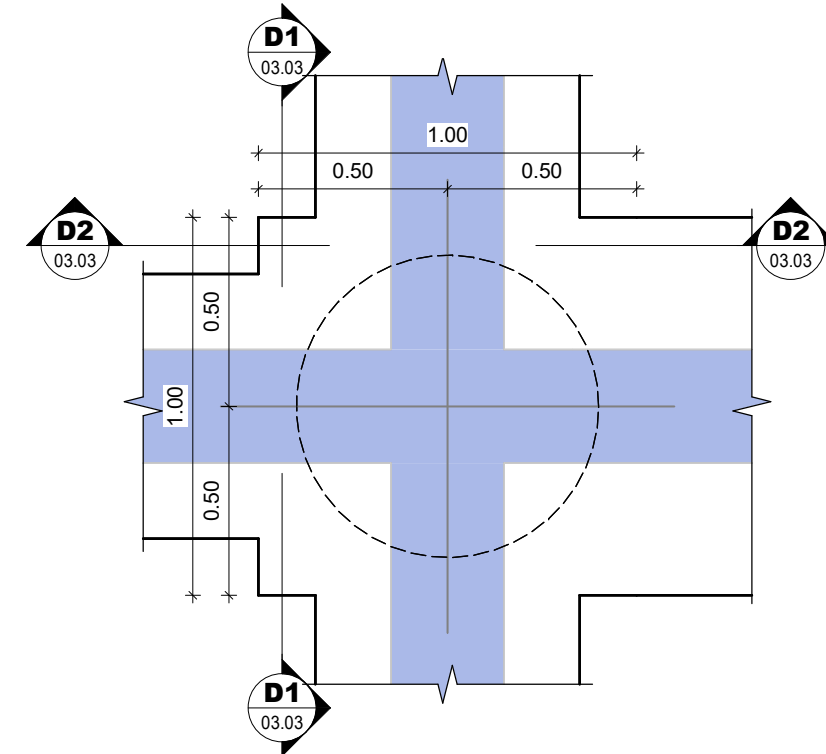


GEOMETRÍA TÍPICA DADOS TIPO 1 Y 2
Escala 1 : 20

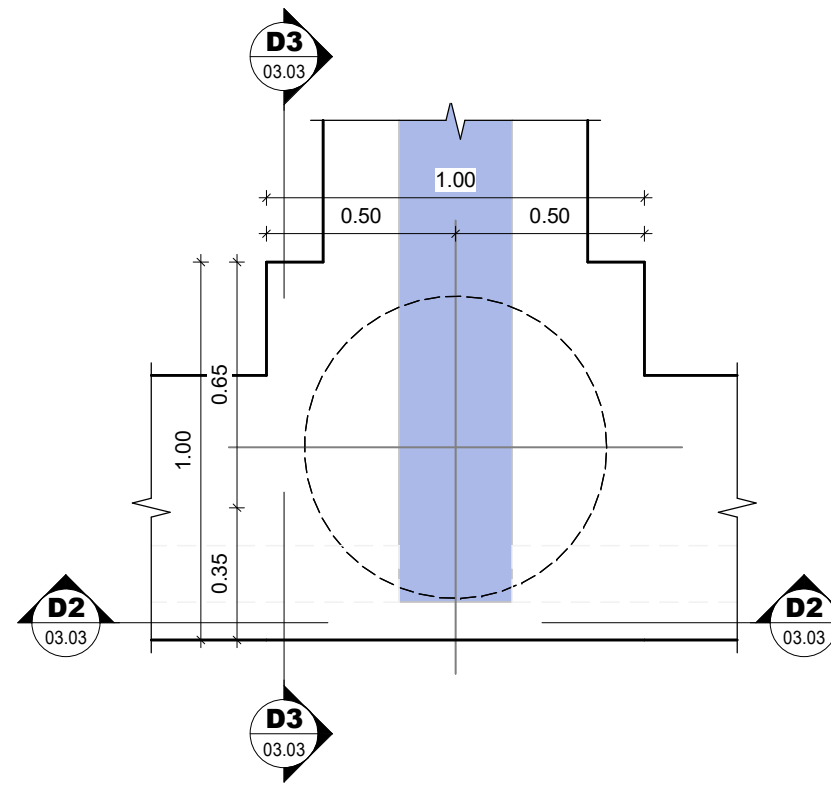


GEOMETRÍA TÍPICA DADOS TIPO 3 Y 4
Escala 1 : 20

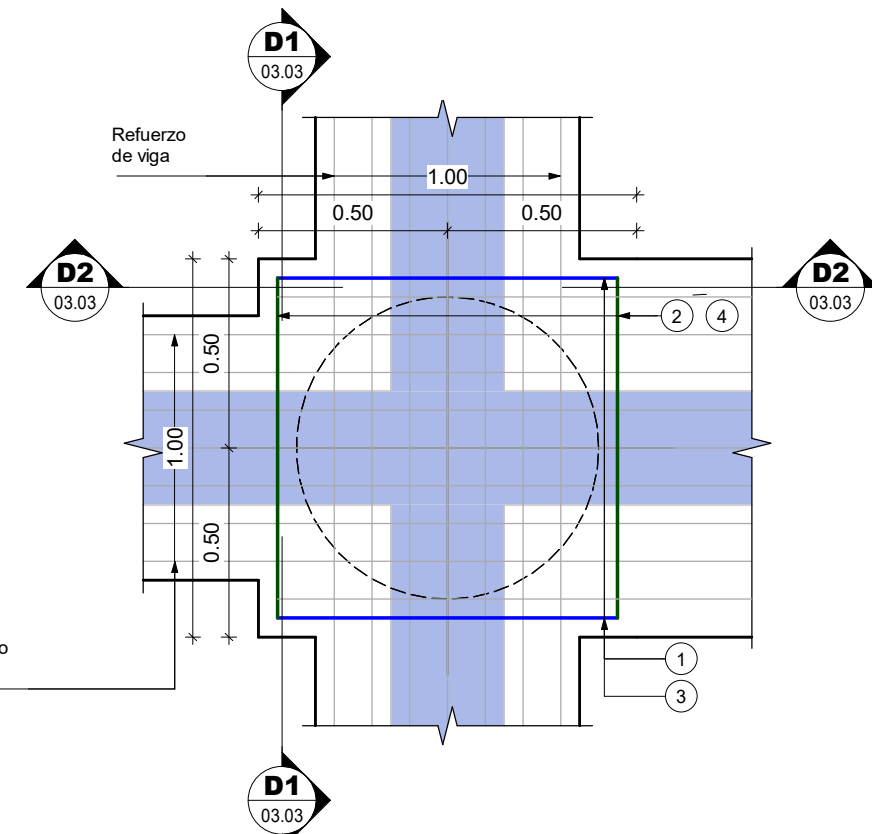


PLANTA REFUERZO TÍPICO DADOS TIPO 1 Y 2
Escala 1 : 20

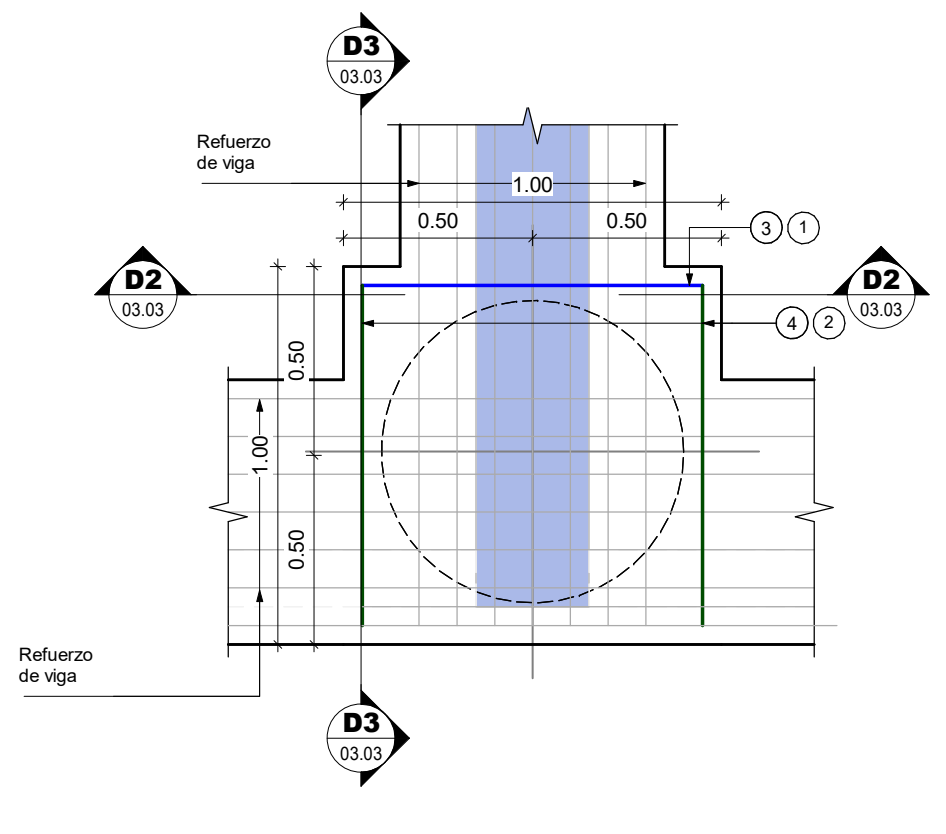


PLANTA REFUERZO TÍPICO DADOS TIPO 3 Y 4
Escala 1 : 20

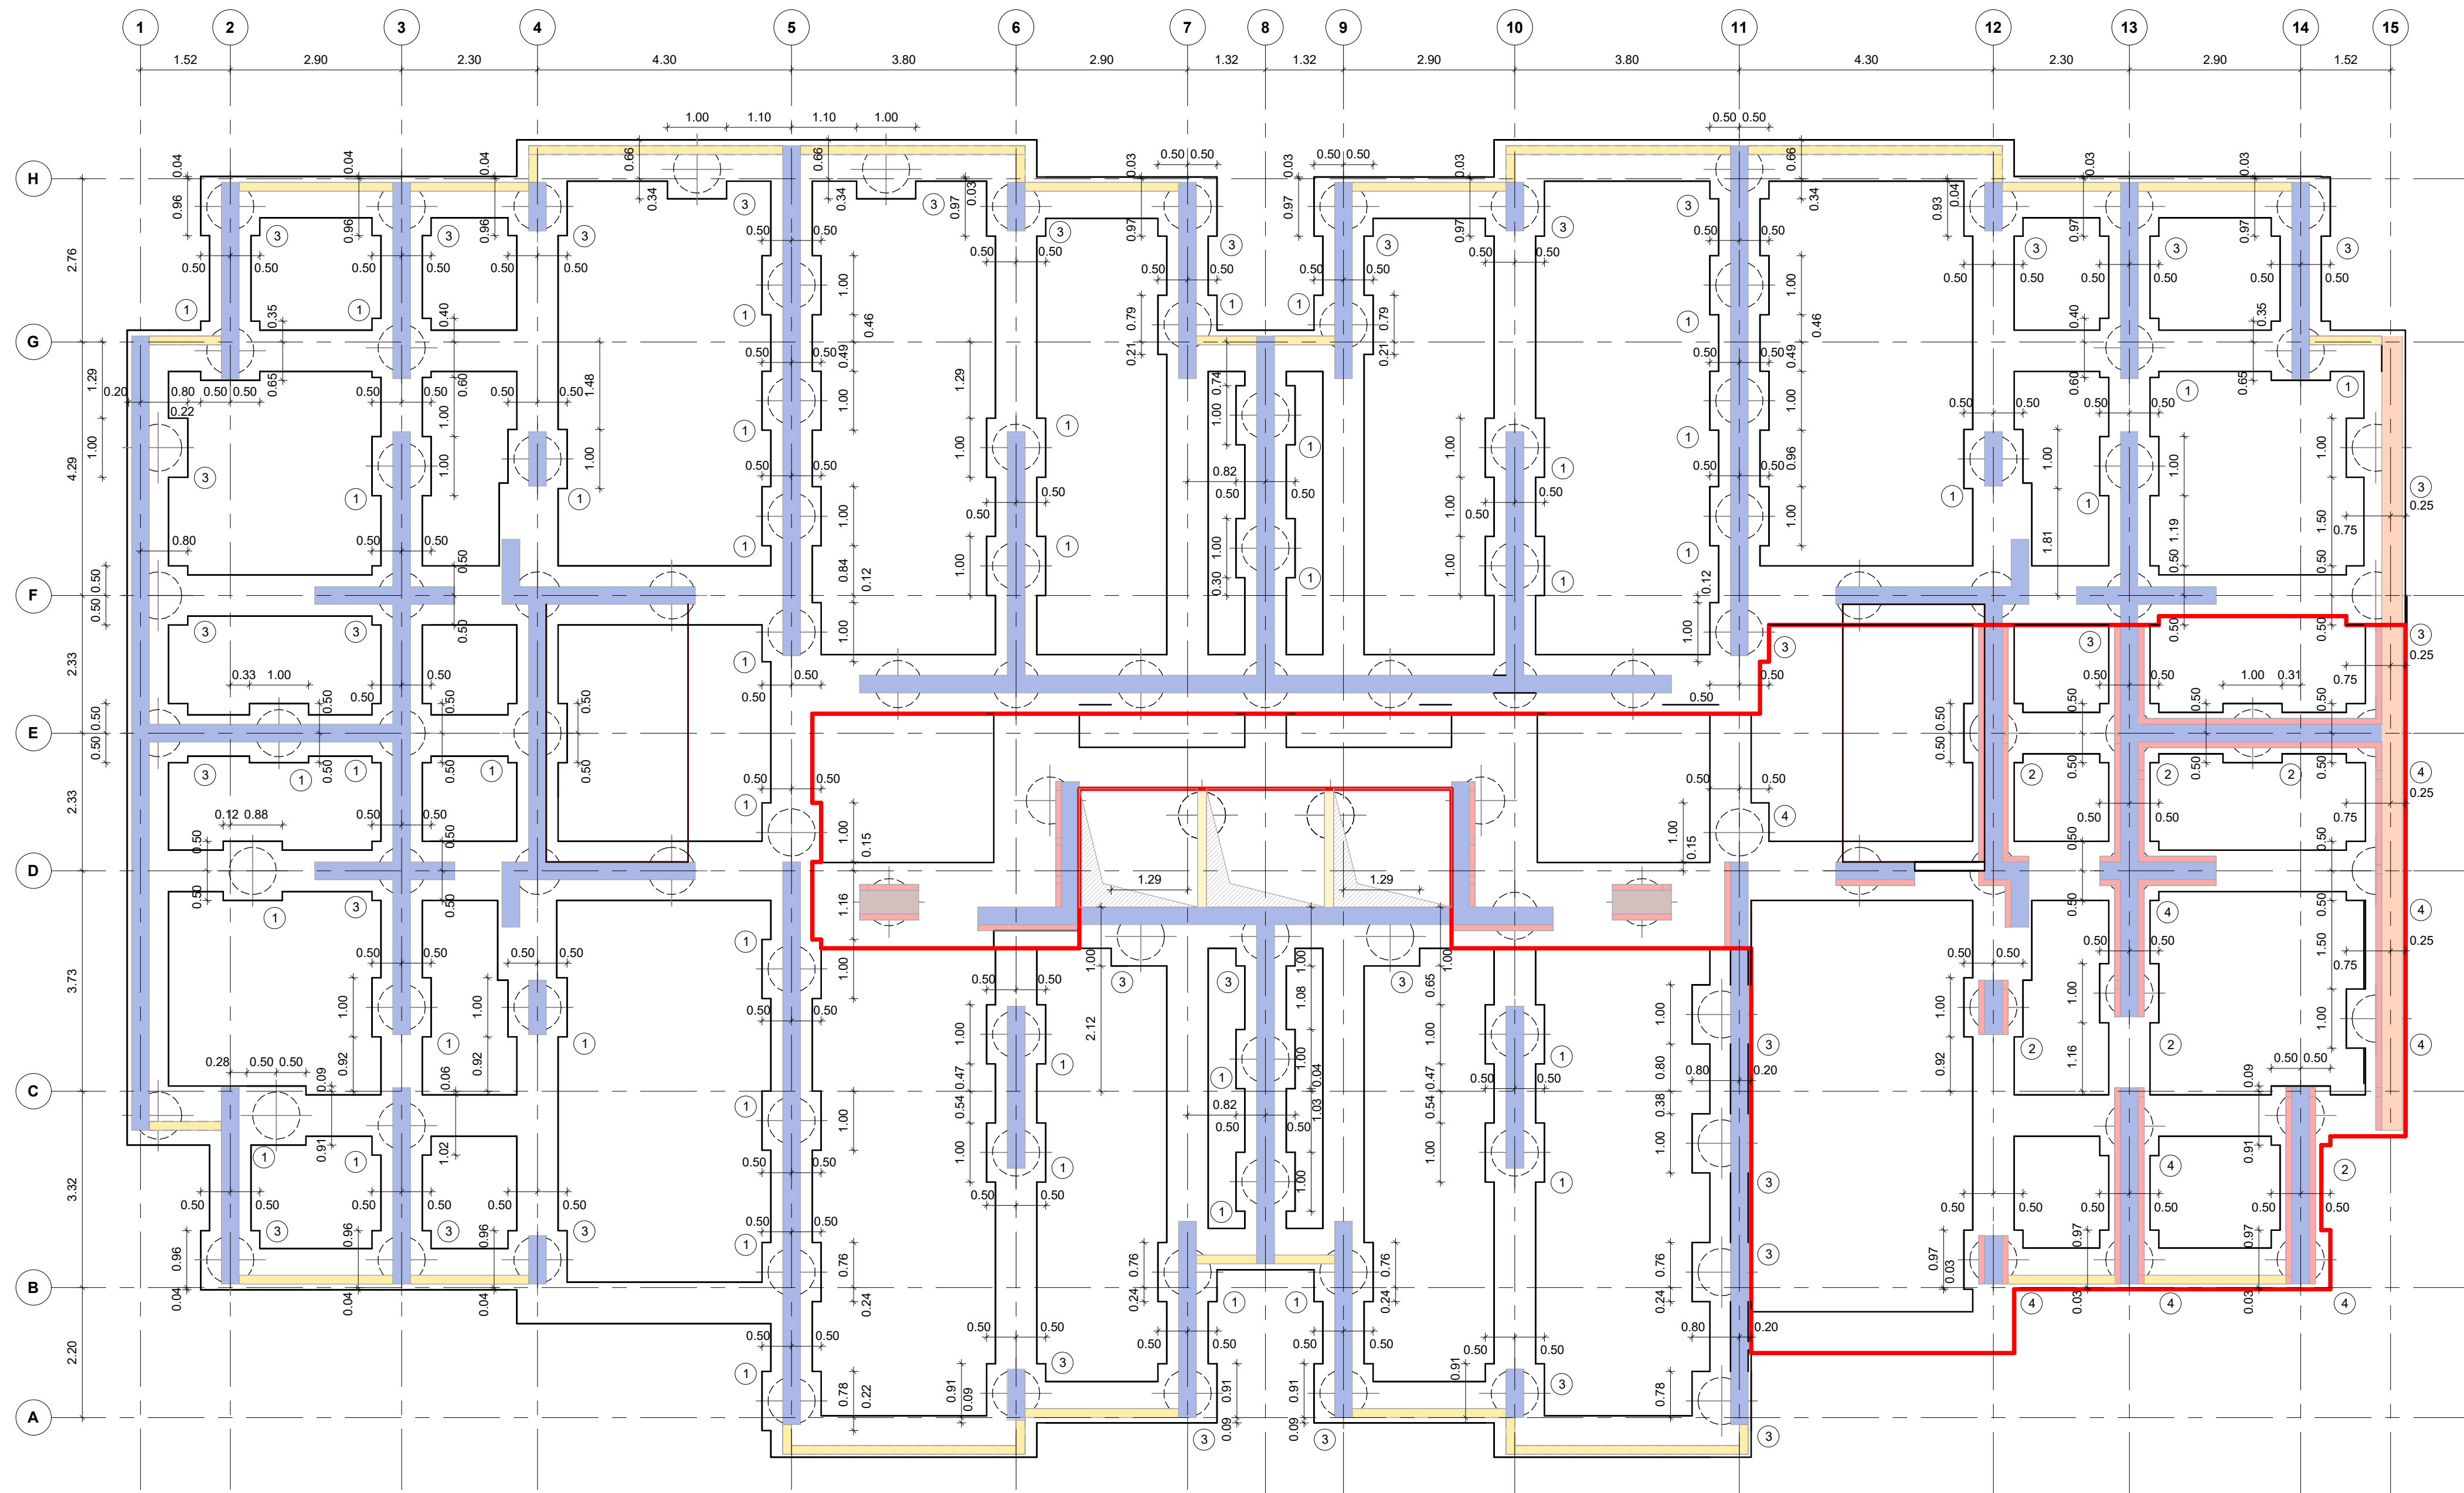


PLANTA DE LOCALIZACIÓN DE DADOS N.E -0.82 Y N.E -1.42
Escala 1 : 75

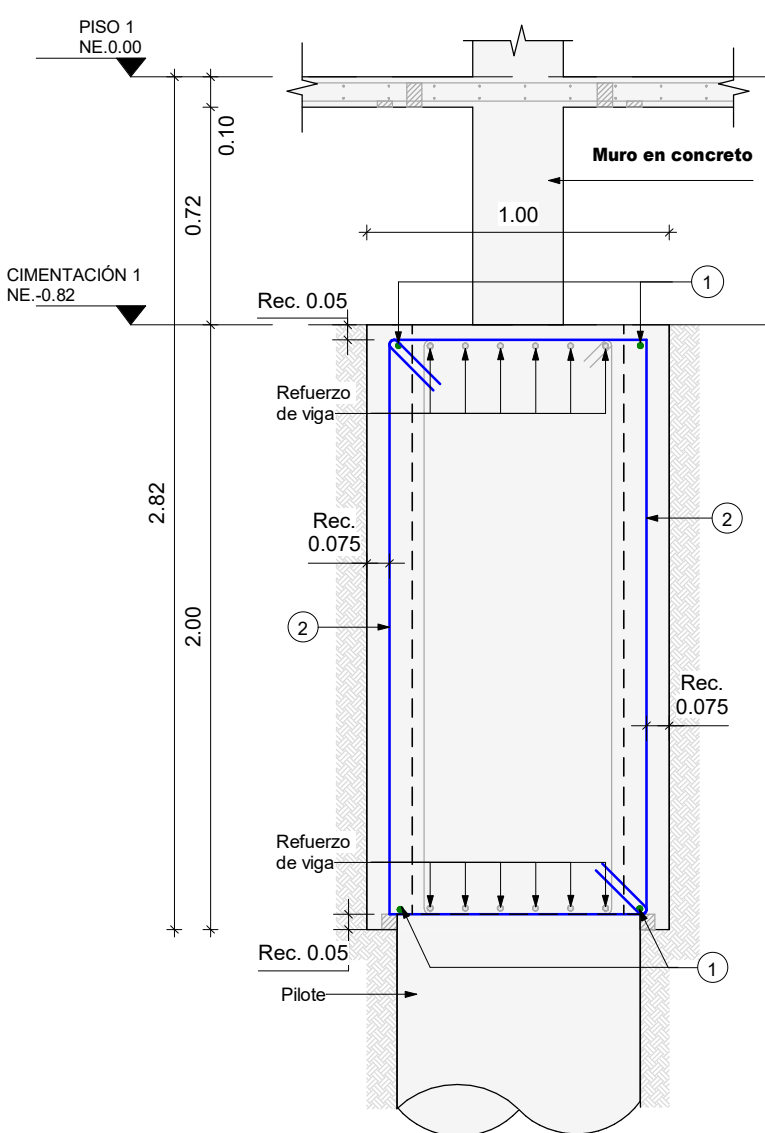


CORTE D1
Escala 1 : 25
DADO TIPO 1

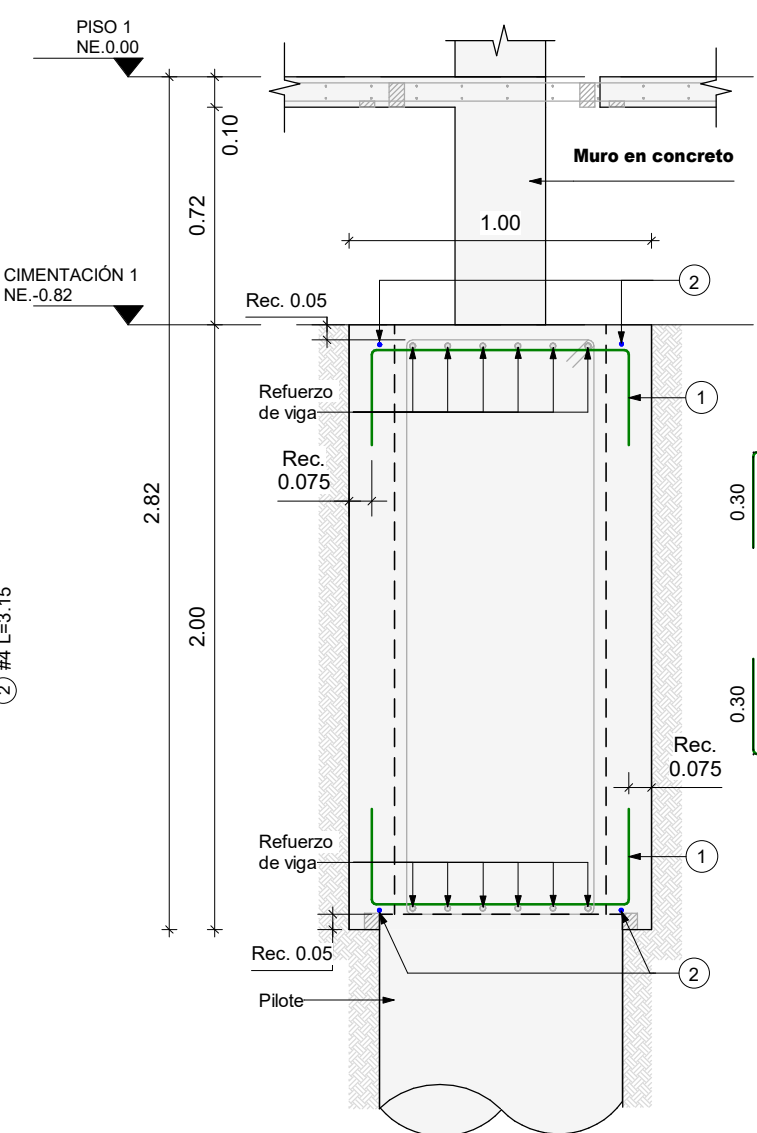


CORTE D2
Escala 1 : 25
DADO TIPO 1 Y 3

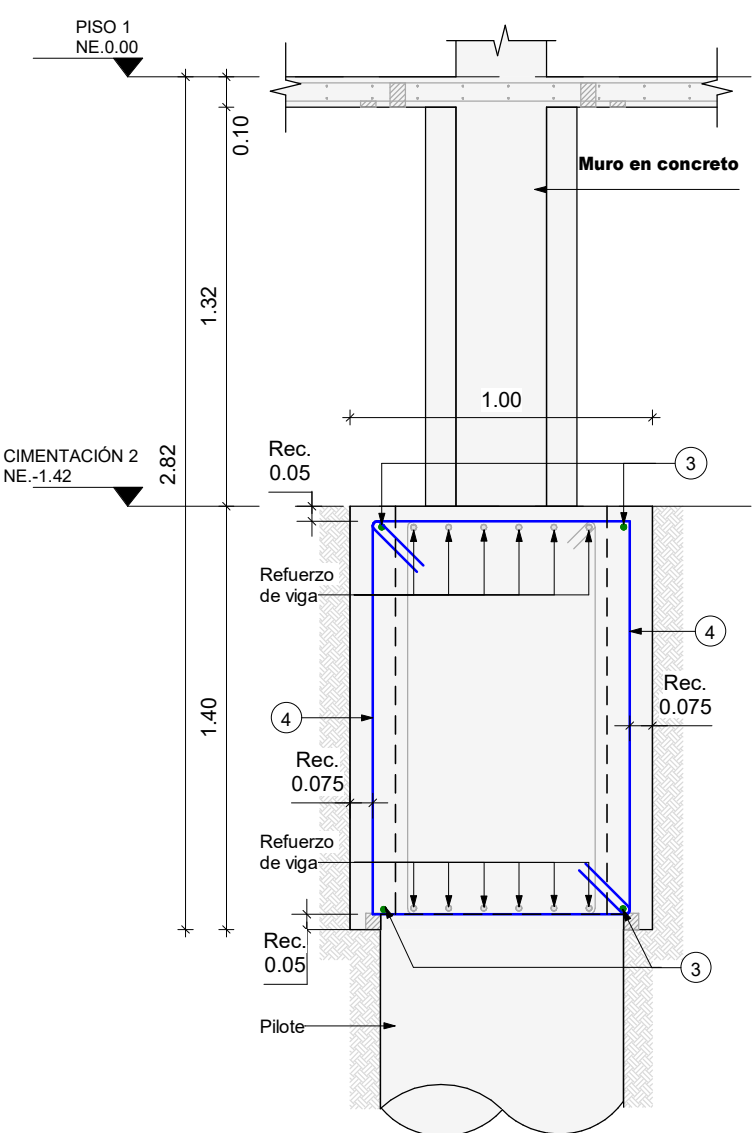


CORTE D1
Escala 1 : 25
DADO TIPO 2

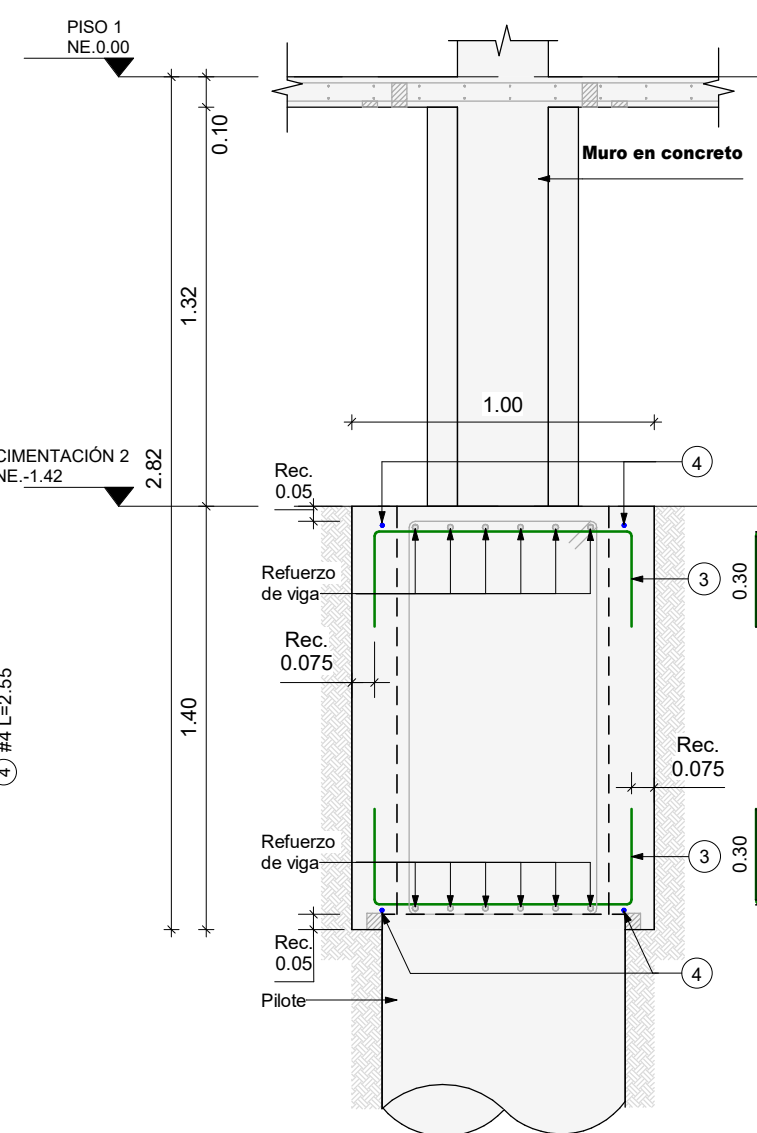

CORTE D2
Escala 1 : 25
DADO TIPO 2 Y 4

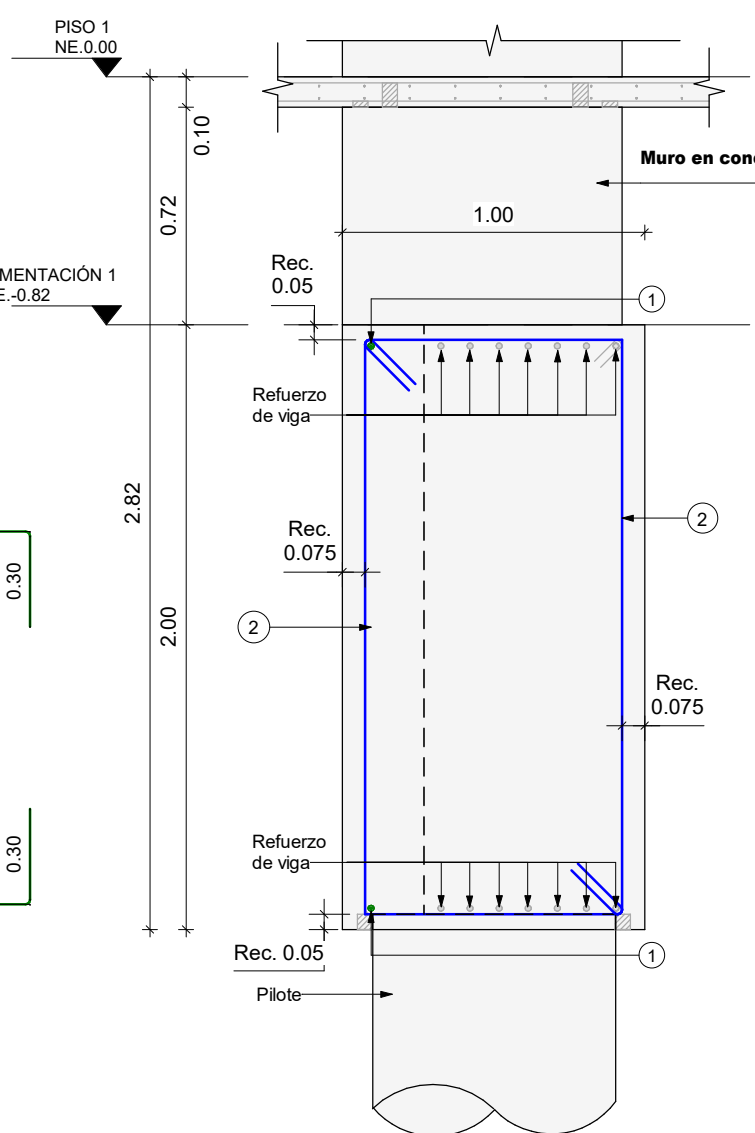

CORTE D3
Escala 1 : 25
DADO TIPO 3

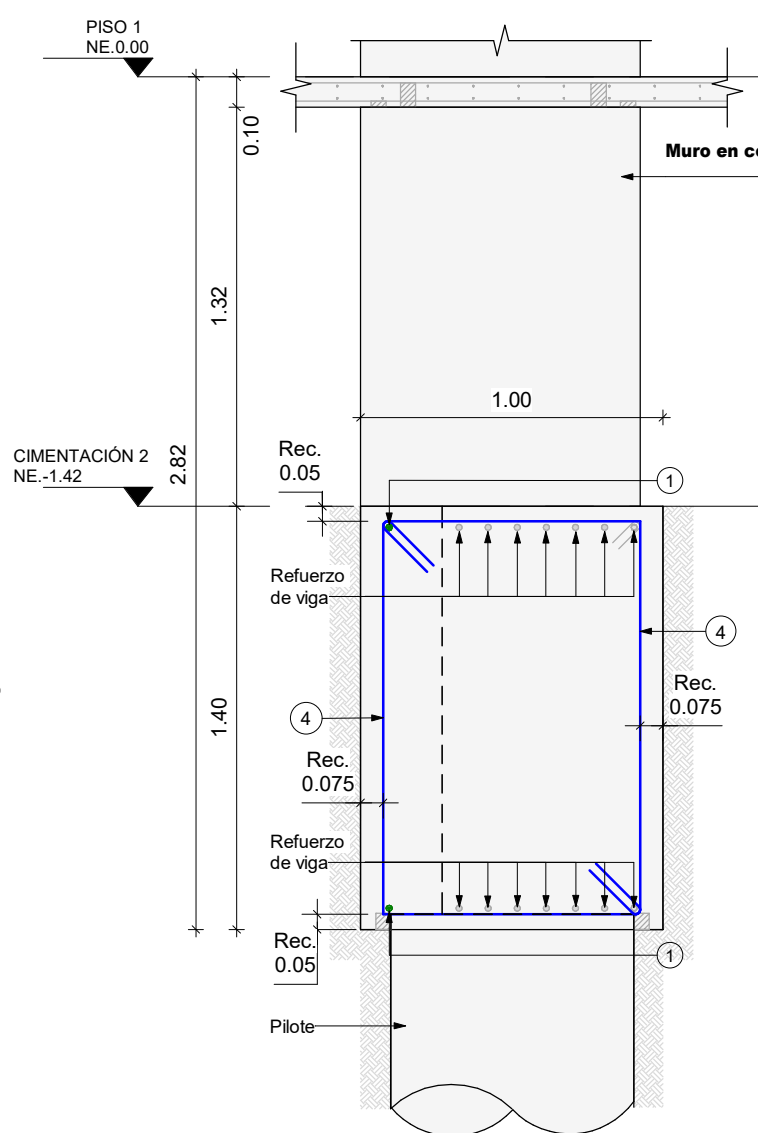

CORTE D4
Escala 1 : 25
DADO TIPO 4

TABLA DE DADOS	
No Dado	Cant.
1	44
2	6
3	36
4	9

NOTA:
Este plano debe ser revisado y aprobado por el
Ingeniero de suelos.

VºBº INGENIERO DE SUELOS

CONVENCIONES

- Indica tipo de dado
- Indica muro $e=0.15$
- Indica muro $e=0.30$
- Indica muro $e=0.35$
- Indica muro $e=0.40$
- Indica zona cambio de profundidad

CONCRETO

$f_c=35$ MPa
 $f_c=350$ kg/cm²
 $f_c=5000$ psi

NOTAS

- Ver detalles generales en el PL. 01.02 y 01.03
- Ver despiece foso de ascensor en PL. 03.04

VERSIÓN :

3

PLANO Nº
03.03

Aycardi
Estructural

GERENTE DE PROYECTO

ROBERTO AYCARDI F.
MAT. 2520257258 CND

INGENIERO

CARLOS ANDRÉS WILCHES C.

MODELADOR

DANIEL CASTELLANOS

MODIFICACIONES

MODIFICACIONES	FECHA
Emisión Inicial	20-02-2025
Se incluyen datos tipo 1 sobre eje H-5 y se incluyen detalles de datos tipo 3 y 4	03-10-2025
Actualización datos ejes C-1 y D-2	29-01-2026



LA SCALA

LA SCALA_EST_TOR-1

TORRE 1

CALLE 170 CON AV. BOYACA

PLANTA DE LOCALIZACIÓN DE DADOS Y
DETALLES

LA SCALA_EST_TOR-1_03.03_LOAD

REVISOR ESTRUCTURAL

RAMÓN ANDRÉS ALVAREZ MANTILLA
MAT. 25202-346546 CND.

PLANO Nº

VERSIÓN :

03.03

3