


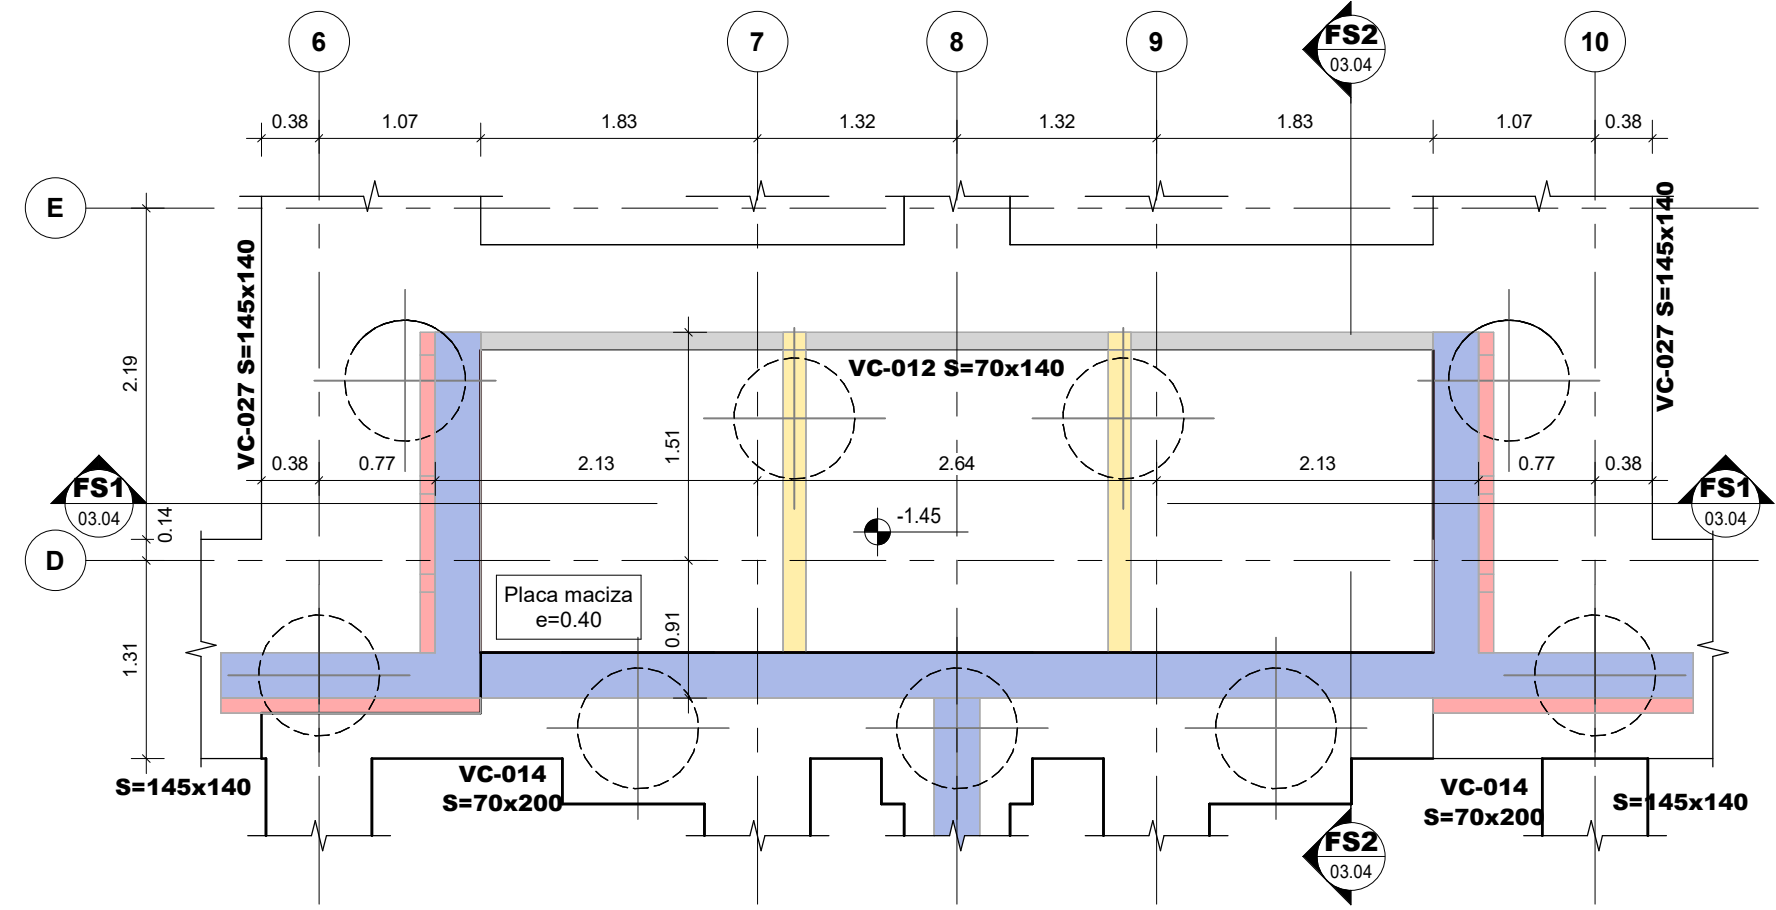


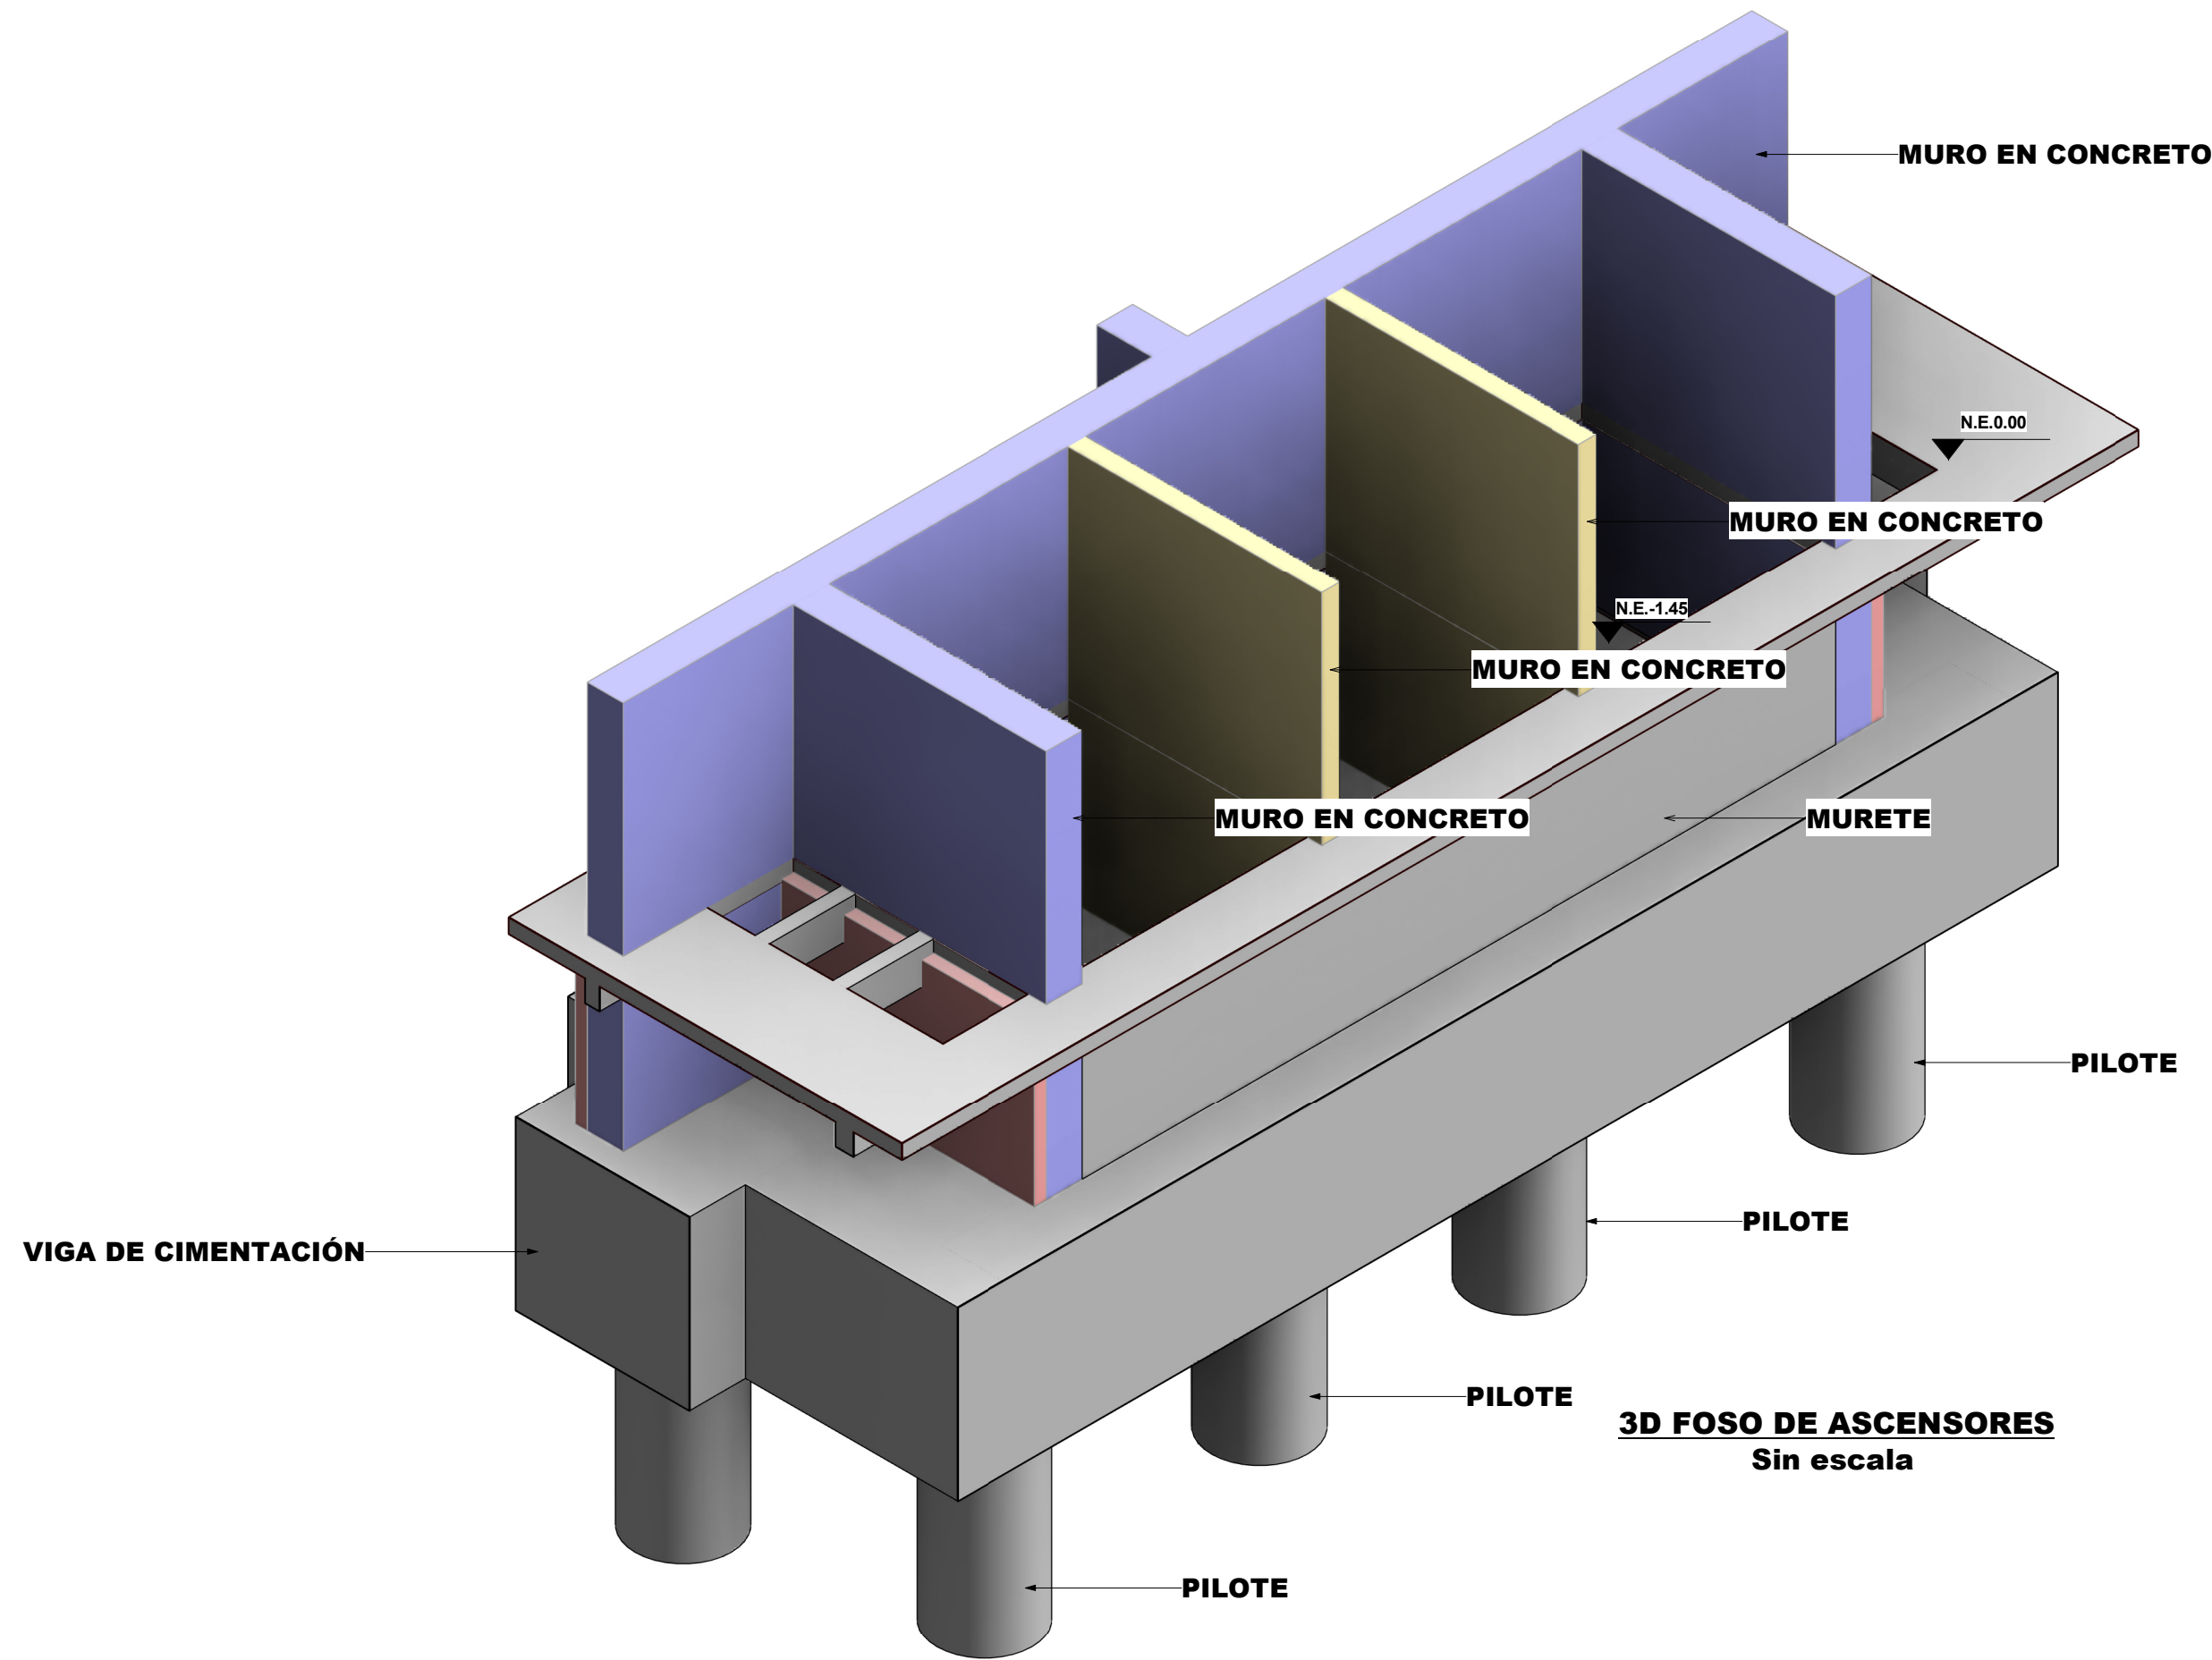


PLANTA DE CIMENTACIÓN FOSO ASCENSORES
Escala 1 : 50

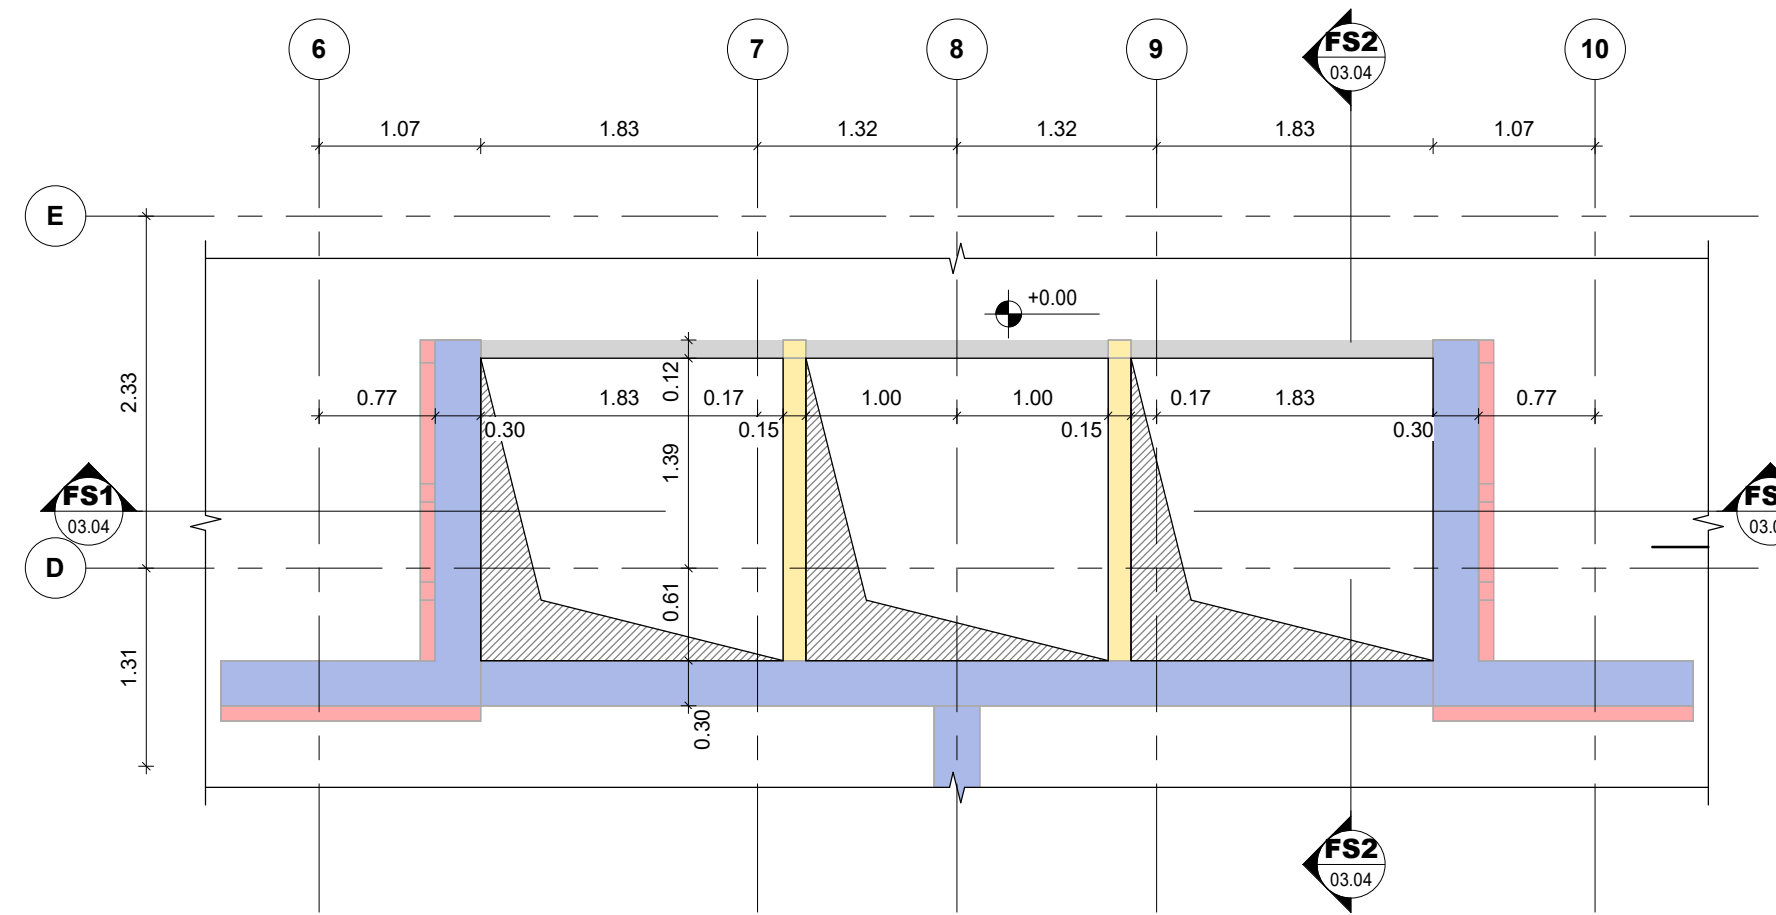

PLANTA FOSO DE ASCENSORES NIVEL 0.00
Escala 1 : 50

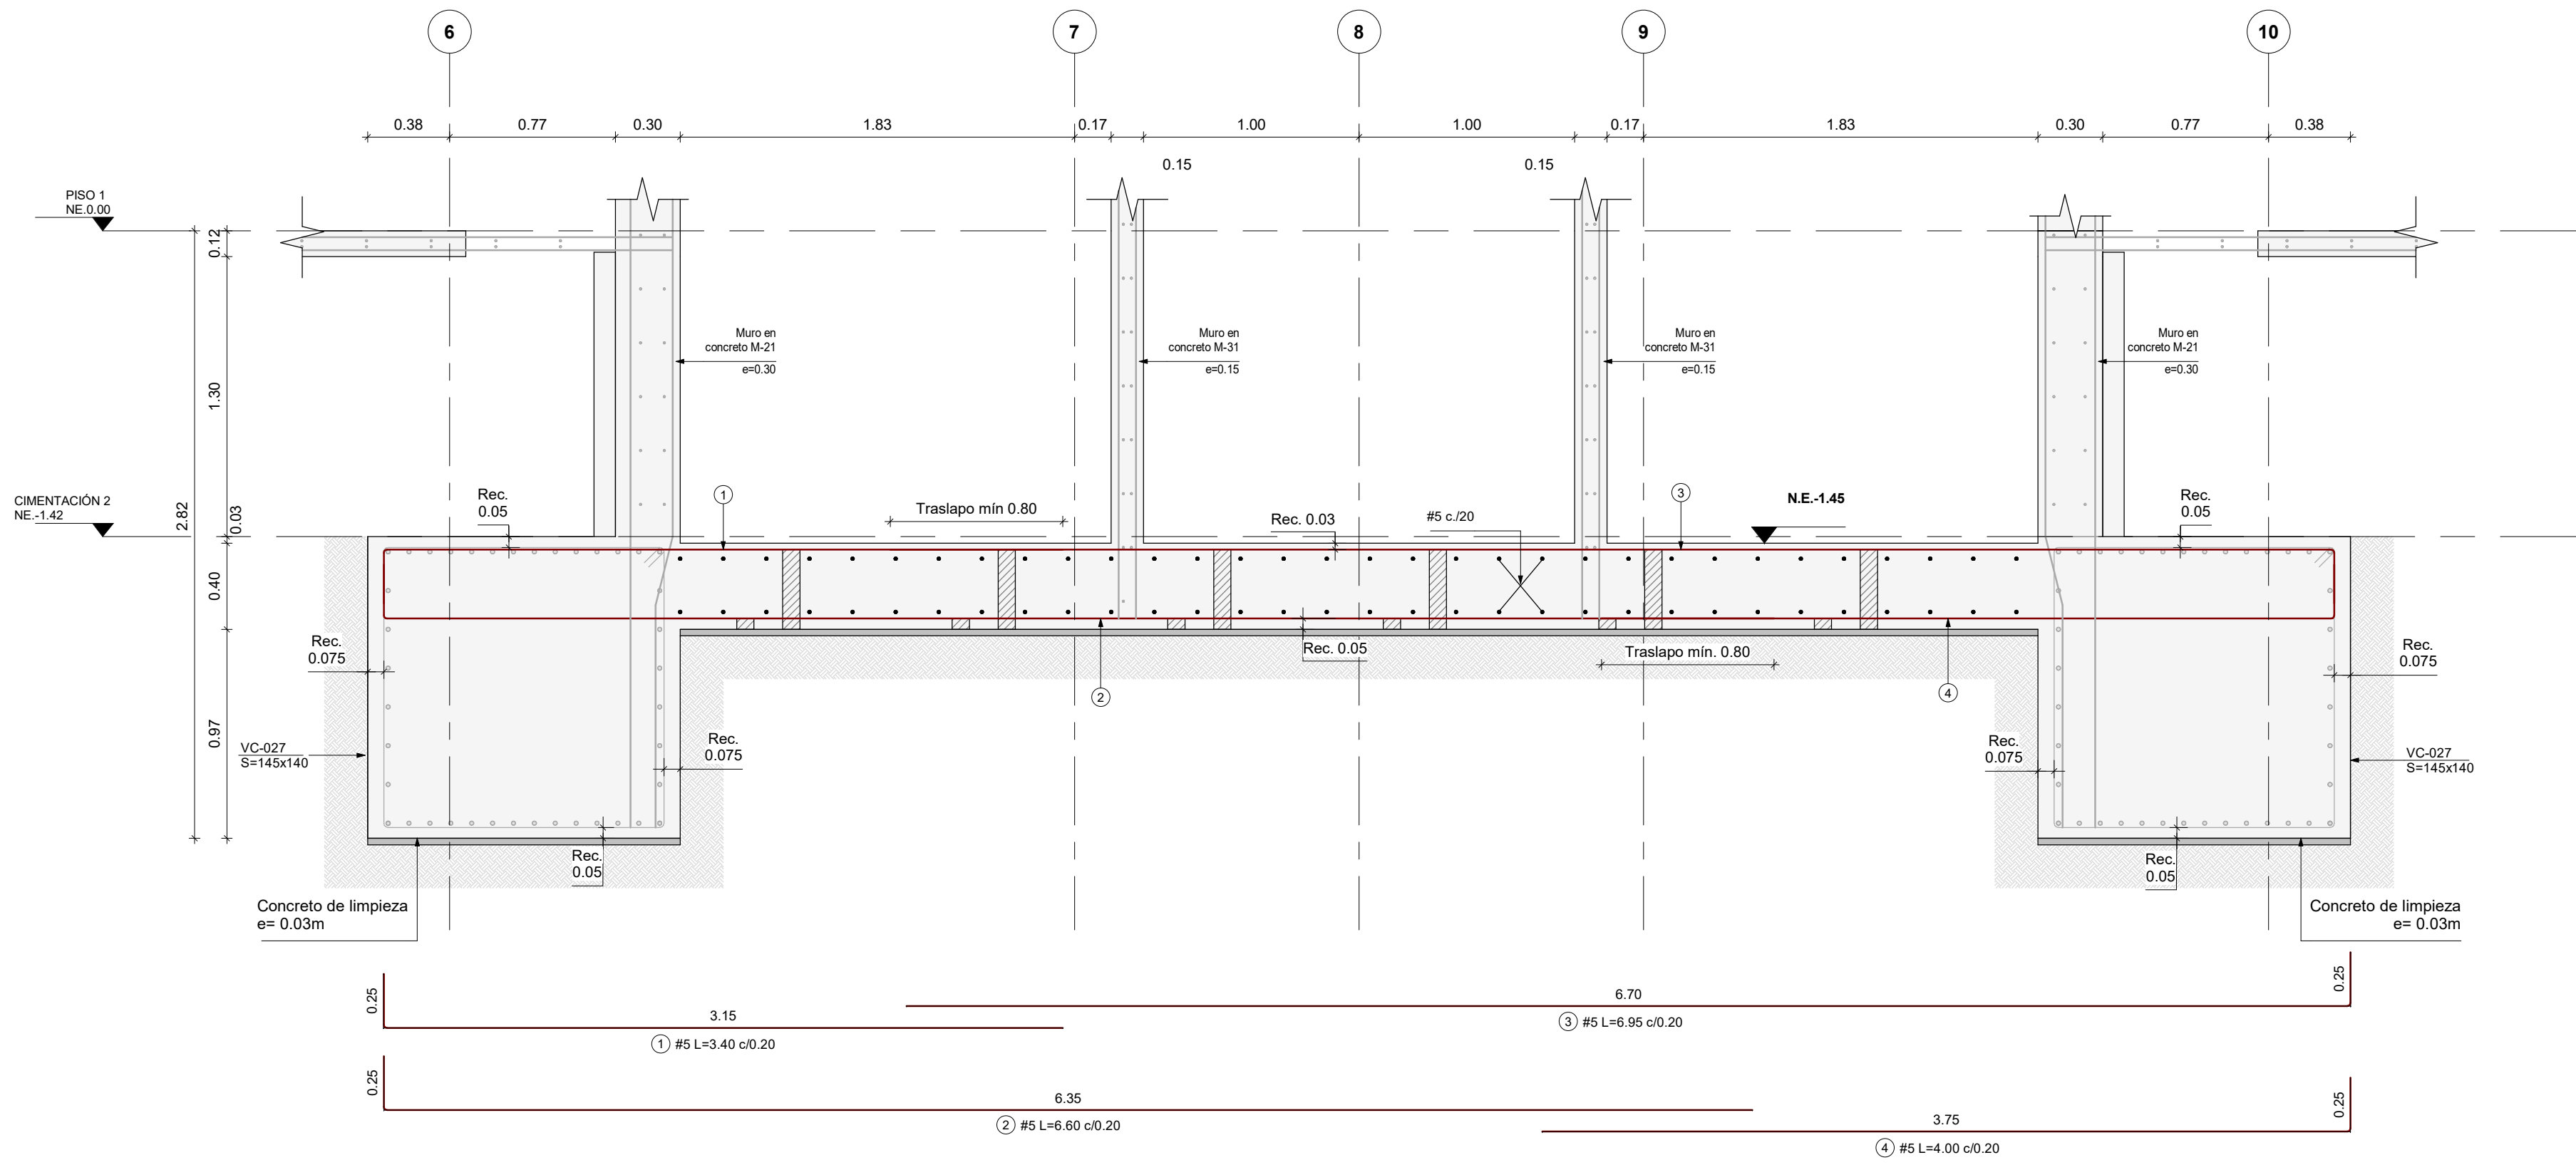

CORTE FS-1
Escala 1 : 25

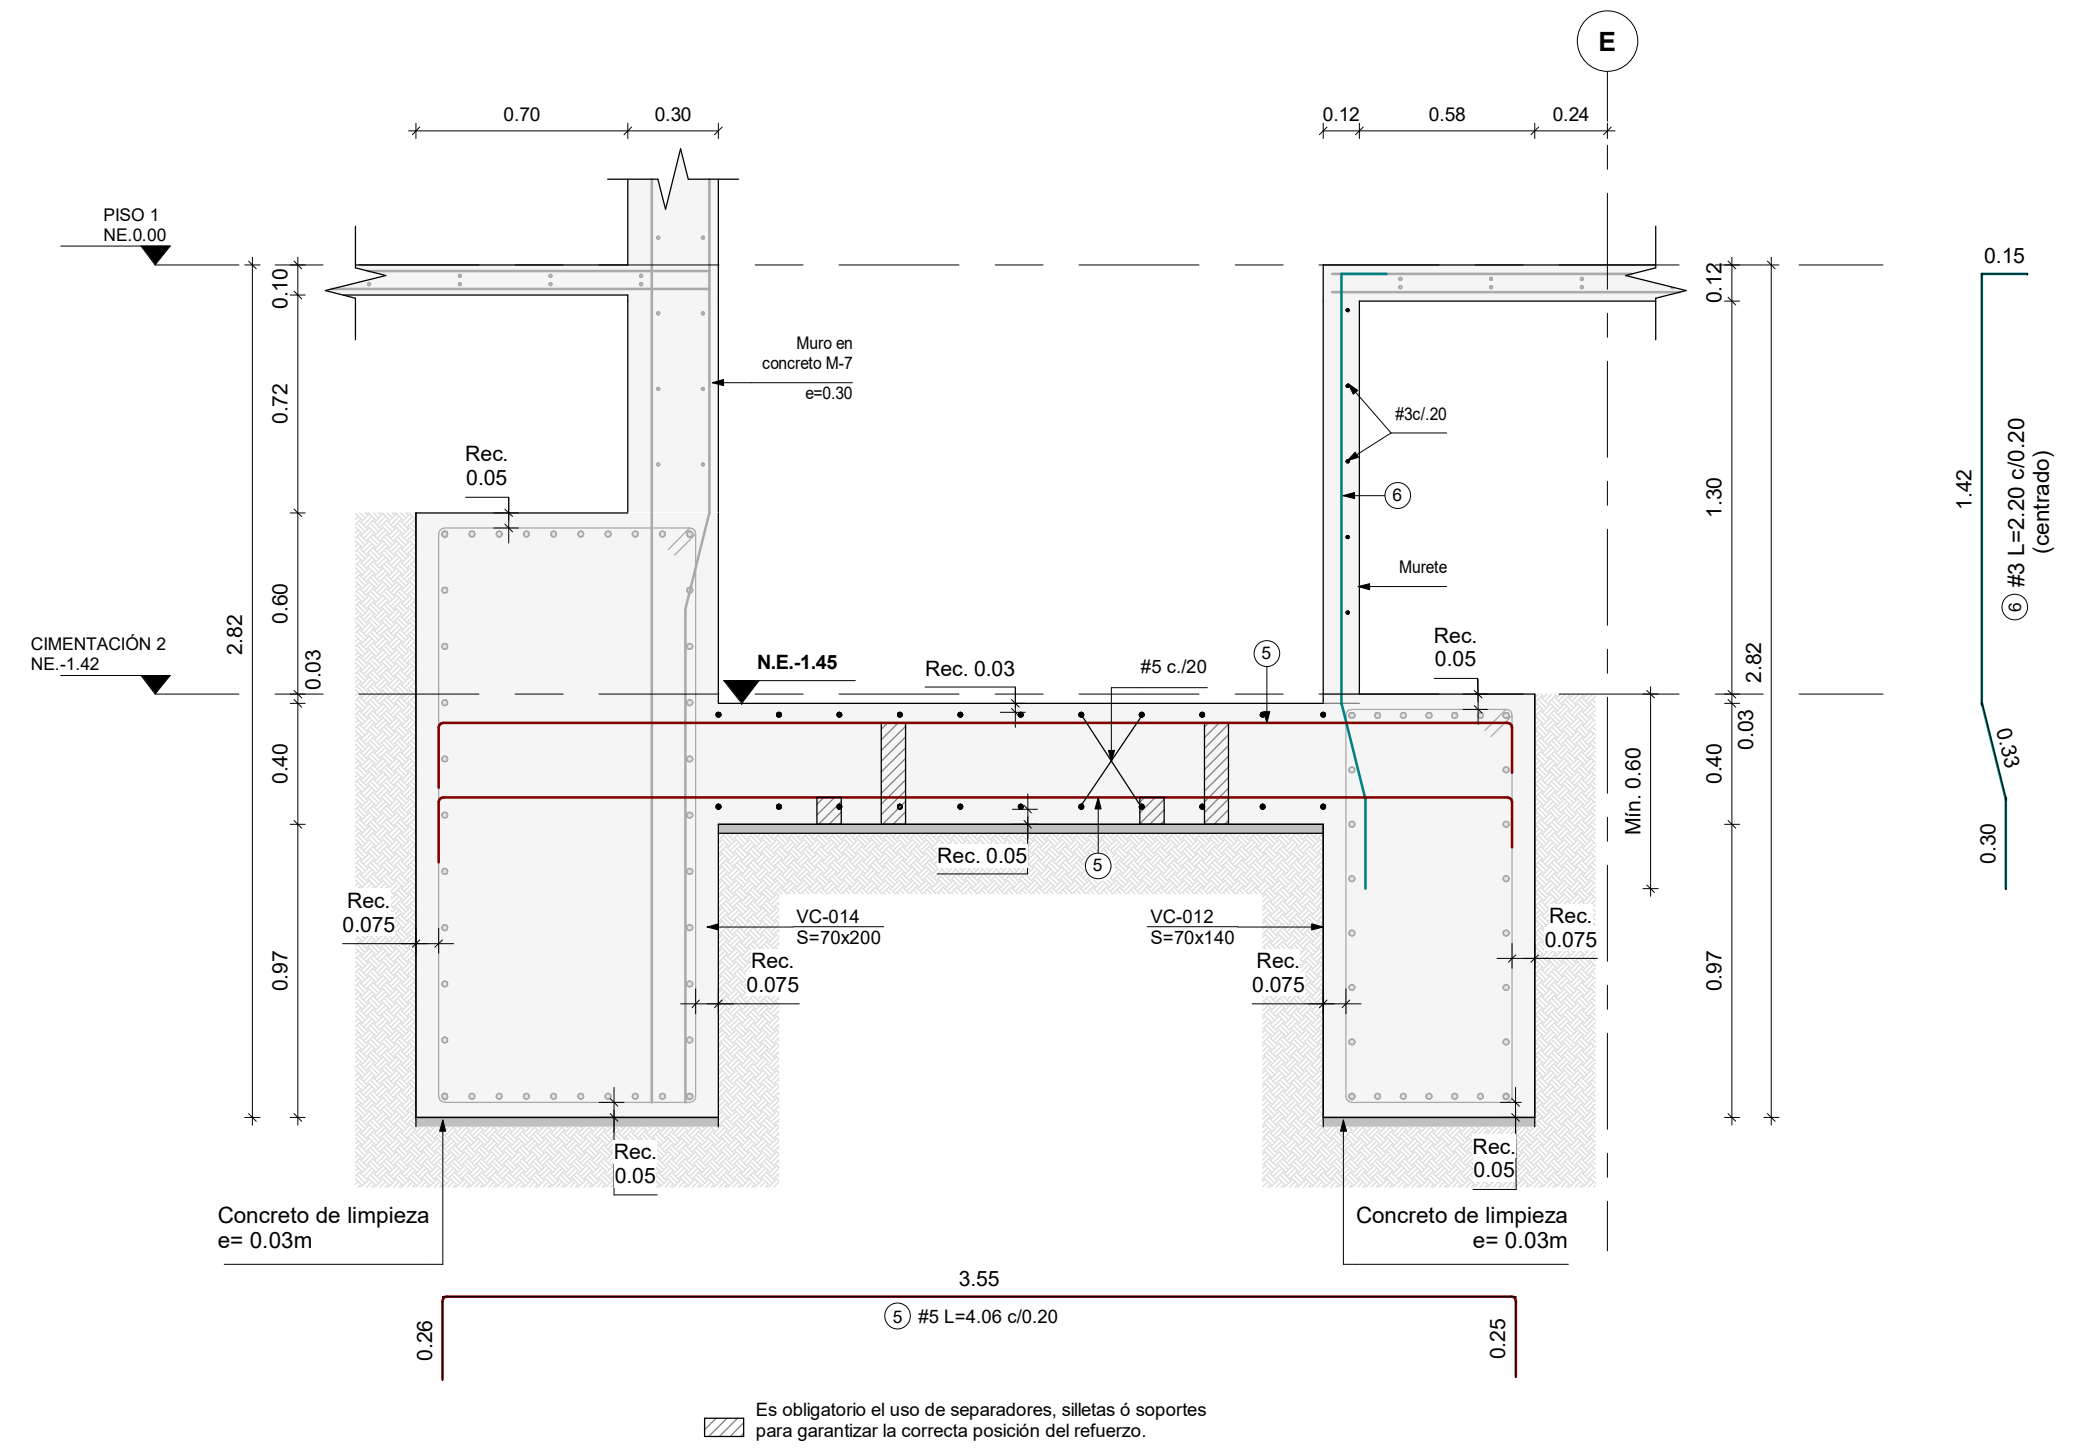

CORTE FS-2
Escala 1 : 25

NOTA:
Este plano debe ser revisado y aprobado por el
Ingeniero de suelos.

V"B" INGENIERO DE SUELOS

CONCRETO
f'c=35 MPa
f'c=350 kg/cm²
f'c=5000 psi

CONVENCIONES
Indica muro e=0.15
Indica muro e=0.30
Indica murete

NOTAS

1. La profundidad del foso del ascensor se debe verificar
con las especificaciones del proveedor.

VERSIÓN :

2

PLANO N°
03.04

GERENTE DE PROYECTO
ROBERTO AYCARDI F.
MAT. 2520257258 CND

INGENIERO
CARLOS ANDRÉS WILCHES C.

MODELADOR
DANIEL CASTELLANOS

MODIFICACIONES		FECHA
Emisión Inicial	Ajuste distribución de refuerzo cortes FS-1 Y FS-2	20-02-2025
		03-10-2025



LA SCALA

LA SCALA_EST_TOR-1
TORRE 1

CALLE 170 CON AV. BOYACA

DESPIECE FOSO DE ASCENSORES

LA SCALA_EST_TOR-1_03.04_DT-FS

REVISOR ESTRUCTURAL
RAMÓN ANDRÉS ALVAREZ MANTILLA
MAT. 25202-346546 CND.

PLANO N°

03.04

VERSIÓN :

2