


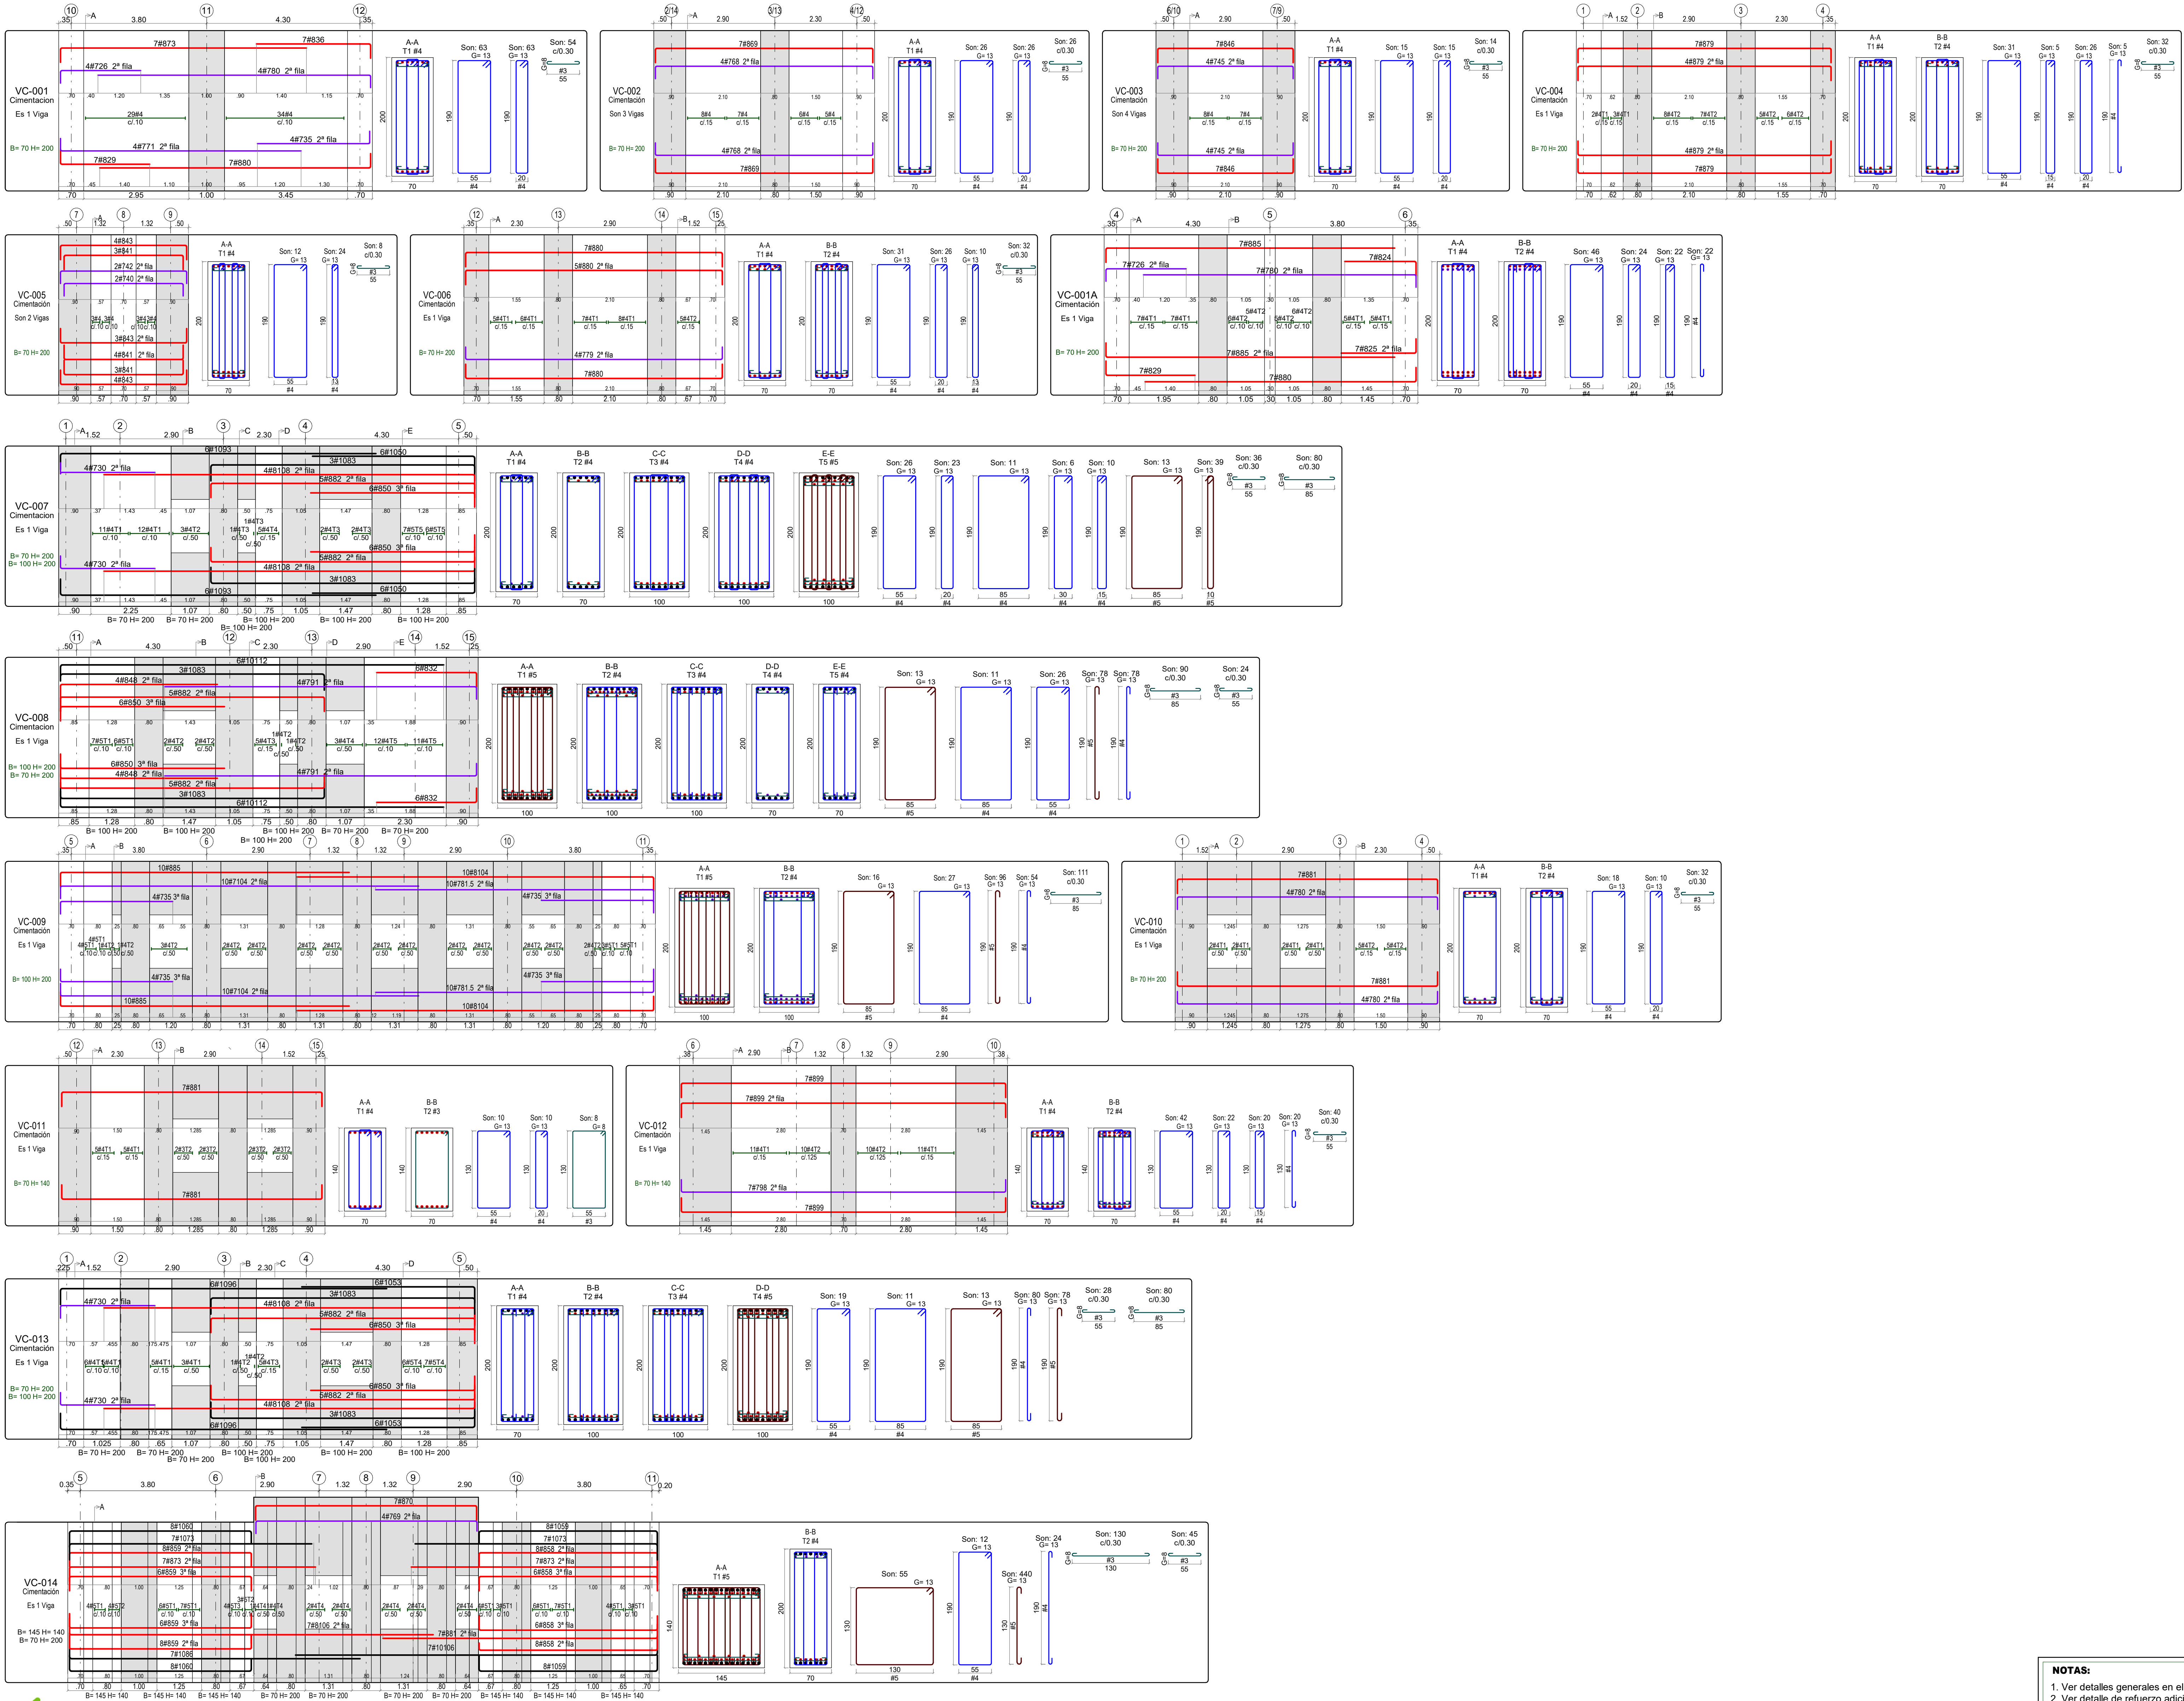

VERSIÓN :

3

PLANO N°

03.05



GERENTE DE PROYECTO

ROBERTO AYCARDI F.
MAT. 2520257258 CND

INGENIERO

CARLOS ANDRÉS WILCHES C.

MODELADOR

DANIEL CASTELLANOS

MODIFICACIONES	FECHA
Emisión Inicial	20-02-2025
Se inserta despiece VC-001A, se actualiza cantidad de viga VC-001 y se actualizan longitudes ganchos estribos	03-10-2025
Se actualiza cantidad de viga VC-004 y se actualiza despiece vigas VC-007, VC-008 y VC-013	29-01-2026



LA SCALA

LA SCALA_EST_TOR-1

TORRE 1

CALLE 170 CON AV. BOYACA

DESPIECE VIGAS DE CIMENTACIÓN

LA SCALA_EST_TOR-1_03.05_CIM-D1

REVISOR ESTRUCTURAL

RAMÓN ANDRÉS ALVAREZ MANTILLA
MAT. 25202-346546 CND.

PLANO N°

03.05

VERSIÓN :

3

NOTAS:
1. Ver detalles generales en el PL. N° 01.02
2. Ver detalle de refuerzo adicional lateral en la cara para vigas altas en PL. N° 01.02
3. Ver planta de cimentación en el PL. N° 03.01

ESCALA 1:75