


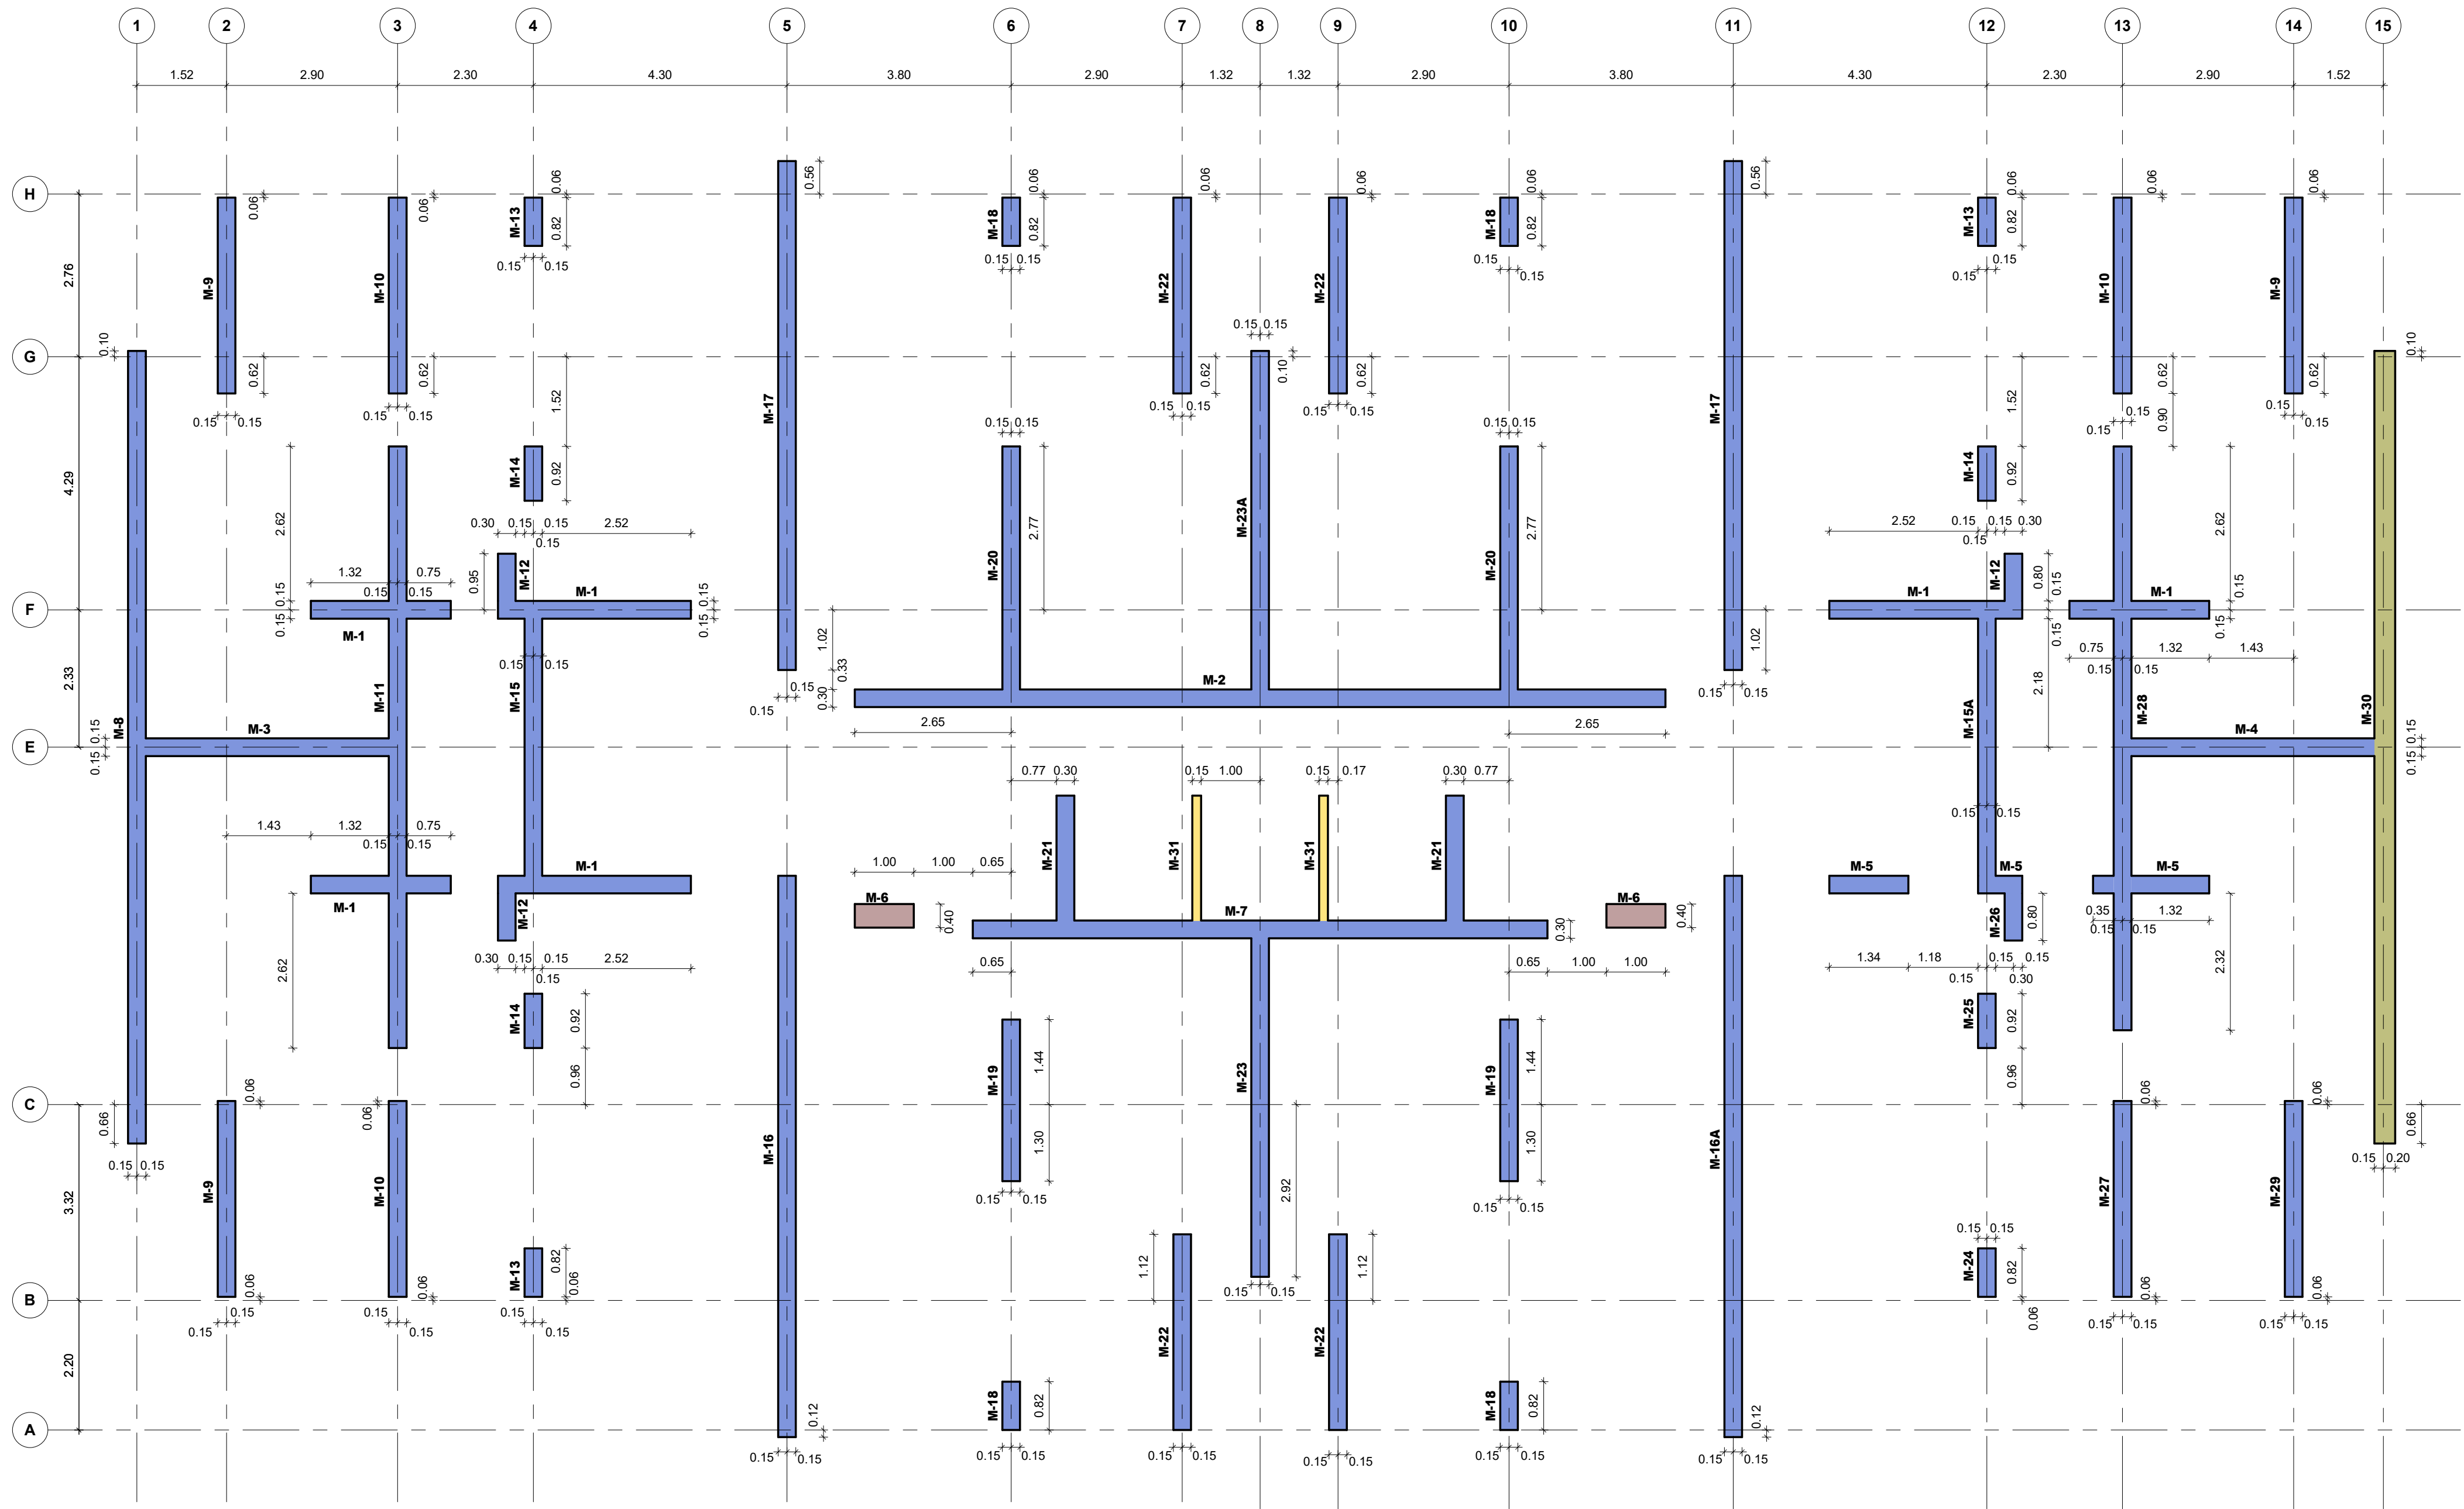

PLANTA LOCALIZACIÓN DE MUROS PISO 1  
Escala 1 : 75

| CONCRETO:                 |                           |                           |                           |
|---------------------------|---------------------------|---------------------------|---------------------------|
| MUROS                     |                           |                           |                           |
| * DE CIMENTACIÓN A PISO 8 | * DE PISO 8 A PISO 15     | * DE PISO 15 A PISO 22    | * DE PISO 22 A CUBIERTA   |
| $f_c=49 \text{ MPa}$      | $f_c=42 \text{ MPa}$      | $f_c=35 \text{ MPa}$      | $f_c=28 \text{ MPa}$      |
| $f_c=490 \text{ kg/cm}^2$ | $f_c=420 \text{ kg/cm}^2$ | $f_c=350 \text{ kg/cm}^2$ | $f_c=280 \text{ kg/cm}^2$ |
| $f_c=7000 \text{ psi}$    | $f_c=6000 \text{ psi}$    | $f_c=5000 \text{ psi}$    | $f_c=4000 \text{ psi}$    |

| CONVENCIONES                                            |                    |
|---------------------------------------------------------|--------------------|
| M-#                                                     | Indica N° de Muro  |
|                                                         | Indica muro e=0.15 |
|                                                         | Indica muro e=0.30 |
|                                                         | Indica muro e=0.35 |
|                                                         | Indica muro e=0.40 |
| NOTAS                                                   |                    |
| 1. Ver detalles generales en PL. N°01.02                |                    |
| 2. Ver despliegos de muros en PL. N° 11.00 a PL N°11.21 |                    |
| 3. Ver detalles de muros en PL N.° 11.22                |                    |

VERSIÓN :

2

PLANO N° 04.00



GERENTE DE PROYECTO

ROBERTO AYCARDI F.  
MAT. 2520257258 CND

INGENIERO

CARLOS ANDRÉS WILCHES C.

MODELADOR

DANIEL CASTELLANOS

| MODIFICACIONES                     | FECHA      |
|------------------------------------|------------|
| Emisión Inicial                    | 28-02-2025 |
| Se actualiza longitud de muro M-19 | 04-11-2025 |
|                                    |            |
|                                    |            |
|                                    |            |



LA SCALA

LA SCALA\_EST\_TOR-1

TORRE 1

CALLE 170 CON AV. BOYACA

PLANTA LOCALIZACIÓN DE MUROS PISO 1

LA SCALA\_EST\_TOR-1\_04.00\_LCM-P1

REVISOR ESTRUCTURAL

RAMÓN ÁNDRES ALVAREZ MANTILLA  
MAT. 25202-346546 CND.

PLANO N°

04.00

VERSIÓN :

2