


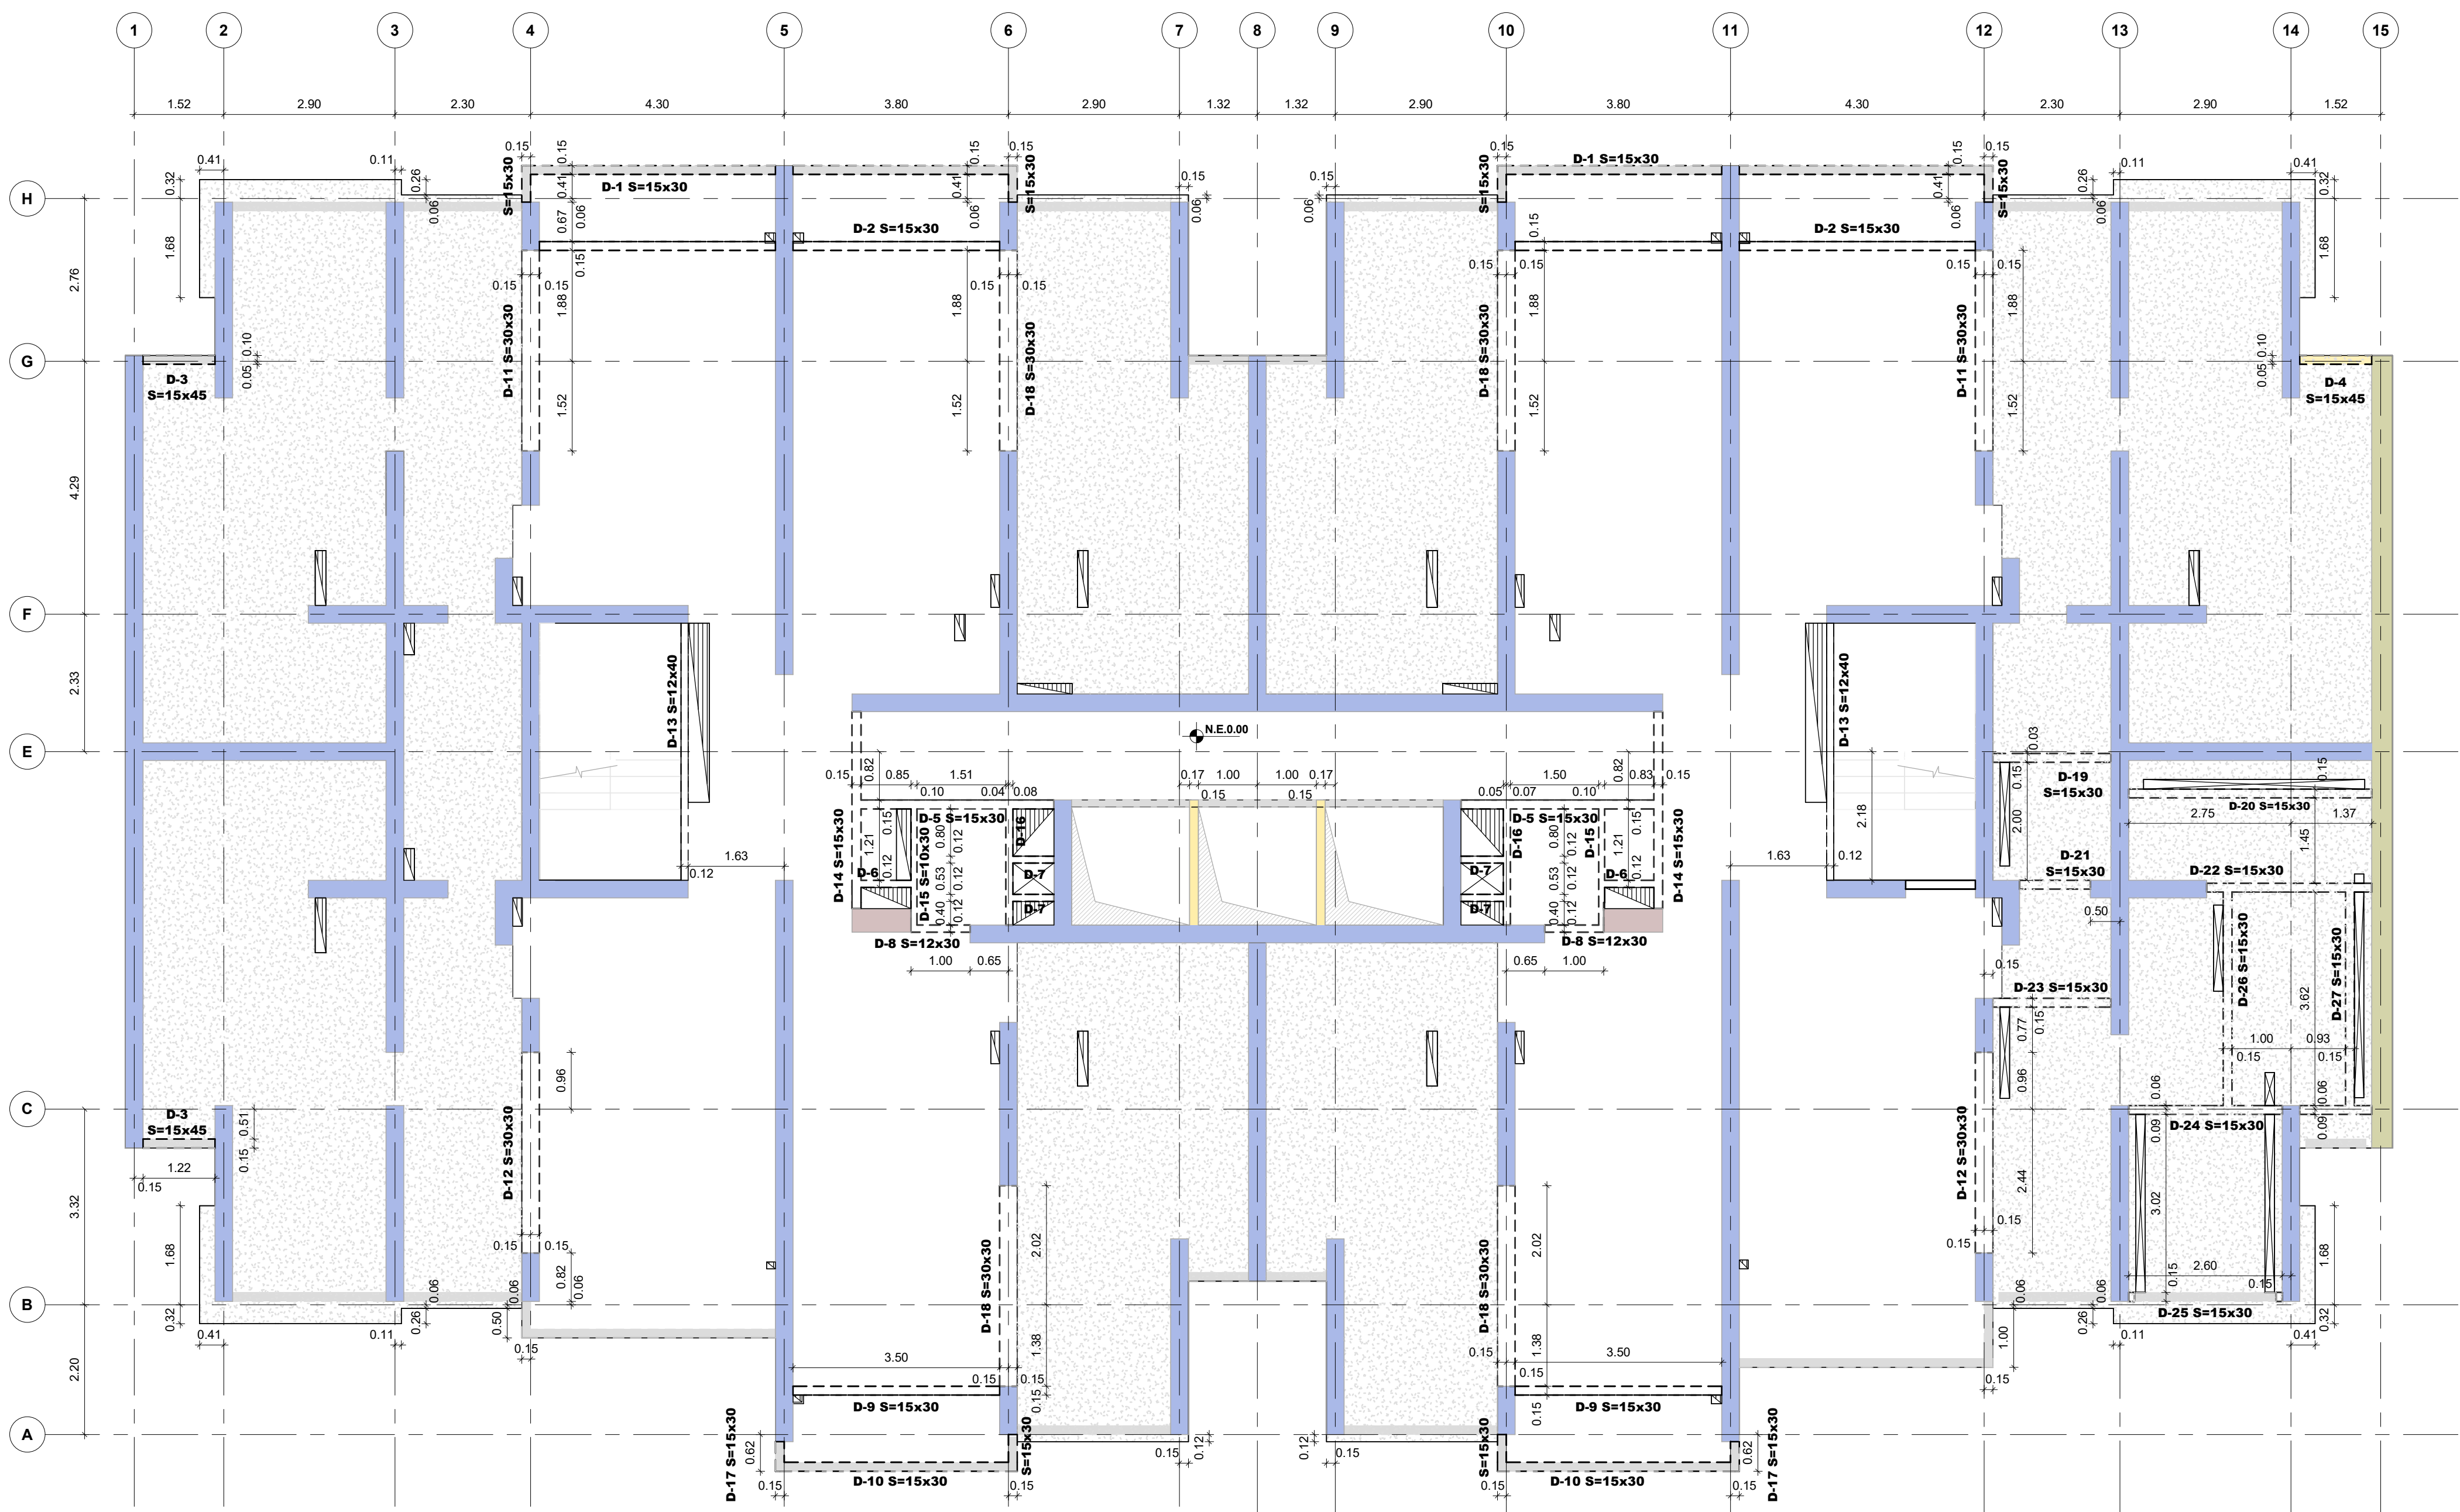

PLANTA LOCALIZACIÓN DE DINTELES PISO 1
Escala 1 : 75

CONCRETO:			
LOSAS Y DINTELES			
* DE PISO 1 A PISO 8	* DE PISO 9 A PISO 15	* DE PISO 16 A PISO 22	* DE PISO 23 A CUBIERTA ASCENSOR Y ESCALERAS
f'c=35 MPa	f'c=32 MPa	f'c=25 MPa	f'c=21 MPa
f'c=350 kg/cm²	f'c=315 kg/cm²	f'c=245 kg/cm²	f'c=210 kg/cm²
f'c=5000 psi	f'c=4500 psi	f'c=3500 psi	f'c=3000 psi

CONVENCIONES	
	Indica dinteles
	Indica N° de dintel
	Indica muro e=0.15
	Indica muro e=0.30
	Indica muro e=0.35
	Indica muro e=0.40
	Indica muretes que mueren
	Indica placa e=0.10
	Indica placa e=0.12
NOTAS	
1. Ver detalles generales en PL. N°01.02	
2. Ver despieces de dinteles en PL. N° 10.00 a 10.04	

VERSIÓN :

2

PLANO N° 04.01



GERENTE DE PROYECTO
ROBERTO AYCARDI F.
MAT. 2520257258 CND

INGENIERO
CARLOS ANDRÉS WILCHES C.

MODELADOR
DANIEL CASTELLANOS

MODIFICACIONES	FECHA
Emisión Inicial	28-02-2025
Actualización borde de placa	03-10-2025



LA SCALA

LA SCALA_EST_TOR-1

TORRE 1

CALLE 170 CON AV. BOYACA

PLANTA LOCALIZACIÓN E IDENTIFICACIÓN
DE DINTELES PISO 1

LA SCALA_EST_TOR-1_04.01_LDINT-P1

REVISOR ESTRUCTURAL
RAMÓN ÁNDRES ALVAREZ MANTILLA
MAT. 25202-346546 CND.

PLANO N°

04.01

VERSIÓN :

2