



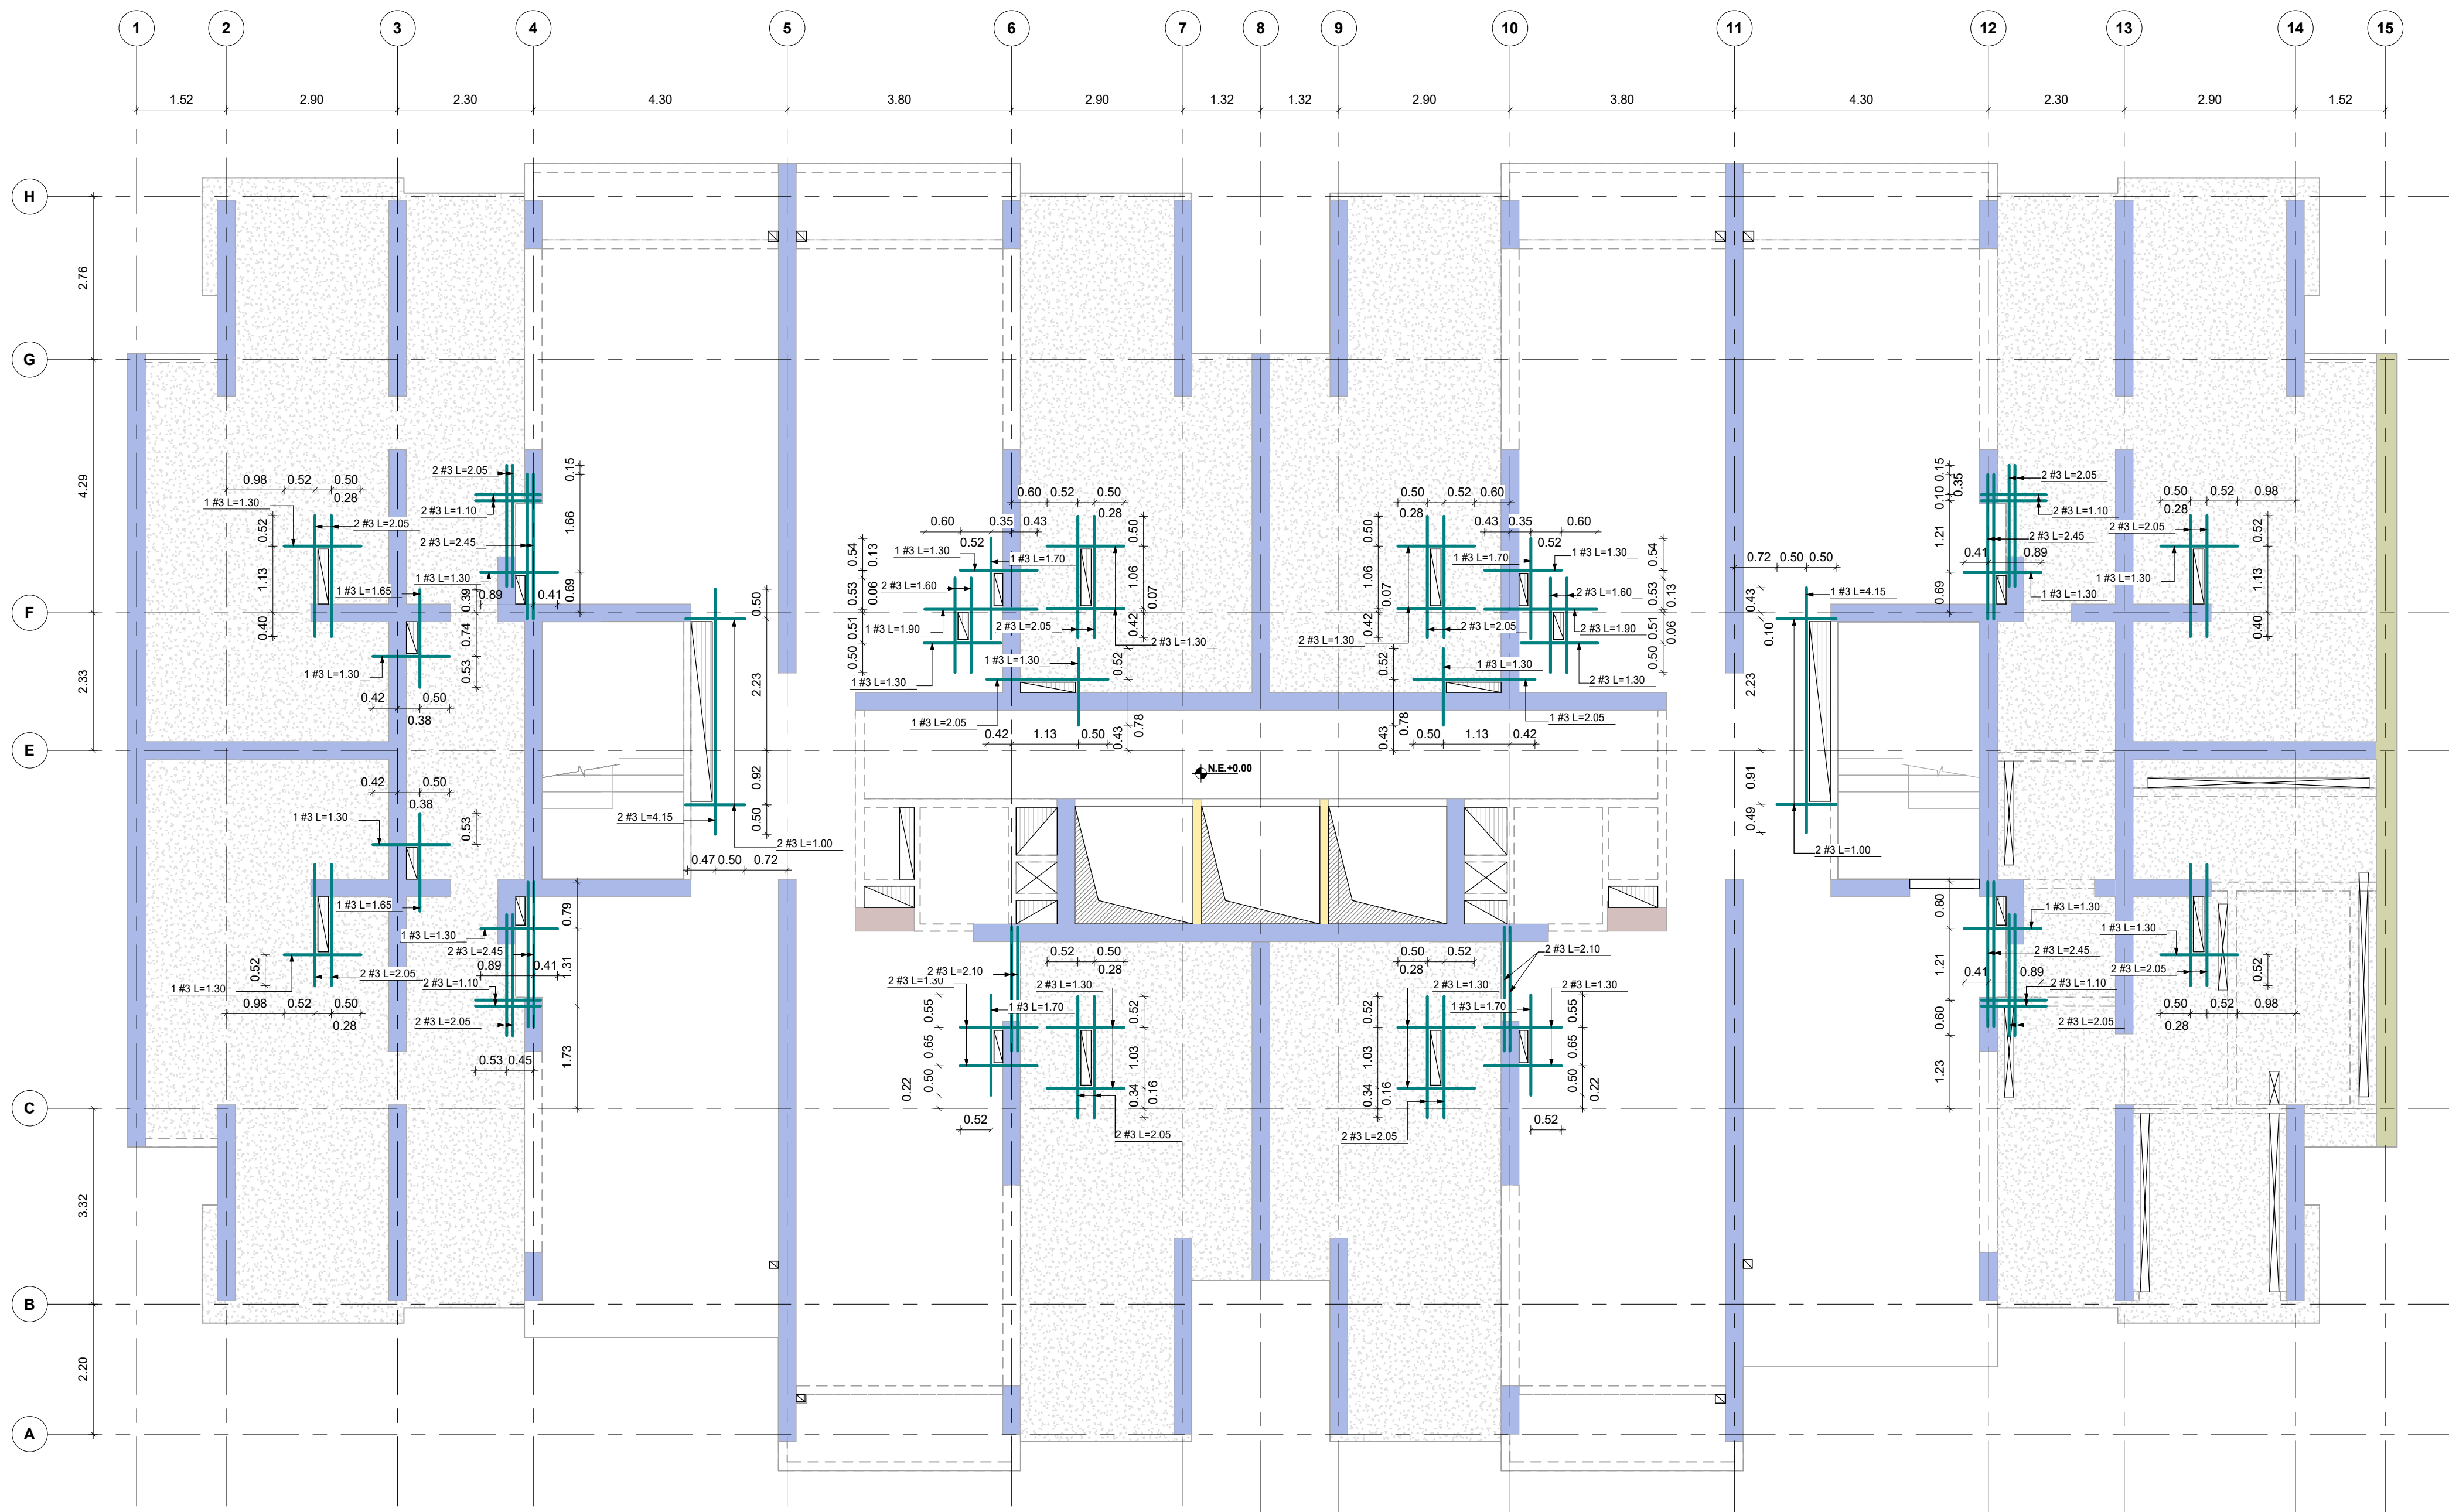


PLANTA DE REFUERZO ADICIONAL (INFERIOR Y SUPERIOR) PISO 1 N.E. 0.00

Escala 1 : 75

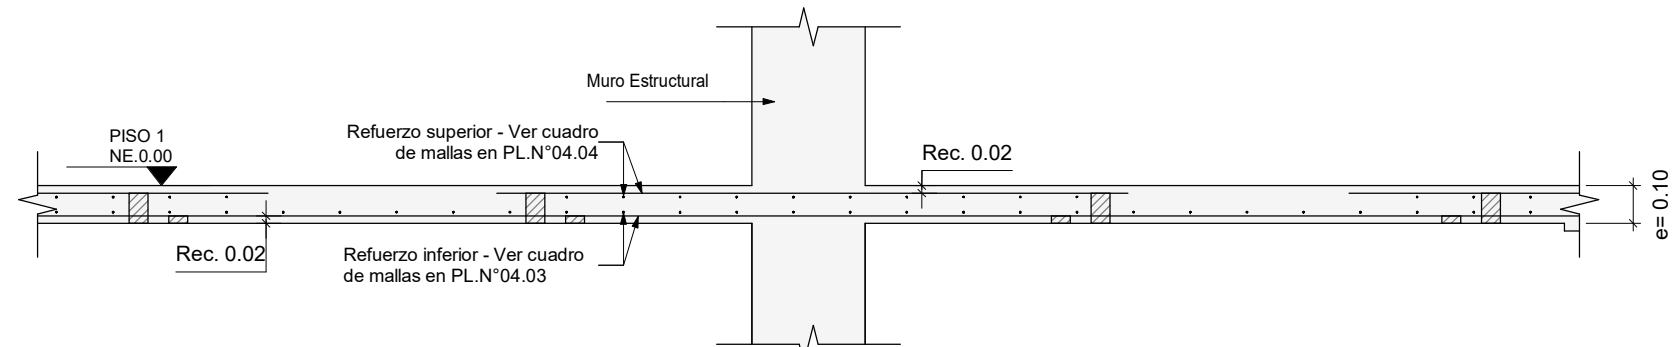


CORTE TÍPICO PLACA AÉREA e=0.10

Escala 1 : 20

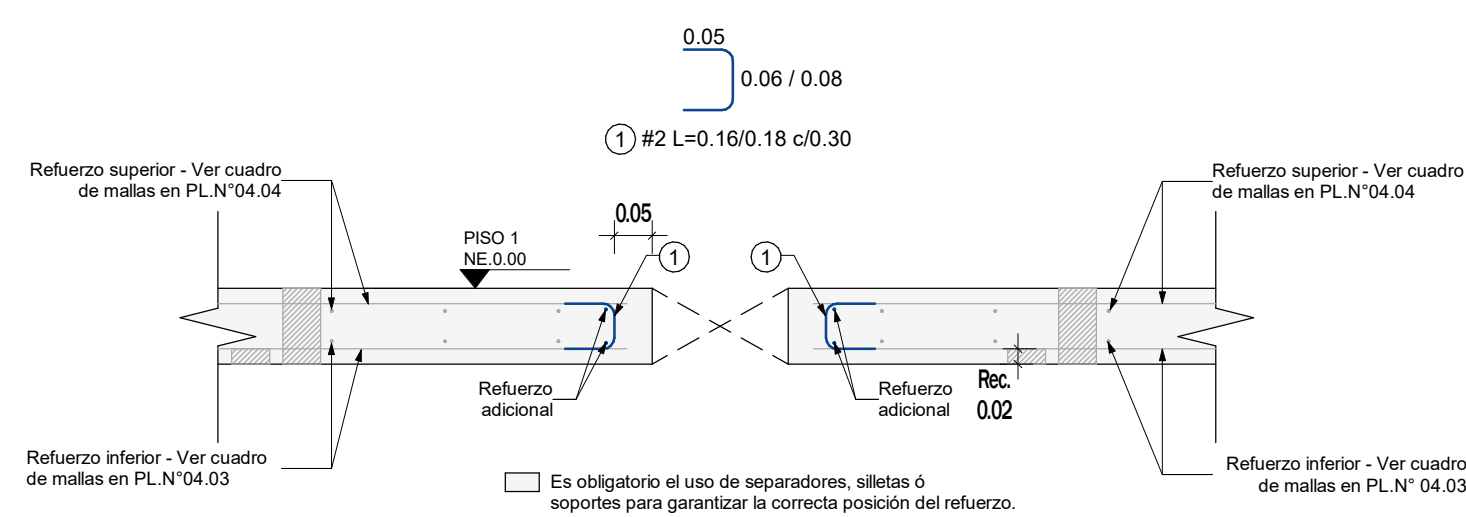


DETALLE TÍPICO - UBICACIÓN REFUERZO ADICIONAL

Escala 1 : 10

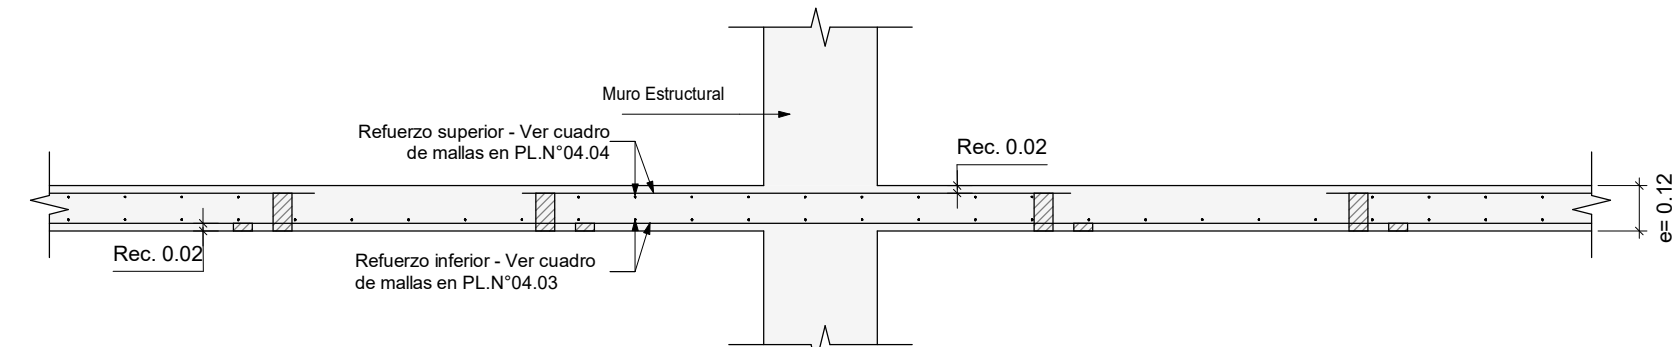

CORTE TÍPICO PLACA AÉREA e=0.12

Escala 1 : 20

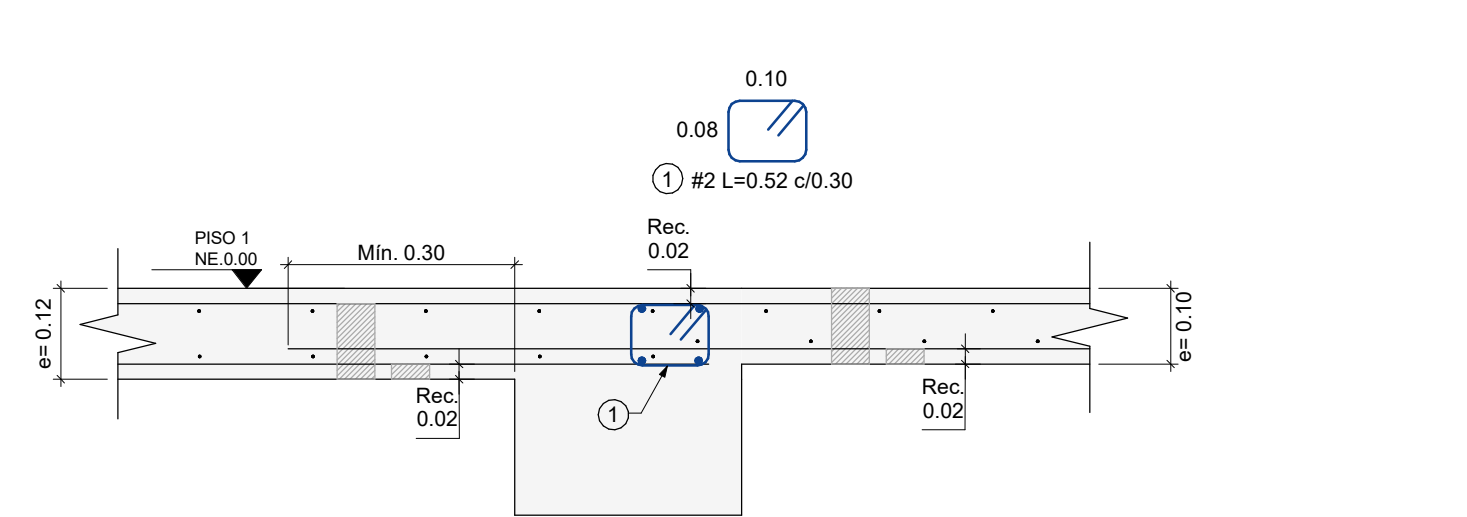

DETALLE TÍPICO - CAMBIO DE SECCIÓN


Escala 1 : 10

NOTAS:
1. Ver detalles generales en PL. N°01.02
2. Ver planta de localización e identificación de dinteles en PL. N° 04.01
3. Ver despieces de dinteles en PL. N° 10.00 a 10.04

CONCRETO:			
LOSAS Y DINTELES			
* DE PISO 1 A PISO 8	* DE PISO 9 A PISO 15	* DE PISO 16 A PISO 22	* DE PISO 23 A CUBIERTA ASCENSOR Y ESCALERAS
f'c=35 MPa	f'c=32 MPa	f'c=25 MPa	f'c=21 MPa
f'c=350 kg/cm²	f'c=315 kg/cm²	f'c=245 kg/cm²	f'c=210 kg/cm²
f'c=5000 psi	f'c=4500 psi	f'c=3500 psi	f'c=3000 psi

CONVENCIONES	
	Indica dinteles
	Indica placa e=0.10
	Indica placa e=0.12
	Indica muro e=0.15
	Indica muro e=0.30
	Indica muro e=0.35
	Indica muro e=0.40

REFUERZO ADICIONAL EN PLACAS
Escala 1 : 25

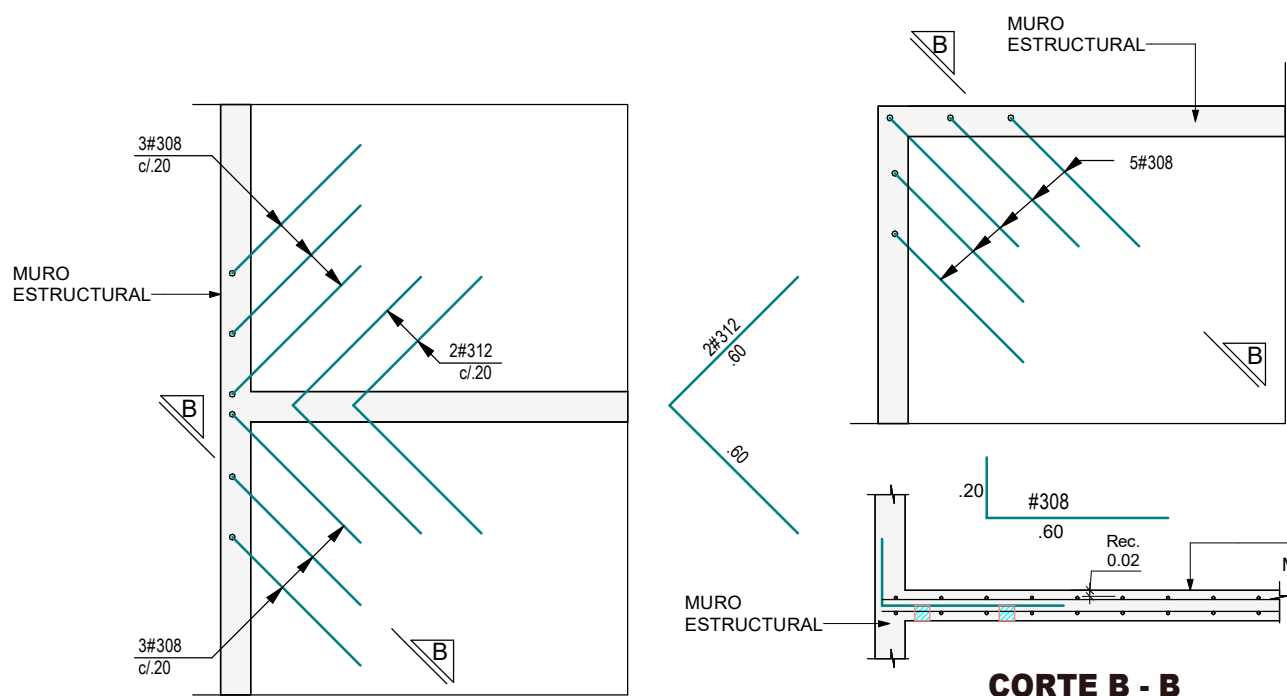

CORTE B - B

Es obligatorio el uso de separadores, sillas o soportes para garantizar la correcta posición del refuerzo.

VERSIÓN :

2

PLANO N°

04.02

GERENTE DE PROYECTO
ROBERTO AYCARDI F.
MAT. 2520257258 CND

INGENIERO
CARLOS ANDRÉS WILCHES C.

MODELADOR
DANIEL CASTELLANOS

MODIFICACIONES	FECHA
Emisión Inicial	28-02-2025
Actualización borde de placa	03-10-2025



LA SCALA

LA SCALA_EST_TOR-1

TORRE 1

CALLE 170 CON AV. BOYACA

PLANTA DE REFUERZO ADICIONAL PISO 1

LA SCALA_EST_TOR-1_04.02_P1-RADC

REVISOR ESTRUCTURAL

RAMÓN ANDRÉS ALVAREZ MANTILLA
MAT. 25202-346546 CND.

PLANO N°

04.02

VERSIÓN :

2