



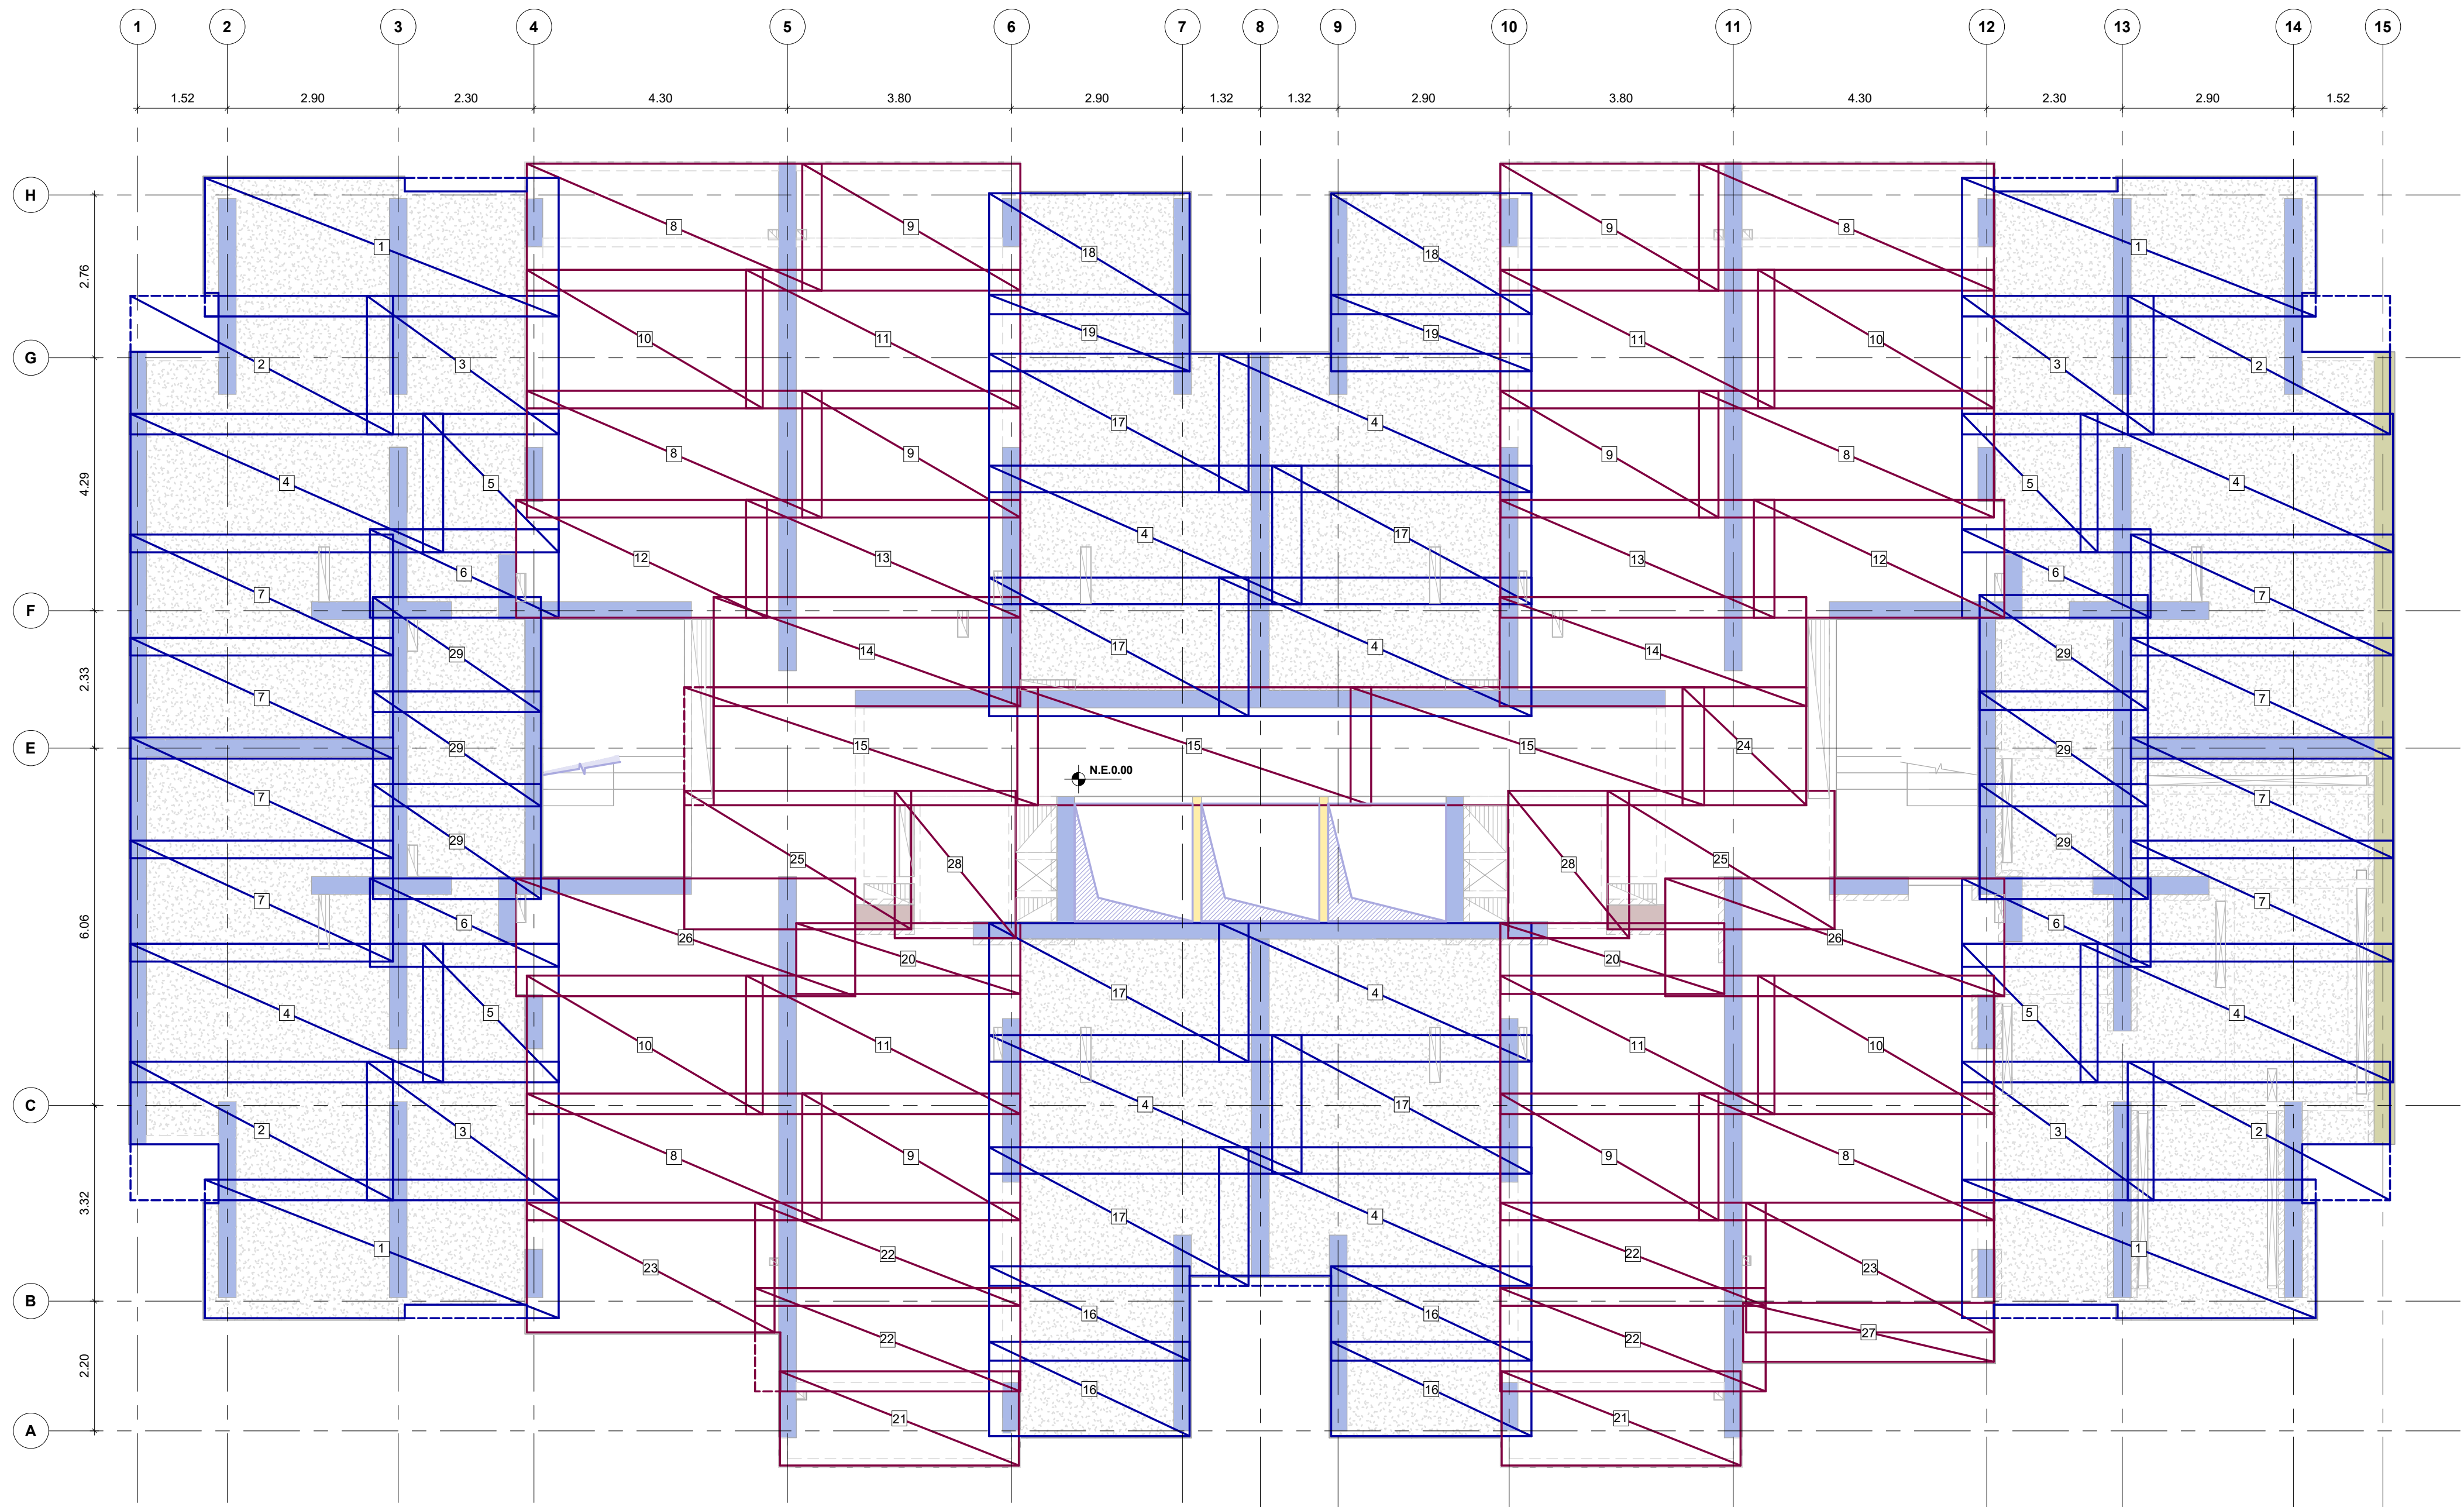


PLANTA DE REFUERZO INFERIOR PISO 1
Escala 1 : 75

CUADRO DE MALLAS REFUERZO INFERIOR PISO 1							
TIPO	A (m)	B(m)	ÁREA (m²)	CANT.	REFUERZO		PESO / MALLA (Kg/m²)
					REFUERZO A	REFUERZO B	
1	6.00	2.35	14 m²	4	Ø6.0mm c/0.15	Ø6.0mm c/0.15	2.993
2	4.45	2.35	10 m²	4	Ø6.0mm c/0.15	Ø6.0mm c/0.15	2.993
3	3.25	2.35	8 m²	4	Ø6.0mm c/0.15	Ø6.0mm c/0.15	2.993
4	5.30	2.35	12 m²	10	Ø6.0mm c/0.15	Ø6.0mm c/0.15	2.993
5	2.35	2.30	5 m²	4	Ø6.0mm c/0.15	Ø6.0mm c/0.15	2.993
6	3.20	1.50	5 m²	4	Ø6.0mm c/0.15	Ø6.0mm c/0.15	2.993
7	4.45	2.05	9 m²	8	Ø6.0mm c/0.15	Ø6.0mm c/0.15	2.993
8	5.00	2.15	11 m²	6	Ø6.5mm c/0.15	Ø6.5mm c/0.15	3.518
9	3.70	2.15	8 m²	6	Ø6.5mm c/0.15	Ø6.5mm c/0.15	3.518
10	4.00	2.35	9 m²	4	Ø6.5mm c/0.15	Ø6.5mm c/0.15	3.518
11	4.65	2.35	11 m²	4	Ø6.5mm c/0.15	Ø6.5mm c/0.15	3.518
12	4.25	2.00	9 m²	2	Ø6.5mm c/0.15	Ø6.5mm c/0.15	3.518
13	4.65	2.00	9 m²	2	Ø6.5mm c/0.15	Ø6.5mm c/0.15	3.518
14	5.20	1.85	10 m²	2	Ø6.5mm c/0.15	Ø6.5mm c/0.15	3.518
15	6.00	2.00	12 m²	3	Ø6.5mm c/0.15	Ø6.5mm c/0.15	3.518
16	3.40	1.60	5 m²	4	Ø6.0mm c/0.15	Ø6.0mm c/0.15	2.993
17	4.40	2.35	10 m²	6	Ø6.0mm c/0.15	Ø6.0mm c/0.15	2.993
18	3.40	2.05	7 m²	2	Ø6.0mm c/0.15	Ø6.0mm c/0.15	2.993
19	3.40	1.30	4 m²	2	Ø6.0mm c/0.15	Ø6.0mm c/0.15	2.993
20	3.80	1.20	5 m²	2	Ø6.5mm c/0.15	Ø6.5mm c/0.15	3.518
21	4.05	1.60	6 m²	2	Ø6.5mm c/0.15	Ø6.5mm c/0.15	3.518
22	4.50	1.75	8 m²	4	Ø6.5mm c/0.15	Ø6.5mm c/0.15	3.518
23	4.20	2.20	9 m²	2	Ø6.5mm c/0.15	Ø6.5mm c/0.15	3.518
24	2.10	2.00	4 m²	1	Ø6.5mm c/0.15	Ø6.5mm c/0.15	3.518
25	3.85	2.35	9 m²	2	Ø6.5mm c/0.15	Ø6.5mm c/0.15	3.518
26	5.75	2.00	12 m²	2	Ø6.5mm c/0.15	Ø6.5mm c/0.15	3.518
27	4.25	1.00	4 m²	1	Ø6.5mm c/0.15	Ø6.5mm c/0.15	3.518
28	2.50	2.05	5 m²	2	Ø6.5mm c/0.15	Ø6.5mm c/0.15	3.518
29	2.85	1.95	6 m²	6	Ø6.0mm c/0.15	Ø6.0mm c/0.15	2.993
TOTAL : 105				105			2982

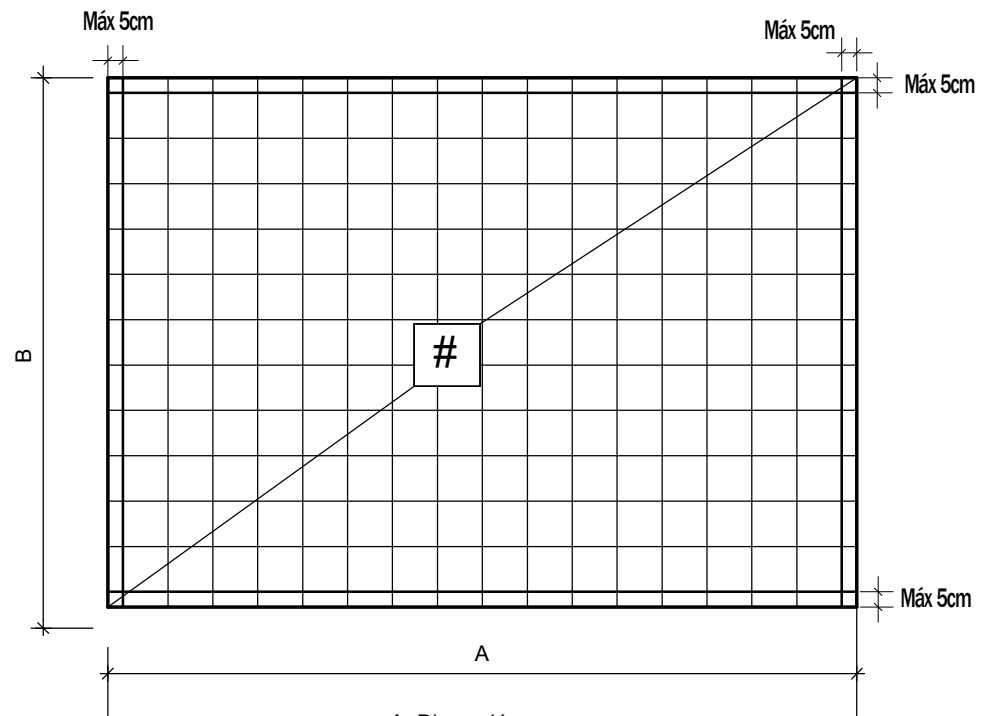

DETALLE CONVENCIÓN MALLAS
Escala 1 : 25

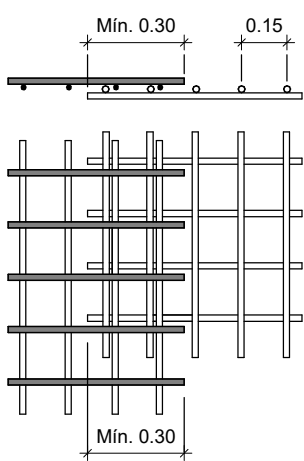

DETALLE TRASLAPO MALLAS
Escala 1 : 25

NOTAS:
1. Ver detalles generales en el PL. N° 01.02
2. Ver planta de refuerzo adicional en PL. N° 04.02
3. Ver planta de refuerzo superior en PL. N° 04.04
4. Las dimensiones de las mallas deben ser verificadas por el constructor.

CONCRETO:			
LOSAS Y DIENTES			
* DE PISO 1 A PISO 8	* DE PISO 9 A PISO 15	* DE PISO 16 A PISO 22	* DE PISO 23 A CUBIERTA ASCENSOR Y ESCALERAS
f'c=35 MPa	f'c=32 MPa	f'c=25 MPa	f'c=21 MPa
f'c=350 kg/cm²	f'c=315 kg/cm²	f'c=245 kg/cm²	f'c=210 kg/cm²
f'c=5000 psi	f'c=4500 psi	f'c=3500 psi	f'c=3000 psi

CONVENCIONES	
Indica Malla	Indica cortar Malla
Indica N° de Malla	

CONVENCIONES	
Indica dinteles	Indica placa e=0.10
Indica placa e=0.12	Indica muros en concreto e=0.15
Indica muros en concreto e=0.30	Indica muros en concreto e=0.35
Indica muros en concreto e=0.40	

VERSIÓN :

2

PLANO N°

04.03

GERENTE DE PROYECTO
ROBERTO AYCARDI F.
MAT. 2520257258 CND

INGENIERO
CARLOS ANDRÉS WILCHES C.

MODELADOR
DANIEL CASTELLANOS

MODIFICACIONES		FECHA
Emisión Inicial	Actualización borde de placa y mallas	28-02-2025 03-10-2025



LA SCALA

LA SCALA_EST_TOR-1

TORRE 1

CALLE 170 CON AV. BOYACA

PLANTA DE REFUERZO INFERIOR PISO 1

LA SCALA_EST_TOR-1_04.03_P1-RINF

REVISOR ESTRUCTURAL
RAMÓN ÁNDRES ALVAREZ MANTILLA
MAT. 25202-346546 CND.

PLANO N°

04.03

VERSIÓN :

2