


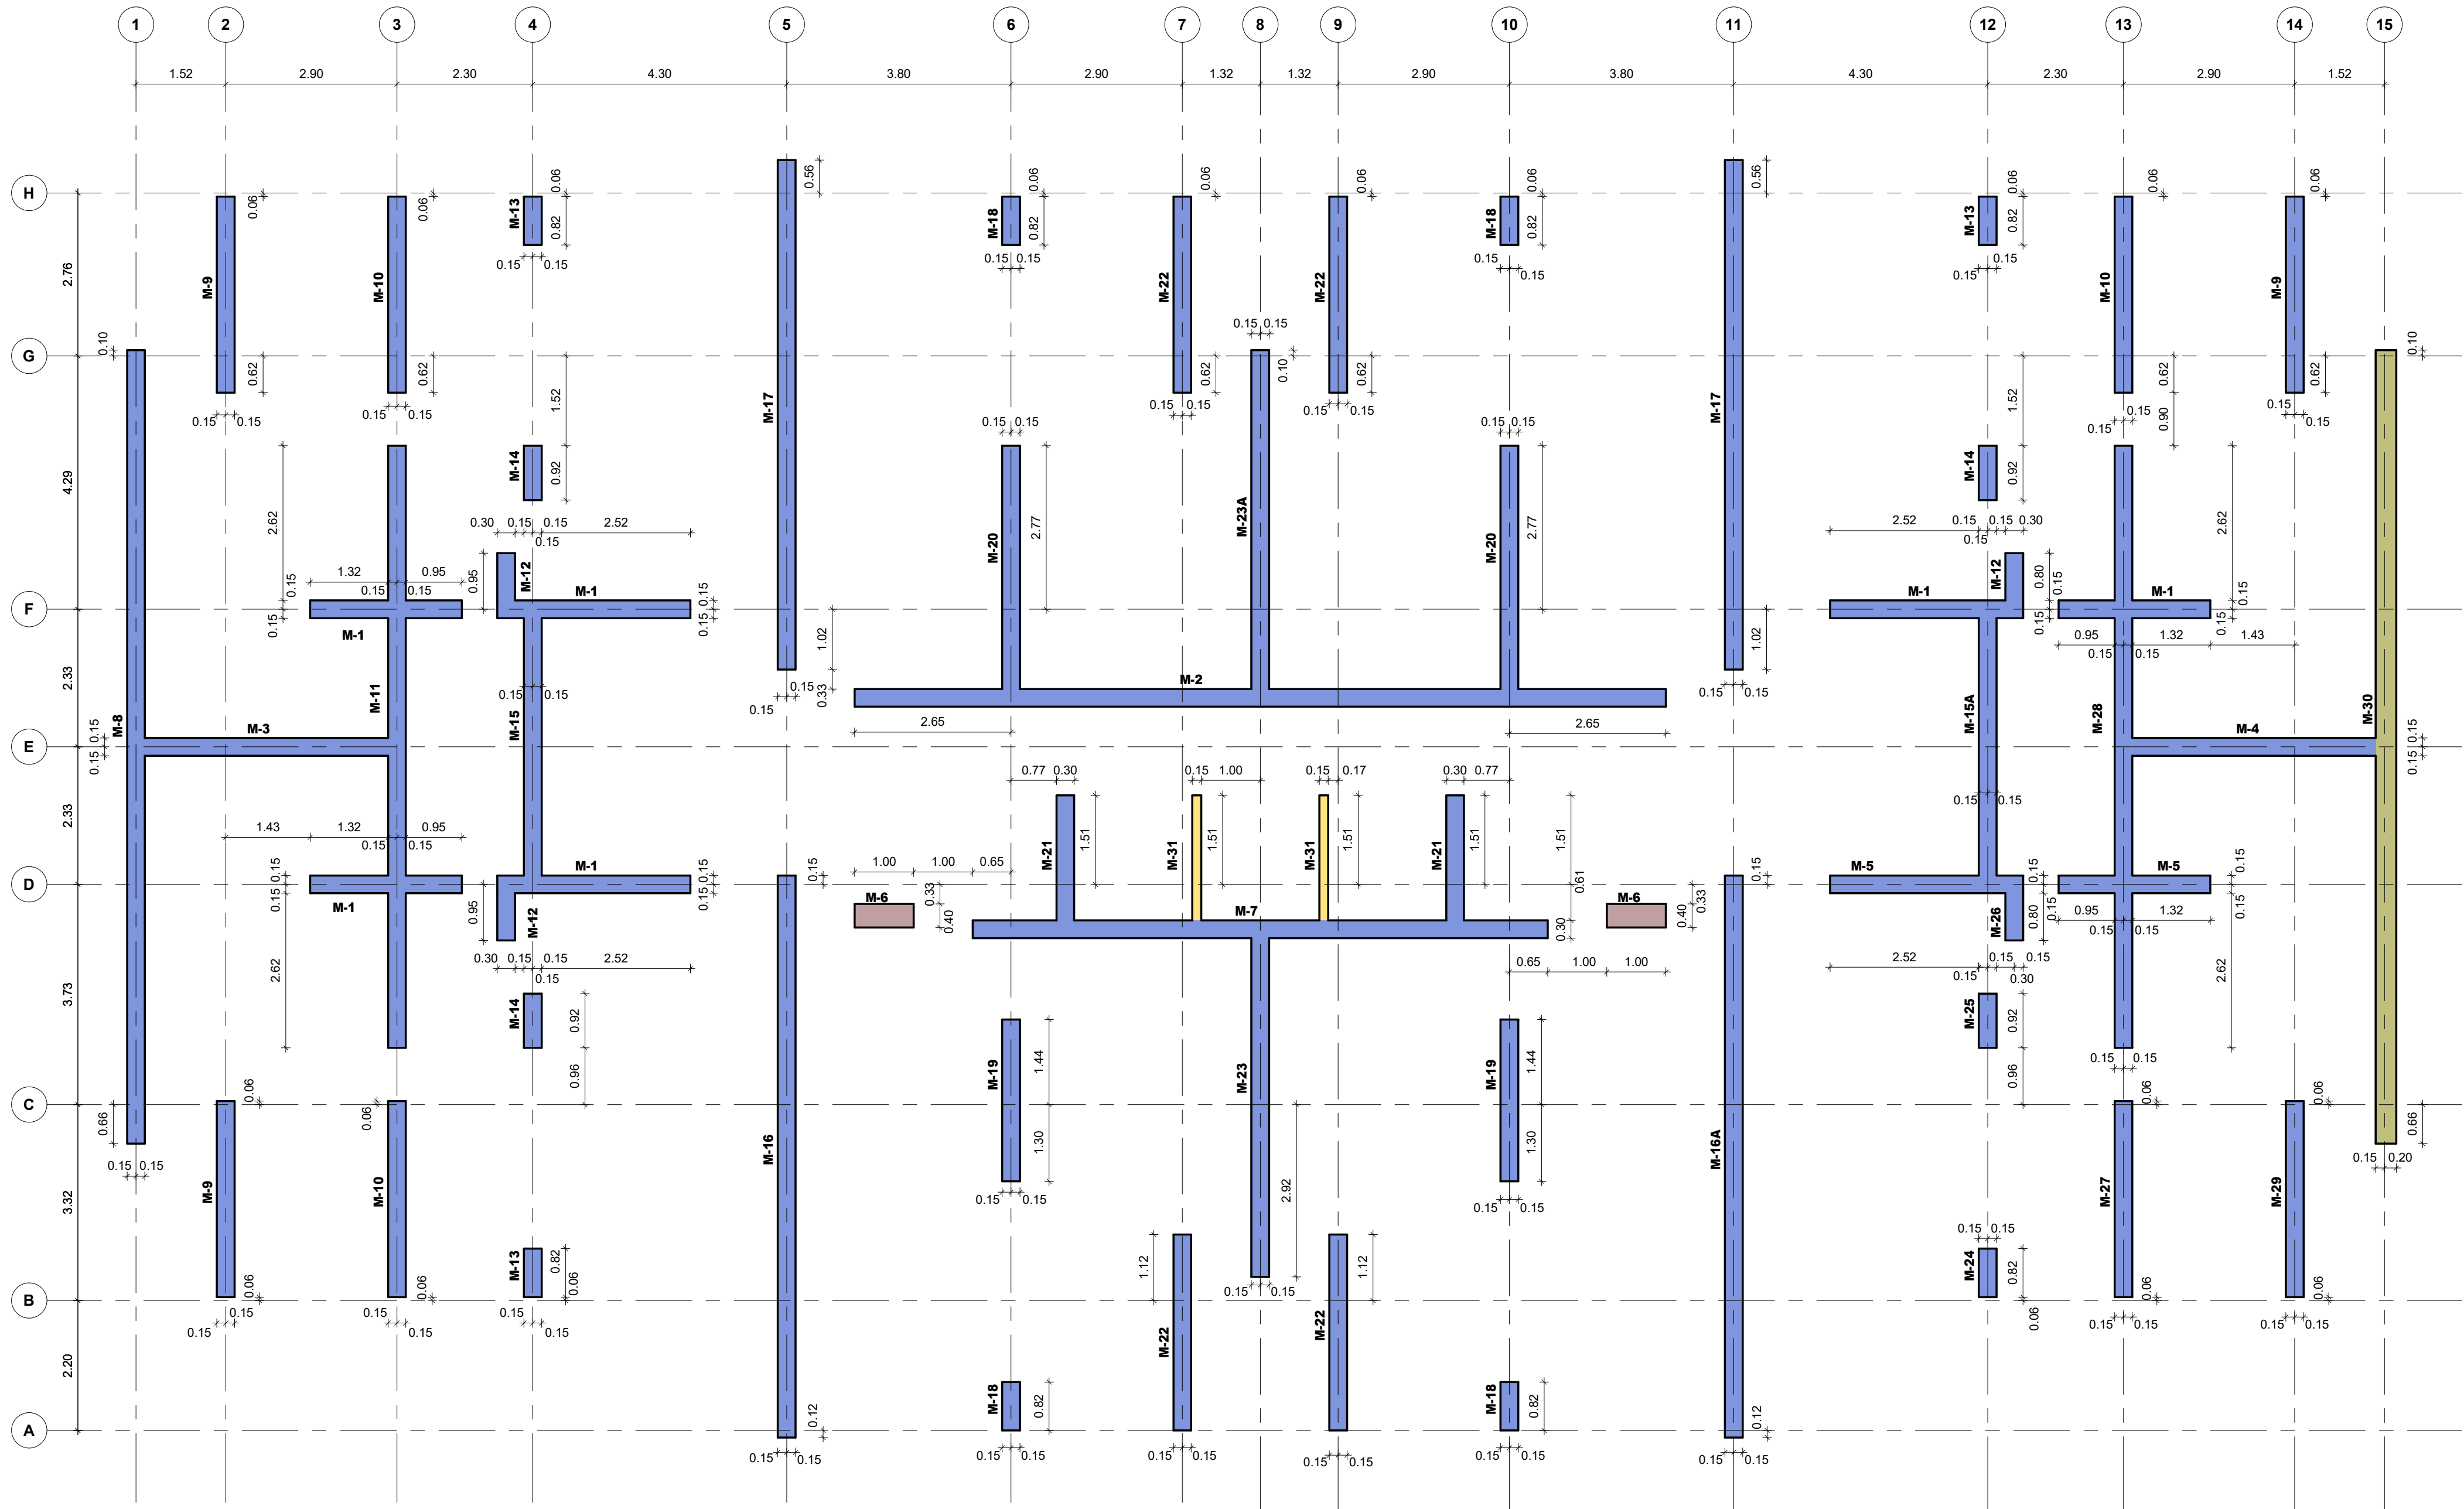

PLANTA LOCALIZACIÓN DE MUROS PISO 2
Escala 1 : 75

CONCRETO:			
MUROS			
* DE CIMENTACIÓN A PISO 8	* DE PISO 8 A PISO 15	* DE PISO 15 A PISO 22	* DE PISO 22 A CUBIERTA ASCENSOR Y ESCALERAS
f _c =49 MPa	f _c =42 MPa	f _c =35 MPa	f _c =28 MPa
f _c =490 kg/cm ²	f _c =420 kg/cm ²	f _c =350 kg/cm ²	f _c =280 kg/cm ²
f _c =7000 psi	f _c =6000 psi	f _c =5000 psi	f _c =4000 psi

CONVENCIONES	
M-#	Indica N° de Muro
	Indica muro e=0.15
	Indica muro e=0.30
	Indica muro e=0.35
	Indica muro e=0.40
NOTAS	
1. Ver detalles generales en PL. N°01.02.	
2. Ver despieces de muros en PL. N° 11.00 a PL. N°11.22.	
3. Ver detalles de muros en PL. N° 11.22.	

MODIFICACIONES		FECHA
Emisión Inicial	Se actualiza longitud de muro M-19	28-02-2025 04-11-2025



LA SCALA

LA SCALA_EST_TOR-1
TORRE 1

CALLE 170 CON AV. BOYACA

PLANTA LOCALIZACIÓN DE MUROS PISO 2

LA SCALA_EST_TOR-1_05.00_LCM-P2

REVISOR ESTRUCTURAL
RAMÓN ANDRÉS ALVAREZ MANTILLA
MAT. 25202-346546 CND.