




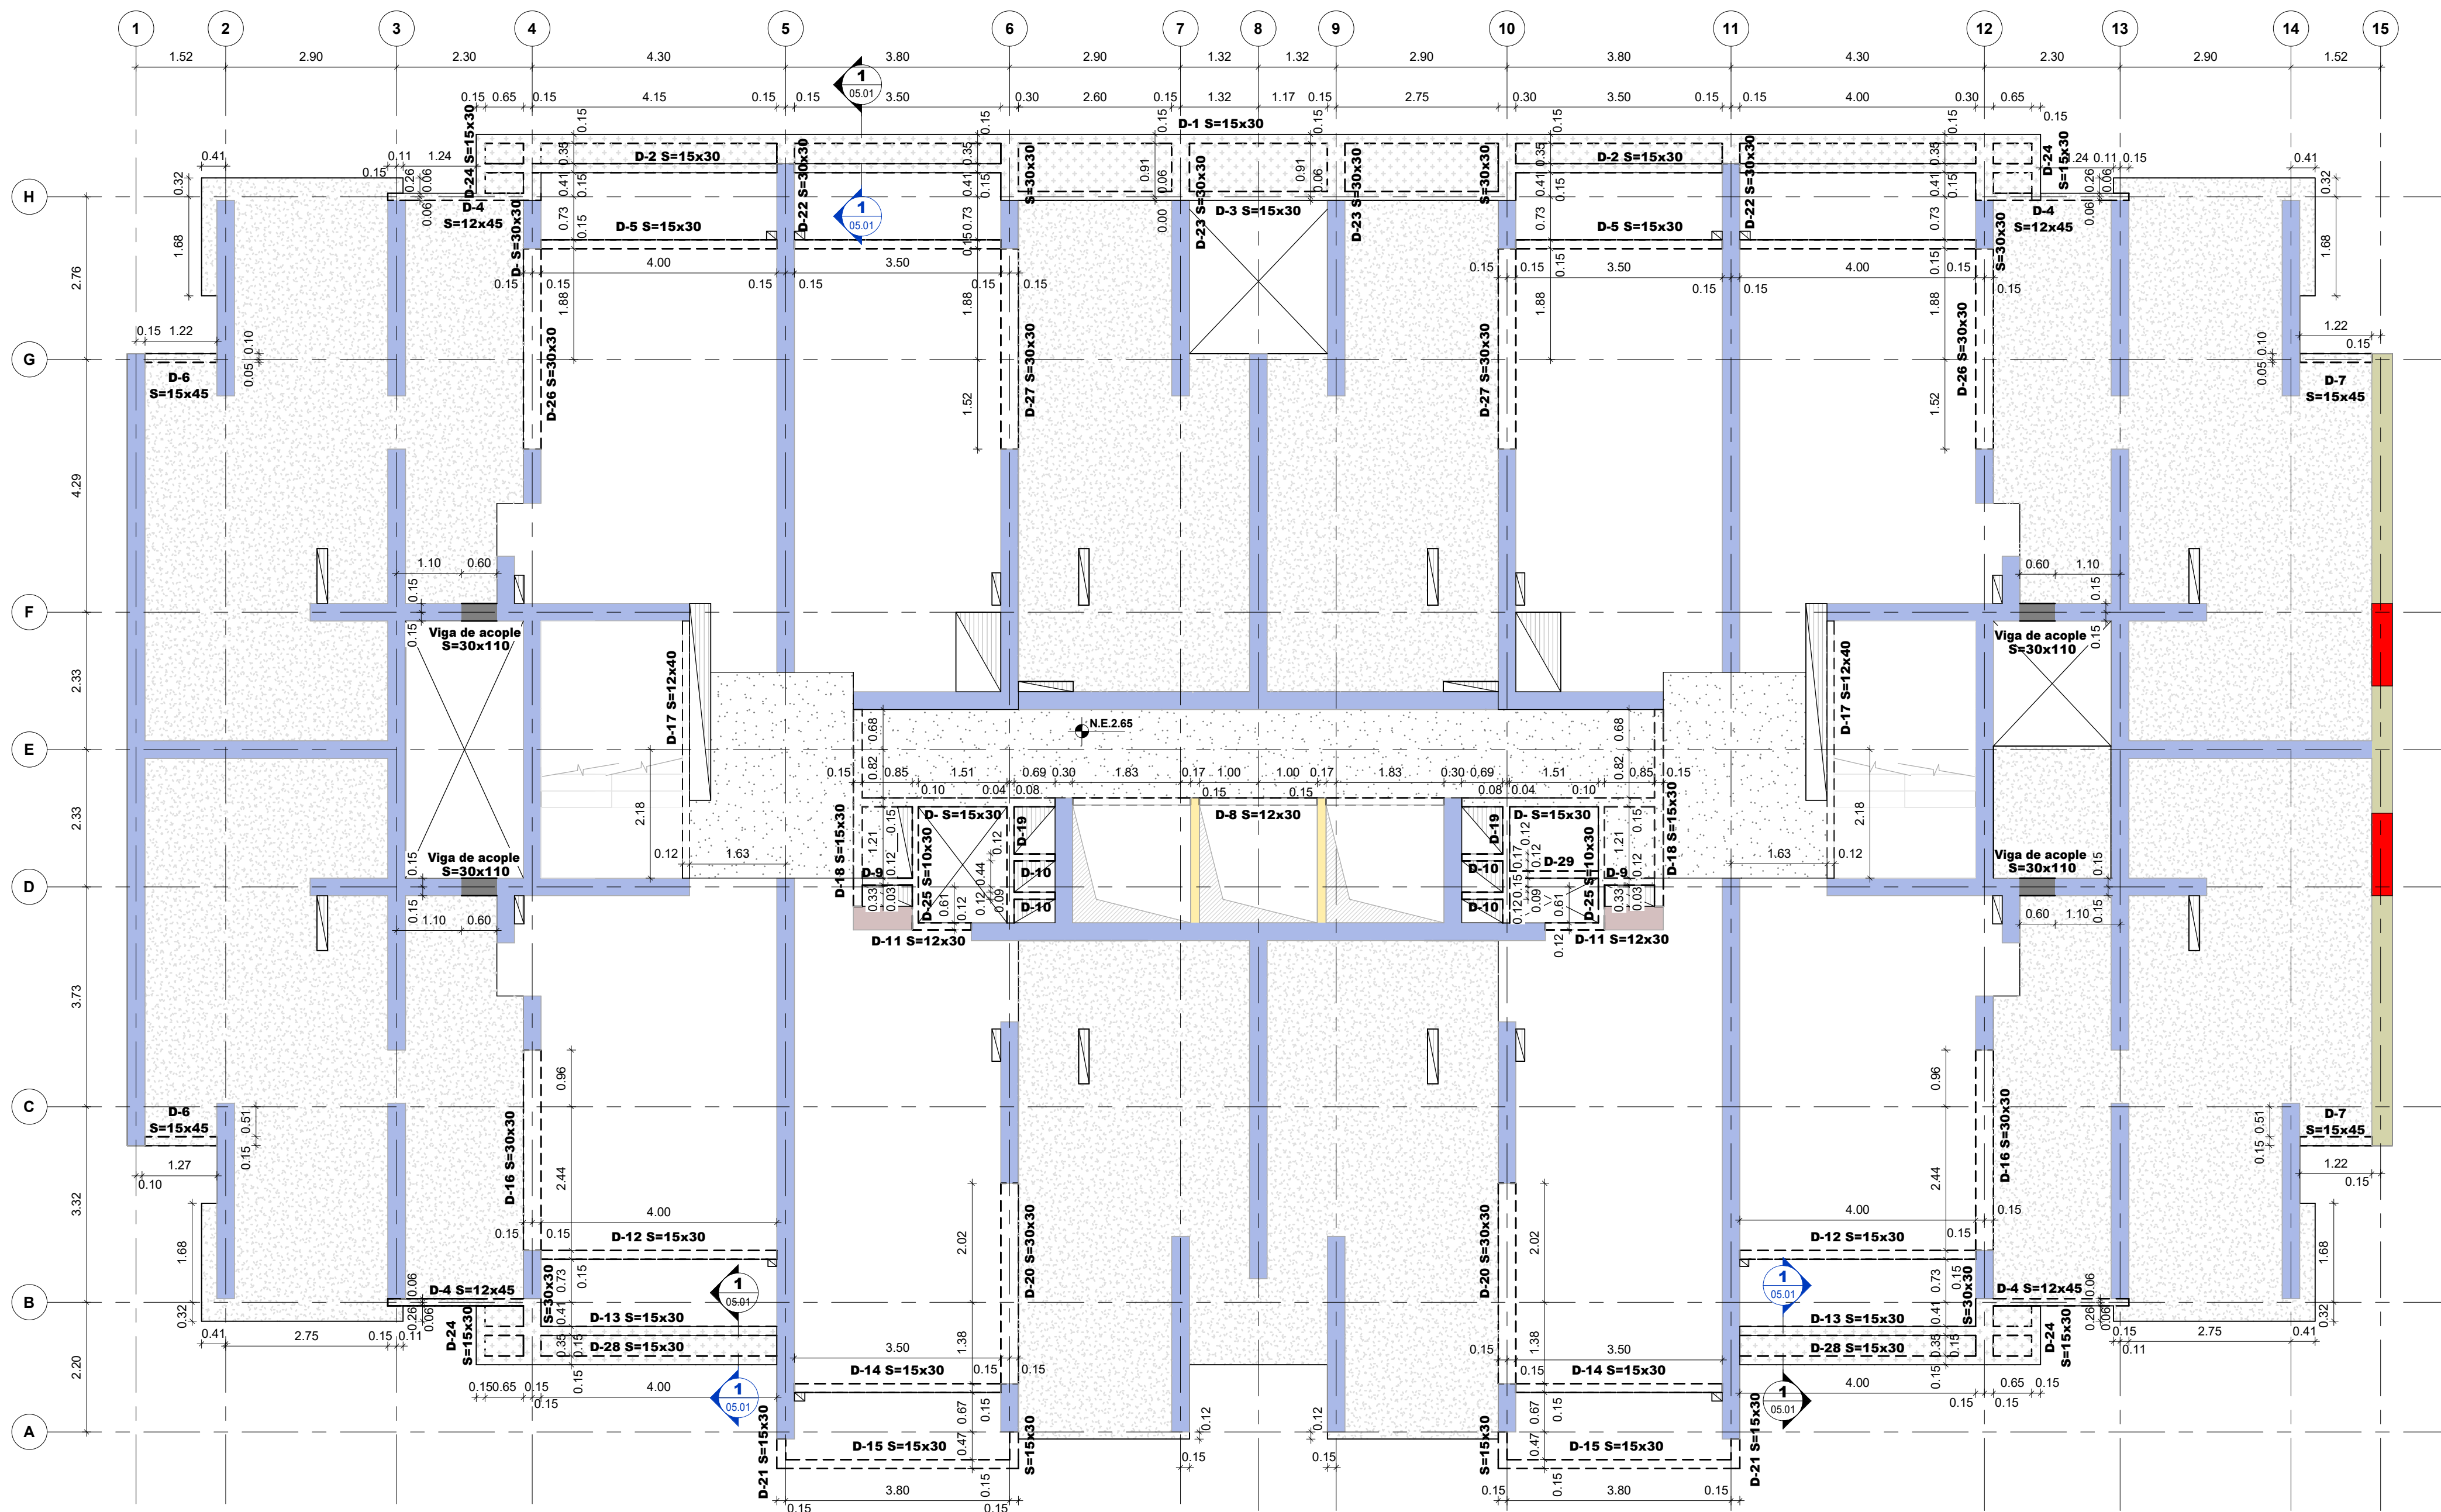

PLANTA LOCALIZACIÓN DE DINTELES PISO 2
Escala 1 : 75

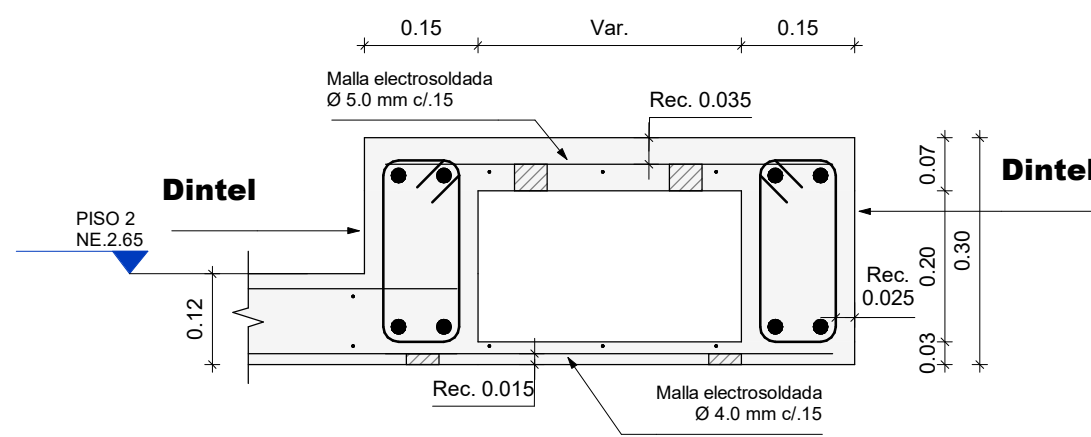

CORTE 1 - 1 PLACA ALIGERADA
Escala 1 : 10

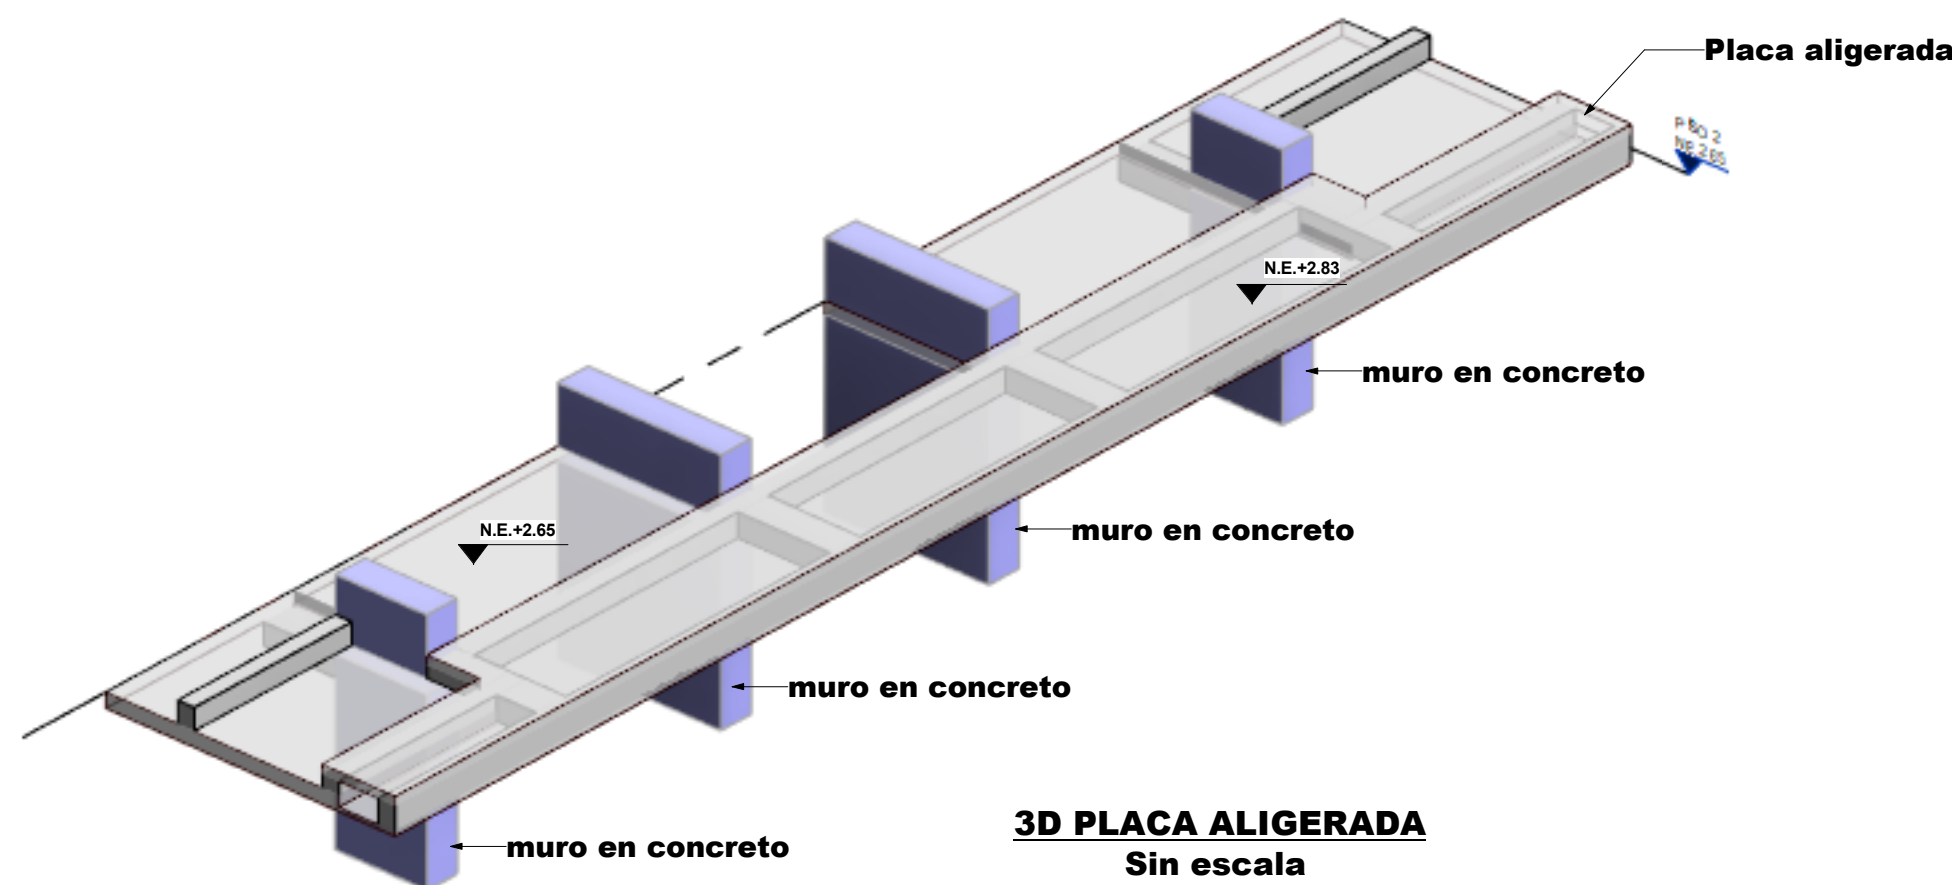

3D PLACA ALIGERADA
Sin escala

CONCRETO: VIGAS DE ACOPILE				CONCRETO: LOSAS Y DINTELES			
* DE PISO 2 A PISO 8	* DE PISO 8 A PISO 15	* DE PISO 15 A PISO 22	* DE PISO 22 A PISO 28	* DE PISO 1 A PISO 8	* DE PISO 9 A PISO 15	* DE PISO 16 A PISO 22	* DE PISO 23 A CUBIERTA ASCENSOR Y ESCALERAS
f'c=49 MPa	f'c=42 MPa	f'c=35 MPa	f'c=28 MPa	f'c=35 MPa	f'c=32 MPa	f'c=25 MPa	f'c=21 MPa
f'c=490 kg/cm²	f'c=420 kg/cm²	f'c=350 kg/cm²	f'c=280 kg/cm²	f'c=350 kg/cm²	f'c=315 kg/cm²	f'c=245 kg/cm²	f'c=210 kg/cm²
f'c=7000 psi	f'c=6000 psi	f'c=5000 psi	f'c=4000 psi	f'c=5000 psi	f'c=4500 psi	f'c=3500 psi	f'c=3000 psi

CONVENCIONES	
□	Indica dinteles
D-#	Indica N° de dintel
■	Indica Vigas de acople
■	Indica muro e=0.15
■	Indica muro e=0.30
■	Indica muro e=0.35
■	Indica muro e=0.40
■	Indica placa e=0.10
■	Indica placa e=0.12
■	Indica placa e=0.15
■	Indica zona de placa aligerada
NOTAS	
1. Ver detalles generales en PL. N°01.02	
2. Ver despieces de dinteles en PL. N° 10.00 a PL. N° 10.04	
3. ver detalle viga de acople en PL. N° 11.01, 11.05 Y 11.20	

MODIFICACIONES	FECHA
Emisión Inicial	28-02-2025
Ajuste borde de placa ejes H-4, H-12, B-4 y B-12	26-02-2026



LA SCALA

LA SCALA_EST_TOR-1

TORRE 1

CALLE 170 CON AV. BOYACA

PLANTA LOCALIZACIÓN E IDENTIFICACIÓN DE DINTELES PISO 2

LA SCALA_EST_TOR-1_05.01_LDINT-P2

REVISOR ESTRUCTURAL

RAMÓN ÁNDRES ALVAREZ MANTILLA
MAT. 25202-346546 CND.