




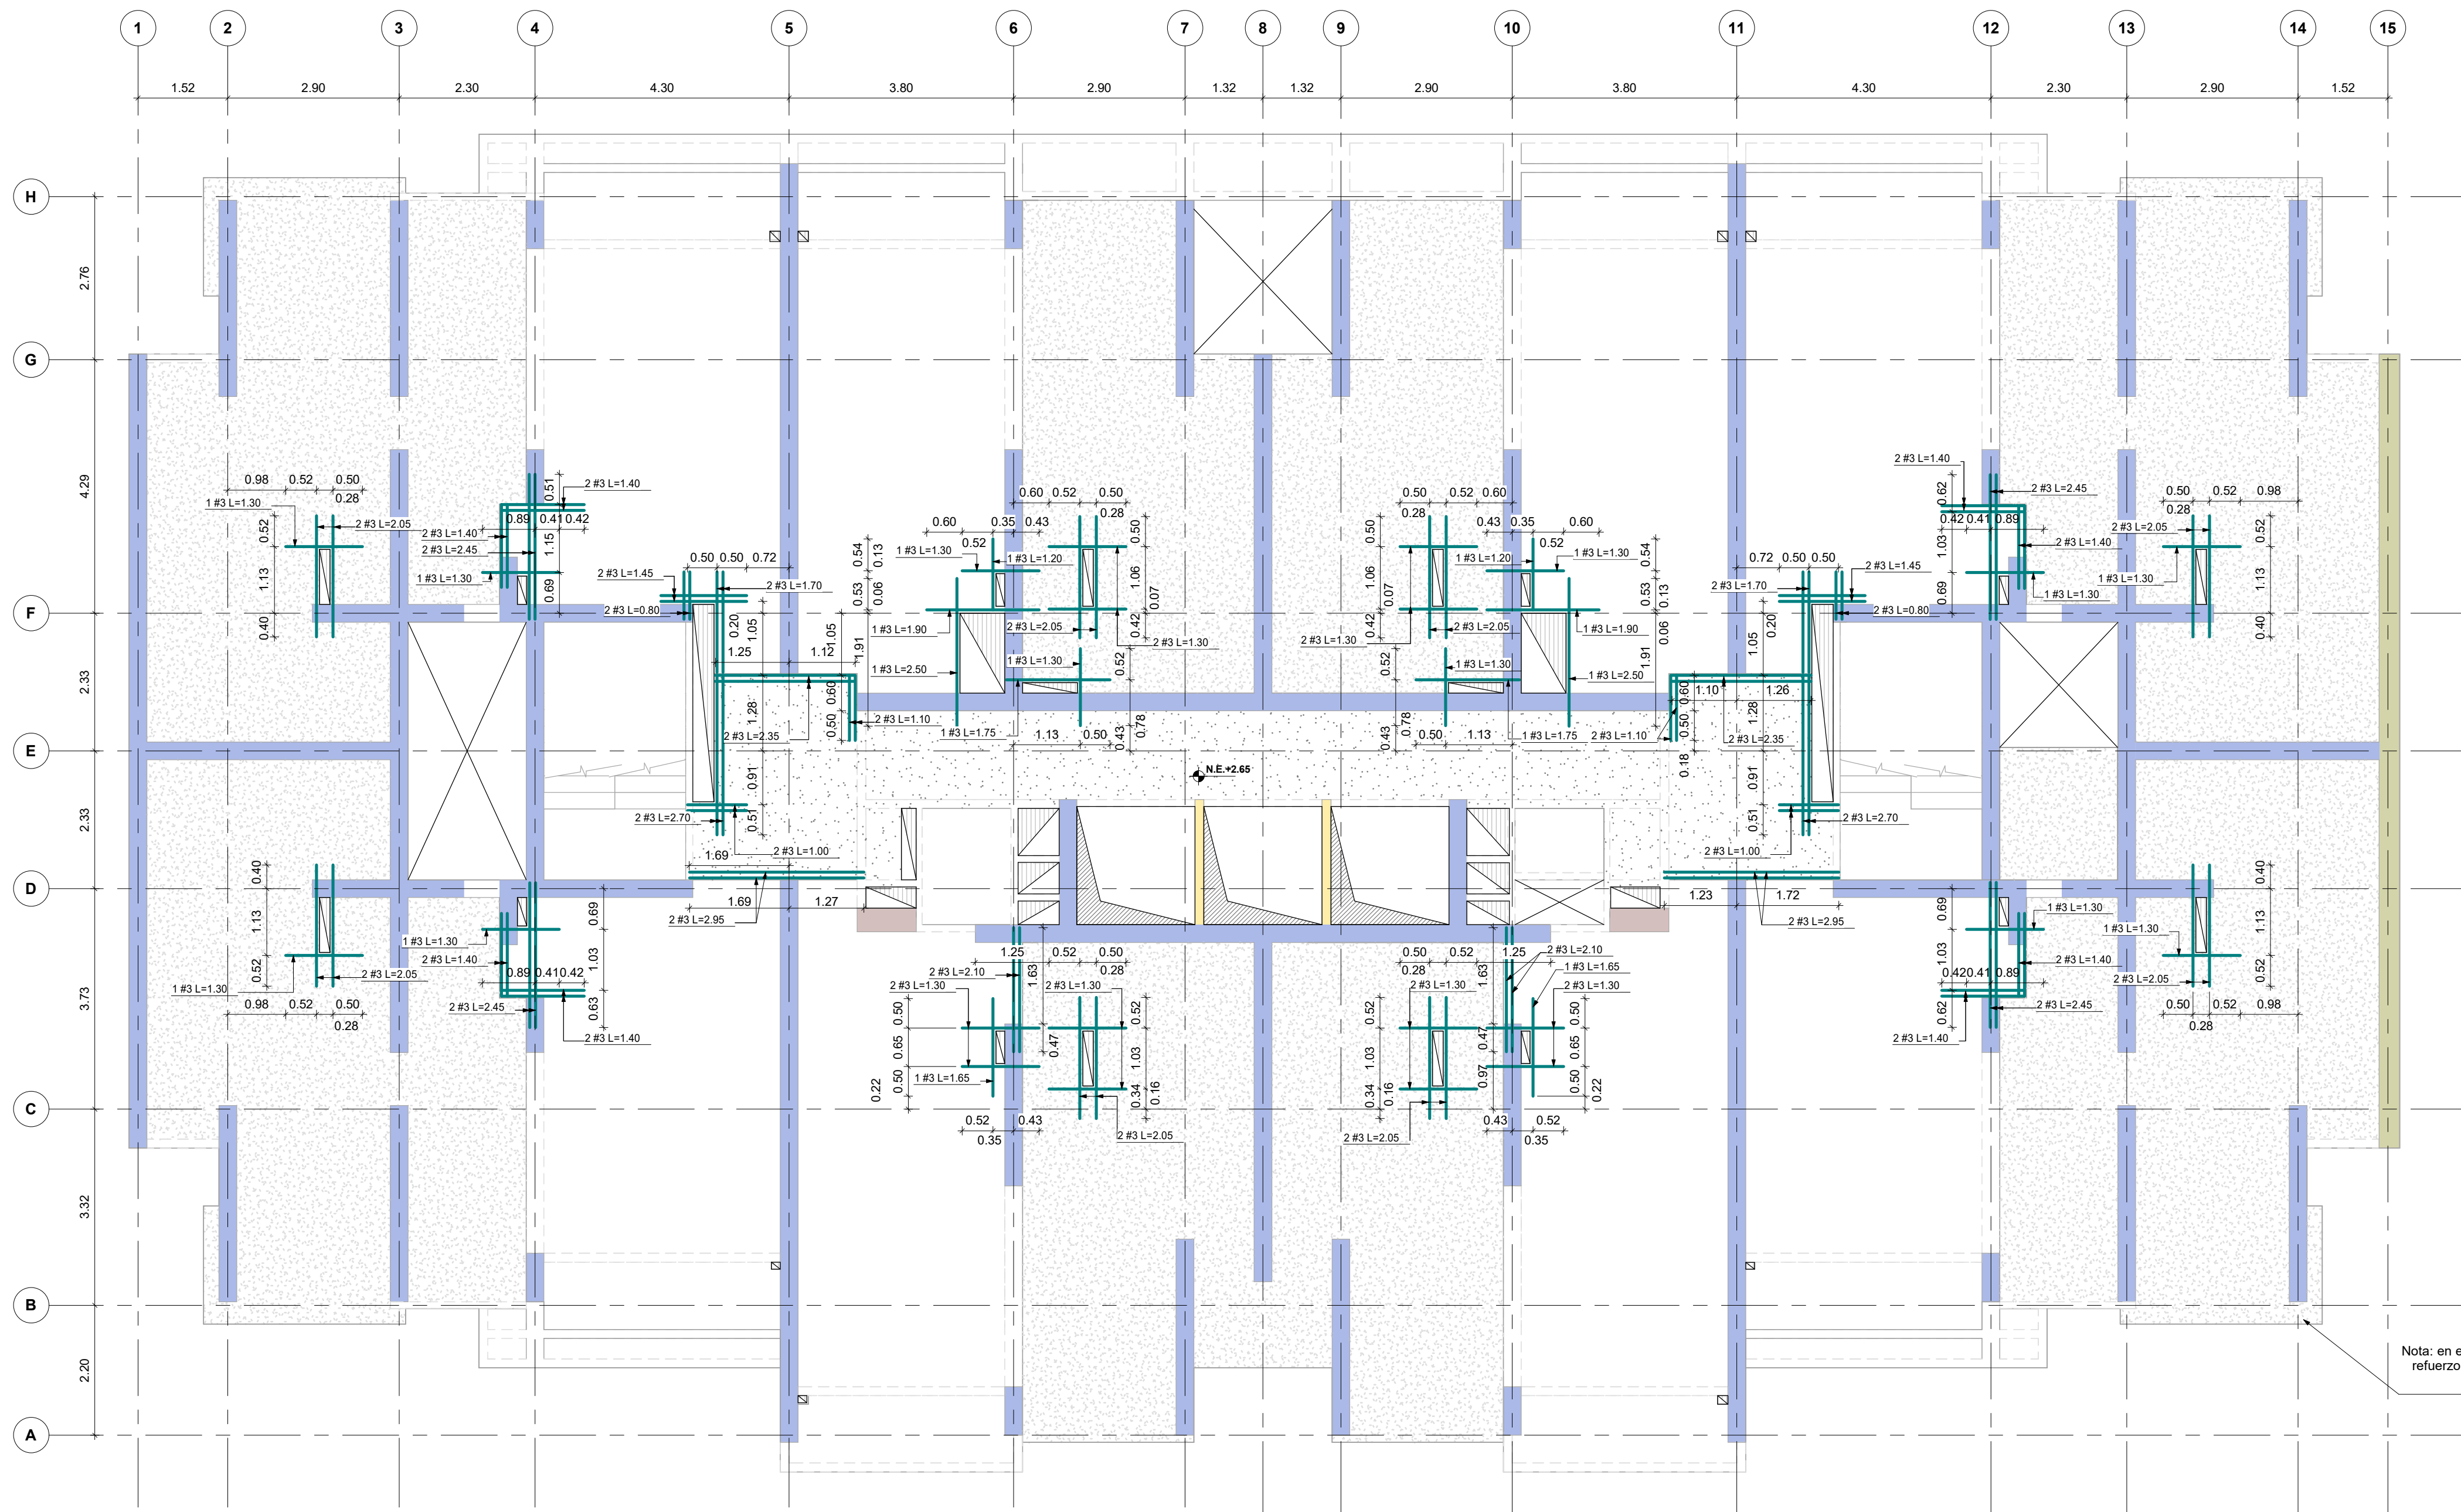


PLANTA DE REFUERZO ADICIONAL (INFERIOR Y SUPERIOR) PISO 2
Escala 1 : 75

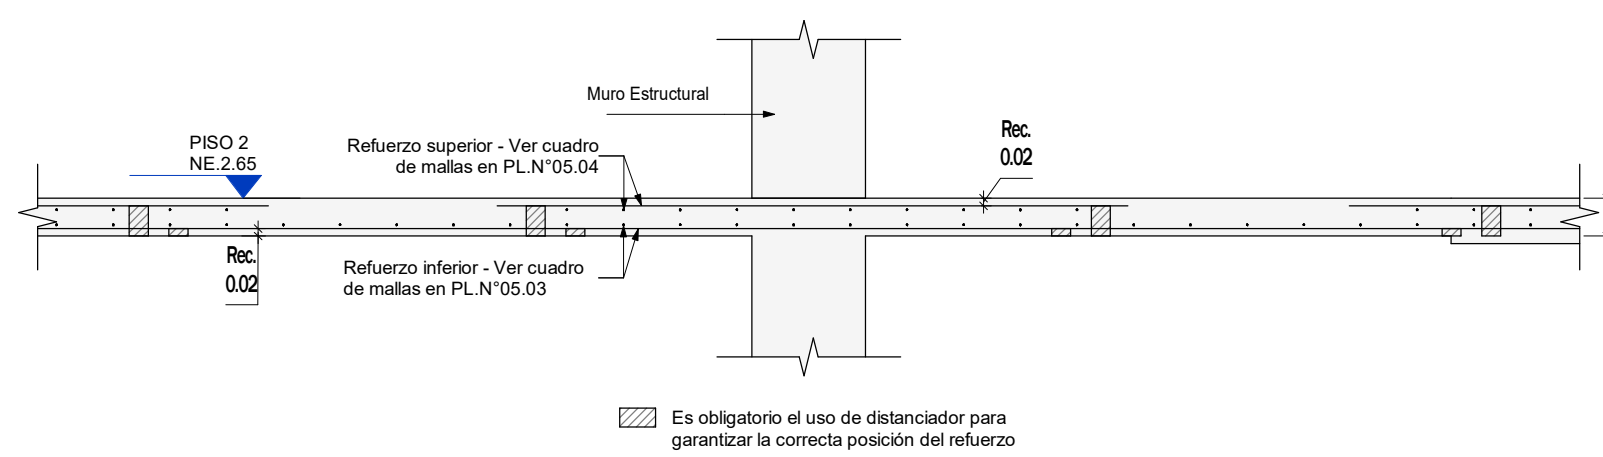


CORTE TÍPICO PLACA ÁEREA e=0.10
Escala 1 : 20

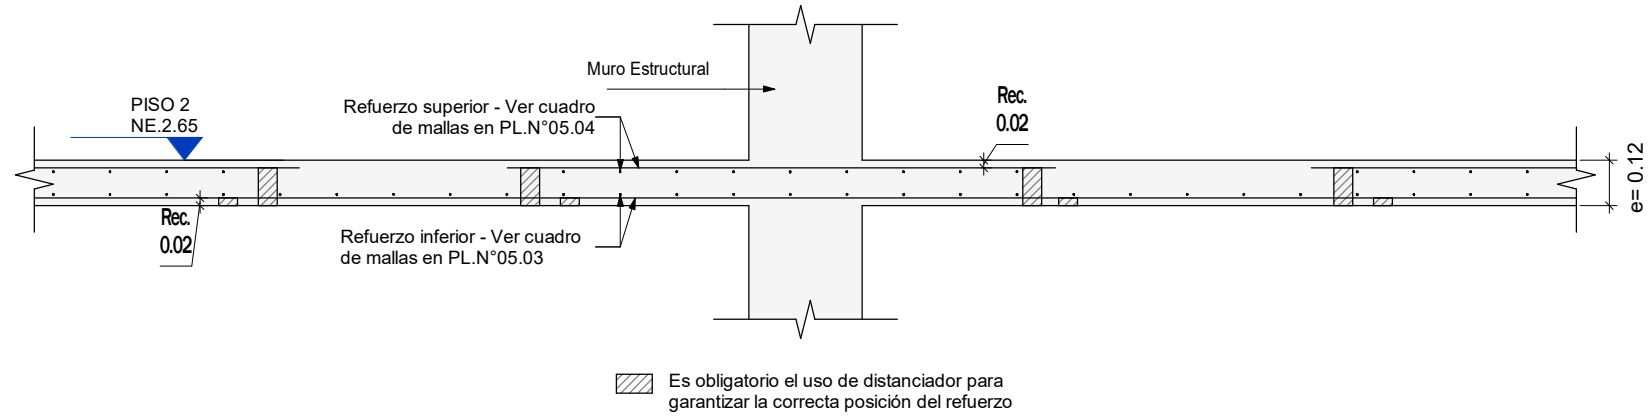




CORTE TÍPICO PLACA ÁEREA e=0.12
Escala 1 : 20

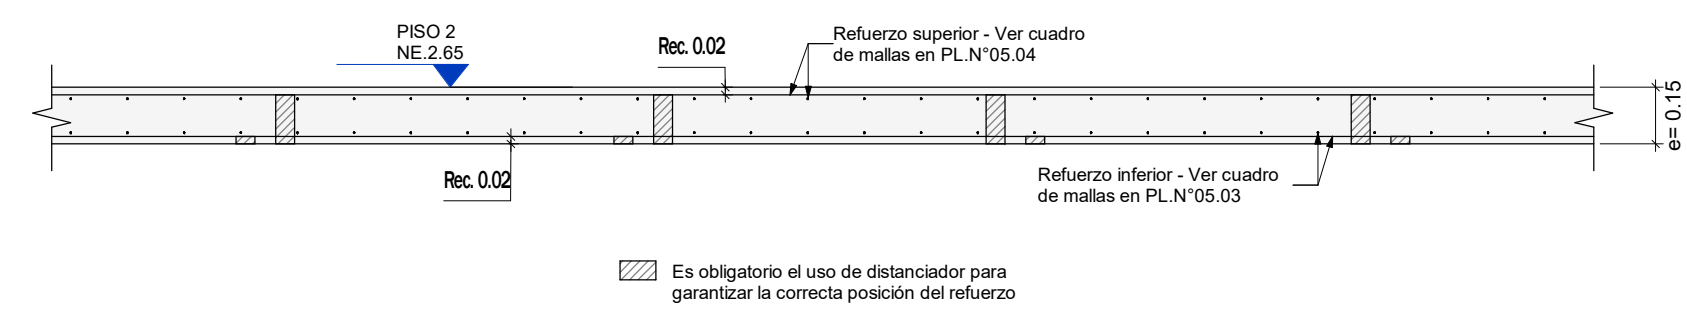

CORTE TÍPICO PLACA ÁEREA e=0.15
Escala 1 : 20

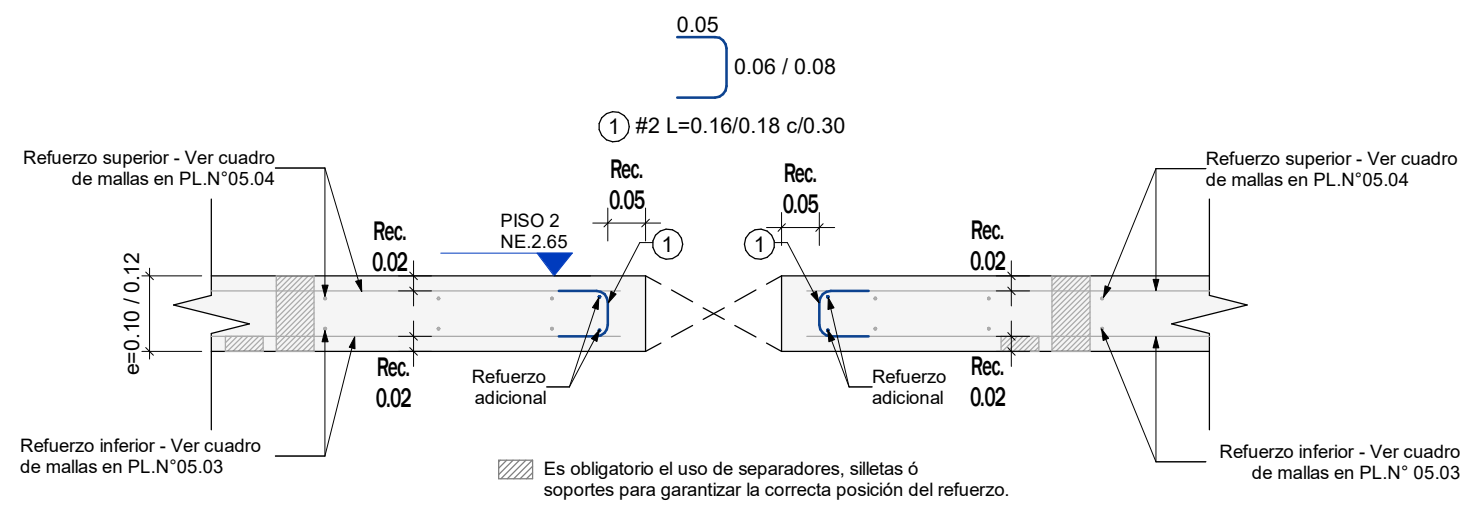

DETALLE TÍPICO - UBICACIÓN REFUERZO ADICIONAL
Escala 1 : 10

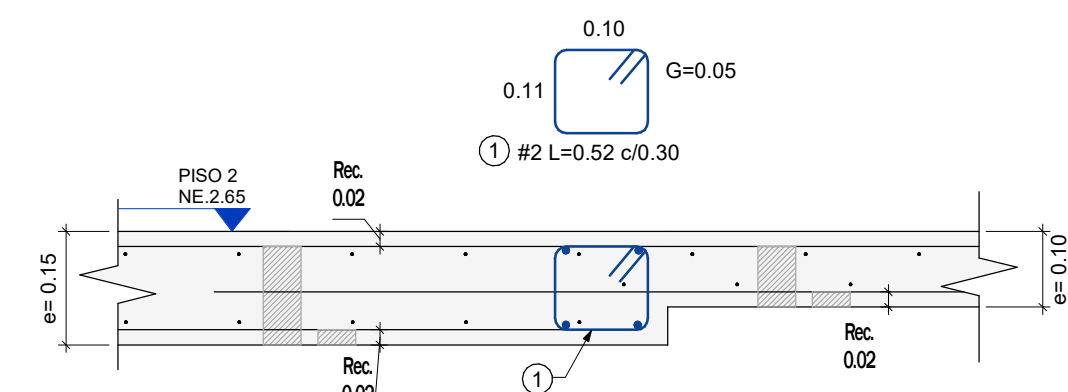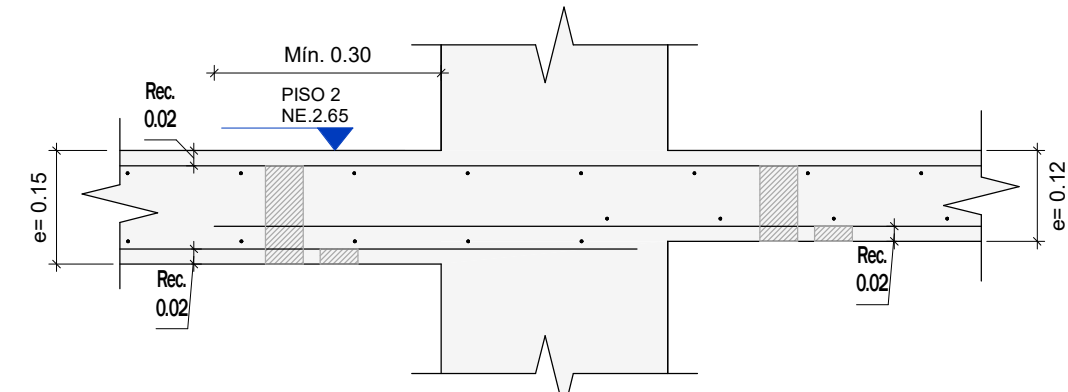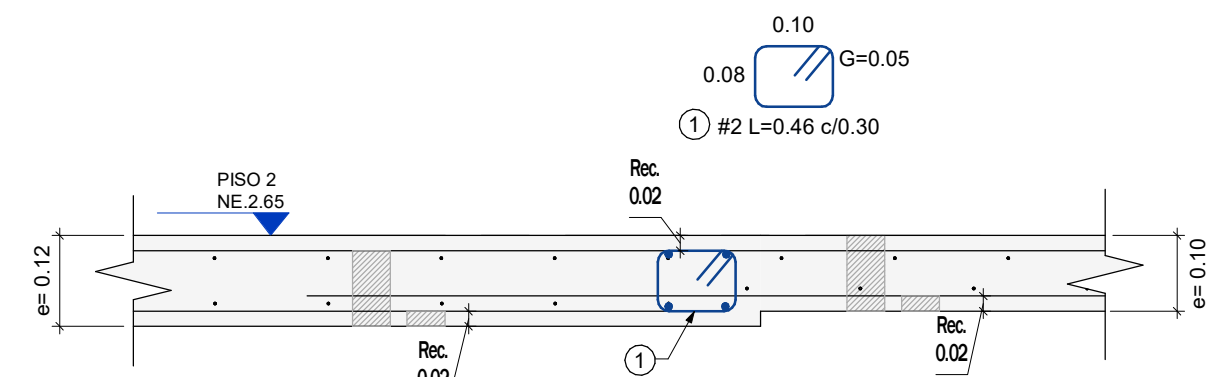

DETALLES TÍPICOS - CAMBIO DE SECCIÓN
Escala 1 : 10

Nota: en el perímetro del piso tener en cuenta
refuerzo indicado en plano N° 13.00 - Muros
de fachada

CONVENCIONES			
	Indica dinteles		
	Indica placa e=0.10		
	Indica placa e=0.12		
	Indica placa e=0.15		
	Indica muro e=0.15		
	Indica muro e=0.30		
	Indica muro e=0.35		
	Indica muro e=0.40		

NOTAS:
1. Ver detalles generales en PL. N°01.02
2. Ver planta de localización e identificación de dinteles en PL. N° 05.01
3. Ver despieces de dinteles en PL. N° 10.00 a 10.04

CONCRETO: LOSAS Y DINTELES			
* DE PISO 1 A PISO 8	* DE PISO 9 A PISO 15	* DE PISO 16 A PISO 22	* DE PISO 23 A CUBIERTA ASCENSOR Y ESCALERAS
f_c=35 MPa	f_c=32 MPa	f_c=25 MPa	f_c=21 MPa
f_c=350 kg/cm²	f_c=315 kg/cm²	f_c=245 kg/cm²	f_c=210 kg/cm²
f_c=5000 psi	f_c=4500 psi	f_c=3500 psi	f_c=3000 psi

PLANO N° 05.02

VERSIÓN : 2



GERENTE DE PROYECTO
ROBERTO AYCARDI F.
MAT. 2520257258 CND

INGENIERO
CARLOS ANDRÉS WILCHES C.

MODELADOR
DANIEL CASTELLANOS

MODIFICACIONES	FECHA
Emisión Inicial	28-02-2025
Ajuste borde de placa ejes H-4, H-12, B-4 y B-12	26-02-2026



LA SCALA

LA SCALA_EST_TOR-1

TORRE 1

CALLE 170 CON AV. BOYACA

PLANTA DE REFUERZO ADICIONAL PISO 2

LA SCALA_EST_TOR-1_05.02_P2-RADC

REVISOR ESTRUCTURAL

RAMÓN ANDRÉS ALVAREZ MANTILLA
MAT. 25202-346546 CND.

PLANO N°

VERSIÓN :

05.02

2