



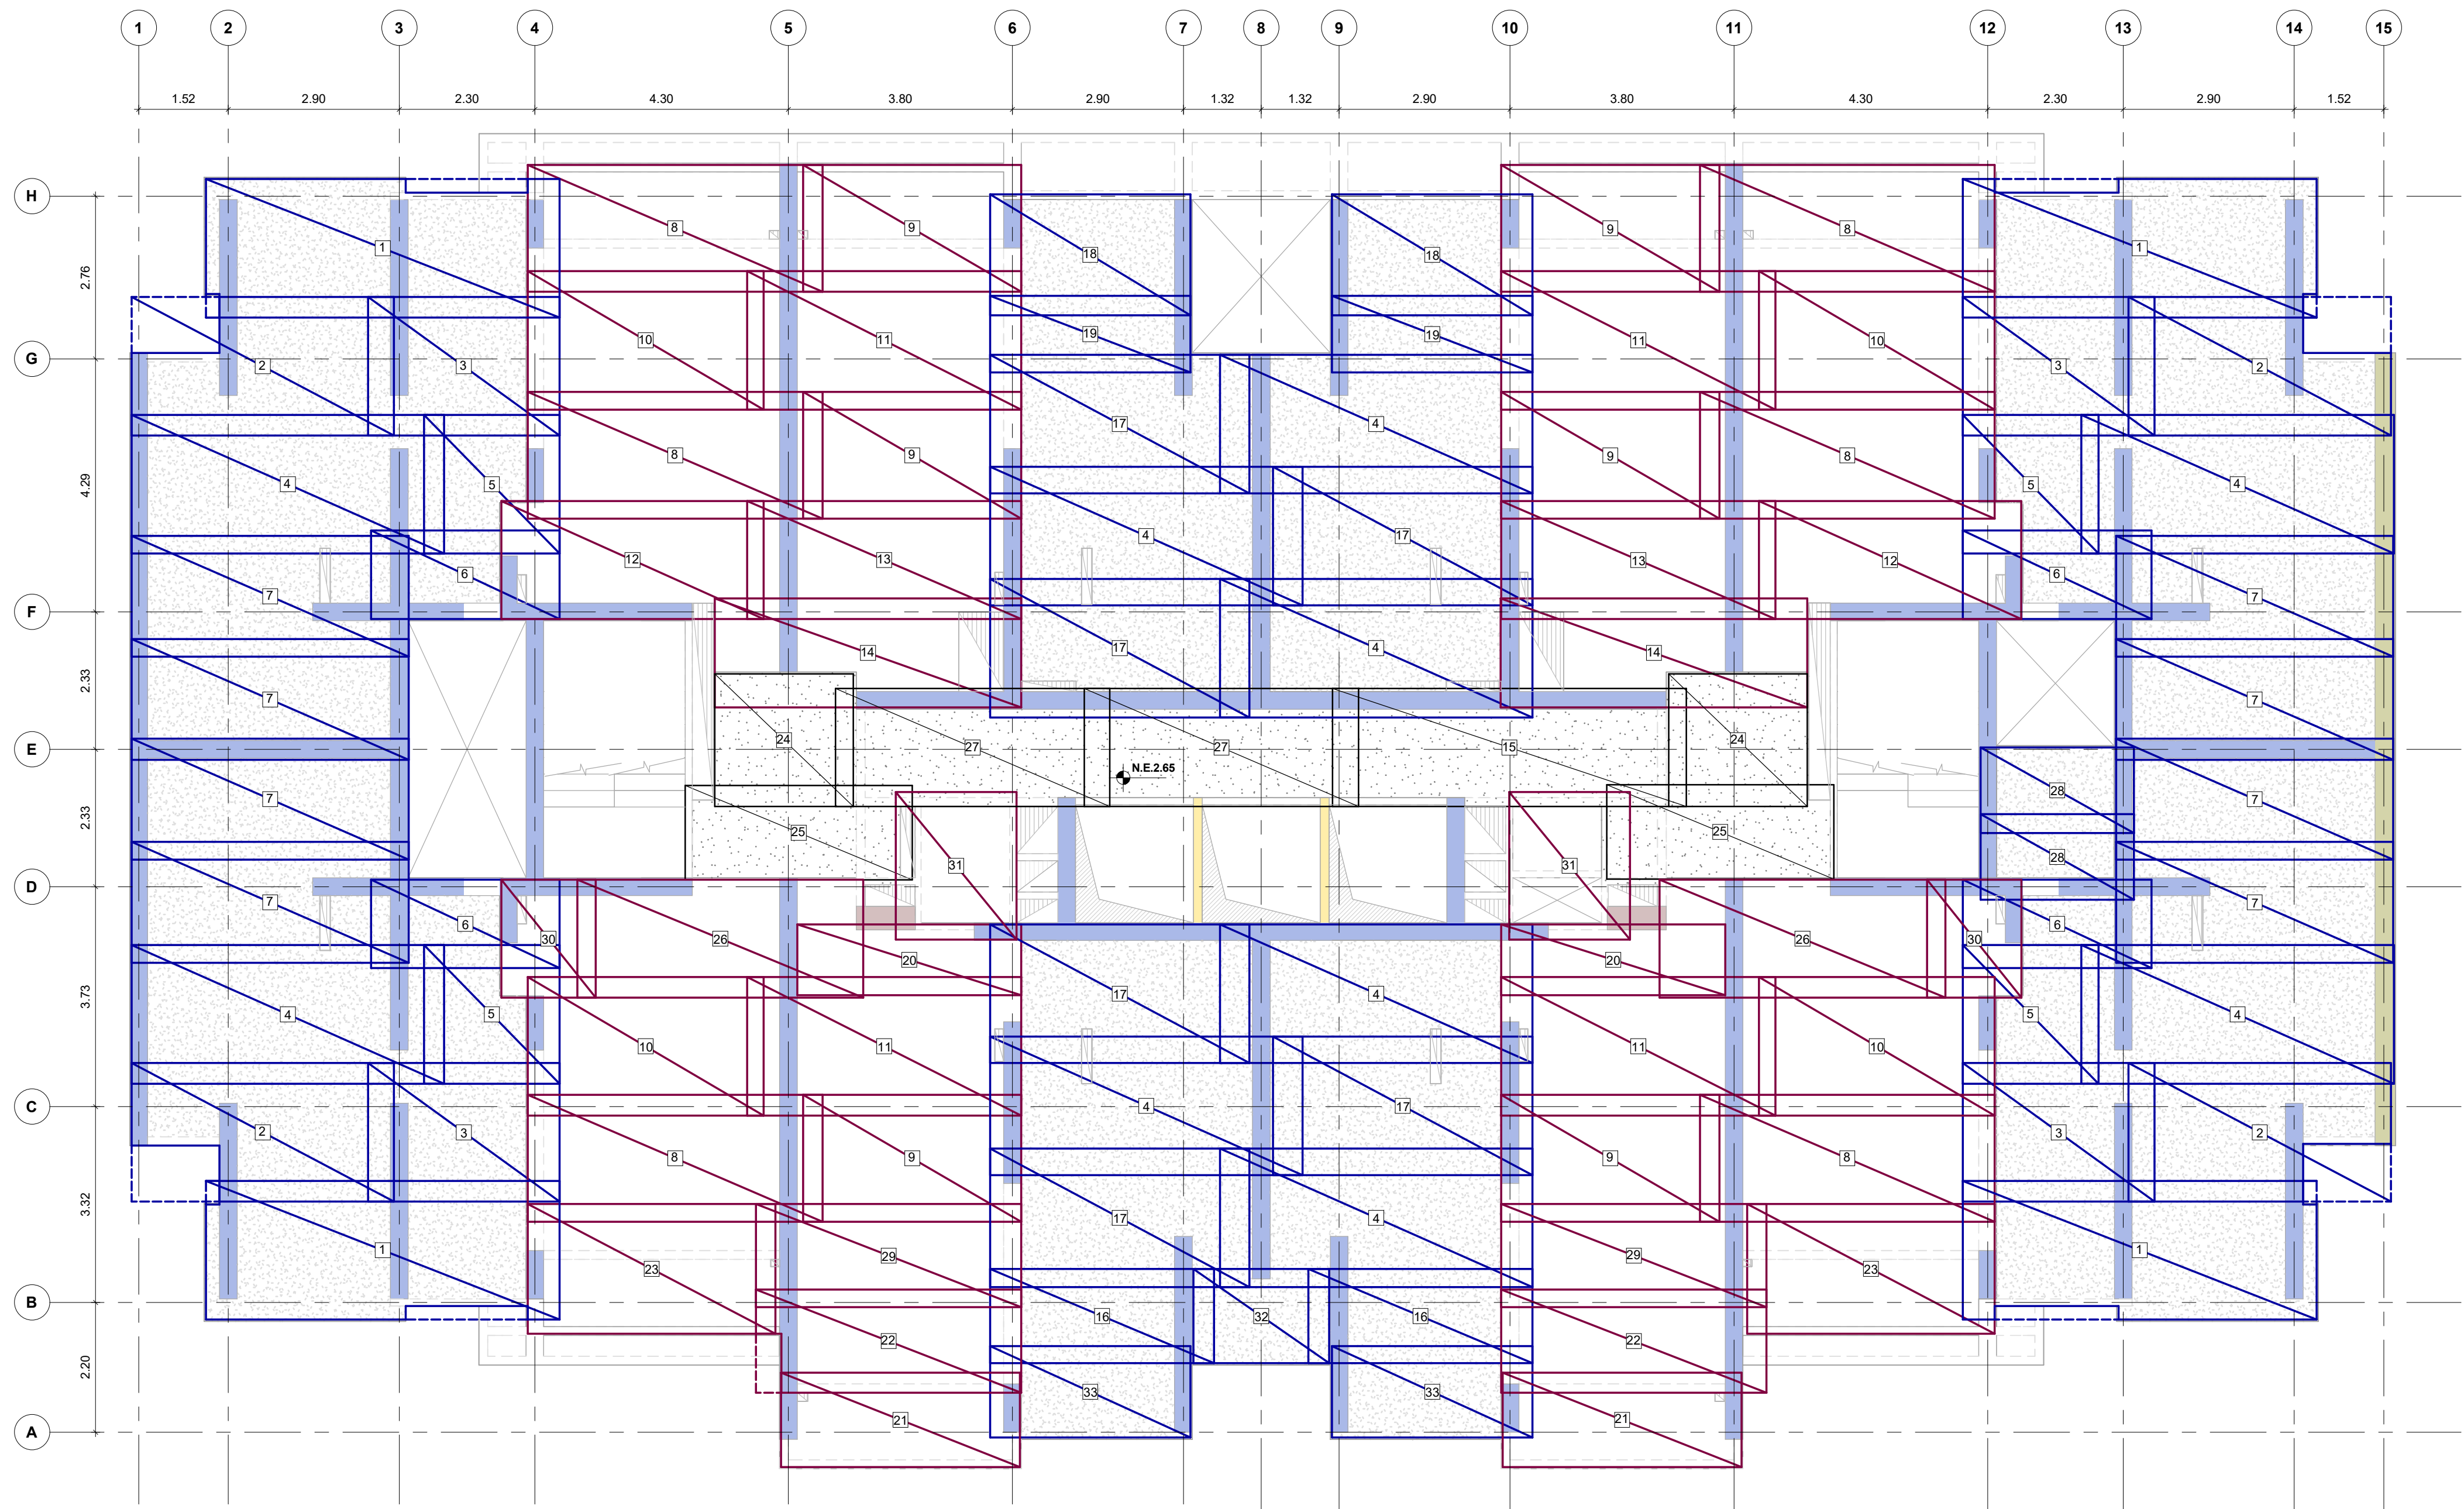


PLANTA DE REFUERZO INFERIOR PISO 2
Escala 1 : 75

CUADRO DE MALLAS REFUERZO INFERIOR PISO 2								
TIPO	A (m)	B(m)	ÁREA (m²)	CANT.	REFUERZO		PESO / MALLA (Kg/m²)	PESO (Kg)
					REFUERZO A	REFUERZO B		
1	6.00	2.35	14 m²	4	Ø6.0mm c/0.15	Ø6.0mm c/0.15	2.993	169
2	4.45	2.35	10 m²	4	Ø6.0mm c/0.15	Ø6.0mm c/0.15	2.993	125
3	3.25	2.35	8 m²	4	Ø6.0mm c/0.15	Ø6.0mm c/0.15	2.993	91
4	5.30	2.35	12 m²	10	Ø6.0mm c/0.15	Ø6.0mm c/0.15	2.993	373
5	2.35	2.30	5 m²	4	Ø6.0mm c/0.15	Ø6.0mm c/0.15	2.993	65
6	3.20	1.50	5 m²	4	Ø6.0mm c/0.15	Ø6.0mm c/0.15	2.993	57
7	4.70	2.05	10 m²	8	Ø6.0mm c/0.15	Ø6.0mm c/0.15	2.993	231
8	5.00	2.15	11 m²	6	Ø6.5mm c/0.15	Ø6.5mm c/0.15	3.518	227
9	3.70	2.15	8 m²	6	Ø6.5mm c/0.15	Ø6.5mm c/0.15	3.518	168
10	4.00	2.35	9 m²	4	Ø6.5mm c/0.15	Ø6.5mm c/0.15	3.518	132
11	4.65	2.35	11 m²	4	Ø6.5mm c/0.15	Ø6.5mm c/0.15	3.518	154
12	4.45	2.00	9 m²	2	Ø6.5mm c/0.15	Ø6.5mm c/0.15	3.518	63
13	4.65	2.00	9 m²	2	Ø6.5mm c/0.15	Ø6.5mm c/0.15	3.518	65
14	5.20	1.85	10 m²	2	Ø6.5mm c/0.15	Ø6.5mm c/0.15	3.518	68
15	6.00	2.00	12 m²	1	Ø7.5mm c/0.15	Ø7.5mm c/0.15	4.674	56
16	3.80	1.60	6 m²	2	Ø6.0mm c/0.15	Ø6.0mm c/0.15	2.993	36
17	4.40	2.35	10 m²	6	Ø6.0mm c/0.15	Ø6.0mm c/0.15	2.993	186
18	3.40	2.05	7 m²	2	Ø6.0mm c/0.15	Ø6.0mm c/0.15	2.993	42
19	3.40	1.30	4 m²	2	Ø6.0mm c/0.15	Ø6.0mm c/0.15	2.993	26
20	3.80	1.20	5 m²	2	Ø6.5mm c/0.15	Ø6.5mm c/0.15	3.518	32
21	4.05	1.60	6 m²	2	Ø6.5mm c/0.15	Ø6.5mm c/0.15	3.518	46
22	4.50	1.75	8 m²	2	Ø6.5mm c/0.15	Ø6.5mm c/0.15	3.518	55
23	4.20	2.20	9 m²	2	Ø6.5mm c/0.15	Ø6.5mm c/0.15	3.518	65
24	2.35	2.25	5 m²	2	Ø7.5mm c/0.15	Ø7.5mm c/0.15	4.674	49
25	3.85	1.60	6 m²	2	Ø7.5mm c/0.15	Ø7.5mm c/0.15	4.674	58
26	4.85	2.00	10 m²	2	Ø6.5mm c/0.15	Ø6.5mm c/0.15	3.518	68
27	4.65	2.00	9 m²	2	Ø7.5mm c/0.15	Ø7.5mm c/0.15	4.674	87
28	2.60	1.45	4 m²	2	Ø6.0mm c/0.15	Ø6.0mm c/0.15	2.993	23
29	4.50	1.75	8 m²	2	Ø6.5mm c/0.15	Ø6.5mm c/0.15	3.518	55
30	1.60	2.00	3 m²	2	Ø6.5mm c/0.15	Ø6.5mm c/0.15	3.518	23
31	2.50	2.05	5 m²	2	Ø6.5mm c/0.15	Ø6.5mm c/0.15	3.518	36
32	2.30	1.60	4 m²	1	Ø6.0mm c/0.15	Ø6.0mm c/0.15	2.993	11
33	3.40	1.55	5 m²	2	Ø6.0mm c/0.15	Ø6.0mm c/0.15	2.993	32
TOTAL : 104				104			2973	

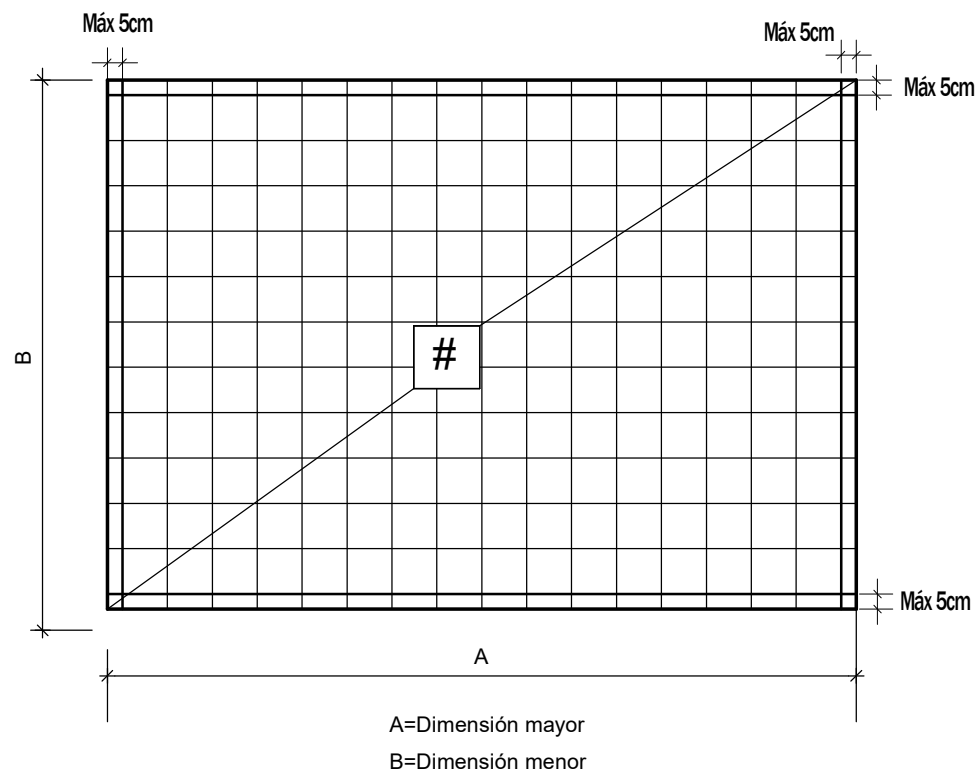

DETALLE CONVENCIÓN MALLAS
Escala 1 : 25

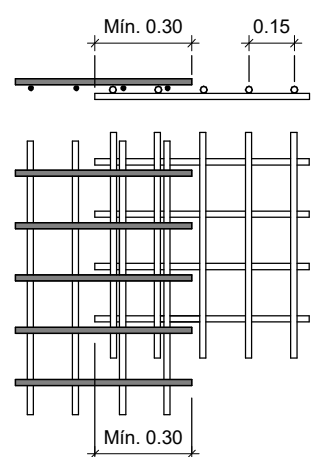

DETALLE TRASLAPO MALLAS
Escala 1 : 25

NOTAS:
1. Ver detalles generales en el PL. N° 01.02
2. Ver planta de refuerzo adicional en PL. N° 05.02
3. Ver planta de refuerzo superior en PL. N° 05.04
4. Las dimensiones de las mallas deben ser verificadas por el constructor.

CONCRETO: LOSAS Y DINTELES			
* DE PISO 1 A PISO 8	* DE PISO 9 A PISO 15	* DE PISO 16 A PISO 22	* DE PISO 23 A CUBIERTA ASCENSOR Y ESCALERAS
f'c=35 MPa	f'c=32 MPa	f'c=25 MPa	f'c=21 MPa
f'c=350 kg/cm²	f'c=315 kg/cm²	f'c=245 kg/cm²	f'c=210 kg/cm²
f'c=5000 psi	f'c=4500 psi	f'c=3500 psi	f'c=3000 psi

CONVENCIONES	
Indica Malla	Indica cortar Malla
Indica N° de Malla	

CONVENCIONES	
Indica dinteles	Indica placa e=0.10
Indica placa e=0.12	Indica placa e=0.15
Indica placa e=0.15	Indica muros en concreto e=0.15
Indica muros en concreto e=0.30	Indica muros en concreto e=0.35
Indica muros en concreto e=0.40	

VERSIÓN :

2

PLANO N°

05.03



GERENTE DE PROYECTO

ROBERTO AYCARDI F.
MAT. 2520257258 CND

INGENIERO

CARLOS ANDRÉS WILCHES C.

MODELADOR

DANIEL CASTELLANOS

MODIFICACIONES

FECHA

Emisión Inicial	28-02-2025
Ajuste borde de placa ejes H-4, H-12, B-4 y B-12 y se actualiza cuadro de mallas	26-02-2026



LA SCALA

LA SCALA_EST_TOR-1

TORRE 1

CALLE 170 CON AV. BOYACA

PLANTA DE REFUERZO INFERIOR PISO 2

LA SCALA_EST_TOR-1_05.03_P2-RINF

REVISOR ESTRUCTURAL

RAMÓN ÁNDRES ALVAREZ MANTILLA
MAT. 25202-346546 CND.

PLANO N°

05.03

VERSIÓN :

2