



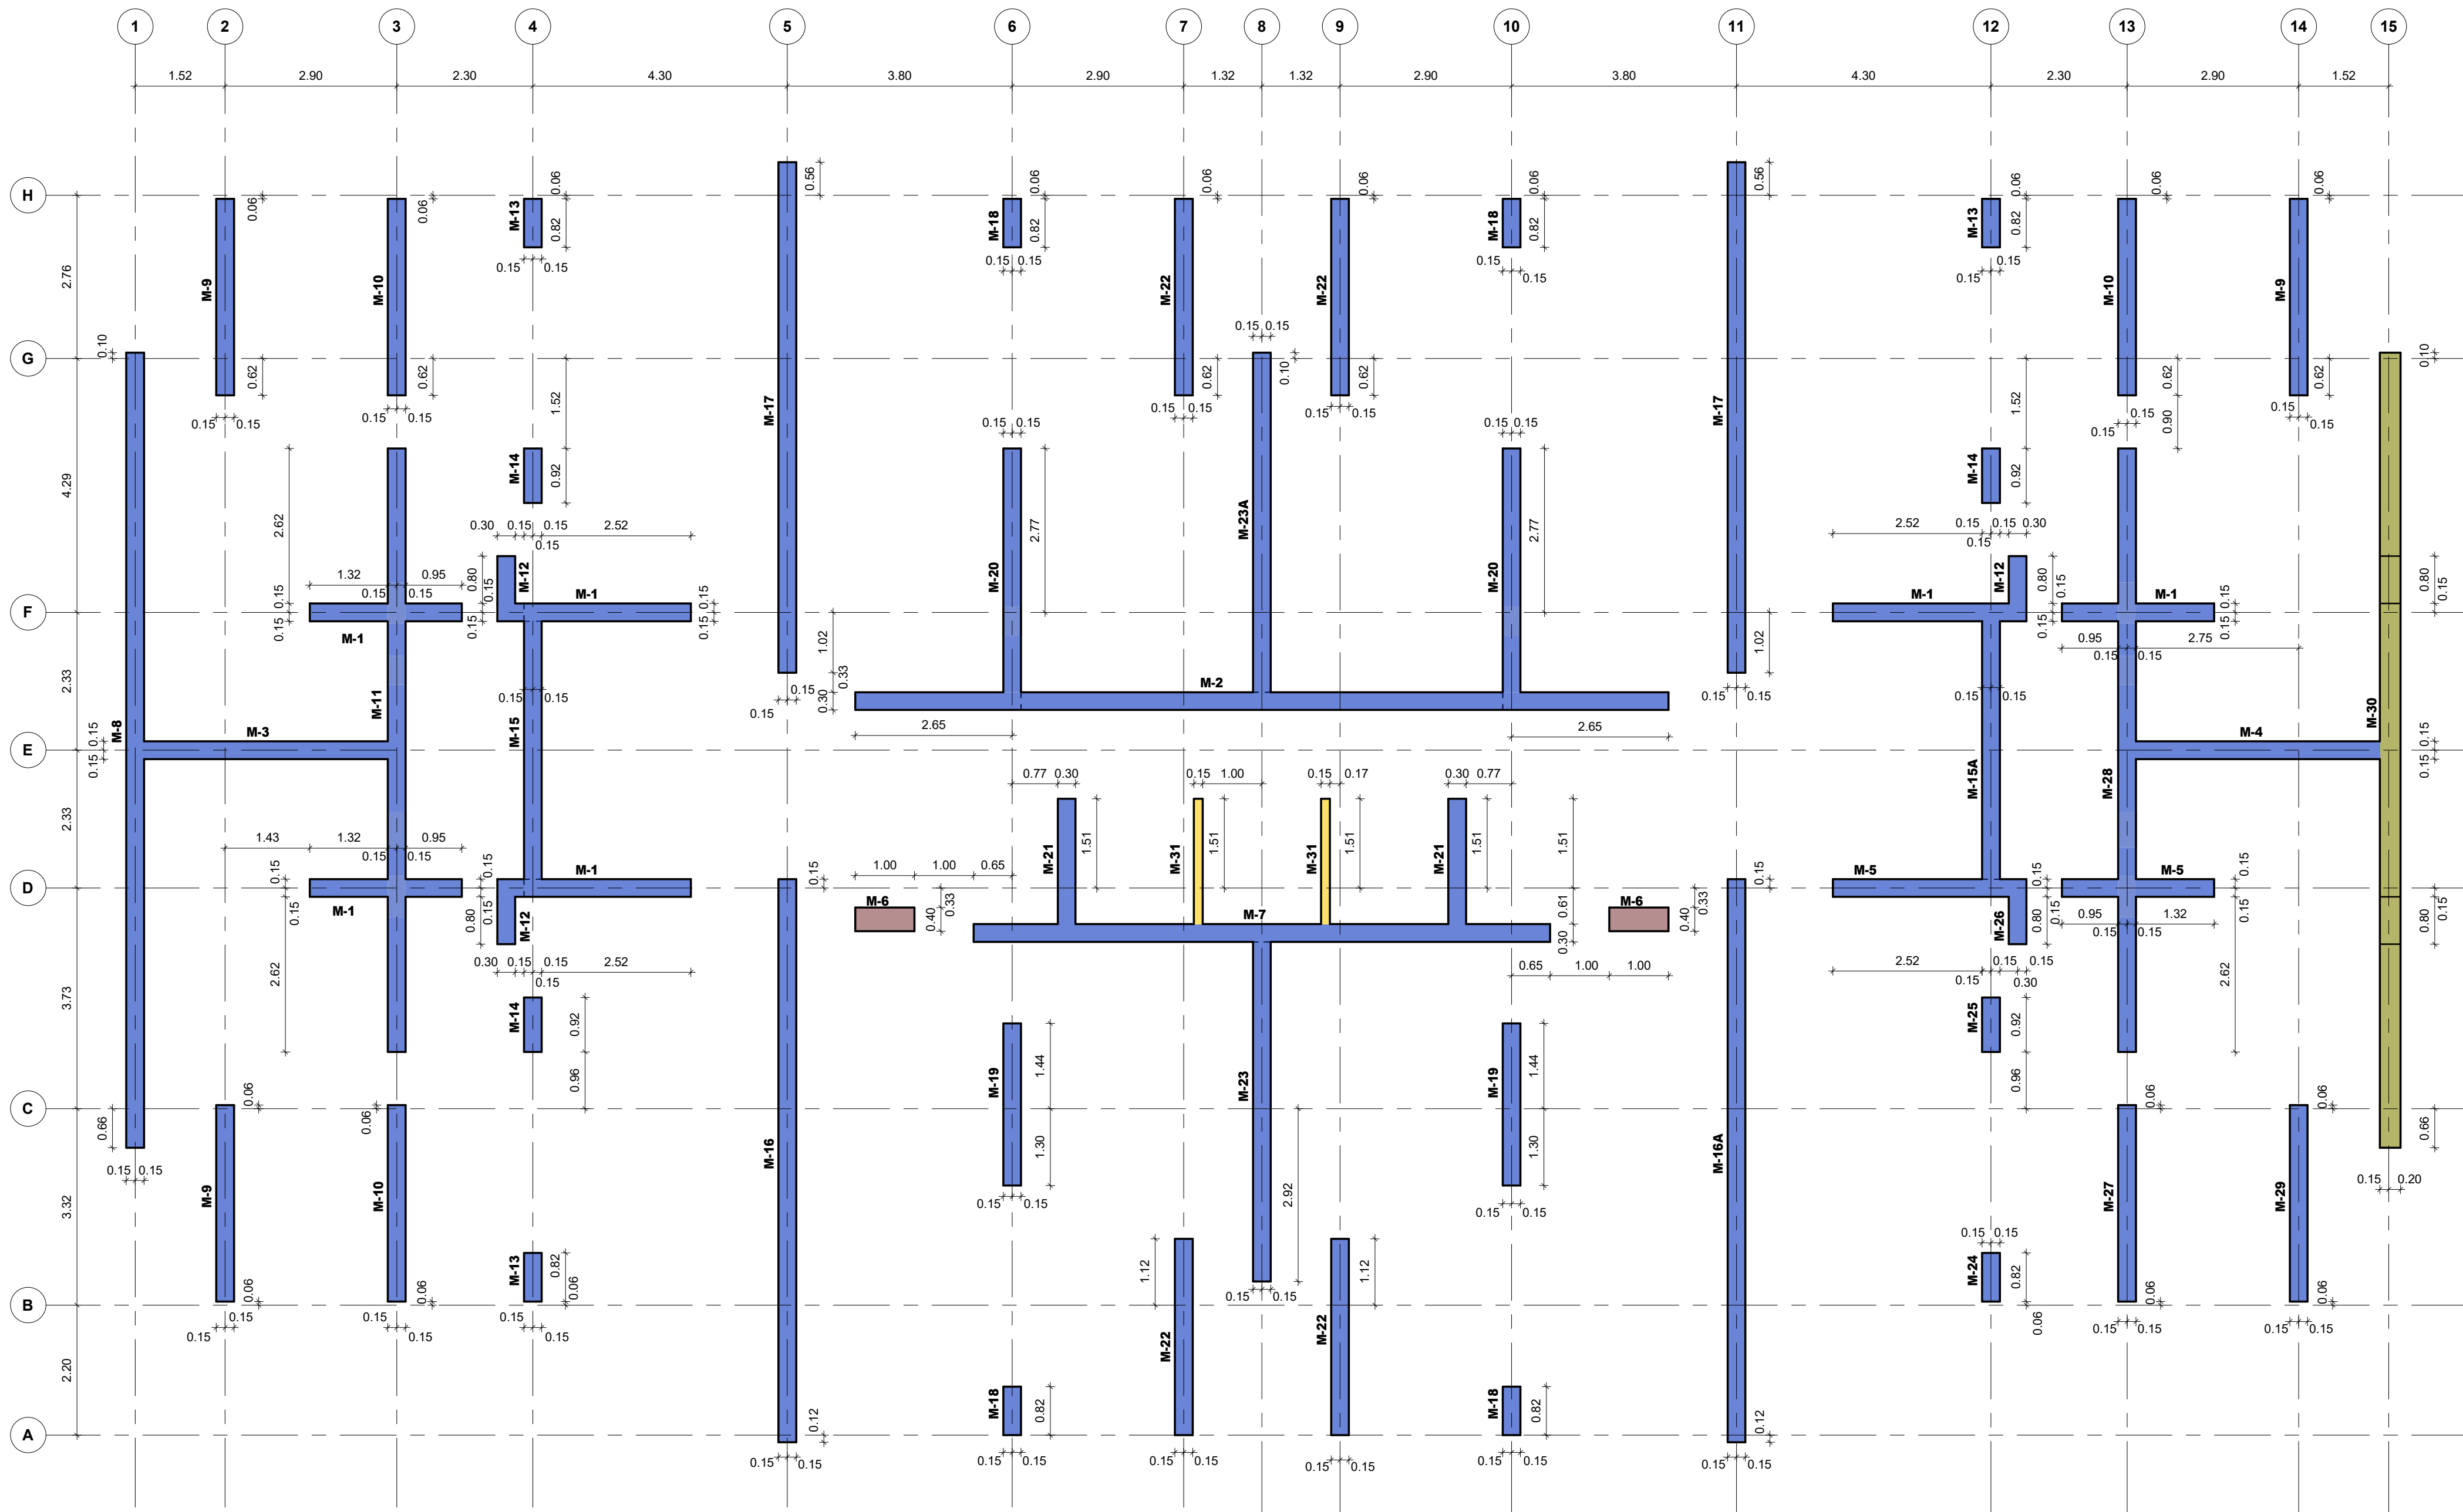

PLANTA LOCALIZACIÓN DE MUROS PISO TIPO 1 (PISO 3 A PISO 14)
Escala 1 : 75

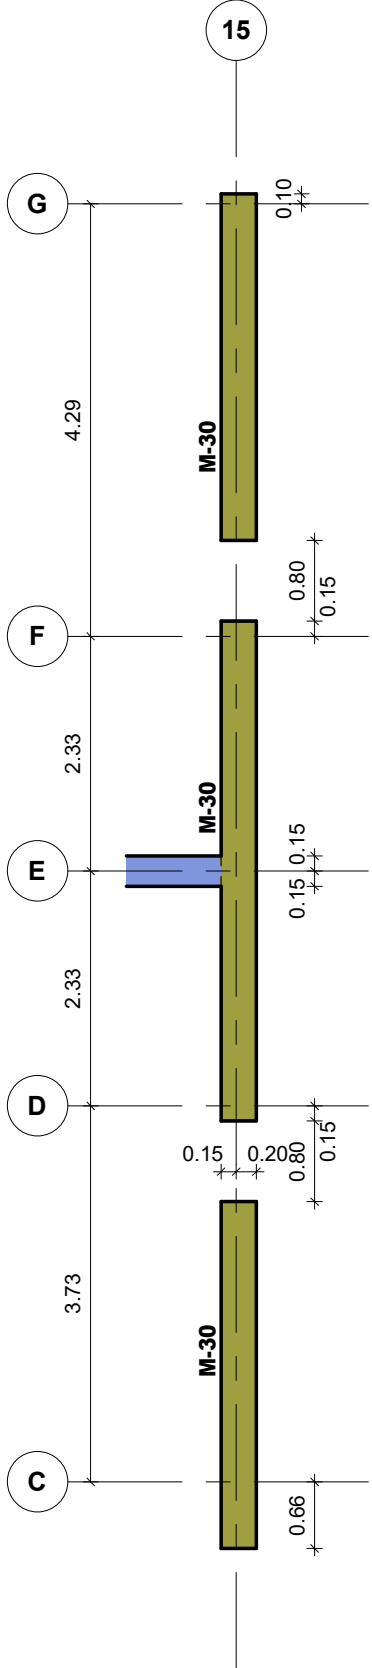

PLANTA LOCALIZACIÓN DE MURO M-30 PISO 7 A 14
Escala 1 : 75

CONCRETO:			
MUROS			
* DE CIMENTACIÓN A PISO 8	* DE PISO 8 A PISO 15	* DE PISO 15 A PISO 22	* DE PISO 22 A CUBIERTA ASCENSOR Y ESCALERAS
f'c=49 MPa	f'c=42 MPa	f'c=35 MPa	f'c=28 MPa
f'c=490 kg/cm²	f'c=420 kg/cm²	f'c=350 kg/cm²	f'c=280 kg/cm²
f'c=7000 psi	f'c=6000 psi	f'c=5000 psi	f'c=4000 psi

CUADRO NIVELES PISO 3 A PISO 15	
PISO	NIVEL(NE.)
PISO 3	5.30
PISO 4	7.95
PISO 5	10.60
PISO 6	13.25
PISO 7	15.90
PISO 8	18.55
PISO 9	21.20
PISO 10	23.85
PISO 11	26.50
PISO 12	29.15
PISO 13	31.80
PISO 14	34.45
PISO 15	37.10

CONVENCIONES	
M-#	Indica N° de Muro
	Indica muro e=0.15
	Indica muro e=0.30
	Indica muro e=0.35
	Indica muro e=0.40
NOTAS	
1. Ver detalles generales en PL. N°01.02	
2. Ver despieces de muros en PL. N° 11.00 a PL. N°11.21	
3. Ver detalles de muros en PL. N° 11.22	

VERSIÓN :

2

PLANO N° 06.00



GERENTE DE PROYECTO
ROBERTO AYCARDI F.
MAT. 2520257258 CND

INGENIERO
CARLOS ANDRÉS WILCHES C.

MODELADOR
DANIEL CASTELLANOS

MODIFICACIONES	FECHA
Emisión Inicial	28-02-2025
Se actualiza longitud de muro M-19	04-11-2025



LA SCALA

LA SCALA_EST_TOR-1

TORRE 1

CALLE 170 CON AV. BOYACA

PLANTA LOCALIZACIÓN DE MUROS PISO TIPO 1

LA SCALA_EST_TOR-1_06.00_LCM-PT1

REVISOR ESTRUCTURAL
RAMÓN ANDRÉS ALVAREZ MANTILLA
MAT. 25202-346546 CND.

PLANO N°

06.00

VERSIÓN :

2