



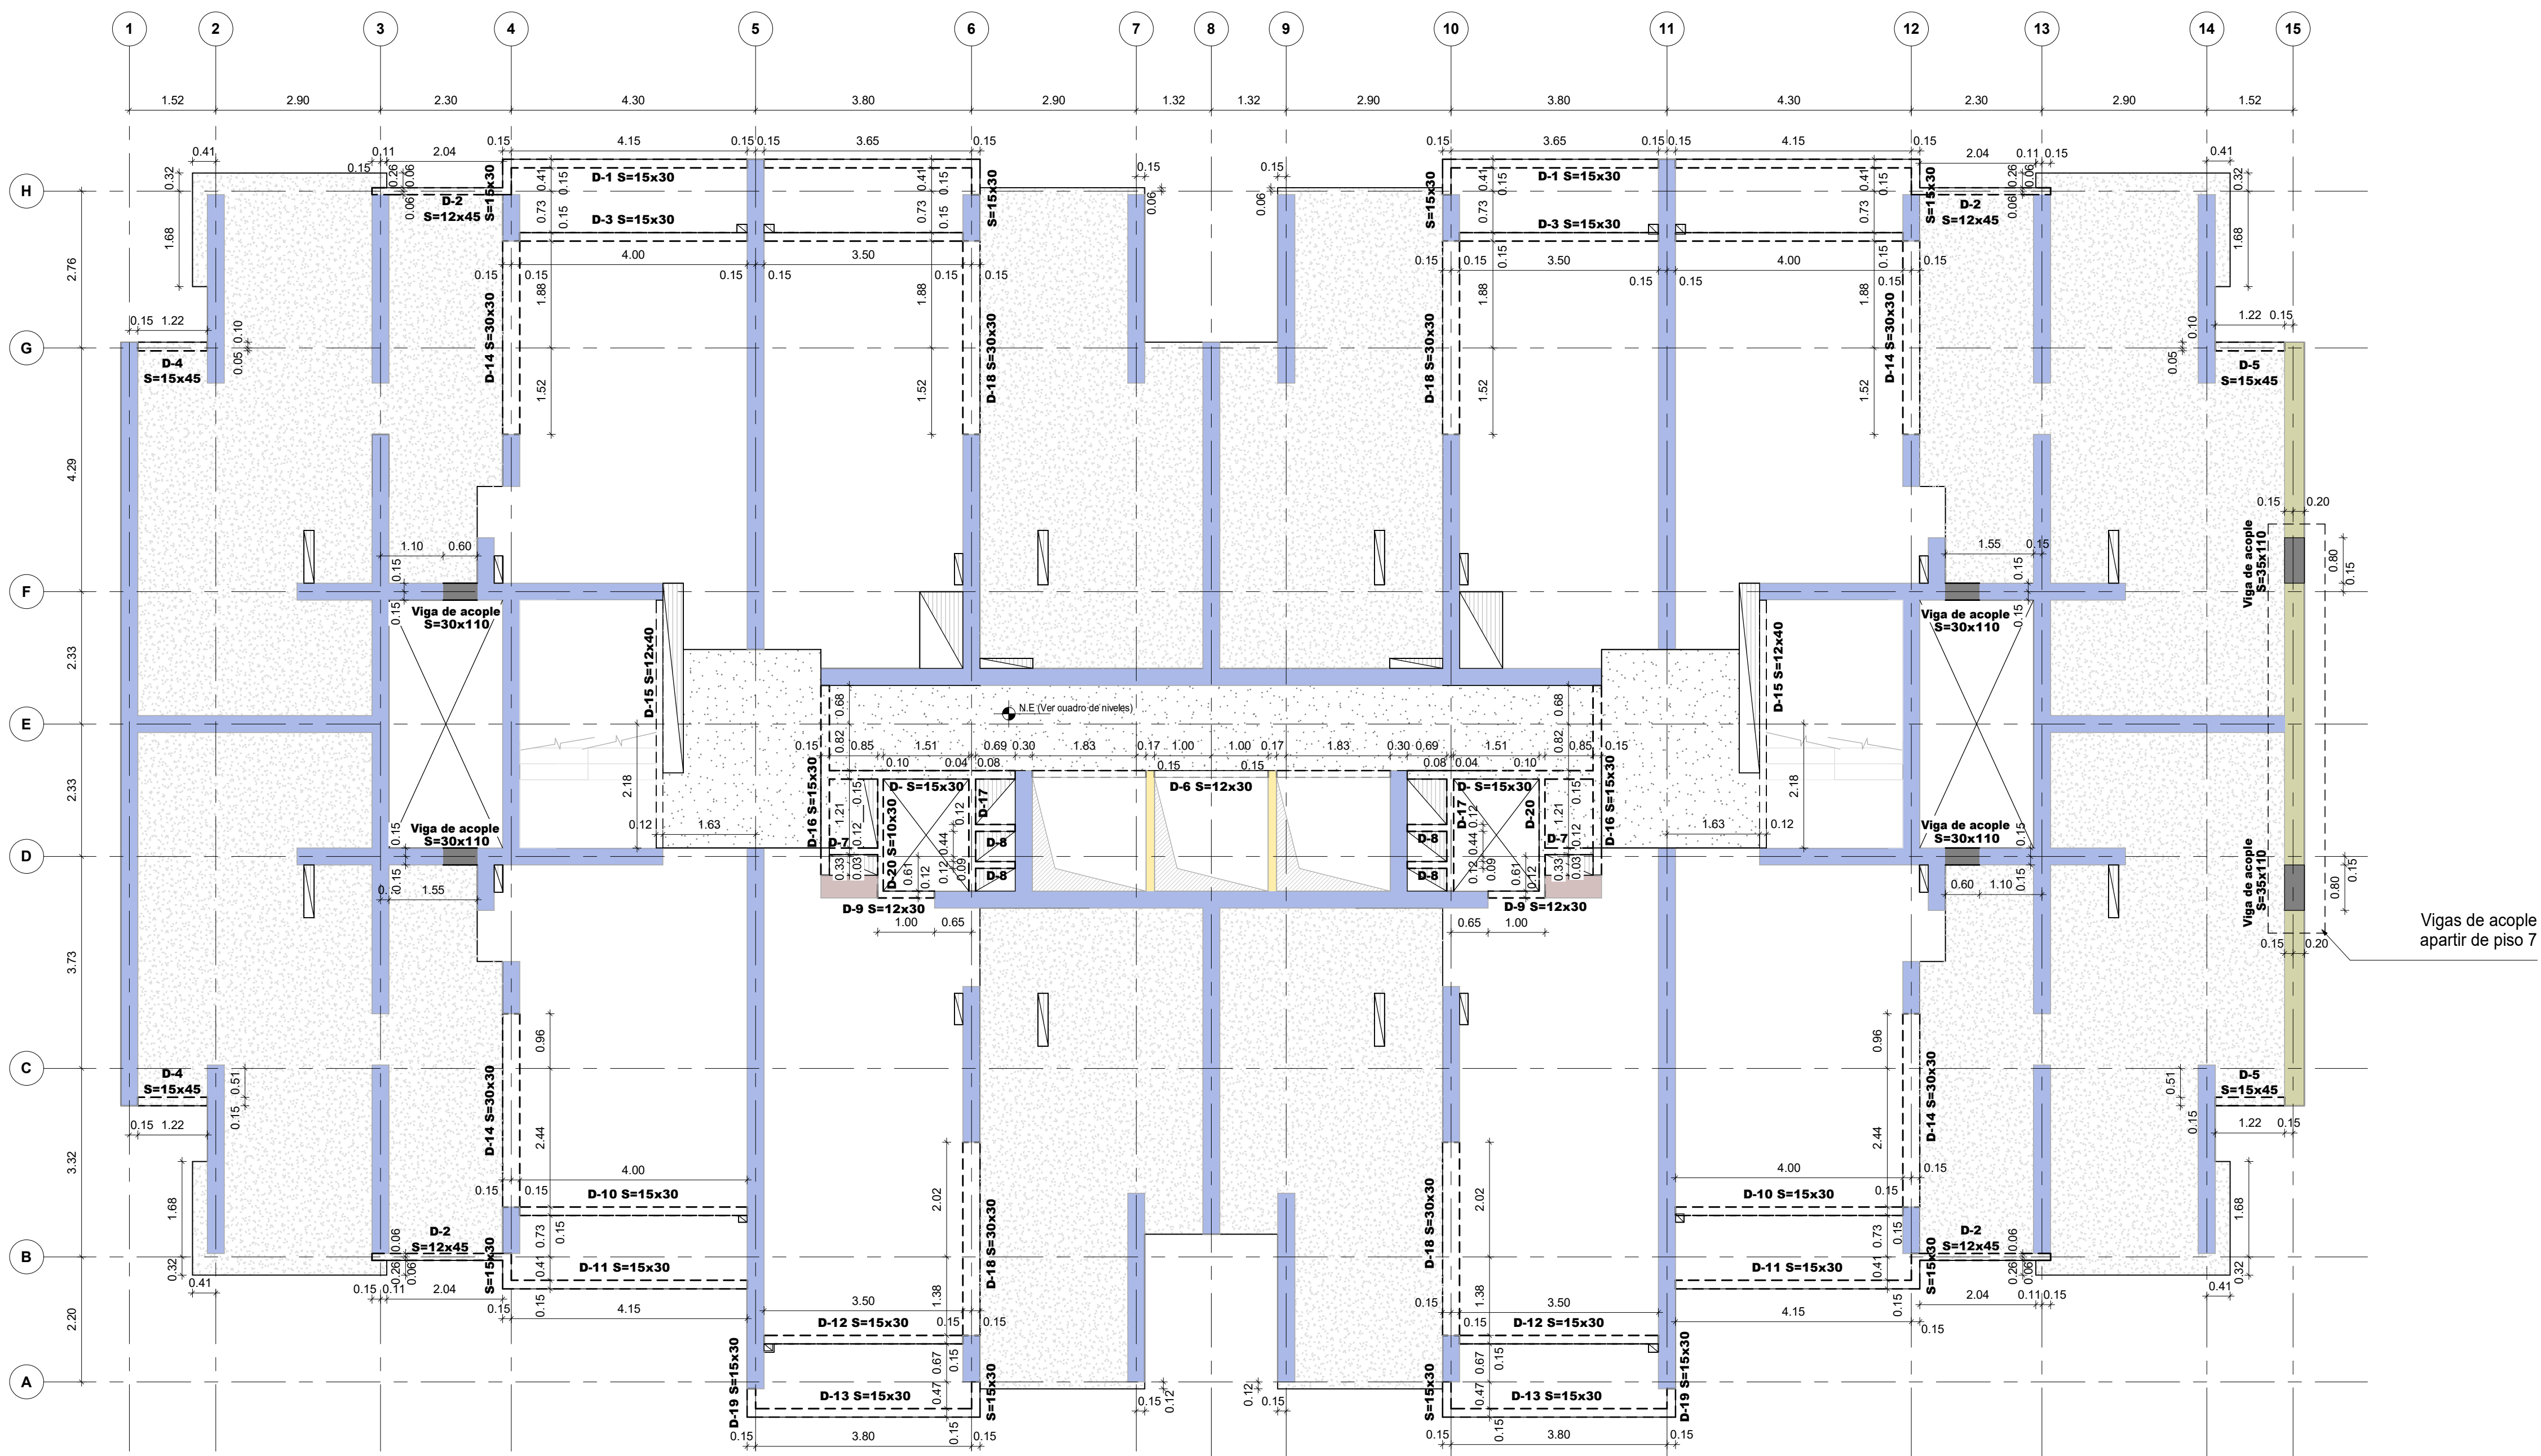

PLANTA LOCALIZACIÓN DE DINTELES PISO TIPO 1 (PISO 3 A PISO 15)
Escala 1 : 75

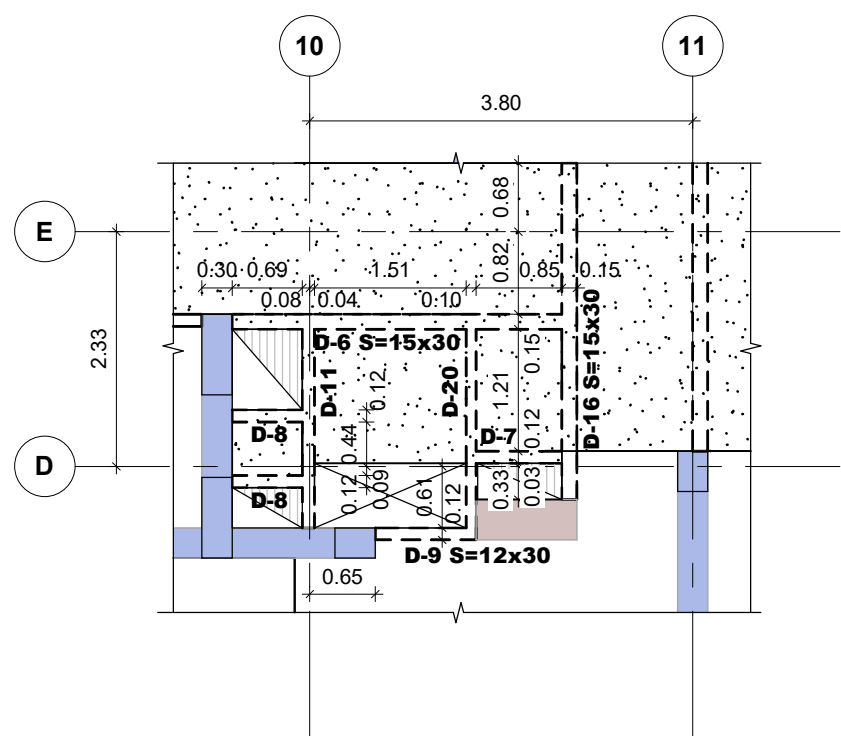

DETALLE PLACA ADICIONAL PISO 14 Y PISO 15
Escala 1 : 75

CONCRETO:			
VIGAS DE ACOPLE			
* DE PISO 2 A PISO 8	* DE PISO 8 A PISO 15	* DE PISO 15 A PISO 22	* DE PISO 22 A PISO 28
f _c =49 MPa	f _c =42 MPa	f _c =35 MPa	f _c =28 MPa
f _c =490 kg/cm ²	f _c =420 kg/cm ²	f _c =350 kg/cm ²	f _c =280 kg/cm ²
f _c =7000 psi	f _c =6000 psi	f _c =5000 psi	f _c =4000 psi

CONCRETO:			
LOSAS Y DINTELES			
* DE PISO 1 A PISO 8	* DE PISO 9 A PISO 15	* DE PISO 16 A PISO 22	* DE PISO 23 A CUBIERTA ASCENSOR Y ESCALERAS
f _c =35 MPa	f _c =32 MPa	f _c =25 MPa	f _c =21 MPa
f _c =350 kg/cm ²	f _c =315 kg/cm ²	f _c =245 kg/cm ²	f _c =210 kg/cm ²
f _c =5000 psi	f _c =4500 psi	f _c =3500 psi	f _c =3000 psi

CUADRO NIVELES PISO 3 A PISO 15	
PISO	NIVEL(N.E.)
PISO 3	5.30
PISO 4	7.85
PISO 5	10.60
PISO 6	13.25
PISO 7	15.90
PISO 8	18.55
PISO 9	21.20
PISO 10	23.85
PISO 11	26.50
PISO 12	29.15
PISO 13	31.80
PISO 14	34.45
PISO 15	37.10

- CONVENCIONES**
- Indica dinteles
 - D-# Indica N° de dintel
 - Indica Vigas de acople
 - Indica muro e=0.15
 - Indica muro e=0.30
 - Indica muro e=0.35
 - Indica muro e=0.40
 - Indica placa e=0.10
 - Indica placa e=0.12
 - Indica placa e=0.15

- NOTAS**
- Ver detalles generales en PL. N°01.02
 - Ver despieces de dinteles en PL. N° 10.00 a 10.04
 - Ver detalle viga de acople en PL. N° 11.01, 11.05 Y 11.20

VERSIÓN :

2

PLANO N°

06.01

2



GERENTE DE PROYECTO
ROBERTO AYCARDI F.
MAT. 2520257258 CND

INGENIERO
CARLOS ANDRÉS WILCHES C.

MODELADOR
DANIEL CASTELLANOS

MODIFICACIONES	FECHA
Emisión Inicial	28-02-2025
Ajuste borde de placa ejes D-6 y D-10	26-02-2026



LA SCALA

LA SCALA_EST_TOR-1

TORRE 1

CALLE 170 CON AV. BOYACA

PLANTA LOCALIZACIÓN E IDENTIFICACIÓN
DE DINTELES PISO TIPO 1 (PISO 3 A PISO
15)

LA SCALA_EST_TOR-1_06.01_LDINT-PT1

REVISOR ESTRUCTURAL

RAMÓN ANDRÉS ALVAREZ MANTILLA
MAT. 25202-346546 CND.

PLANO N°

06.01

VERSIÓN :

2