




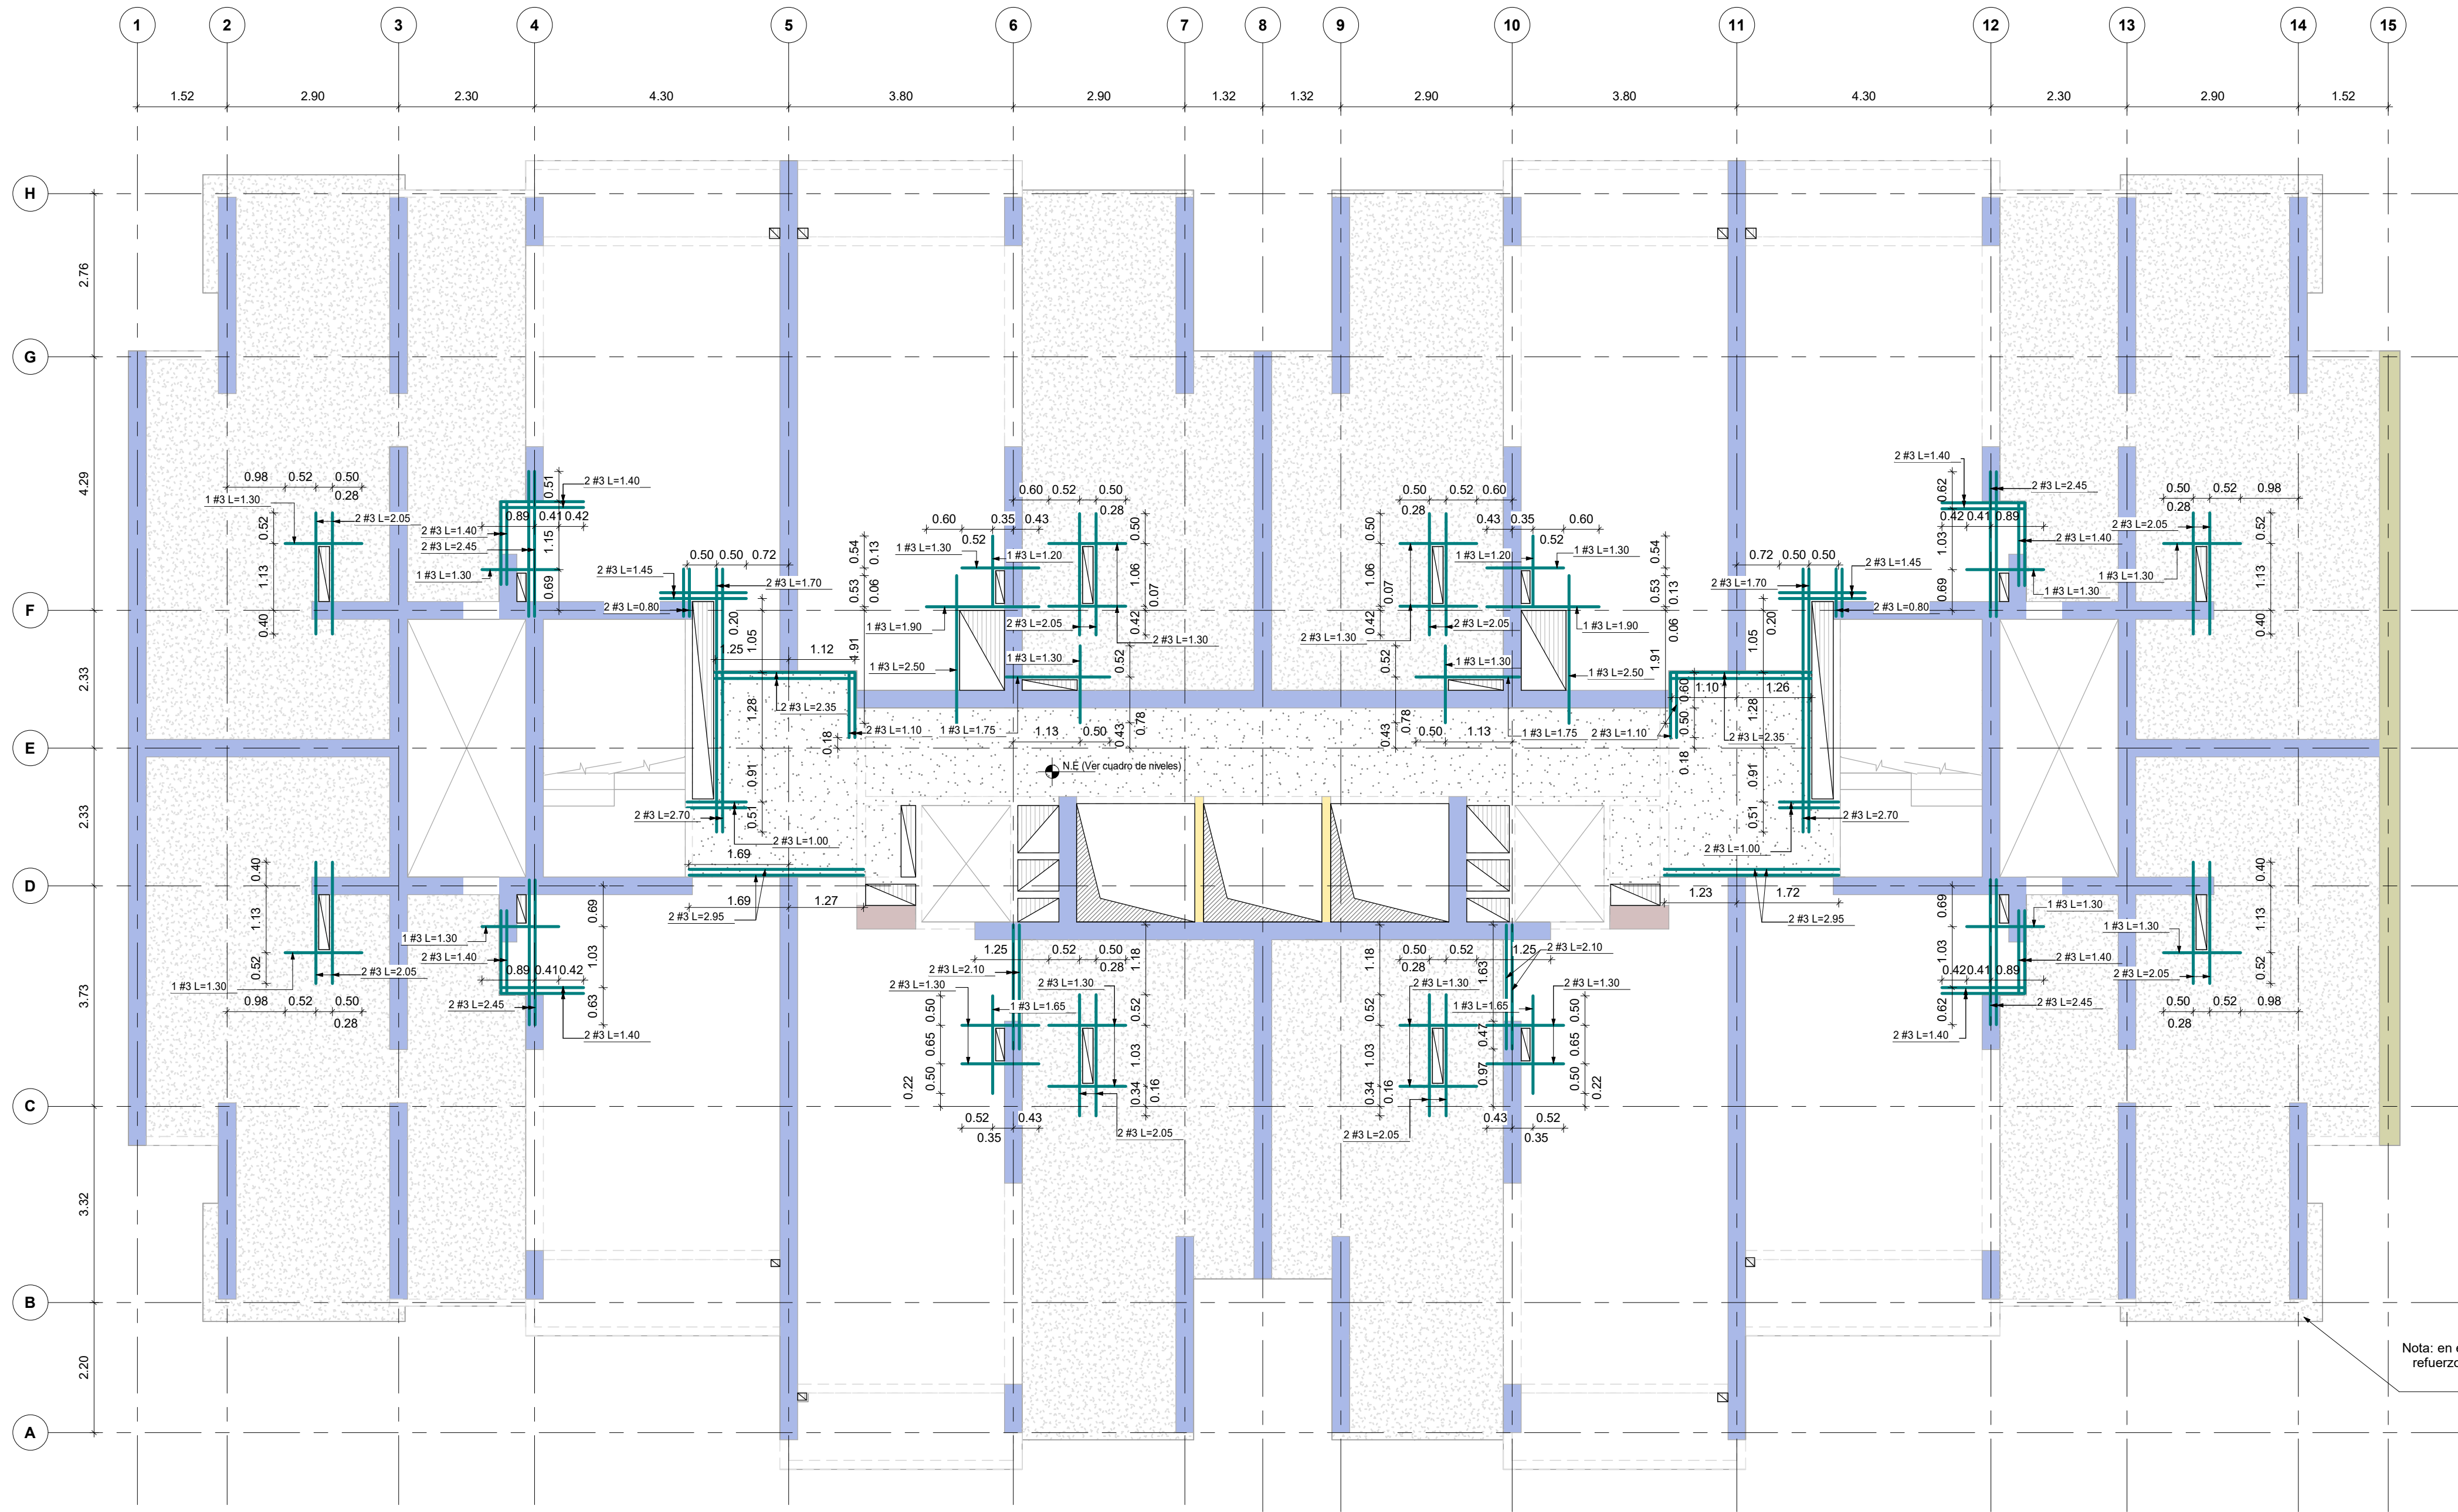


PLANTA DE REFUERZO ADICIONAL PISO TIPO 1 (PISO 3 A PISO 15)
Escala 1 : 75

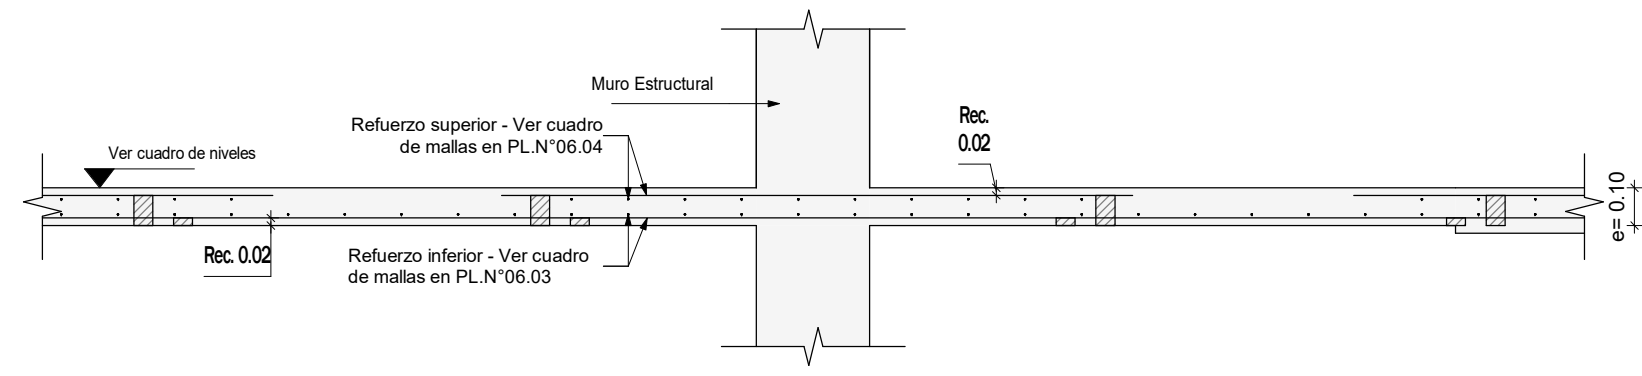


CORTE TÍPICO PLACA AÉREA e=0.10
Escala 1 : 20

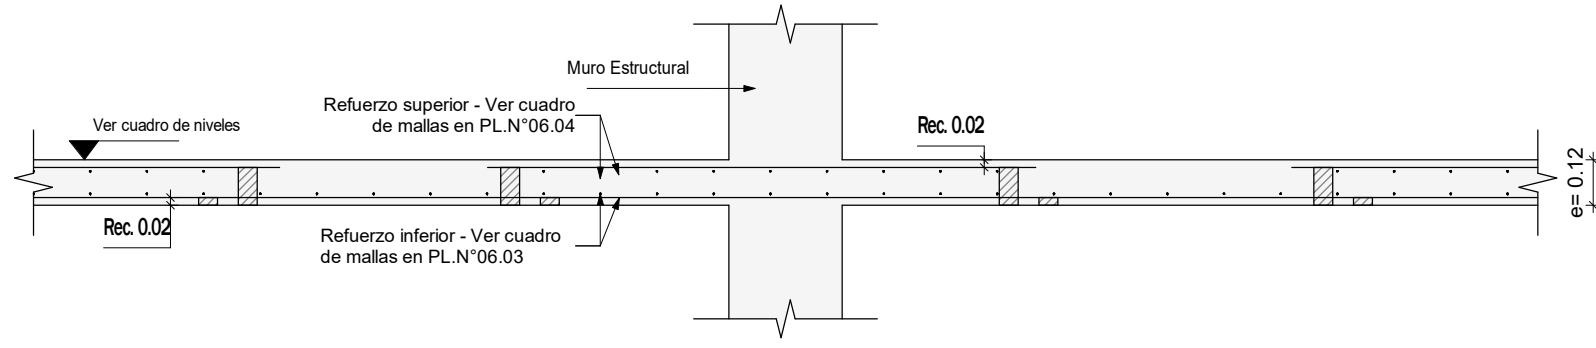


CORTE TÍPICO PLACA AÉREA e=0.12
Escala 1 : 20

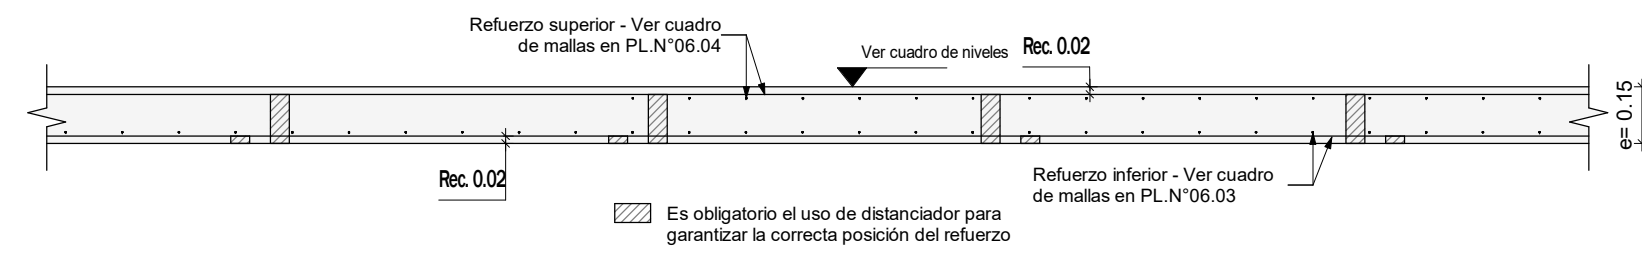

CORTE PLACA AÉREA e=0.15
Escala 1 : 20

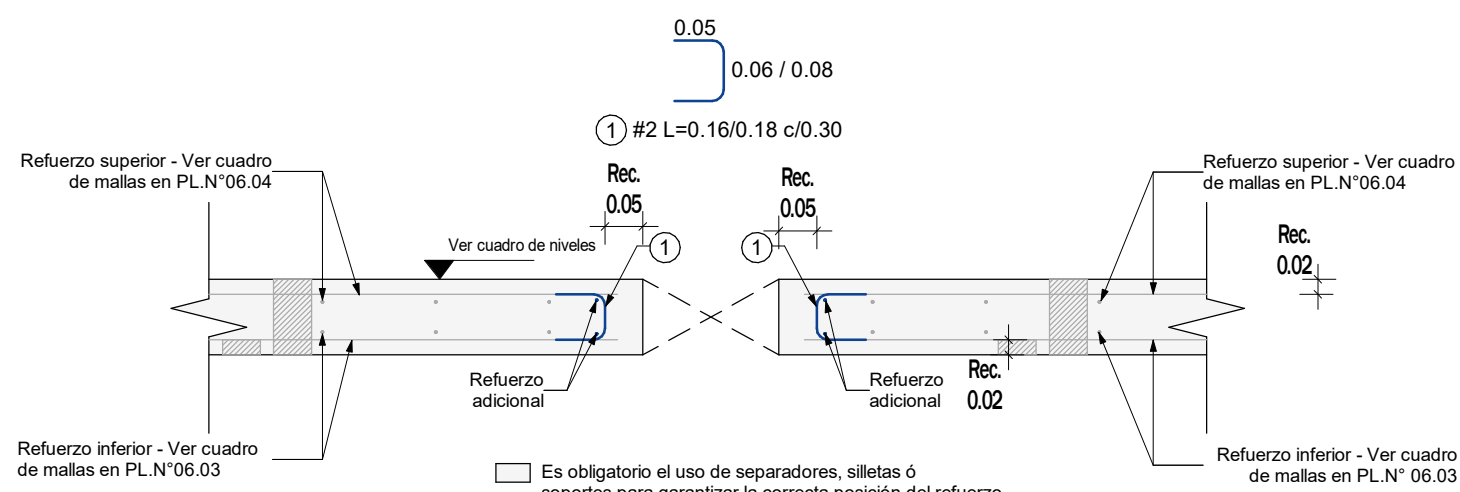

DETALLE TÍPICO - UBICACIÓN REFUERZO ADICIONAL
Escala 1 : 10

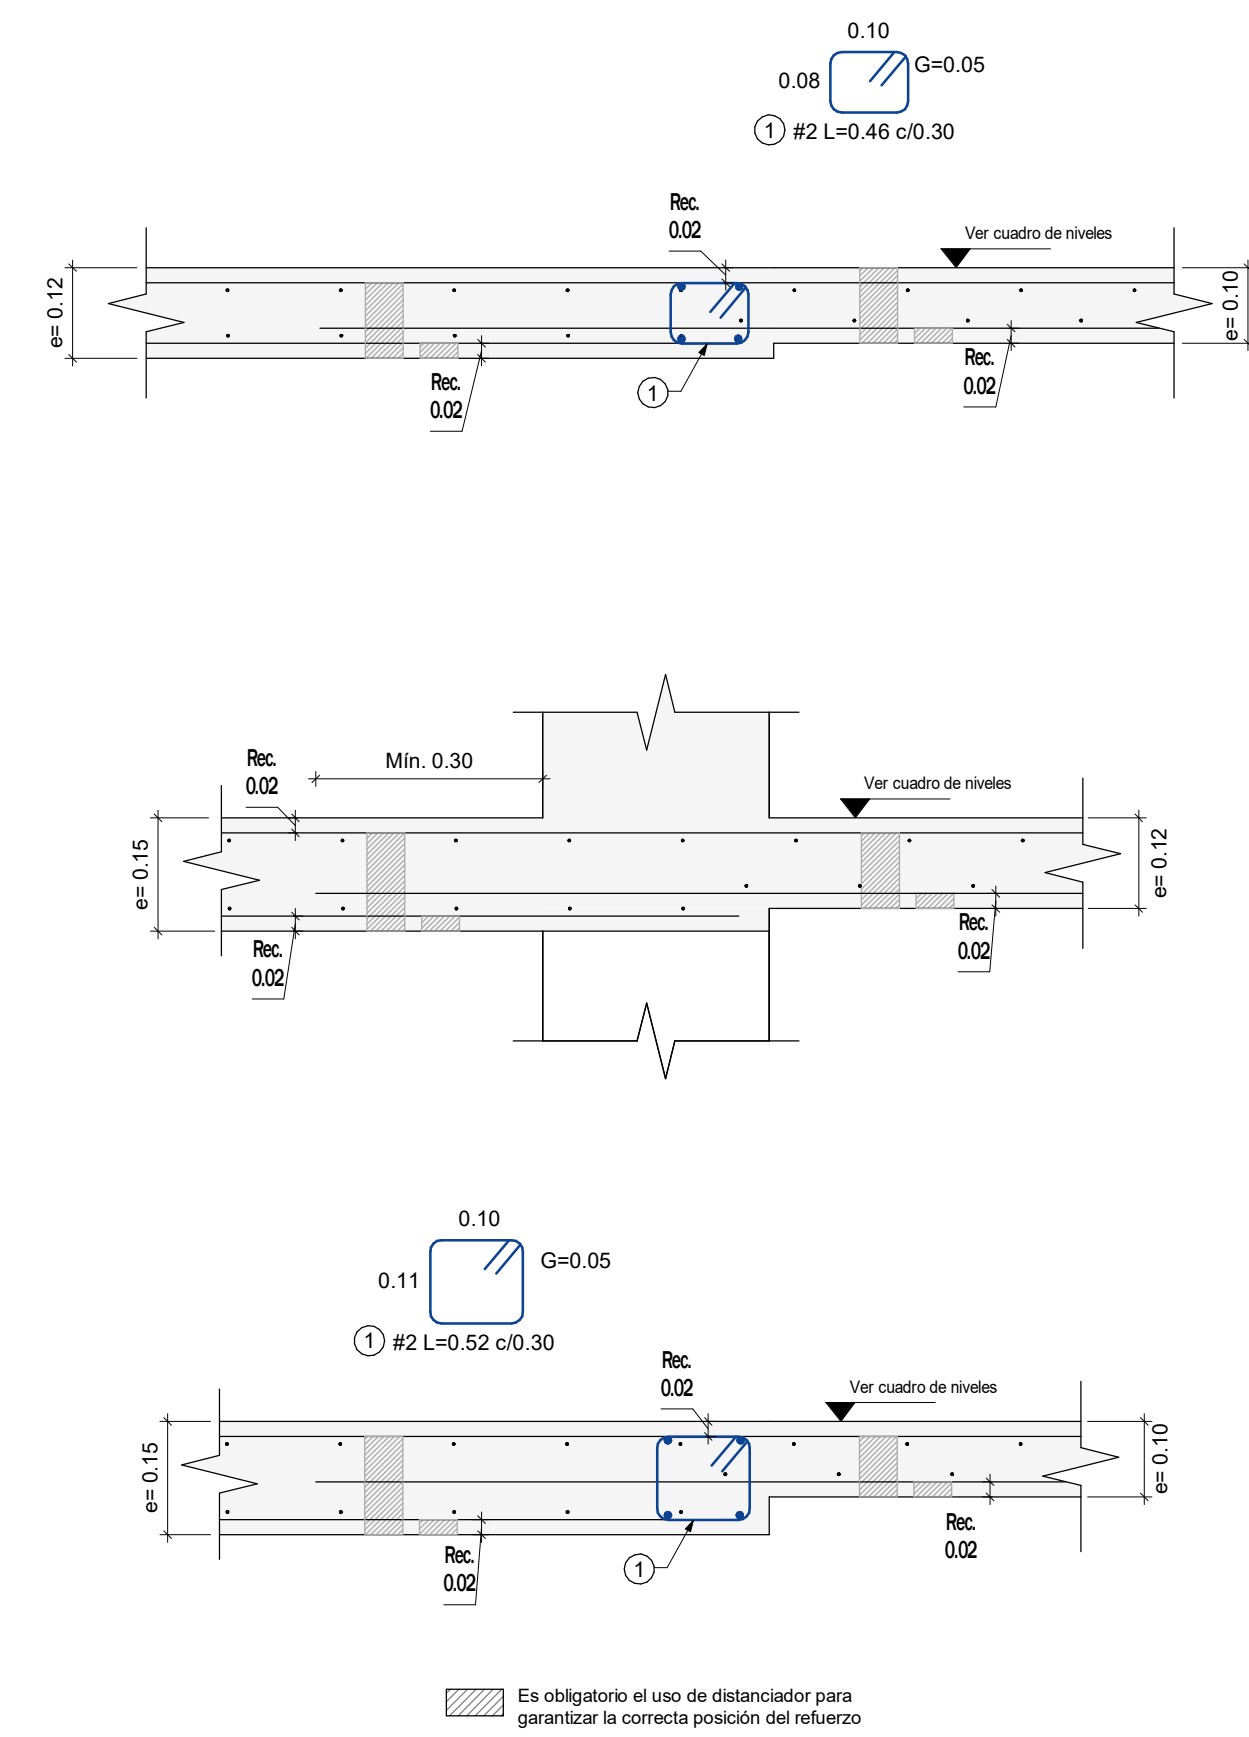

DETALLES TÍPICOS - CAMBIO DE SECCIÓN
Escala 1 : 10

- NOTAS:**
- Ver detalles generales en PL. N°01.02
 - Ver planta de localización e identificación de dinteles en PL N° 06.01
 - Ver despieces de dinteles en PL N° 10.00 a 10.04

CONCRETO:			
LOSAS Y DINTELES			
* DE PISO 1 A PISO 8	* DE PISO 9 A PISO 15	* DE PISO 16 A PISO 22	* DE PISO 23 A CUBIERTA ASCENSOR Y ESCALERAS
f_c=35 MPa	f_c=32 MPa	f_c=25 MPa	f_c=21 MPa
f_c=3500 kg/cm²	f_c=315 kg/cm²	f_c=245 kg/cm²	f_c=210 kg/cm²
f_c=5000 psi	f_c=4500 psi	f_c=3500 psi	f_c=3000 psi

CUADRO NIVELES PISO 3 A PISO 15	
PISO	NIVEL(N.E.)
PISO 3	5.30
PISO 4	7.95
PISO 5	10.60
PISO 6	13.25
PISO 7	15.90
PISO 8	18.55
PISO 9	21.20
PISO 10	23.85
PISO 11	26.50
PISO 12	29.15
PISO 13	31.80
PISO 14	34.45
PISO 15	37.10

GERENTE DE PROYECTO
ROBERTO AYCARDI F.
MAT. 2520257258 CND

INGENIERO
CARLOS ANDRÉS WILCHES C.

MODELADOR
DANIEL CASTELLANOS

MODIFICACIONES	FECHA
Emisión Inicial	28-02-2025
Ajuste borde de placa ejes D-6 y D-10	26-02-2026



LA SCALA

LA SCALA_EST_TOR-1

TORRE 1

CALLE 170 CON AV. BOYACA

PLANTA DE REFUERZO ADICIONAL PISO
TIPO 1 (PISO 3 A 15)

LA SCALA_EST_TOR-1_06.02_PT1-RADC

REVISOR ESTRUCTURAL
RAMÓN ANDRÉS ALVAREZ MANTILLA
MAT. 25202-346546 CND.

PLANO N° 06.02

VERSIÓN : 2