




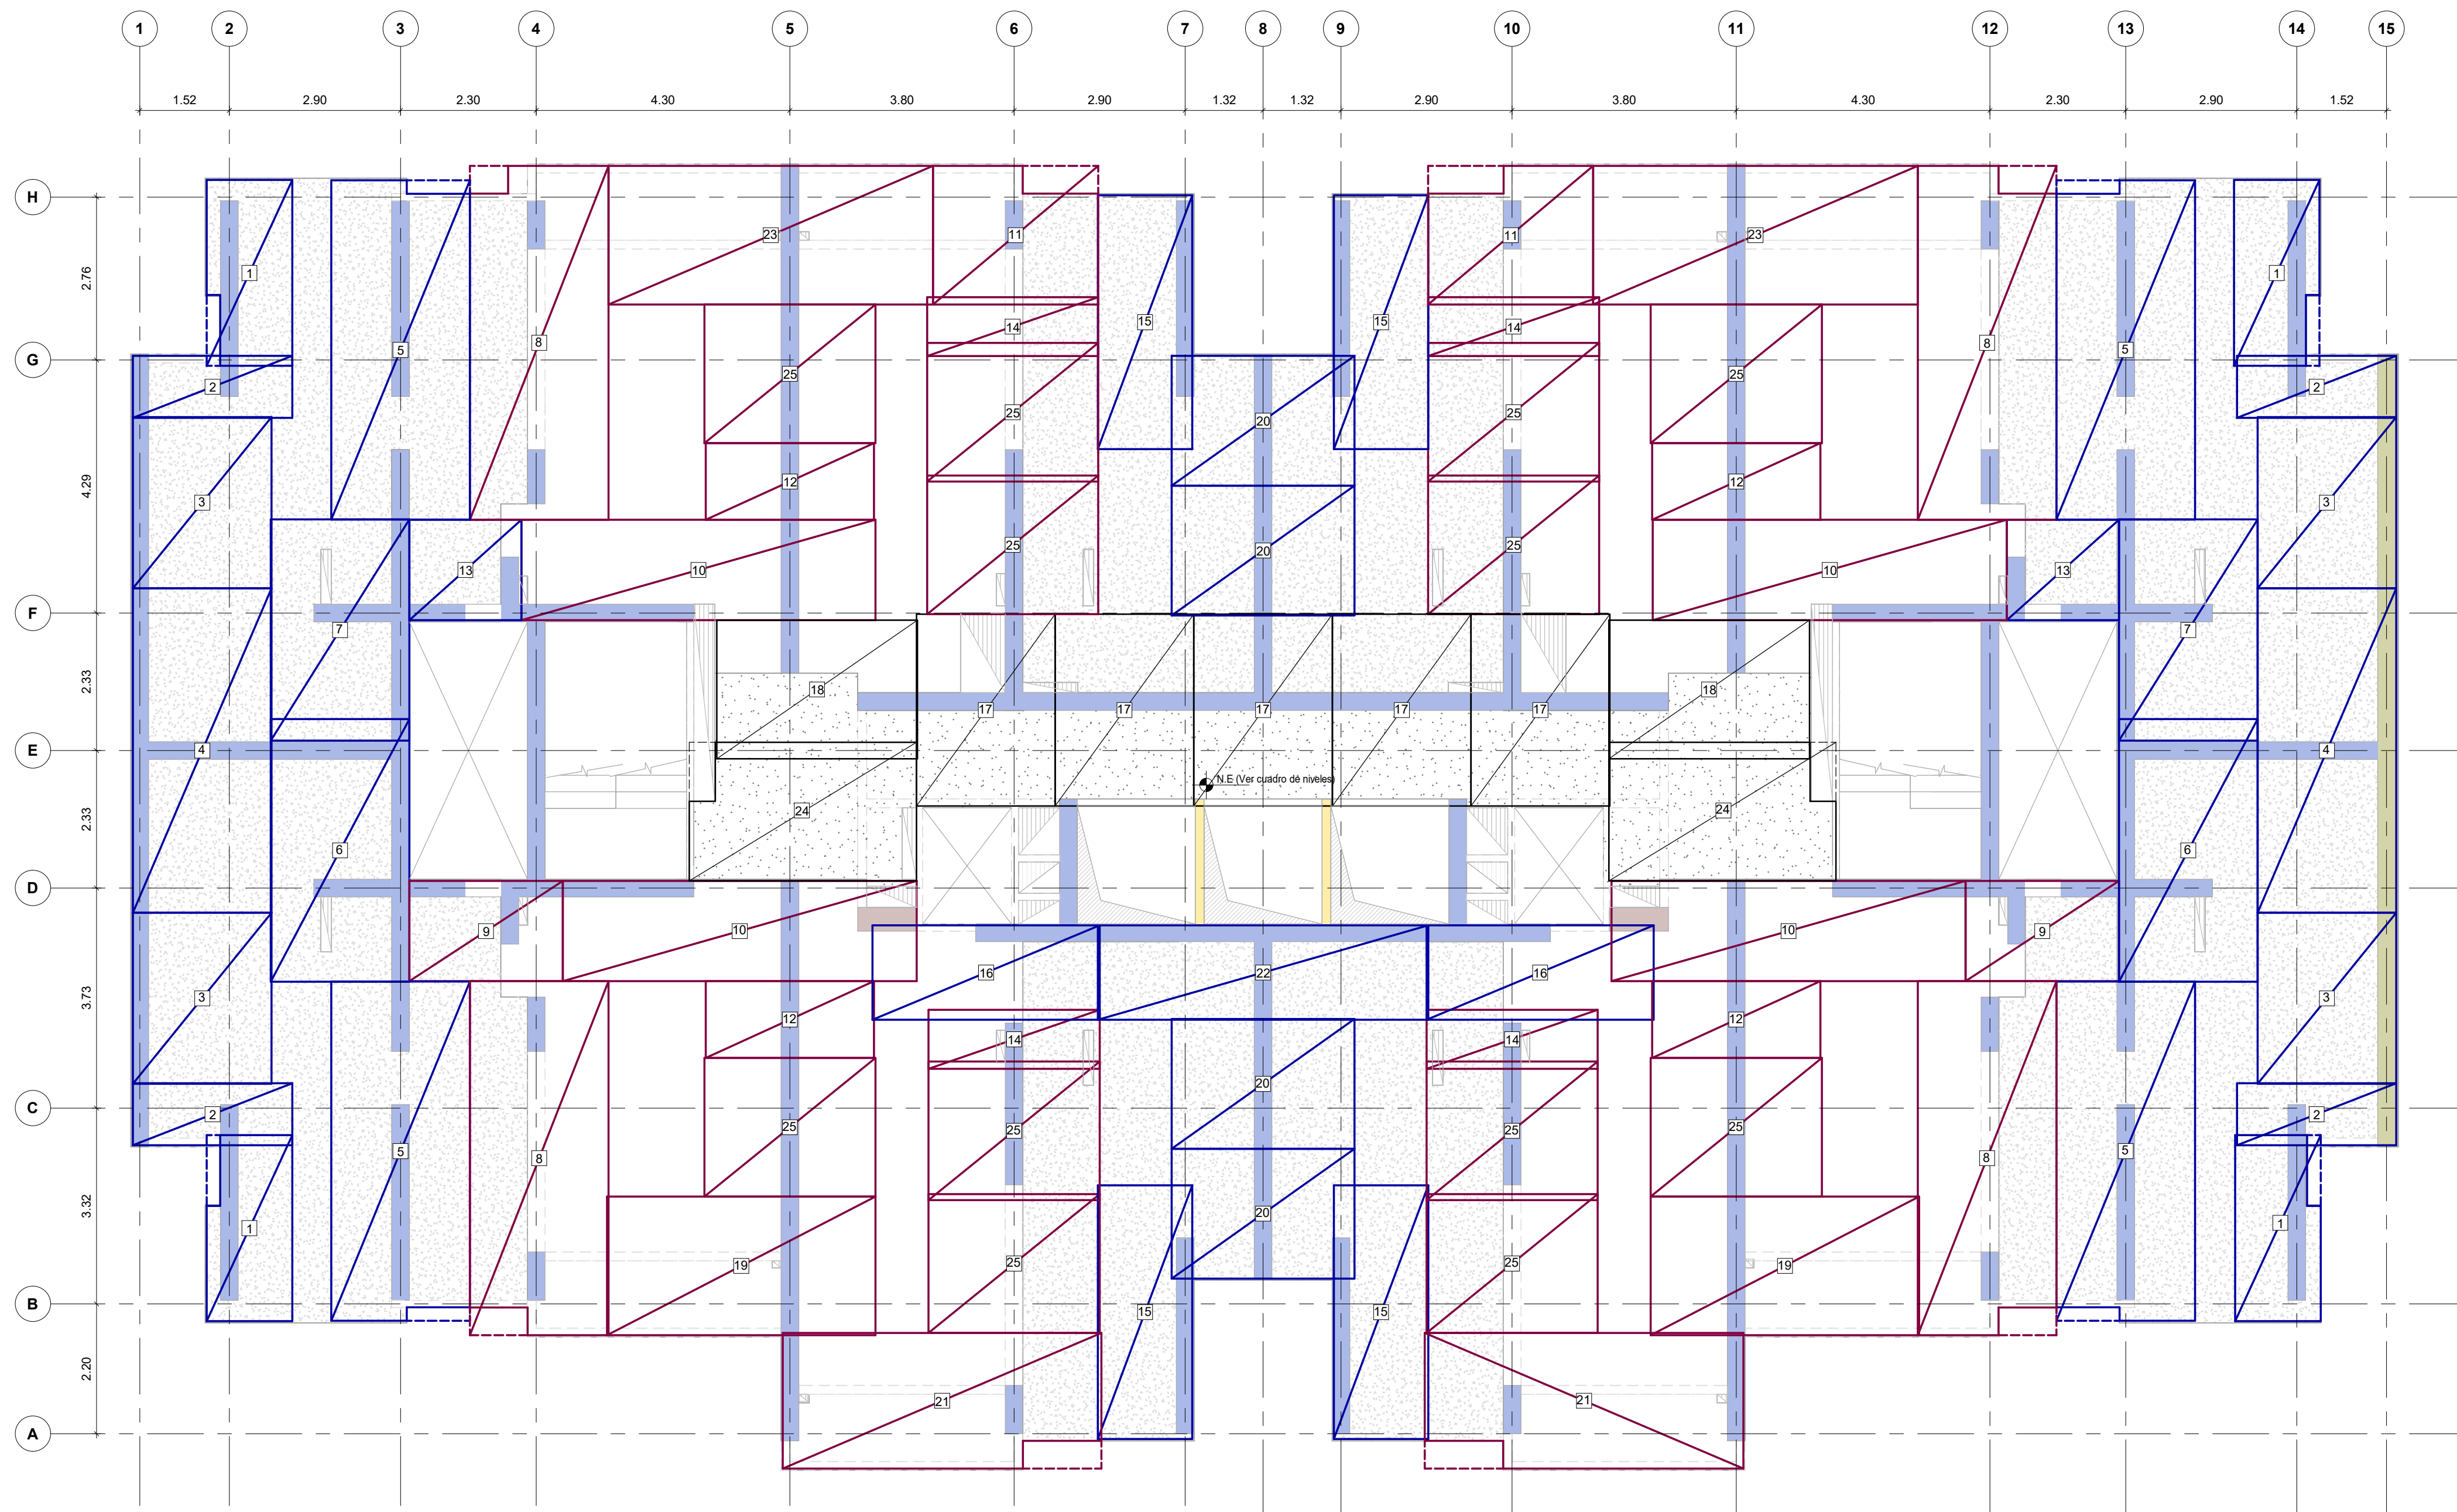


PLANTA DE REFUERZO SUPERIOR PISO TIPO 1 (PISO 3 A PISO 15)  
Escala 1 : 75

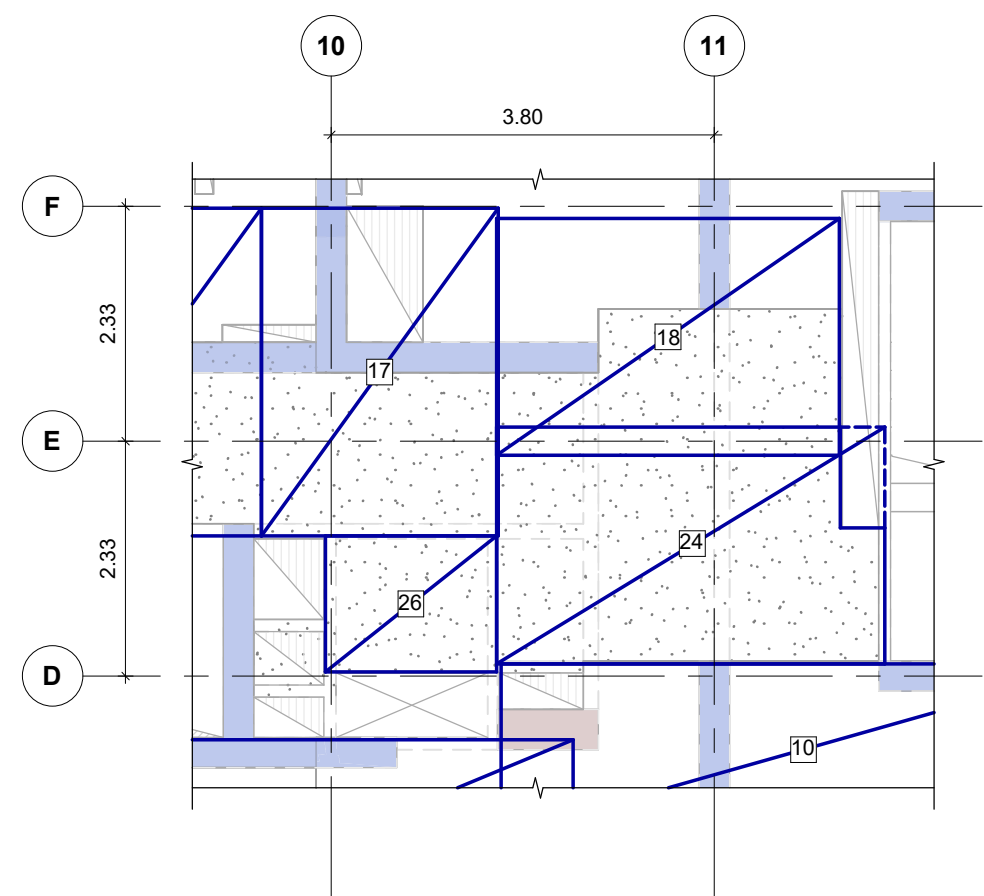

PLANTA DE REFUERZO SUPERIOR PISO 14 Y PISO 15  
Escala 1 : 75

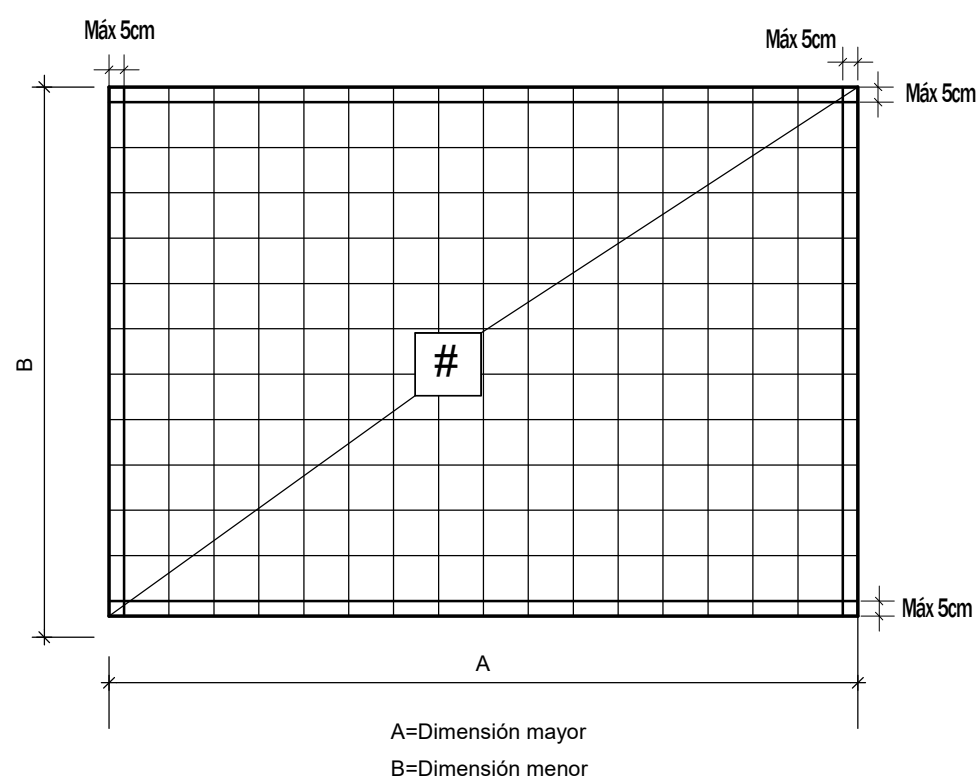

DETALLE CONVENCIÓN MALLAS  
Escala 1 : 25

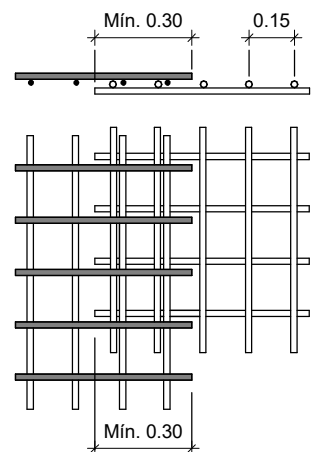

DETALLE TRASLAPO MALLAS  
Escala 1 : 25

| CUADRO DE MALLAS REFUERZO SUPERIOR TIPO 1 ( PISO 3 A PISO 15) |       |      |           |       |               |               |                      |           |
|---------------------------------------------------------------|-------|------|-----------|-------|---------------|---------------|----------------------|-----------|
| TIPO                                                          | A (m) | B(m) | ÁREA (m²) | CANT. | REFUERZO      |               | PESO / MALLA (Kg/m²) | PESO (Kg) |
|                                                               |       |      |           |       | REFUERZO A    | REFUERZO B    |                      |           |
| 1                                                             | 3.15  | 1.45 | 5 m²      | 4     | Ø6.0mm c/0.15 | Ø6.0mm c/0.15 | 2.993                | 55        |
| 2                                                             | 2.70  | 1.05 | 3 m²      | 4     | Ø6.0mm c/0.15 | Ø6.0mm c/0.15 | 2.993                | 34        |
| 3                                                             | 2.90  | 2.35 | 7 m²      | 4     | Ø6.0mm c/0.15 | Ø6.0mm c/0.15 | 2.993                | 82        |
| 4                                                             | 5.50  | 2.35 | 13 m²     | 2     | Ø6.0mm c/0.15 | Ø6.0mm c/0.15 | 2.993                | 77        |
| 5                                                             | 5.75  | 2.35 | 14 m²     | 4     | Ø6.0mm c/0.15 | Ø6.0mm c/0.15 | 3.518                | 190       |
| 6                                                             | 4.45  | 2.35 | 10 m²     | 2     | Ø6.0mm c/0.15 | Ø6.0mm c/0.15 | 2.993                | 63        |
| 7                                                             | 3.75  | 2.35 | 9 m²      | 2     | Ø6.0mm c/0.15 | Ø6.0mm c/0.15 | 2.993                | 53        |
| 8                                                             | 6.00  | 2.35 | 14 m²     | 4     | Ø6.5mm c/0.15 | Ø6.5mm c/0.15 | 3.518                | 198       |
| 9                                                             | 2.60  | 1.70 | 4 m²      | 2     | Ø6.5mm c/0.15 | Ø6.5mm c/0.15 | 3.518                | 31        |
| 10                                                            | 6.00  | 1.70 | 10 m²     | 4     | Ø6.5mm c/0.15 | Ø6.5mm c/0.15 | 3.518                | 144       |
| 11                                                            | 2.80  | 2.35 | 7 m²      | 2     | Ø6.5mm c/0.15 | Ø6.5mm c/0.15 | 3.518                | 46        |
| 12                                                            | 2.85  | 1.30 | 4 m²      | 4     | Ø6.5mm c/0.15 | Ø6.5mm c/0.15 | 3.518                | 52        |
| 13                                                            | 1.90  | 1.70 | 3 m²      | 2     | Ø6.5mm c/0.15 | Ø6.5mm c/0.15 | 2.993                | 19        |
| 14                                                            | 2.90  | 1.00 | 3 m²      | 4     | Ø6.5mm c/0.15 | Ø6.5mm c/0.15 | 3.518                | 41        |
| 15                                                            | 4.30  | 1.60 | 7 m²      | 4     | Ø6.0mm c/0.15 | Ø6.0mm c/0.15 | 2.993                | 82        |
| 16                                                            | 3.85  | 1.60 | 6 m²      | 2     | Ø6.0mm c/0.15 | Ø6.0mm c/0.15 | 2.993                | 37        |
| 17                                                            | 3.25  | 2.35 | 8 m²      | 5     | Ø7.5mm c/0.15 | Ø7.5mm c/0.15 | 4.674                | 178       |
| 18                                                            | 3.40  | 2.35 | 8 m²      | 2     | Ø7.5mm c/0.15 | Ø7.5mm c/0.15 | 4.674                | 75        |
| 19                                                            | 4.55  | 2.35 | 11 m²     | 2     | Ø6.5mm c/0.15 | Ø6.5mm c/0.15 | 3.518                | 75        |
| 20                                                            | 3.10  | 2.20 | 7 m²      | 4     | Ø6.0mm c/0.15 | Ø6.0mm c/0.15 | 2.993                | 82        |
| 21                                                            | 5.40  | 2.30 | 12 m²     | 2     | Ø6.5mm c/0.15 | Ø6.5mm c/0.15 | 3.518                | 87        |
| 22                                                            | 5.60  | 1.60 | 9 m²      | 1     | Ø6.0mm c/0.15 | Ø6.0mm c/0.15 | 2.993                | 27        |
| 23                                                            | 5.50  | 2.35 | 13 m²     | 2     | Ø6.5mm c/0.15 | Ø6.5mm c/0.15 | 3.518                | 91        |
| 24                                                            | 3.85  | 2.35 | 9 m²      | 2     | Ø7.5mm c/0.15 | Ø7.5mm c/0.15 | 2.993                | 54        |
| 25                                                            | 2.90  | 2.35 | 7 m²      | 12    | Ø6.5mm c/0.15 | Ø6.5mm c/0.15 | 3.518                | 288       |
| 26                                                            | 1.70  | 1.35 | 2 m²      | 1     | Ø6.0mm c/0.15 | Ø6.0mm c/0.15 | 2.993                | 7         |
| TOTAL : 83                                                    |       |      |           | 83    |               |               |                      | 2168      |

**NOTAS:**  
1. Ver detalles generales en el PL. N° 01.02  
2. Ver planta de refuerzo adicional en PL. N° 06.02  
3. Ver planta de refuerzo inferior en PL. N° 06.03  
4. Las dimensiones de las mallas deben ser verificadas por el constructor.

**CONCRETO:**  
LOSAS Y DÍNTILES  
\* DE PISO 1 A PISO 8  
\* DE PISO 9 A PISO 15  
\* DE PISO 16 A PISO 22  
\* DE PISO 23 A CUBIERTA ASCENSOR Y ESCALERAS  
f'c=35 MPa f'c=32 MPa f'c=25 MPa f'c=21 MPa  
f'c=350 kg/cm² f'c=315 kg/cm² f'c=245 kg/cm² f'c=210 kg/cm²  
f'c=5000 psi f'c=4500 psi f'c=3500 psi f'c=3000 psi

| CUADRO NIVELES PISO 3 A PISO 15 |            |
|---------------------------------|------------|
| PISO                            | NIVEL(NE.) |
| PISO 3                          | 5.30       |
| PISO 4                          | 7.95       |
| PISO 5                          | 10.60      |
| PISO 6                          | 13.25      |
| PISO 7                          | 15.90      |
| PISO 8                          | 18.55      |
| PISO 9                          | 21.20      |
| PISO 10                         | 23.85      |
| PISO 11                         | 26.50      |
| PISO 12                         | 29.15      |
| PISO 13                         | 31.80      |
| PISO 14                         | 34.45      |
| PISO 15                         | 37.10      |

**CONVENCIÓN**  
Indica Malla  
Indica cortar Malla  
Indica N° de Malla

**CONVENCIÓN**  
Indica dinteles  
Indica placa e=0.10  
Indica placa e=0.12  
Indica placa e=0.15  
Indica muros en concreto e=0.15  
Indica muros en concreto e=0.30  
Indica muros en concreto e=0.35  
Indica muros en concreto e=0.40

PLANO N° 06.04

VERSIÓN : 2



GERENTE DE PROYECTO  
ROBERTO AYCARDI F.  
MAT. 2520257258 CND

INGENIERO  
CARLOS ANDRÉS WILCHES C.

MODELADOR  
DANIEL CASTELLANOS

| MODIFICACIONES                                                        | FECHA      |
|-----------------------------------------------------------------------|------------|
| Emisión Inicial                                                       | 28-02-2025 |
| Ajuste borde de placa ejes D-6 y D-10 y se actualiza cuadro de mallas | 26-02-2026 |
|                                                                       |            |
|                                                                       |            |
|                                                                       |            |



LA SCALA

LA SCALA\_EST\_TOR-1

TORRE 1

CALLE 170 CON AV. BOYACA

PLANTA DE REFUERZO SUPERIOR PISO TIPO 1 (PISO 3 A PISO 15)

LA SCALA\_EST\_TOR-1\_06.04\_PT1-RSUP

REVISOR ESTRUCTURAL  
RAMÓN ANDRÉS ALVAREZ MANTILLA  
MAT. 25202-346546 CND.

PLANO N°

VERSIÓN :

06.04

2