


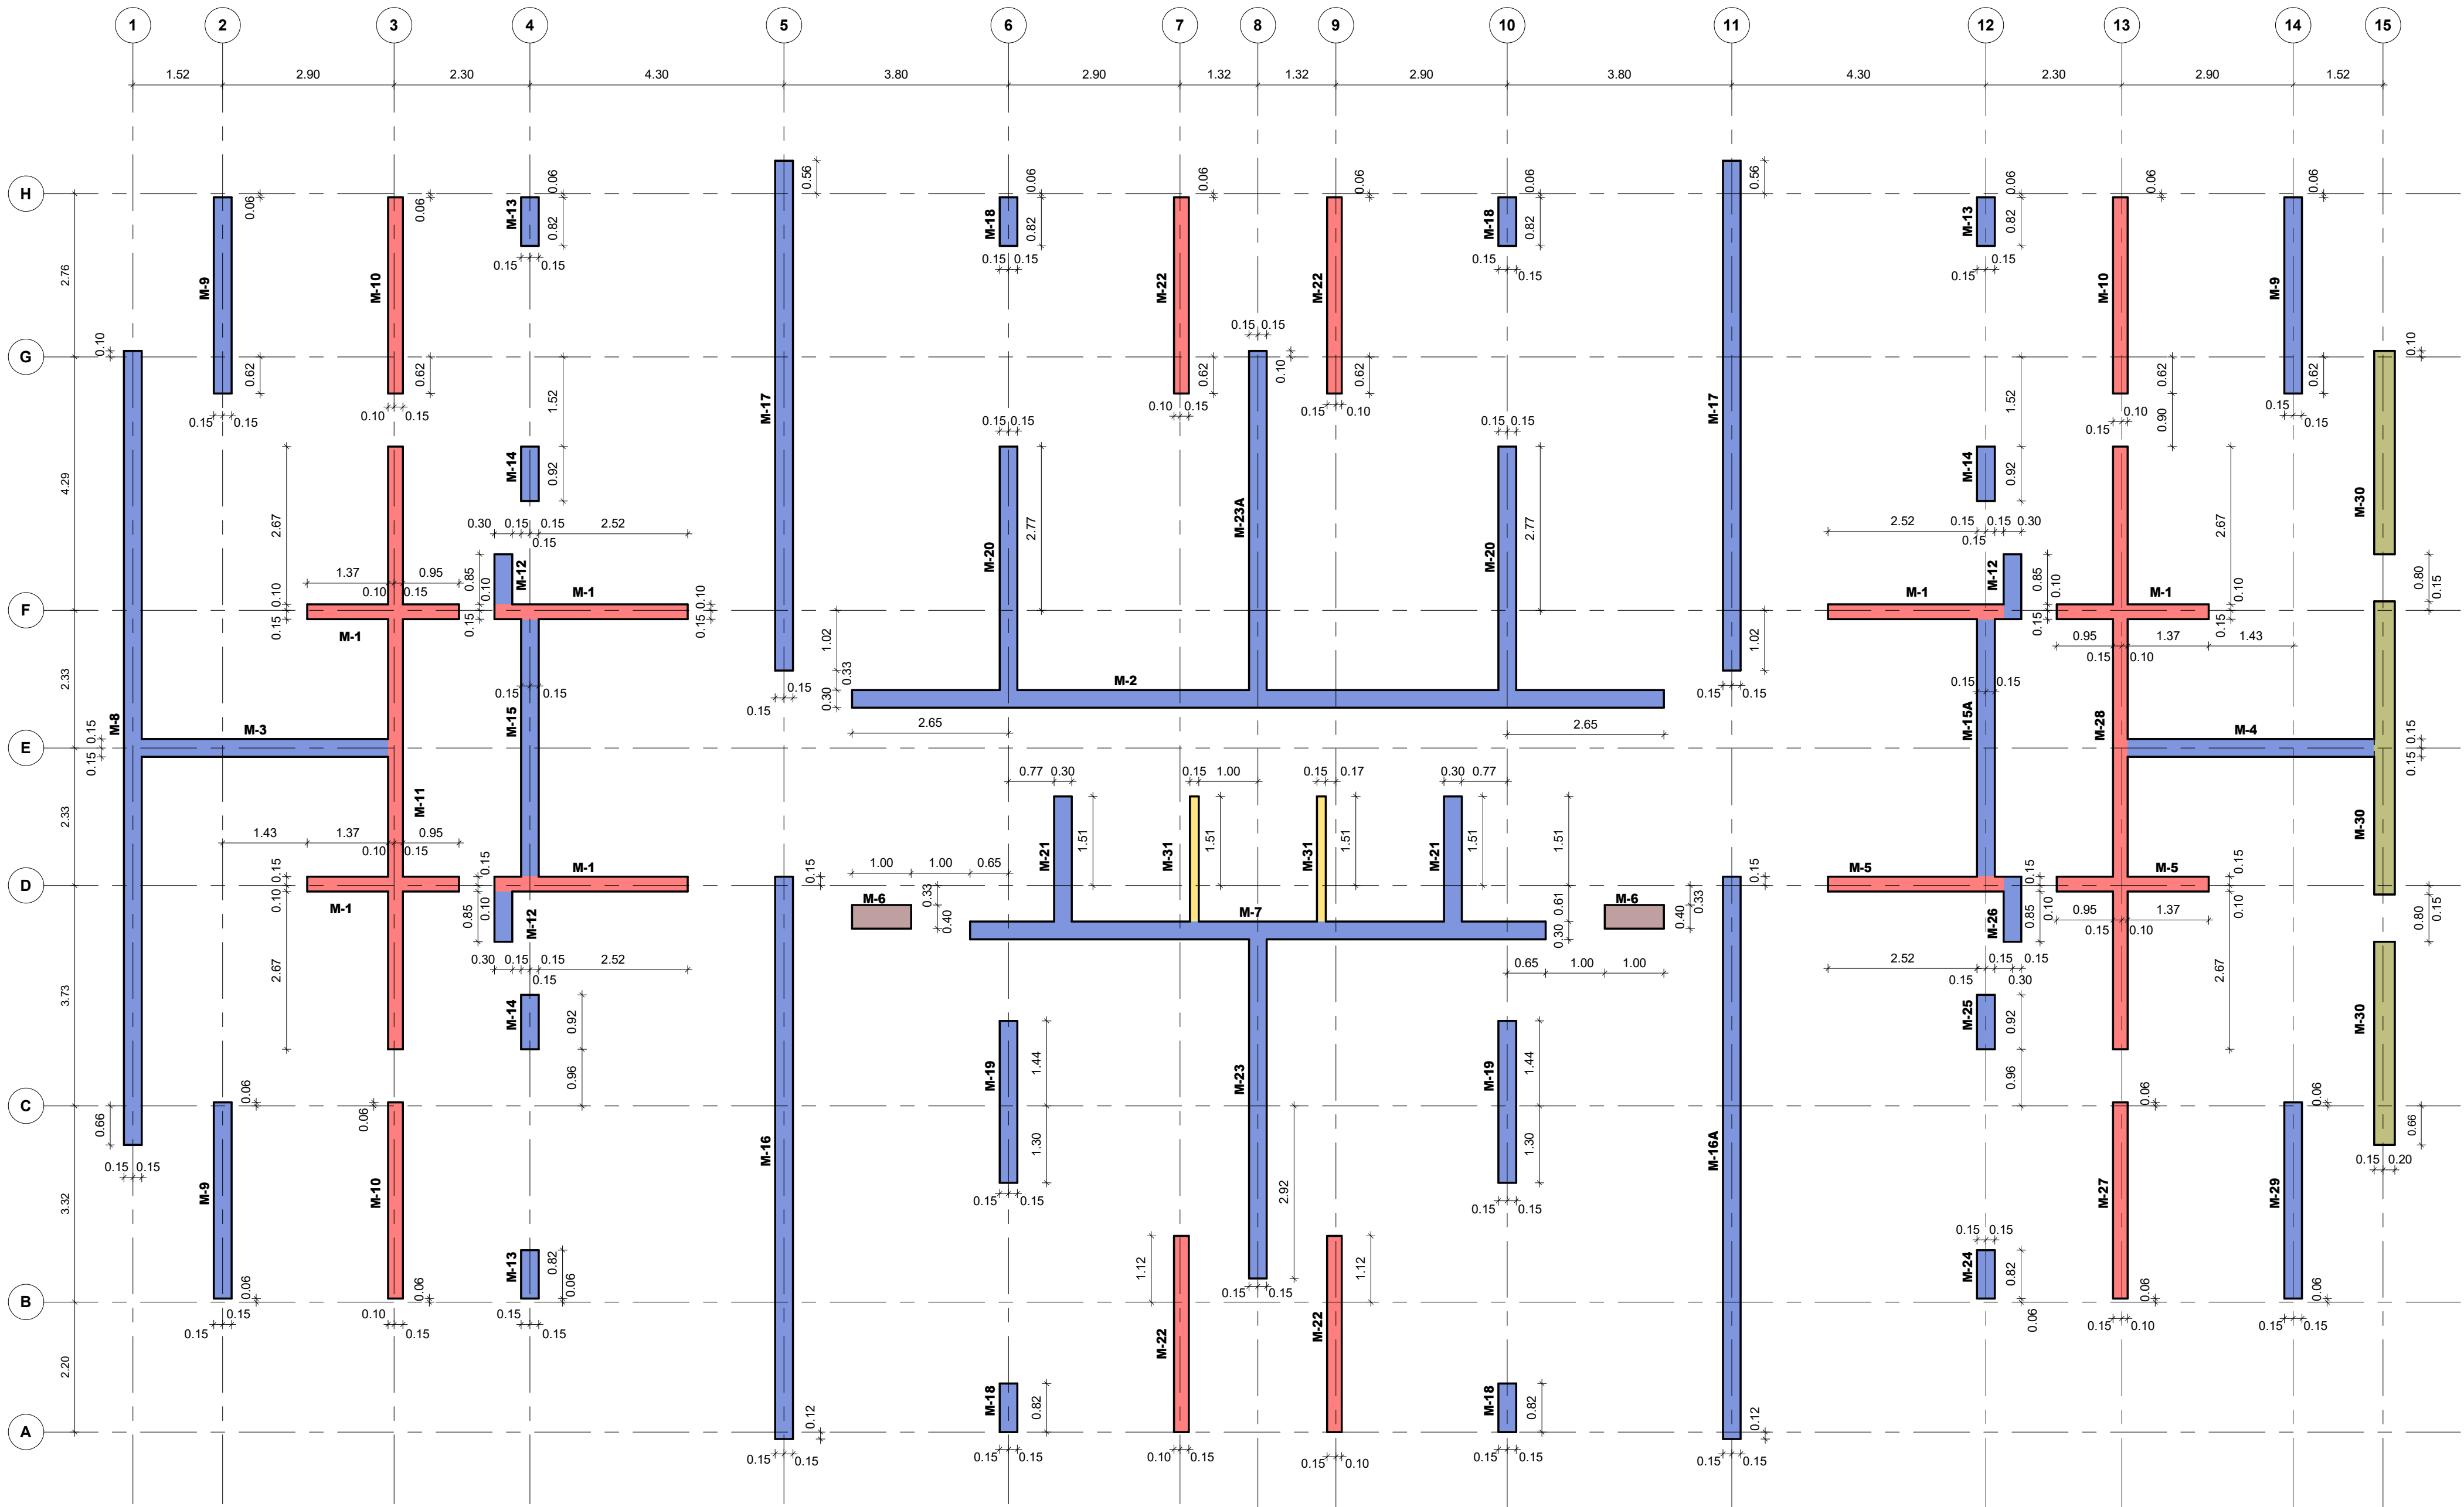

PLANTA LOCALIZACIÓN DE MUROS PISO TIPO 2 (PISO 15 A PISO 21)
Escala 1 : 75

CUADRO NIVELES PISO 16 A PISO 22	
PISO	NIVEL(NE.)
PISO 16	39.75
PISO 17	42.40
PISO 18	45.05
PISO 19	47.70
PISO 20	50.35
PISO 21	53.00
PISO 22	55.65

CONCRETO: MUROS			
* DE CIMENTACIÓN A PISO 8	* DE PISO 8 A PISO 15	* DE PISO 15 A PISO 22	* DE PISO 22 A CUBIERTA ASCENSOR Y ESCALERAS
f'c=49 MPa	f'c=42 MPa	f'c=35 MPa	f'c=28 MPa
f'c=490 kg/cm²	f'c=420 kg/cm²	f'c=350 kg/cm²	f'c=280 kg/cm²
f'c=7000 psi	f'c=6000 psi	f'c=5000 psi	f'c=4000 psi

CONVENCIONES	
M-#	Indica N° de Muro
[Yellow Box]	Indica muro e=0.15
[Red Box]	Indica muro e=0.25
[Blue Box]	Indica muro e=0.30
[Green Box]	Indica muro e=0.35
[Brown Box]	Indica muro e=0.40
NOTAS	
1. Ver detalles generales en PL. N°01.02.	
2. Ver desplieces de muros en PL. N° 11.00 a PL. N°11.21	
3. Ver detalles de muros en PL. N° 11.22	

MODIFICACIONES		FECHA
Emisión Inicial		28-02-2025
Se actualiza longitud de muro M-19		04-11-2025



LA SCALA

LA SCALA_EST_TOR-1

TORRE 1

CALLE 170 CON AV. BOYACA

PLANTA LOCALIZACIÓN DE MUROS PISO TIPO 2 (PISO 15 A PISO 21)

LA SCALA_EST_TOR-1_07.00_LCM-PT2