


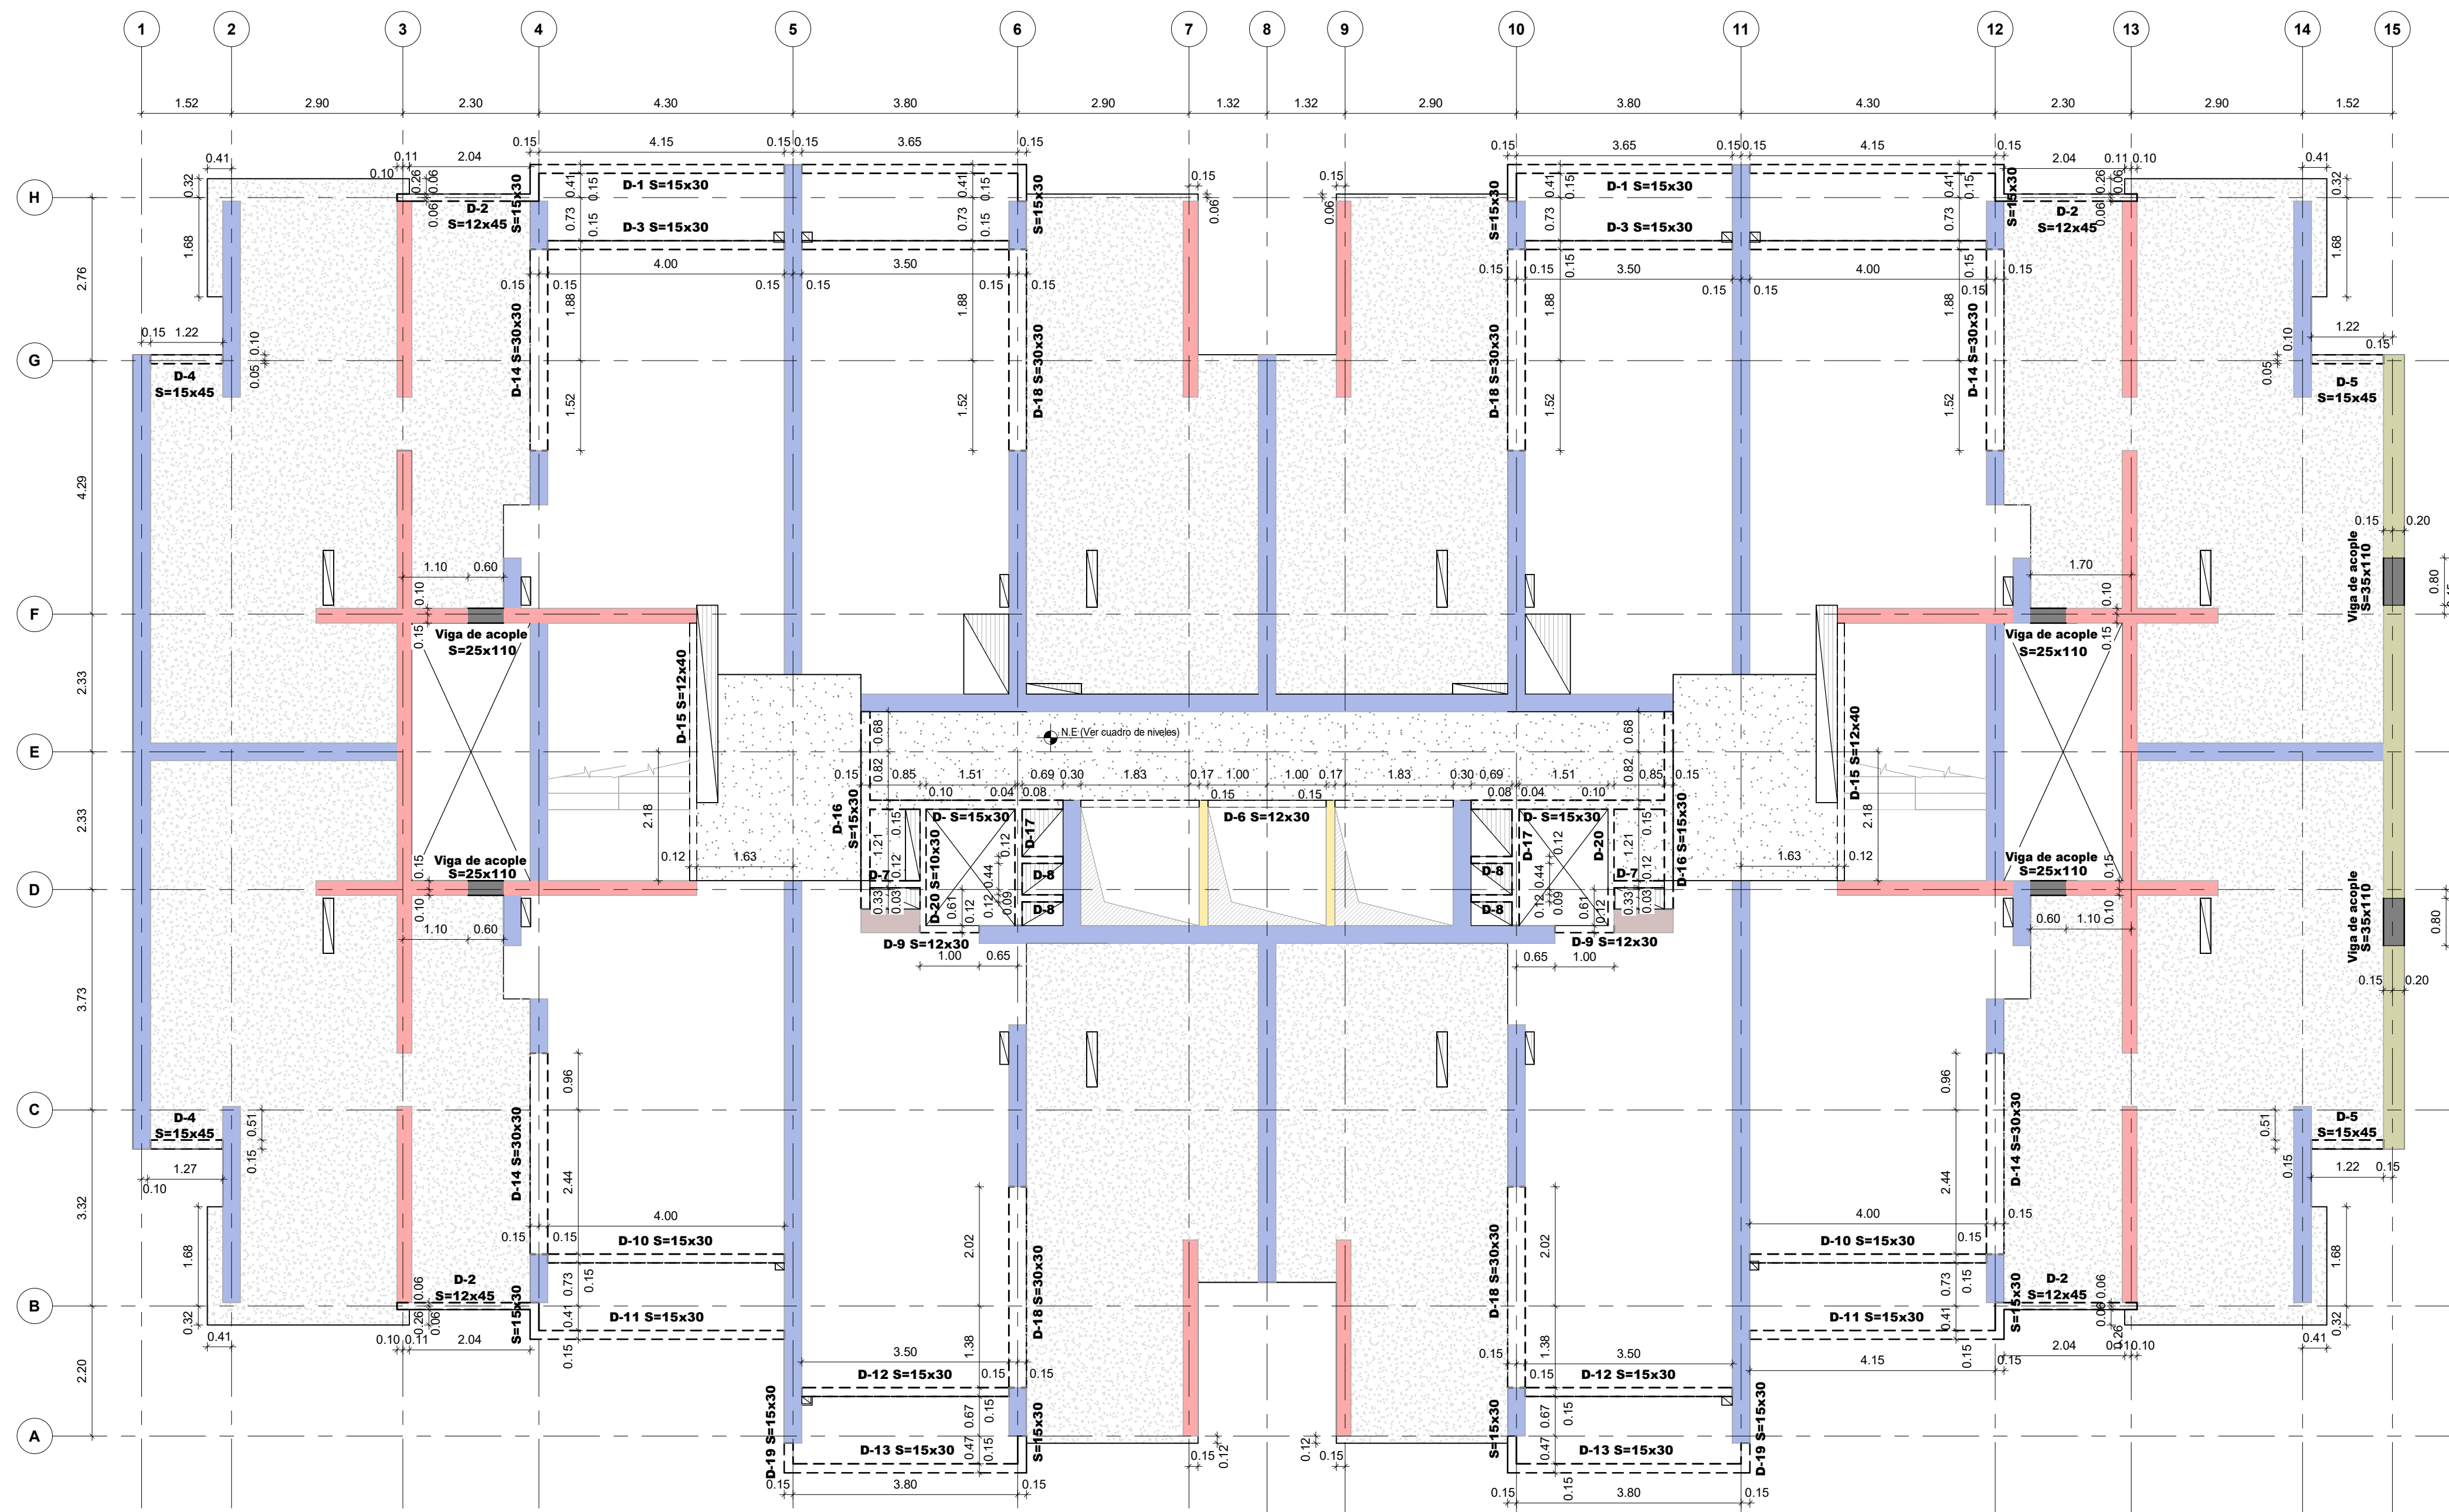

PLANTA LOCALIZACIÓN DE DINTELES PISO TIPO 2 (PISO 16 A PISO 22)
Escala 1 : 75

CONCRETO: VIGAS DE ACOPLE			
* DE PISO 2 A PISO 8	* DE PISO 8 A PISO 15	* DE PISO 15 A PISO 22	* DE PISO 22 A PISO 28
f_c=49 MPa	f_c=42 MPa	f_c=35 MPa	f_c=28 MPa
f_c=490 kg/cm²	f_c=420 kg/cm²	f_c=350 kg/cm²	f_c=280 kg/cm²
f_c=7000 psi	f_c=6000 psi	f_c=5000 psi	f_c=4000 psi

CONCRETO: LOSAS Y DINTELES			
* DE PISO 1 A PISO 8	* DE PISO 9 A PISO 15	* DE PISO 16 A PISO 22	* DE PISO 23 A CUBIERTA ASCENSOR Y ESCALERAS
f_c=35 MPa	f_c=32 MPa	f_c=25 MPa	f_c=21 MPa
f_c=350 kg/cm²	f_c=315 kg/cm²	f_c=245 kg/cm²	f_c=210 kg/cm²
f_c=5000 psi	f_c=4500 psi	f_c=3500 psi	f_c=3000 psi

CUADRO NIVELES PISO 16 A PISO 22	
PISO	NIVEL(ME.)
PISO 16	38.75
PISO 17	42.40
PISO 18	46.05
PISO 19	49.70
PISO 20	53.35
PISO 21	57.00
PISO 22	60.65

CONVENCIONES	
	Indica dinteles
	Indica N° de dintel
	Indica Vigas de acople
	Indica muro e=0.15
	Indica muro e=0.25
	Indica muro e=0.30
	Indica muro e=0.35
	Indica muro e=0.40
	Indica placa e=0.10
	Indica placa e=0.12
	Indica placa e=0.15
NOTAS	
1. Ver detalles generales en PL. N°01.02	
2. Ver despieces de dinteles en PL N° 10.00 a 10.04	
3. ver detalle viga de acople en PL N° 11.01,11.05,11.20	

PLANO N° 07.01

VERSIÓN : 2



GERENTE DE PROYECTO
ROBERTO AYCARDI F.
MAT. 2520257258 CND

INGENIERO
CARLOS ANDRÉS WILCHES C.

MODELADOR
DANIEL CASTELLANOS

MODIFICACIONES	FECHA
Emisión Inicial	28-02-2025
Ajuste borde de placa ejes D-6 y D-10	26-02-2026



LA SCALA

LA SCALA_EST_TOR-1

TORRE 1

CALLE 170 CON AV. BOYACA

PLANTA LOCALIZACIÓN E IDENTIFICACIÓN
DE DINTELES PISO TIPO 2 (PISO 16 A PISO
22)

LA SCALA_EST_TOR-1_07.01_LDINT-PT2

REVISOR ESTRUCTURAL
RAMÓN ANDRÉS ALVAREZ MANTILLA
MAT. 25202-346546 CND.

PLANO N°

07.01

VERSIÓN :

2