




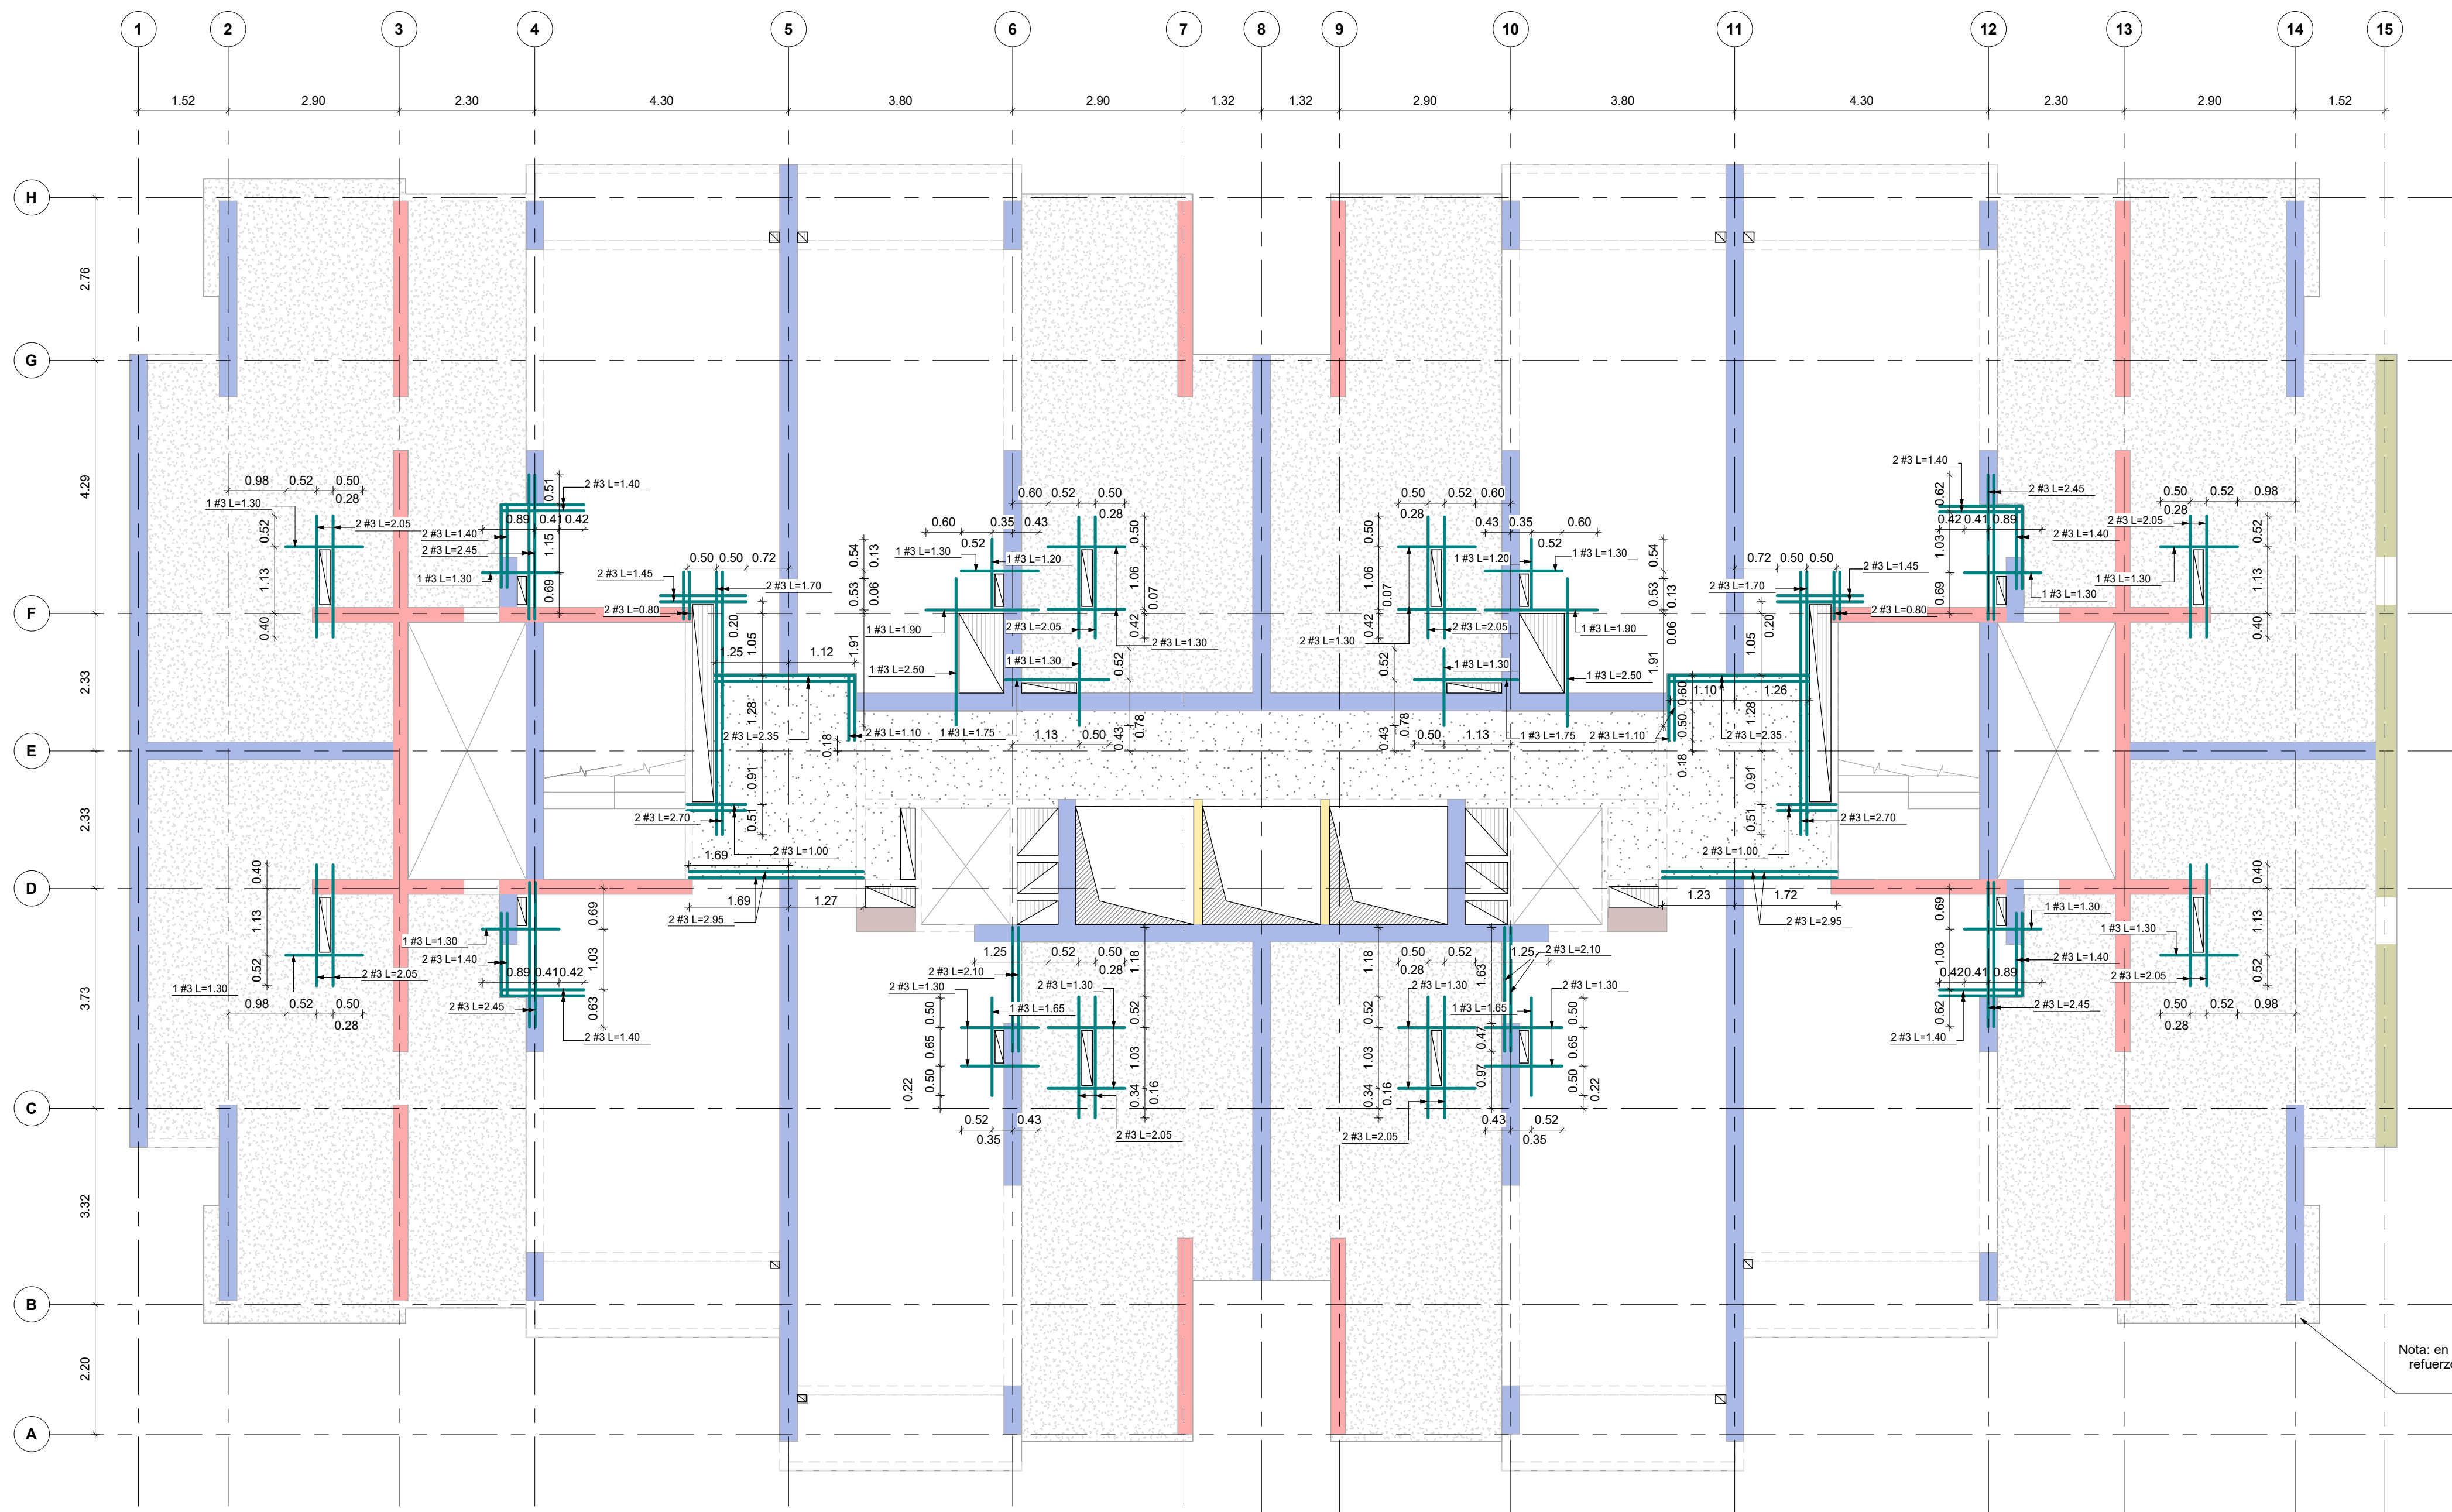


PLANTA DE REFUERZO ADICIONAL PISO TIPO 2 (PISO 16 A PISO 22)
Escala 1 : 75

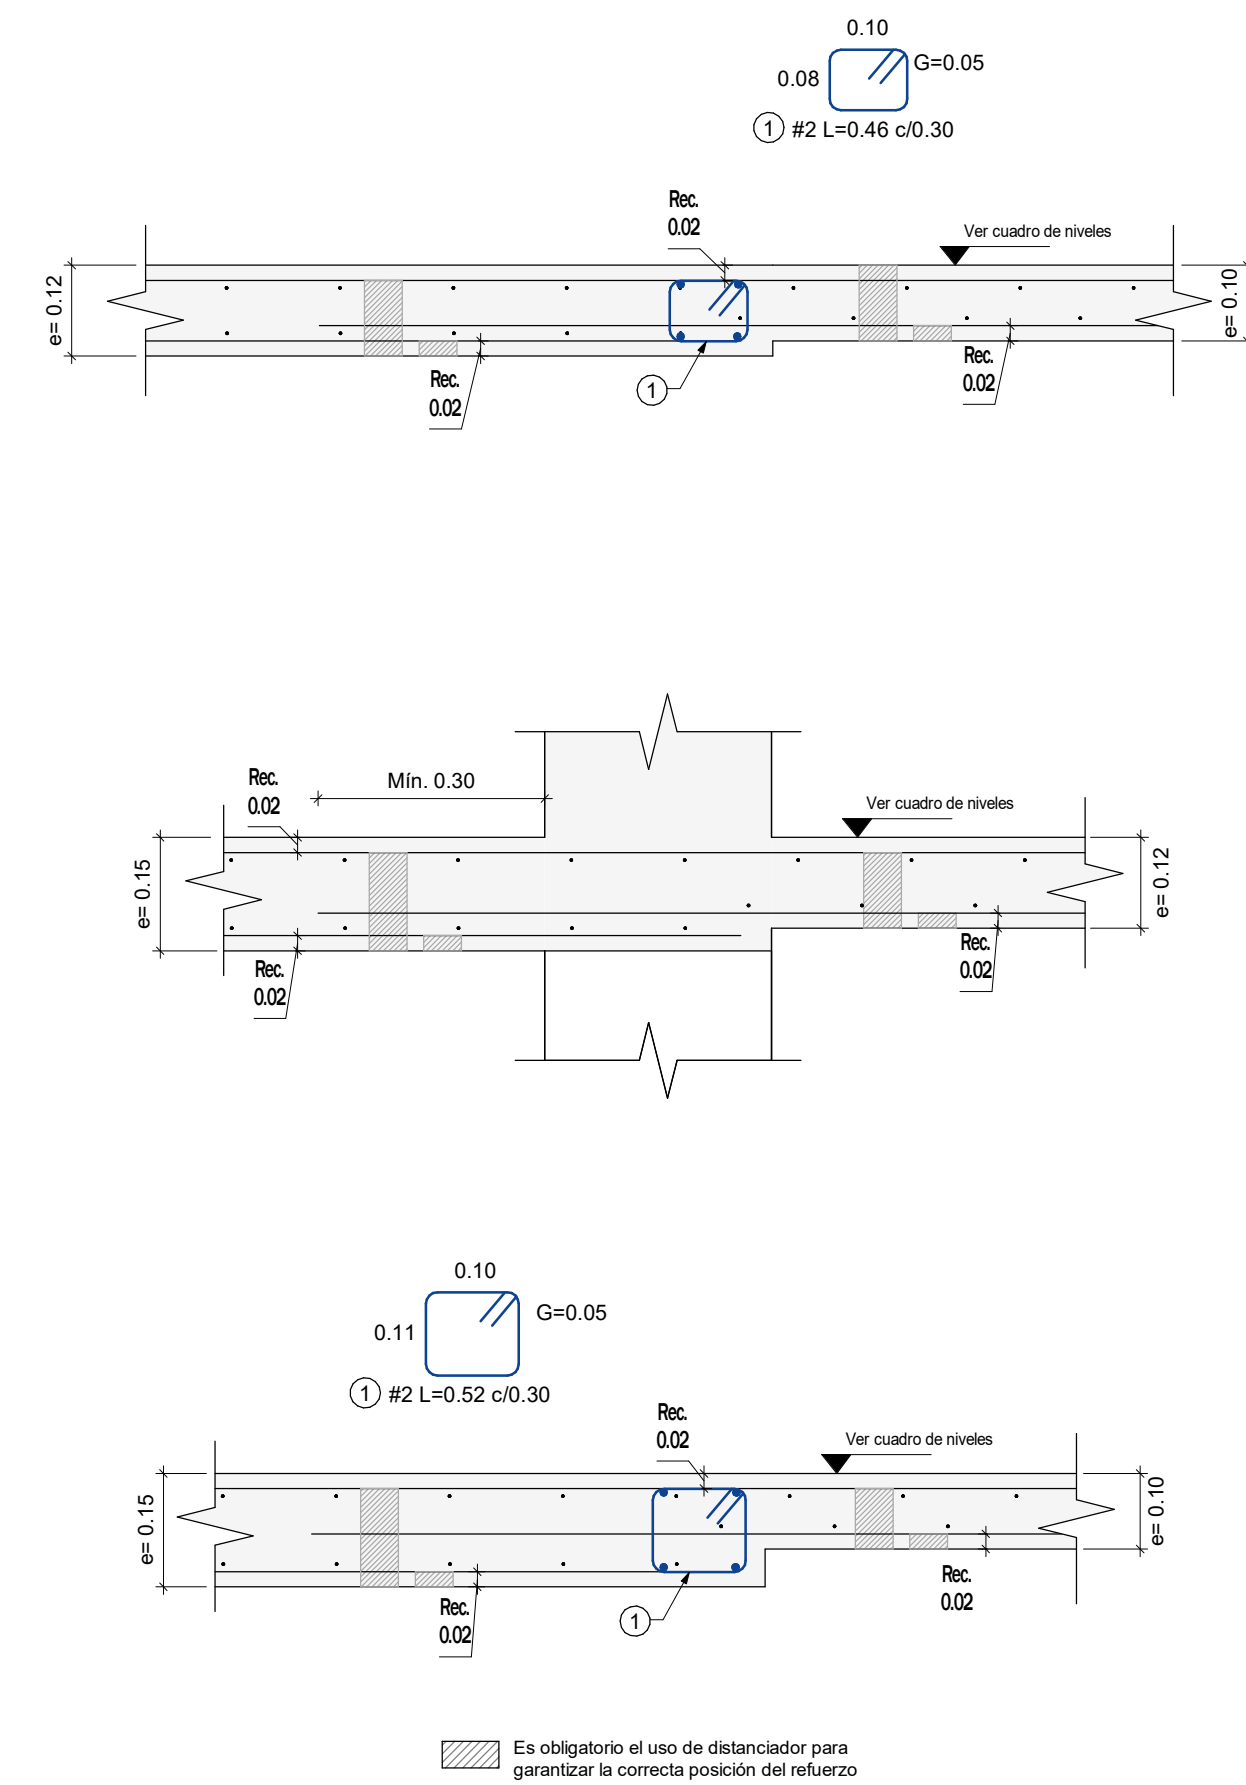


DETALLES TÍPICOS - CAMBIO DE SECCIÓN
Escala 1 : 10

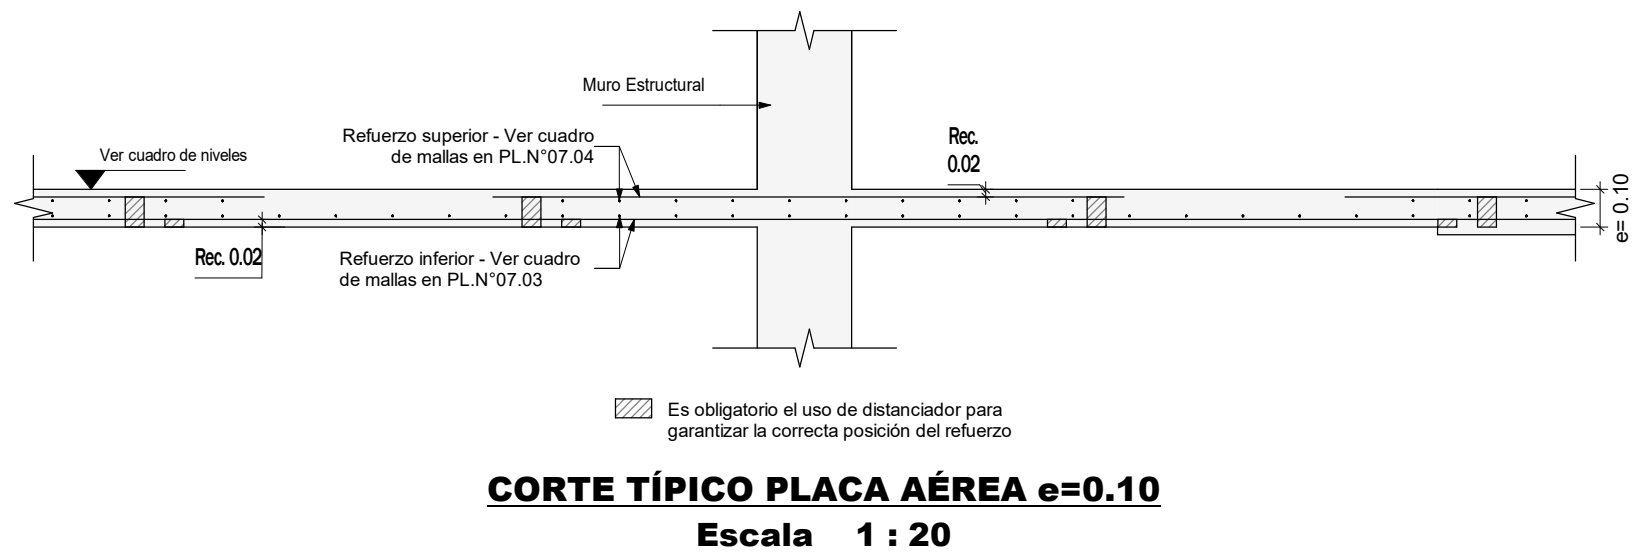


CORTE TÍPICO PLACA AÉREA e=0.10
Escala 1 : 20

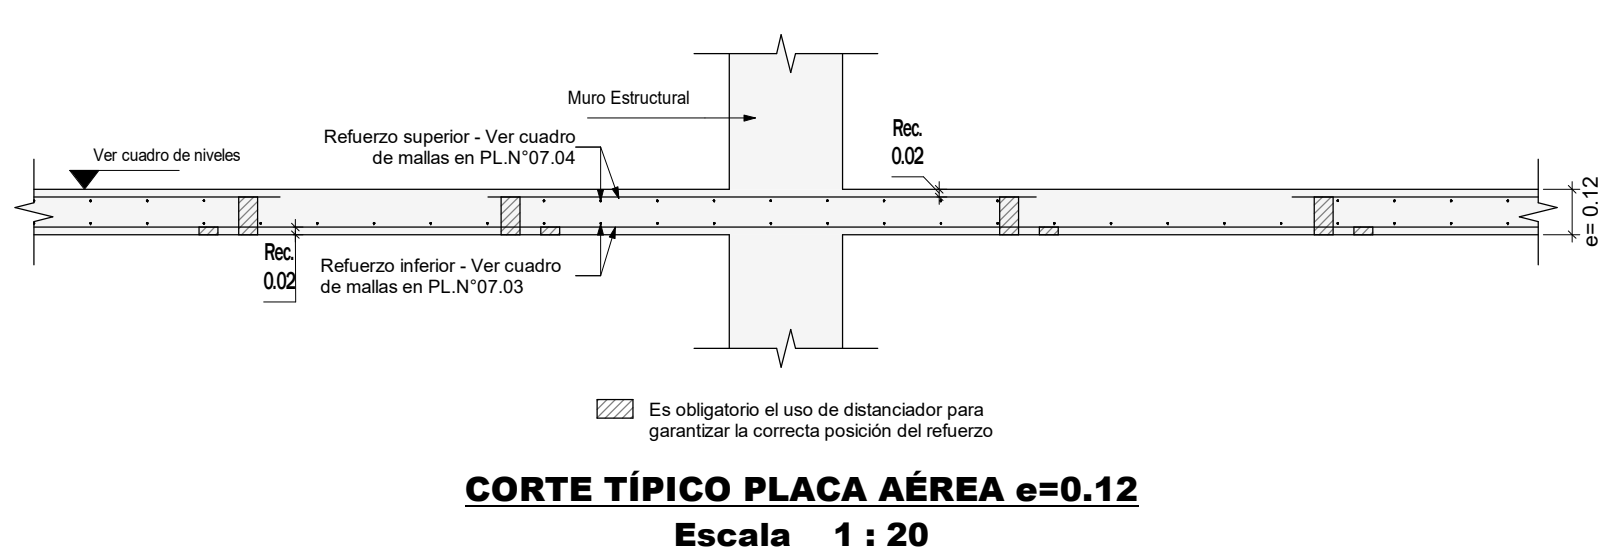


CORTE TÍPICO PLACA AÉREA e=0.12
Escala 1 : 20

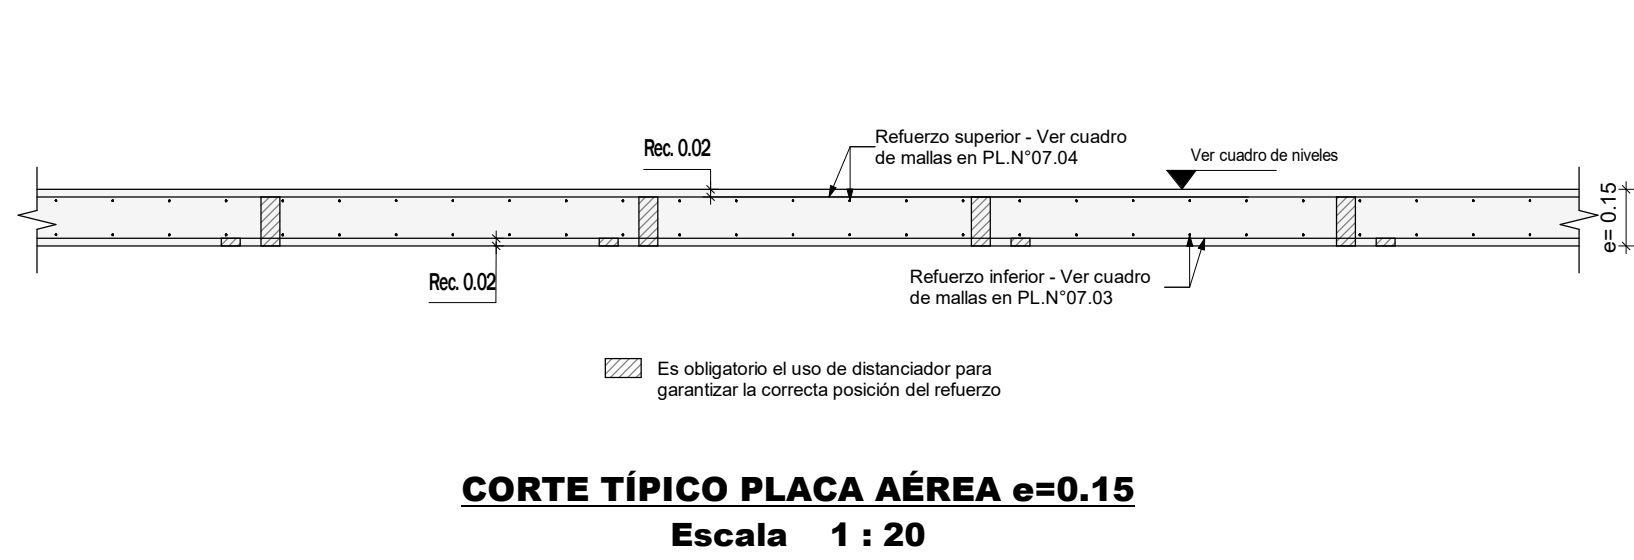

CORTE TÍPICO PLACA AÉREA e=0.15
Escala 1 : 20

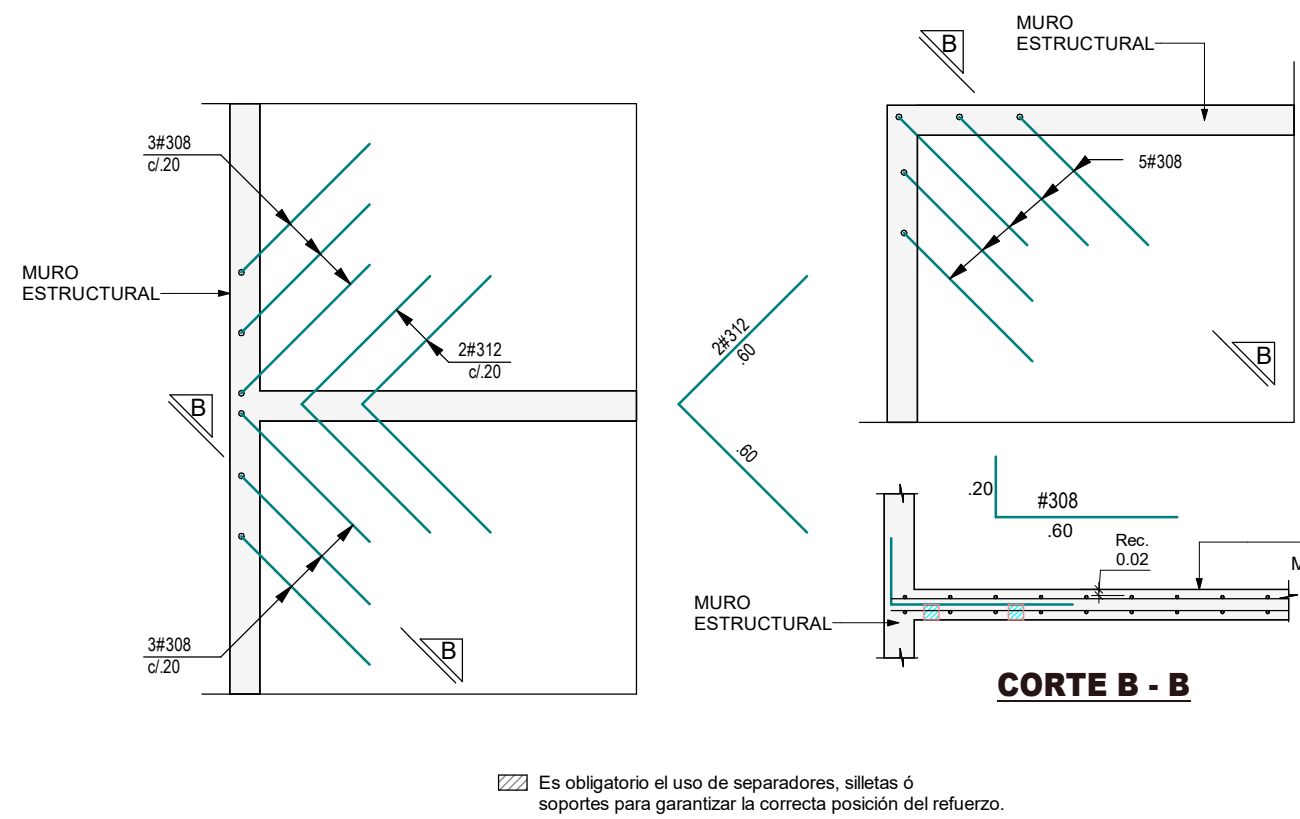

REFUERZO ADICIONAL EN PLACAS
Escala 1 : 25

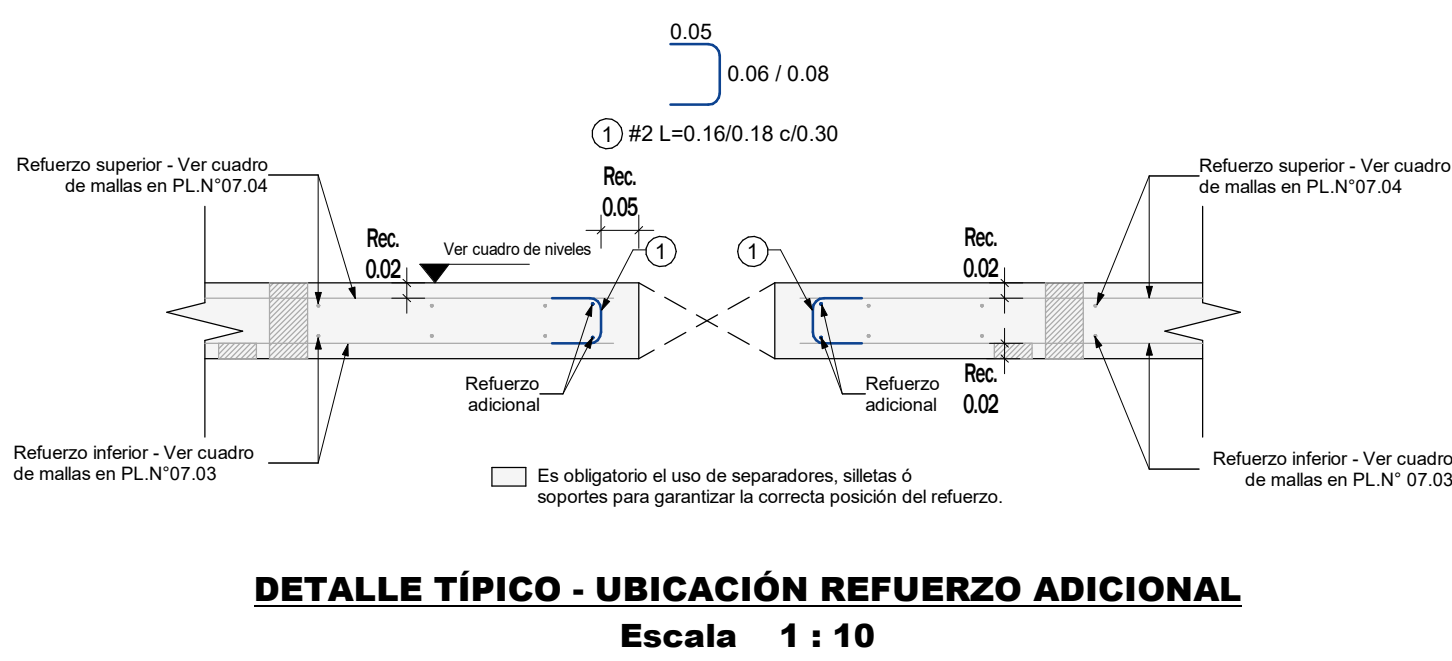

DETALLE TÍPICO - UBICACIÓN REFUERZO ADICIONAL
Escala 1 : 10

NOTAS:
1. Ver detalles generales en PL. N°01.02
2. Ver planta de localización e identificación de dinteles en PL. N° 07.01
3. Ver despieces de dinteles en PL. N° 10.00 a 10.04

CONVENCIÓNES			
	Indica dinteles		Indica placa e=0.10
	Indica placa e=0.12		Indica placa e=0.15
	Indica muro e=0.15		Indica muro e=0.25
	Indica muro e=0.30		Indica muro e=0.35
	Indica muro e=0.40		

CUADRO NIVELES PISO 16 A PISO 22			
PISO	NIVEL(NE.)		
PISO 16	39.75		
PISO 17	42.40		
PISO 18	45.05		
PISO 19	47.70		
PISO 20	50.35		
PISO 21	53.00		
PISO 22	55.65		

CONCRETO:			
LOSAS Y DINTELES			
* DE PISO 1 A PISO 8	* DE PISO 9 A PISO 15	* DE PISO 16 A PISO 22	* DE PISO 23 A CUBIERTA ASCENSOR Y ESCALERAS
f'c=35 MPa	f'c=32 MPa	f'c=25 MPa	f'c=21 MPa
f'c=350 kg/cm²	f'c=315 kg/cm²	f'c=245 kg/cm²	f'c=210 kg/cm²
f'c=5000 psi	f'c=4500 psi	f'c=3500 psi	f'c=3000 psi

GERENTE DE PROYECTO
ROBERTO AYCARDI F.
MAT. 2520257258 CND

INGENIERO
CARLOS ANDRÉS WILCHES C.

MODELADOR
DANIEL CASTELLANOS

MODIFICACIONES	FECHA
Emisión Inicial	28-02-2025
Ajuste borde de placa ejes D-6 y D-10	26-02-2026



LA SCALA

LA SCALA_EST_TOR-1

TORRE 1

CALLE 170 CON AV. BOYACA

PLANTA DE REFUERZO ADICIONAL PISO
TIPO 2 (PISO 16 A 22)

LA SCALA_EST_TOR-1_07.02_PT2-RADC

REVISOR ESTRUCTURAL
RAMÓN ANDRÉS ALVAREZ MANTILLA
MAT. 25202-346546 CND.

PLANO N°

07.02

VERSIÓN :

2