



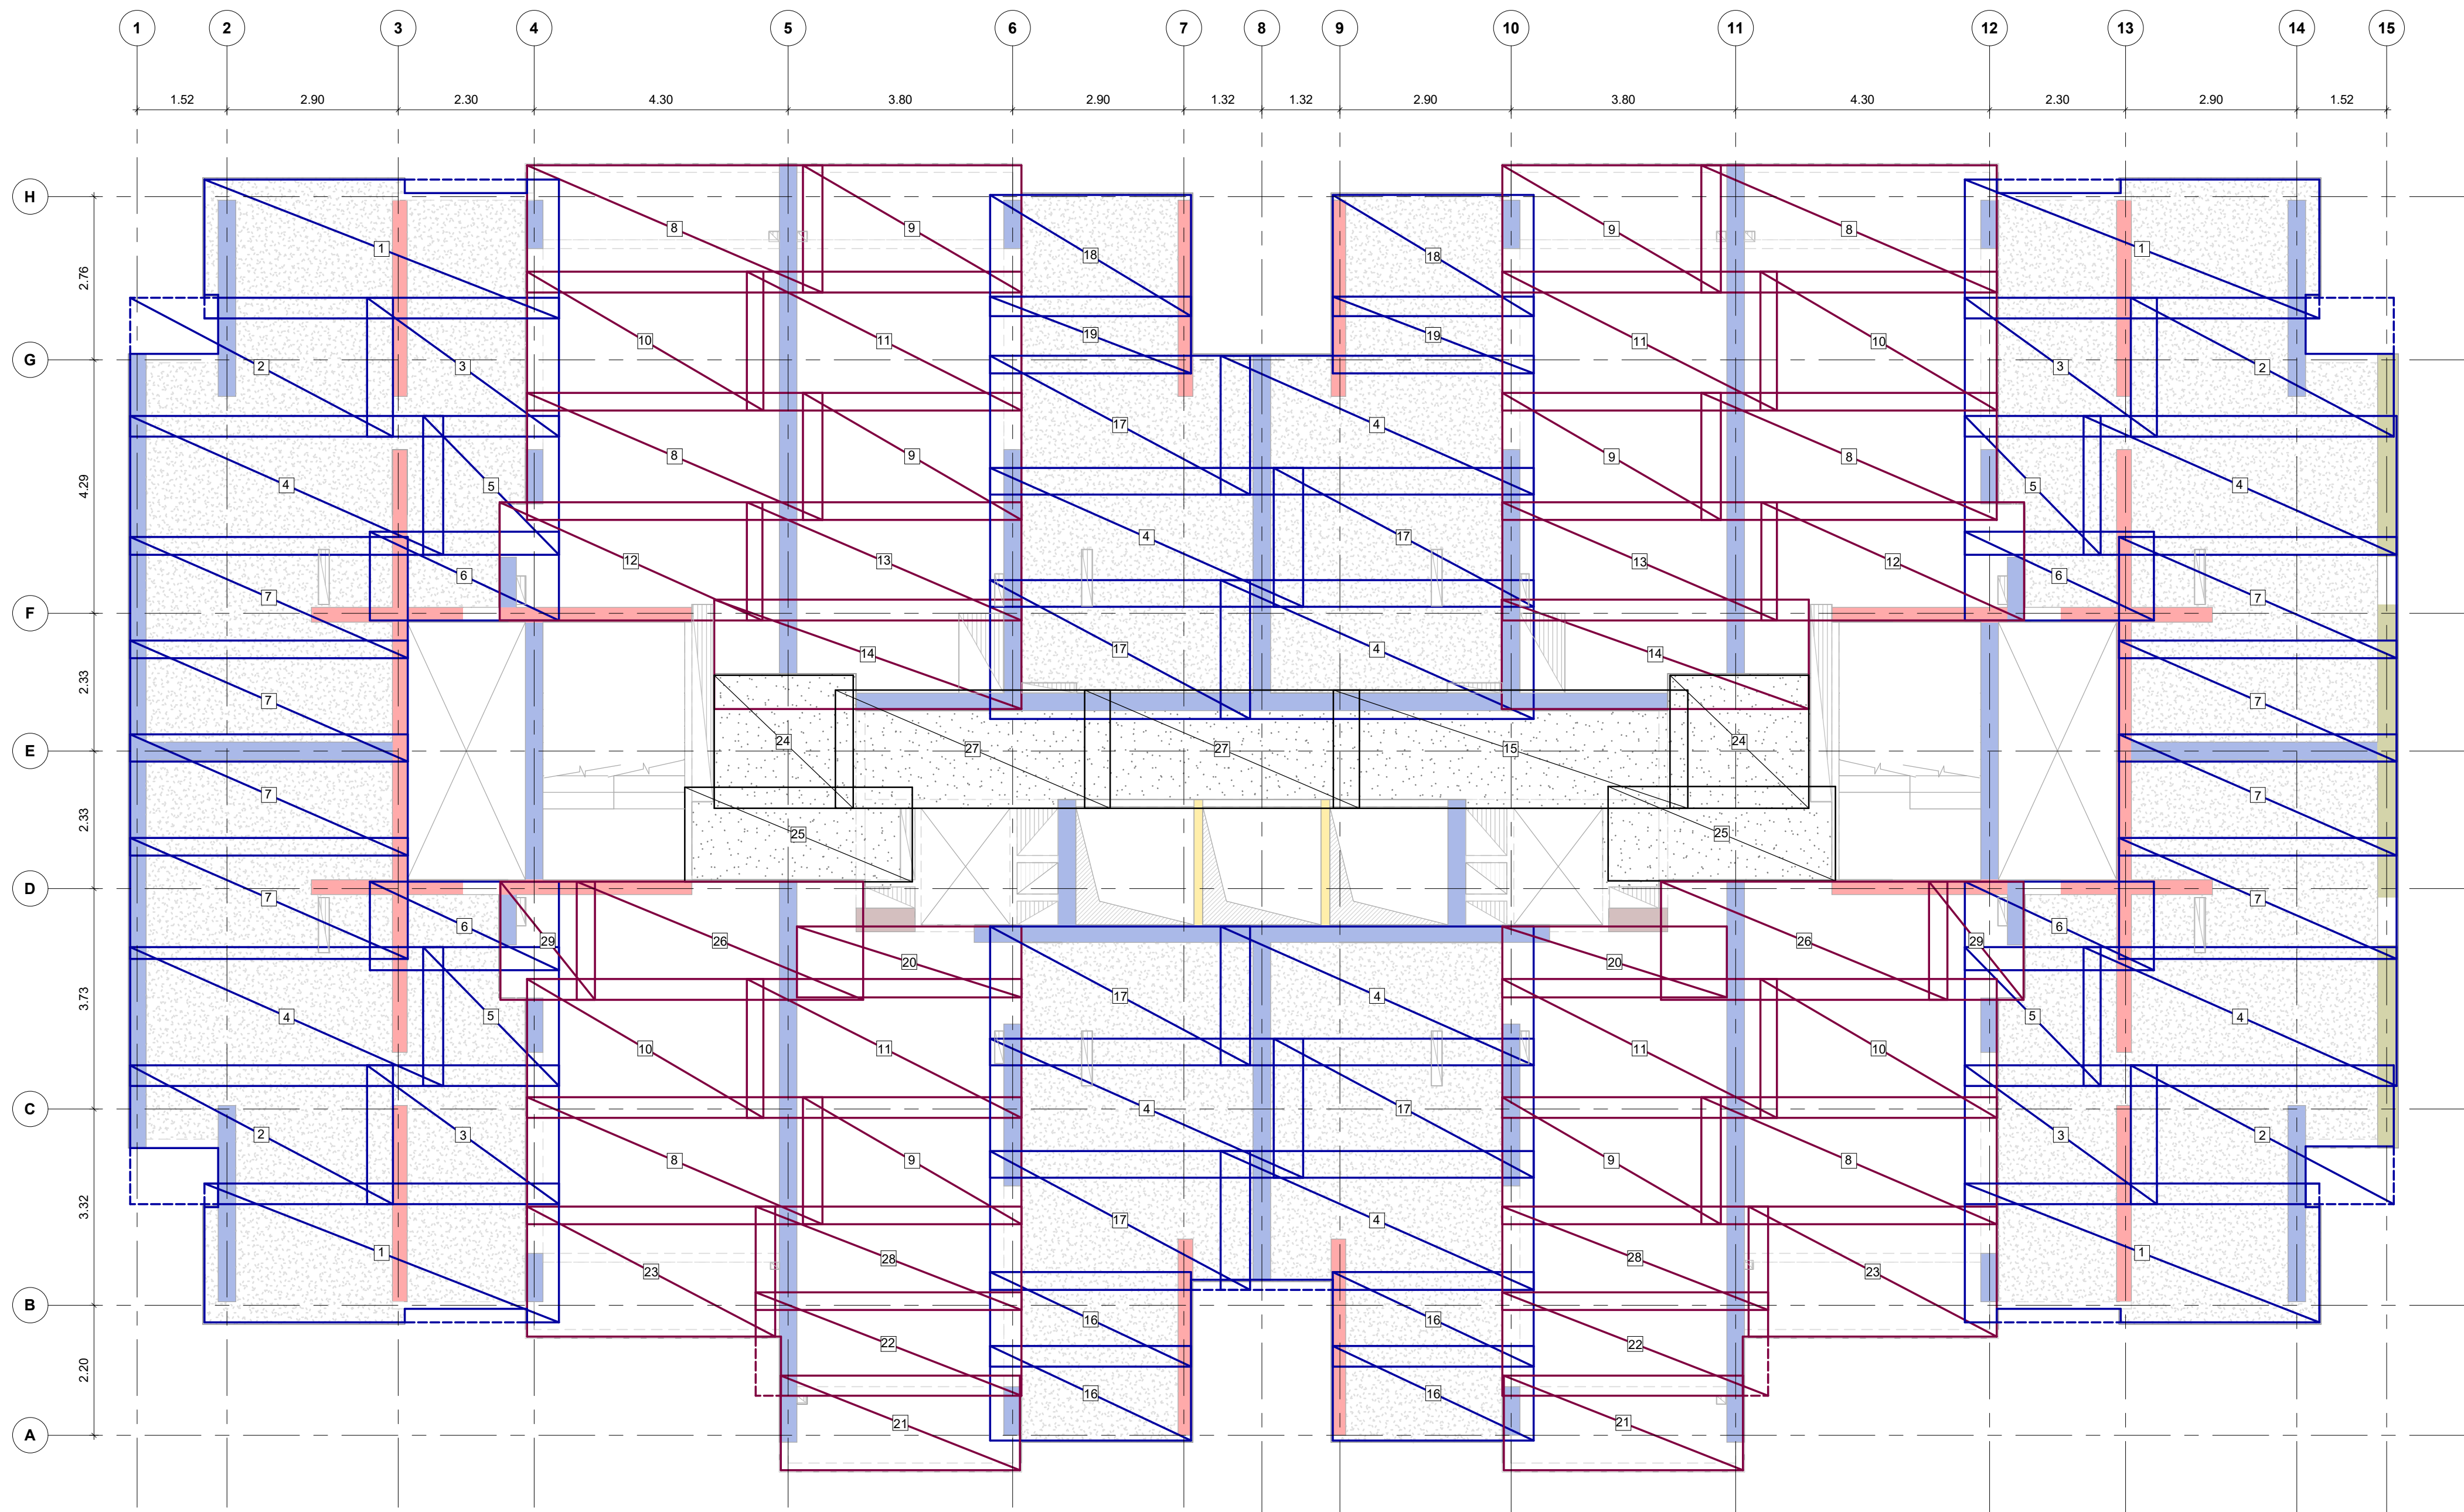


PLANTA DE REFUERZO INFERIOR PISO TIPO 2 (PISO 16 A PISO 22)
Escala 1 : 75

CUADRO DE MALLAS REFUERZO INFERIOR PISO TIPO 2 (PISO 16 A PISO 22)							
TIPO	A (m)	B(m)	ÁREA (m²)	CANT.	REFUERZO		PESO / MALLA (Kg/m²)
					REFUERZO A	REFUERZO B	
1	6.00	2.35	14 m²	4	Ø6.0mm c/0.15	Ø6.0mm c/0.15	2.993
2	4.45	2.35	10 m²	4	Ø6.0mm c/0.15	Ø6.0mm c/0.15	2.993
3	3.25	2.35	8 m²	4	Ø6.0mm c/0.15	Ø6.0mm c/0.15	2.993
4	5.30	2.35	12 m²	10	Ø6.0mm c/0.15	Ø6.0mm c/0.15	2.993
5	2.35	2.30	5 m²	4	Ø6.0mm c/0.15	Ø6.0mm c/0.15	2.993
6	3.20	1.50	5 m²	4	Ø6.0mm c/0.15	Ø6.0mm c/0.15	2.993
7	4.70	2.05	10 m²	8	Ø6.0mm c/0.15	Ø6.0mm c/0.15	2.993
8	5.00	2.15	11 m²	6	Ø6.5mm c/0.15	Ø6.5mm c/0.15	3.518
9	3.70	2.15	8 m²	6	Ø6.5mm c/0.15	Ø6.5mm c/0.15	3.518
10	4.00	2.35	9 m²	4	Ø6.5mm c/0.15	Ø6.5mm c/0.15	3.518
11	4.65	2.35	11 m²	4	Ø6.5mm c/0.15	Ø6.5mm c/0.15	3.518
12	4.45	2.00	9 m²	2	Ø6.5mm c/0.15	Ø6.5mm c/0.15	3.518
13	4.65	2.00	9 m²	2	Ø6.5mm c/0.15	Ø6.5mm c/0.15	3.518
14	5.20	1.85	10 m²	2	Ø6.5mm c/0.15	Ø6.5mm c/0.15	3.518
15	6.00	2.00	12 m²	1	Ø7.5mm c/0.15	Ø7.5mm c/0.15	4.674
16	3.40	1.60	5 m²	4	Ø6.0mm c/0.15	Ø6.0mm c/0.15	2.993
17	4.40	2.35	10 m²	6	Ø6.0mm c/0.15	Ø6.0mm c/0.15	2.993
18	3.40	2.05	7 m²	2	Ø6.0mm c/0.15	Ø6.0mm c/0.15	2.993
19	3.40	1.30	4 m²	2	Ø6.0mm c/0.15	Ø6.0mm c/0.15	2.993
20	3.80	1.20	5 m²	2	Ø6.5mm c/0.15	Ø6.5mm c/0.15	3.518
21	4.05	1.60	6 m²	2	Ø6.5mm c/0.15	Ø6.5mm c/0.15	3.518
22	4.50	1.75	8 m²	2	Ø6.5mm c/0.15	Ø6.5mm c/0.15	3.518
23	4.20	2.20	9 m²	2	Ø6.5mm c/0.15	Ø6.5mm c/0.15	3.518
24	2.35	2.25	5 m²	2	Ø7.5mm c/0.15	Ø7.5mm c/0.15	4.674
25	3.85	1.60	6 m²	2	Ø7.5mm c/0.15	Ø7.5mm c/0.15	4.674
26	4.85	2.00	10 m²	2	Ø6.5mm c/0.15	Ø6.5mm c/0.15	3.518
27	4.65	2.00	9 m²	2	Ø7.5mm c/0.15	Ø7.5mm c/0.15	4.674
28	4.50	1.75	8 m²	2	Ø6.5mm c/0.15	Ø6.5mm c/0.15	3.518
29	1.60	2.00	3 m²	2	Ø6.5mm c/0.15	Ø6.5mm c/0.15	3.518
TOTAL : 99				99			2901

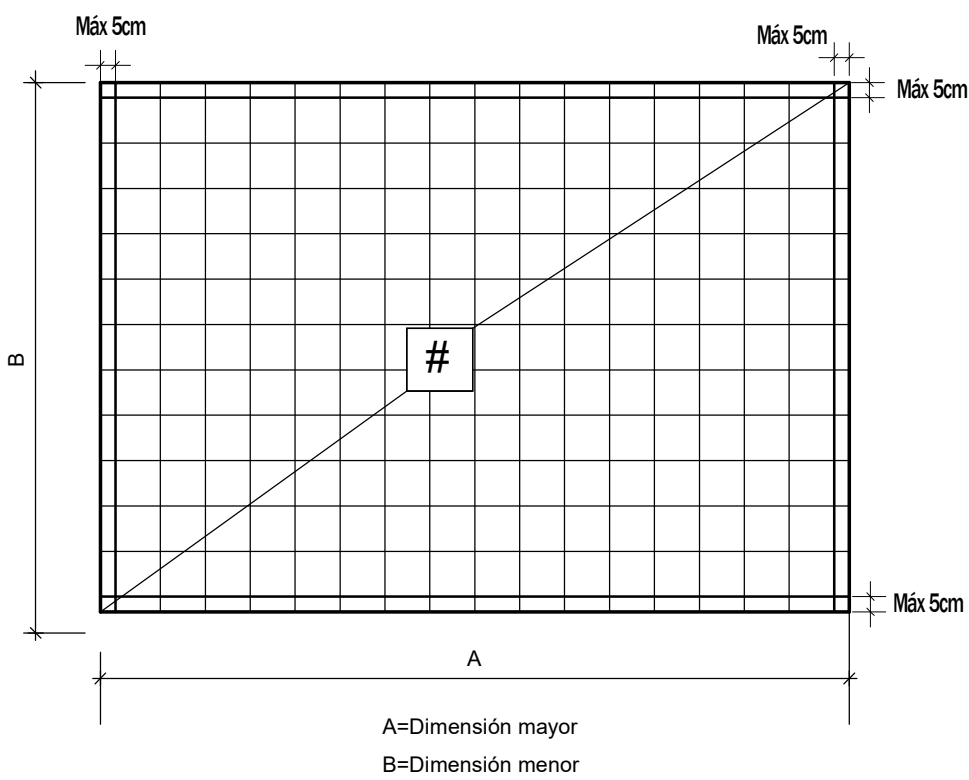

Nota: El grafi de cada extremo de la malla no puede estar a mas de 5cm del borde de la malla

DETALLE CONVENCION MALLAS
Escala 1 : 25

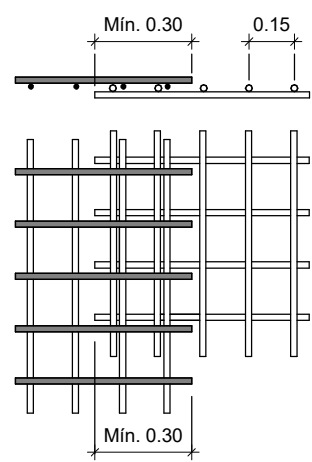

DETALLE TRASLAPO MALLAS
Escala 1 : 25

NOTAS:
1. Ver detalles generales en el PL. N° 01.02
2. Ver planta de refuerzo adicional en PL. N° 07.02
3. Ver planta de refuerzo superior en PL. N° 07.04
4. Las dimensiones de las mallas deben ser verificadas por el constructor.

CONCRETO: LOSAS Y DINTELES			
* DE PISO 1 A PISO 8	* DE PISO 9 A PISO 15	* DE PISO 16 A PISO 22	* DE PISO 23 A CUBIERTA ASCENSOR Y ESCALERAS
f'c=35 MPa	f'c=32 MPa	f'c=25 MPa	f'c=21 MPa
f'c=350 kg/cm²	f'c=315 kg/cm²	f'c=245 kg/cm²	f'c=210 kg/cm²
f'c=5000 psi	f'c=4500 psi	f'c=3500 psi	f'c=3000 psi

CUADRO NIVELES PISO 16 A PISO 22	
PISO	NIVEL(NE.)
PISO 16	39.75
PISO 17	42.40
PISO 18	45.05
PISO 19	47.70
PISO 20	50.35
PISO 21	53.00
PISO 22	55.65

CONVENCIONES	
Indica Malla	Indica cortar Malla
Indica N° de Malla	

CONVENCIONES	
Indica dinteles	Indica placa e=0.10
Indica placa e=0.12	Indica placa e=0.15
Indica muros en concreto e=0.15	Indica muros en concreto e=0.25
Indica muros en concreto e=0.30	Indica muros en concreto e=0.35
Indica muros en concreto e=0.40	

VERSIÓN :

2

PLANO N°

07.03

GERENTE DE PROYECTO
ROBERTO AYCARDI F.
MAT. 2520257258 CND

INGENIERO
CARLOS ANDRÉS WILCHES C.

MODELADOR
DANIEL CASTELLANOS

MODIFICACIONES	FECHA
Emisión Inicial	28-02-2025
Ajuste borde de placa ejes D-6 y D-10 y se actualiza cuadro de mallas	26-02-2026



LA SCALA

LA SCALA_EST_TOR-1

TORRE 1

CALLE 170 CON AV. BOYACA

PLANTA DE REFUERZO INFERIOR PISO TIPO 2 (PISO 16 A PISO 22)

LA SCALA_EST_TOR-1_07.03_PT2-RINF

REVISOR ESTRUCTURAL

RAMÓN ÁNDRES ALVAREZ MANTILLA
MAT. 25202-346546 CND.

PLANO N°

VERSIÓN :

07.03

2