


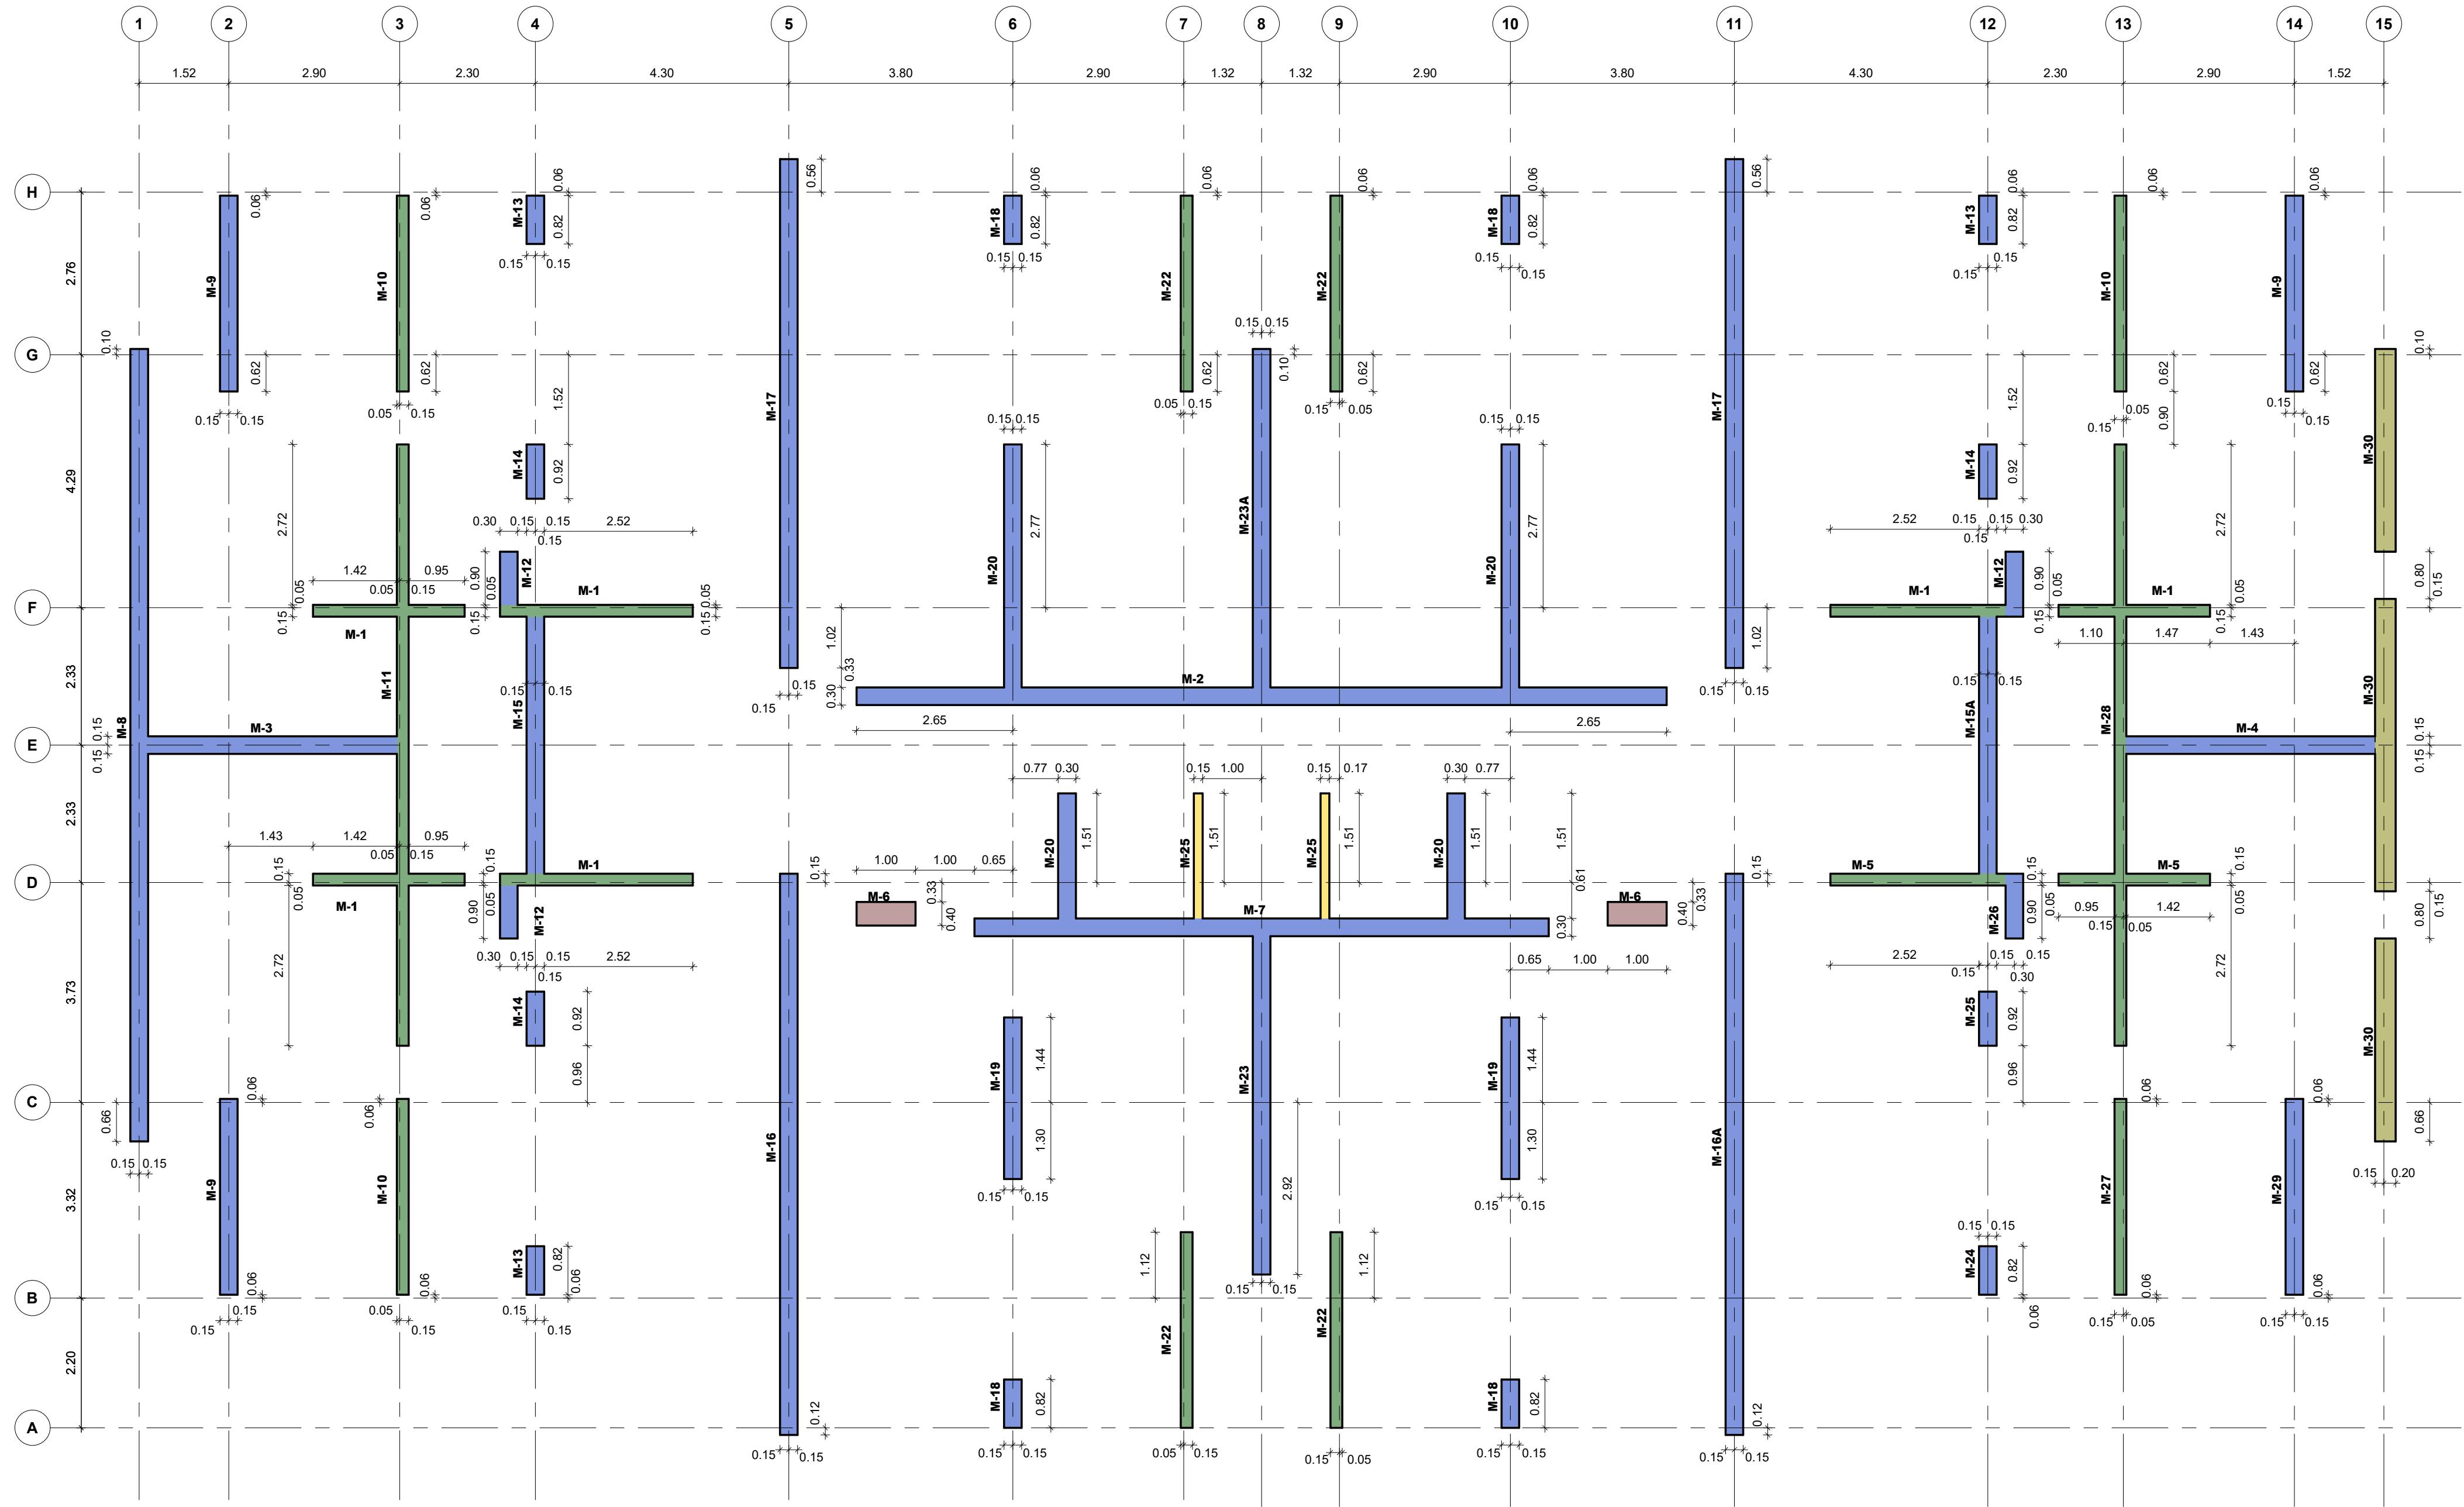

PLANTA LOCALIZACIÓN DE MUROS PISO TIPO 3 (PISO 22 A PISO PISO 28)
Escala 1 : 75

CUADRO NIVELES PISO 23 A PISO 28	
PISO	NIVEL(ME.)
PISO 23	58.30
PISO 24	60.95
PISO 25	63.60
PISO 26	66.25
PISO 27	68.90
PISO 28	71.55

CONCRETO:			
MUROS			
* DE CIMENTACIÓN A PISO 8	* DE PISO 8 A PISO 15	* DE PISO 15 A PISO 22	* DE PISO 22 A CUBIERTA ASCENSOR Y ESCALERAS
f_c=49 MPa	f_c=42 MPa	f_c=35 MPa	f_c=28 MPa
f_c=490 kg/cm²	f_c=420 kg/cm²	f_c=350 kg/cm²	f_c=280 kg/cm²
f_c=7000 psi	f_c=6000 psi	f_c=5000 psi	f_c=4000 psi

CONVENCIONES	
M-#	Indica N° de Muro
	Indica muro e=0.15
	Indica muro e=0.20
	Indica muro e=0.30
	Indica muro e=0.35
	Indica muro e=0.40
NOTAS	
1. Ver detalles generales en PL. N°01.02	
2. Ver despieces de muros en PL. N° 11.00 a PL. N°11.21	
3. Ver detalles de muros en PL. N° 11.22	

MODIFICACIONES		FECHA
Emisión Inicial		28-02-2025
Se actualiza longitud de muro M-19		04-11-2025



LA SCALA

LA SCALA_EST_TOR-1

TORRE 1

CALLE 170 CON AV. BOYACA

PLANTA LOCALIZACIÓN DE MUROS PISO TIPO 3 (PISO 22 A PISO PISO 28)

LA SCALA_EST_TOR-1_08.00_LCM-PT3