


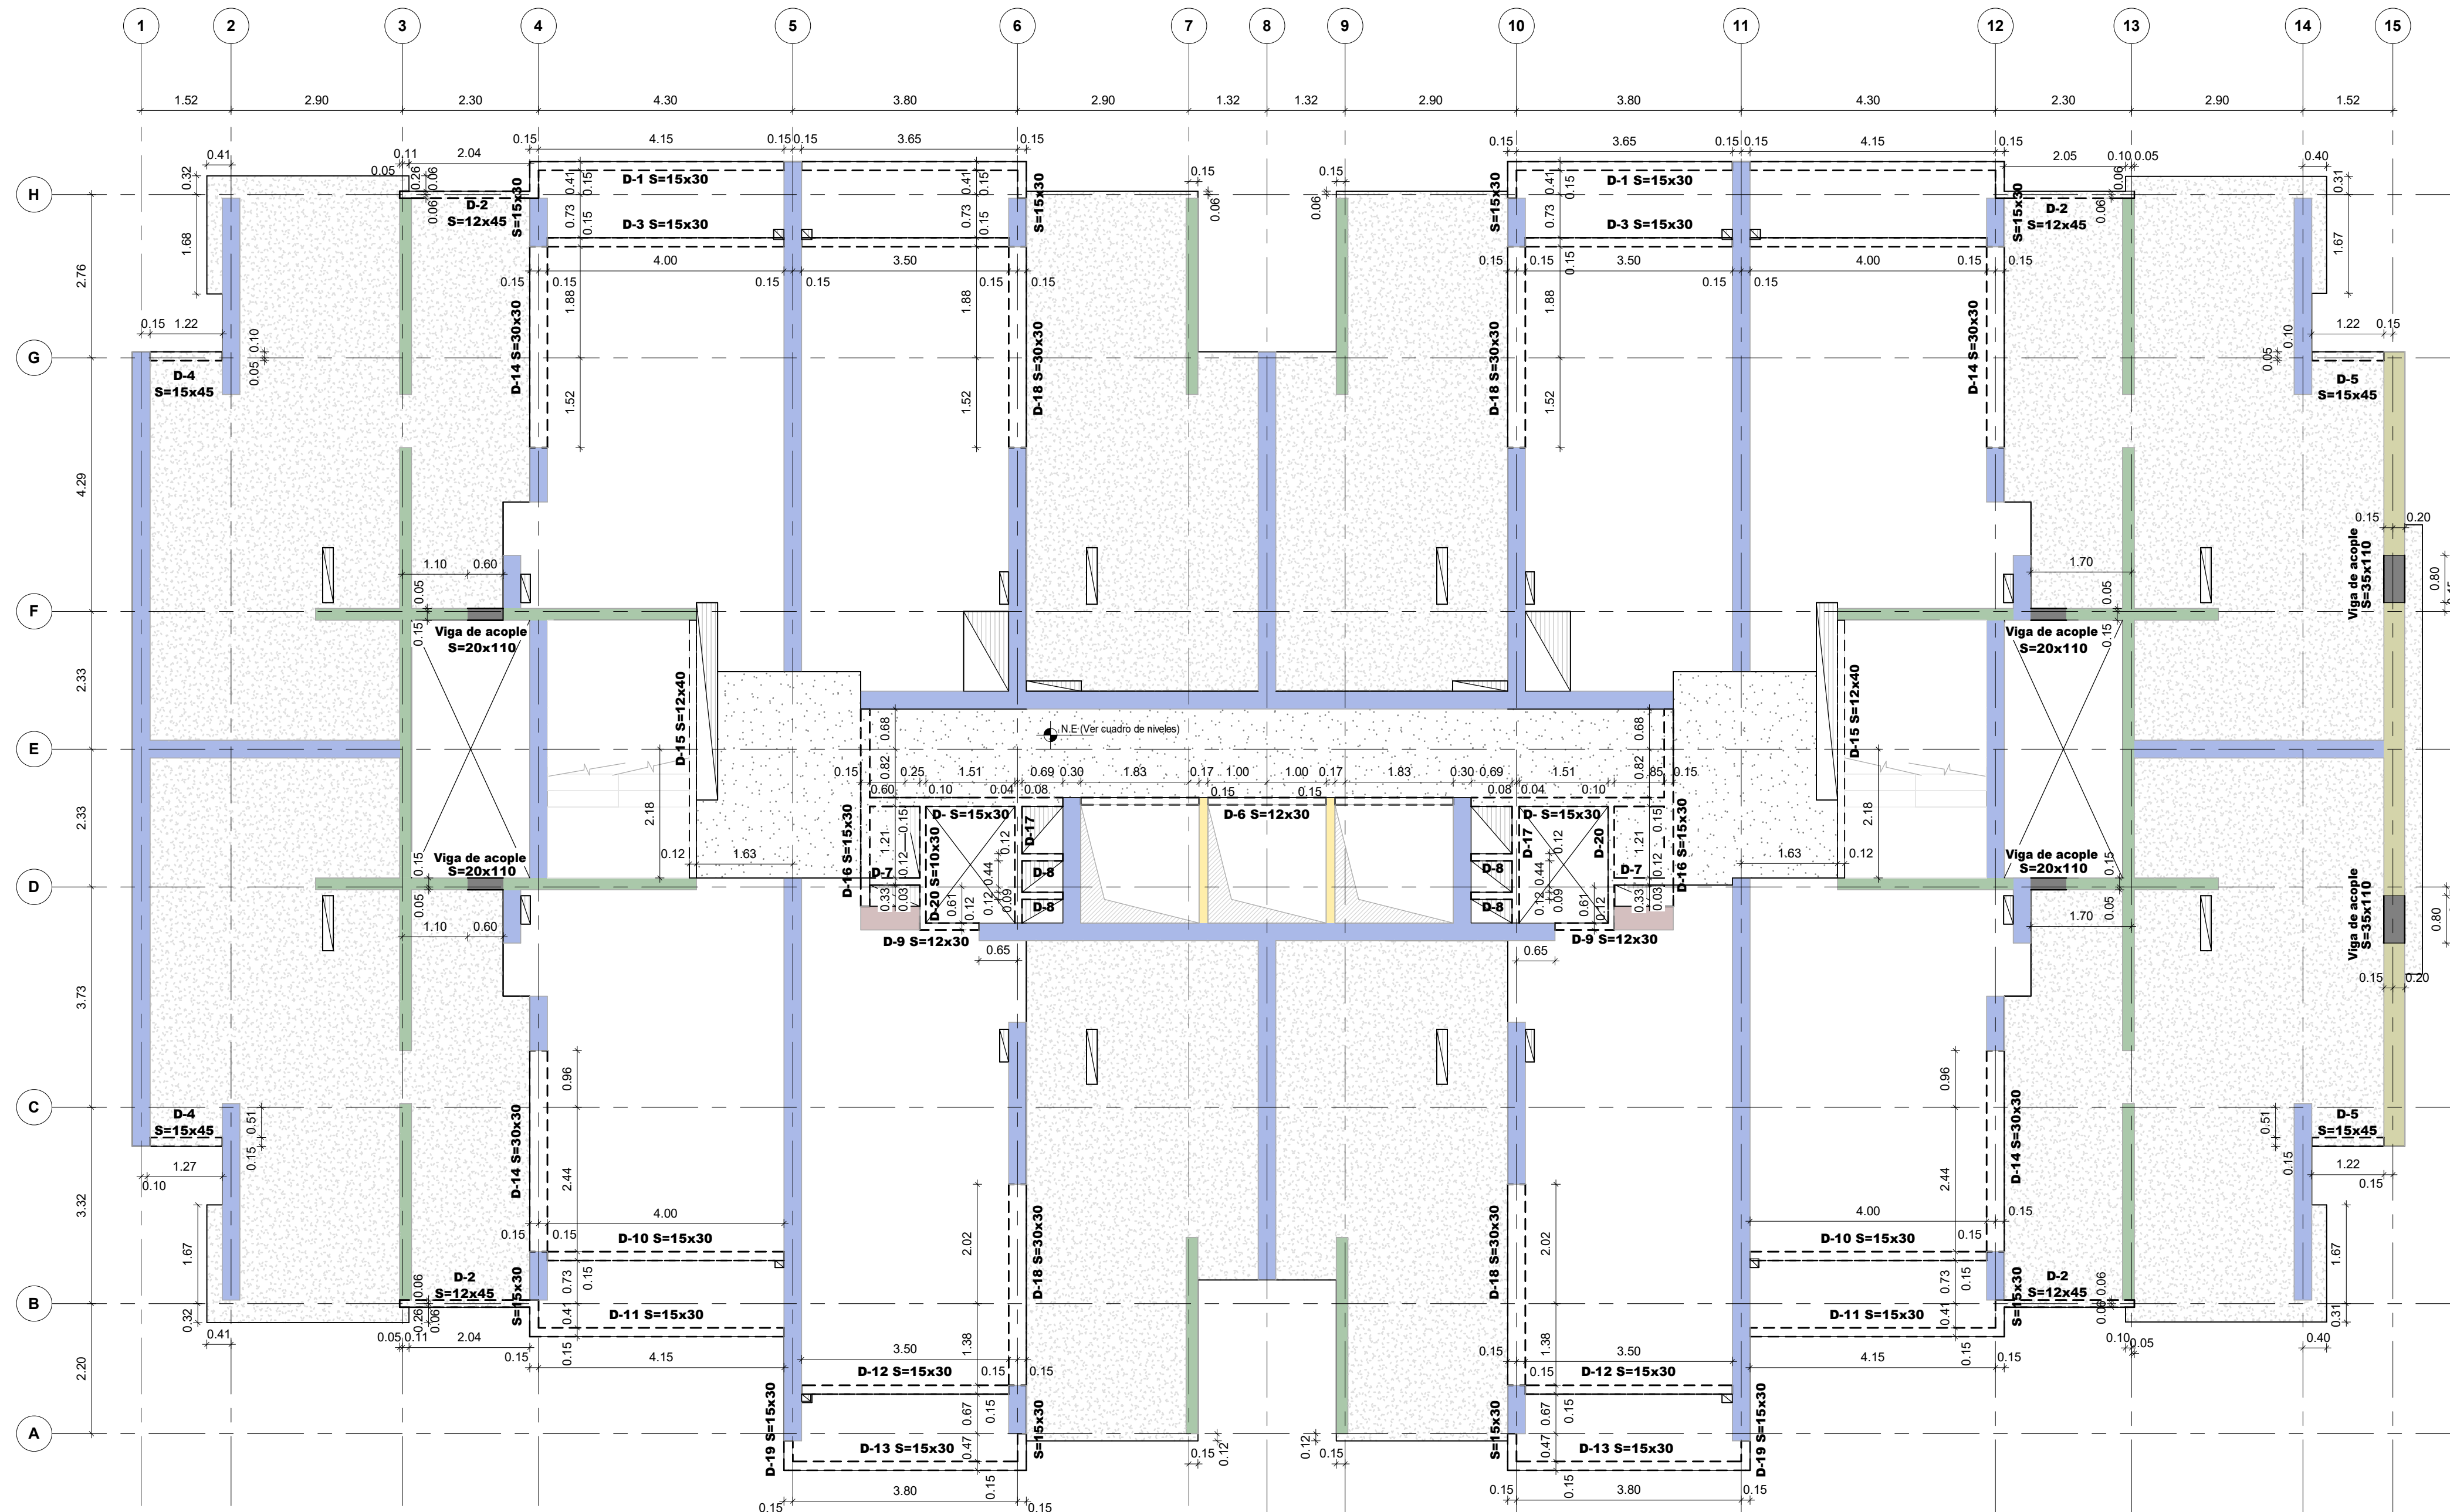

PLANTA LOCALIZACIÓN DE DINTELES PISO TIPO 3 (PISO 23 A PISO 28)
Escala 1 : 75

CUADRO NIVELES PISO 23 A PISO 28	
PISO	NIVEL(NE.)
PISO 23	58.30
PISO 24	60.95
PISO 25	63.60
PISO 26	66.25
PISO 27	68.90
PISO 28	71.55

CONCRETO: VIGAS DE ACOPLE			
* DE PISO 2 A PISO 8	* DE PISO 8 A PISO 15	* DE PISO 15 A PISO 22	* DE PISO 22 A PISO 28
f'c=49 MPa	f'c=42 MPa	f'c=35 MPa	f'c=28 MPa
f'c=490 kg/cm²	f'c=420 kg/cm²	f'c=350 kg/cm²	f'c=280 kg/cm²
f'c=7000 psi	f'c=6000 psi	f'c=5000 psi	f'c=4000 psi

CONCRETO: LOSAS Y DINTELES			
* DE PISO 1 A PISO 8	* DE PISO 9 A PISO 15	* DE PISO 16 A PISO 22	* DE PISO 23 A CUBIERTA ASCENSOR Y ESCALERAS
f'c=35 MPa	f'c=32 MPa	f'c=25 MPa	f'c=21 MPa
f'c=350 kg/cm²	f'c=315 kg/cm²	f'c=245 kg/cm²	f'c=210 kg/cm²
f'c=5000 psi	f'c=4500 psi	f'c=3500 psi	f'c=3000 psi

- CONVENCIONES**
- Indica dinteles
 - Indica N° de dintel
 - Indica Vigas de acople
 - Indica muro e=0.15
 - Indica muro e=0.20
 - Indica muro e=0.30
 - Indica muro e=0.35
 - Indica muro e=0.40
 - Indica placa e=0.10
 - Indica placa e=0.12
 - Indica placa e=0.15
- NOTAS**
- Ver detalles generales en PL. N°01.02
 - Ver despieces de dinteles en PL. N° 10.00 a 10.04
 - Ver detalle viga de acople en PL. N° 11.01,11.05,11.20

GERENTE DE PROYECTO
ROBERTO AYCARDI F.
MAT. 2520257258 CND

INGENIERO
CARLOS ANDRÉS WILCHES C.

MODELADOR
DANIEL CASTELLANOS

MODIFICACIONES	FECHA
Emisión Inicial	28-02-2025
Ajuste borde de placa ejes D-6 y D-10	26-02-2026



LA SCALA

LA SCALA_EST_TOR-1

TORRE 1

CALLE 170 CON AV. BOYACA

PLANTA LOCALIZACIÓN E IDENTIFICACIÓN
DE DINTELES PISO TIPO 3 (PISO 23 A PISO 28)

LA SCALA_EST_TOR-1_08.01_LDINT-PT3

REVISOR ESTRUCTURAL
RAMÓN ANDRÉS ALVAREZ MANTILLA
MAT. 25202-346546 CND.