

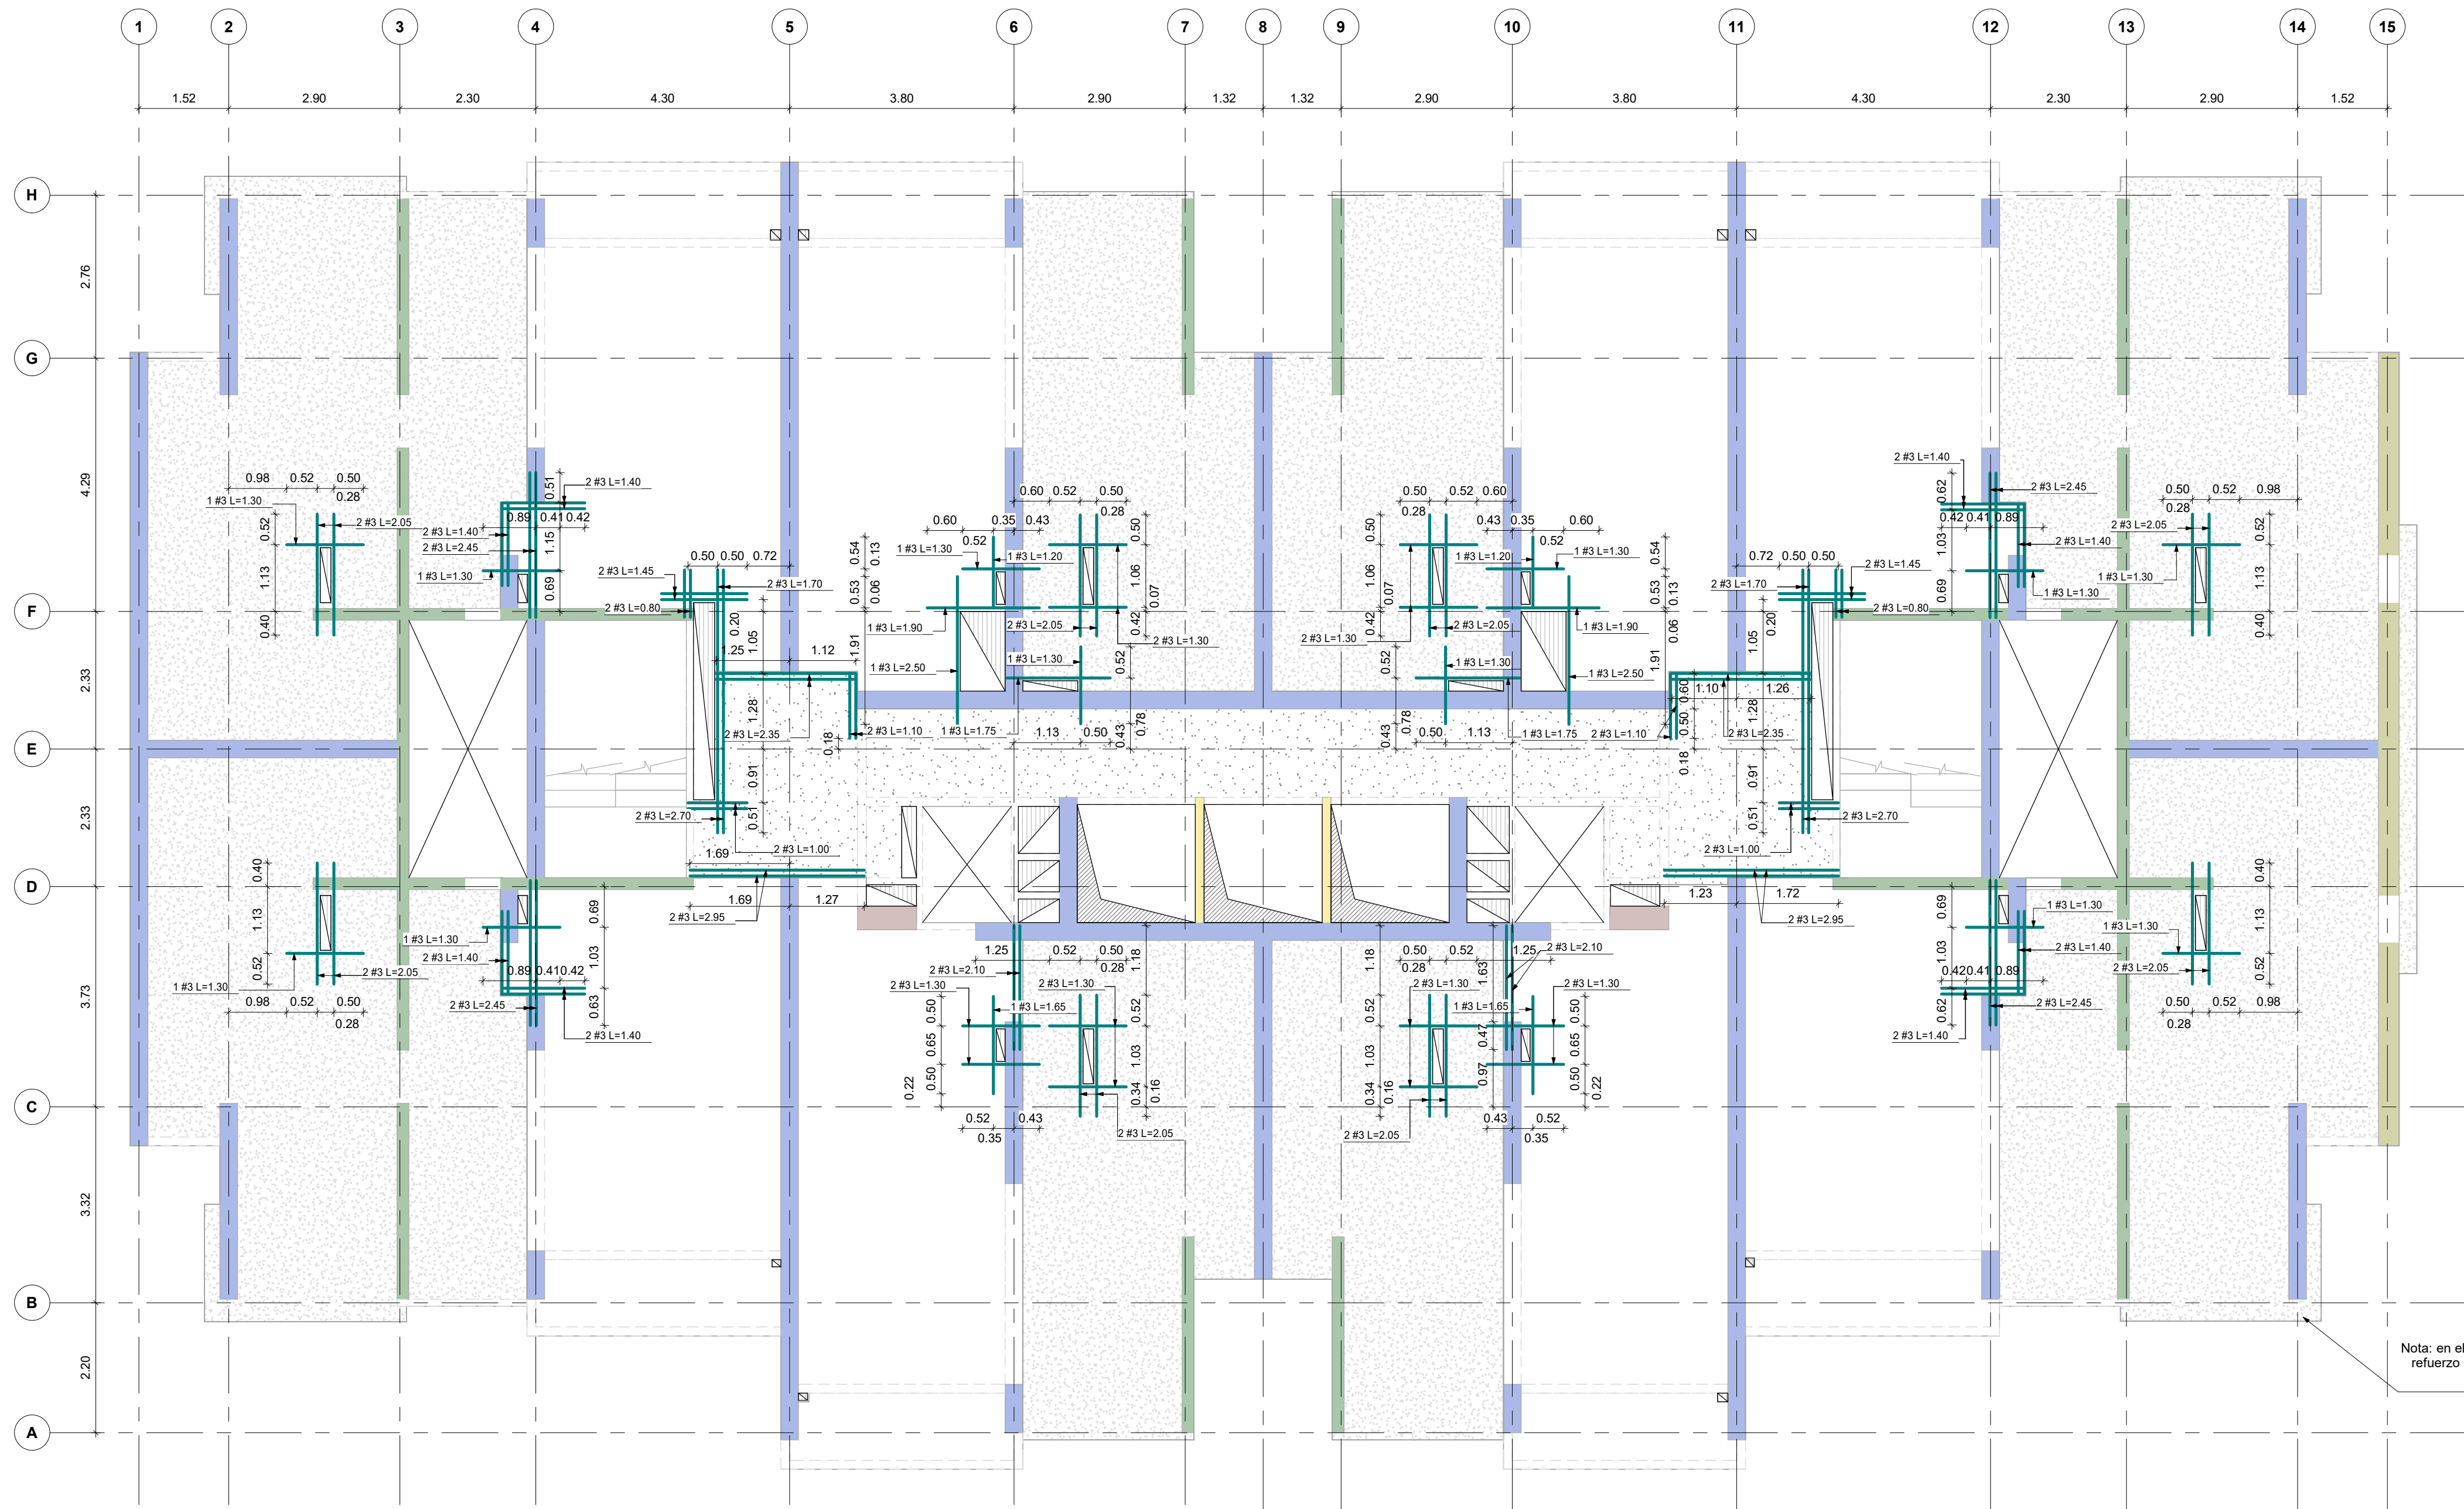
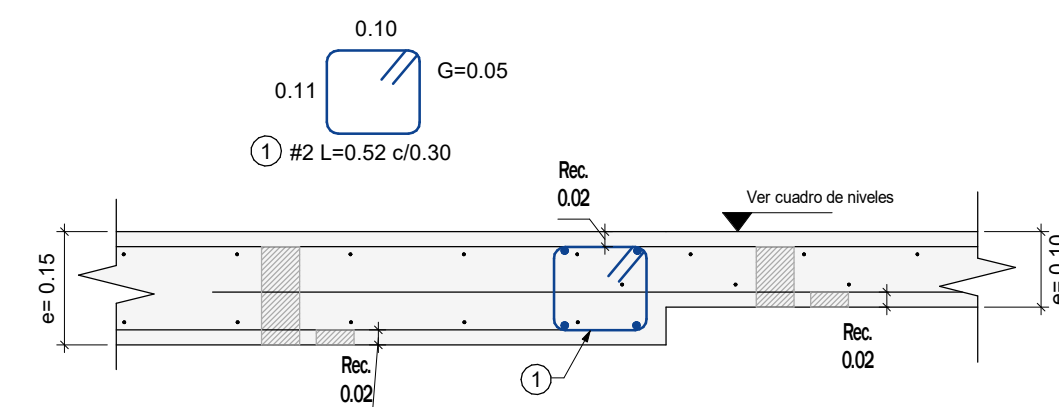


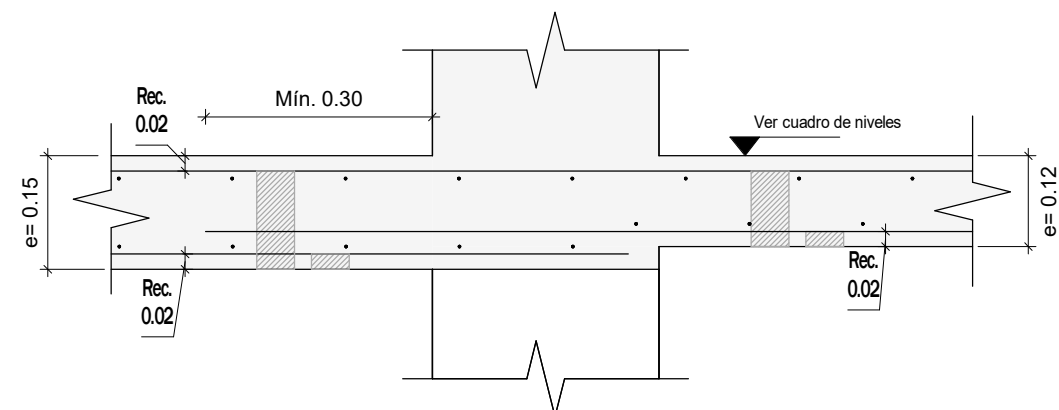


PLANTA DE REFUERZO ADICIONAL PISO TIPO 3 (PISO 23 A PISO 28)
Escala 1 : 75

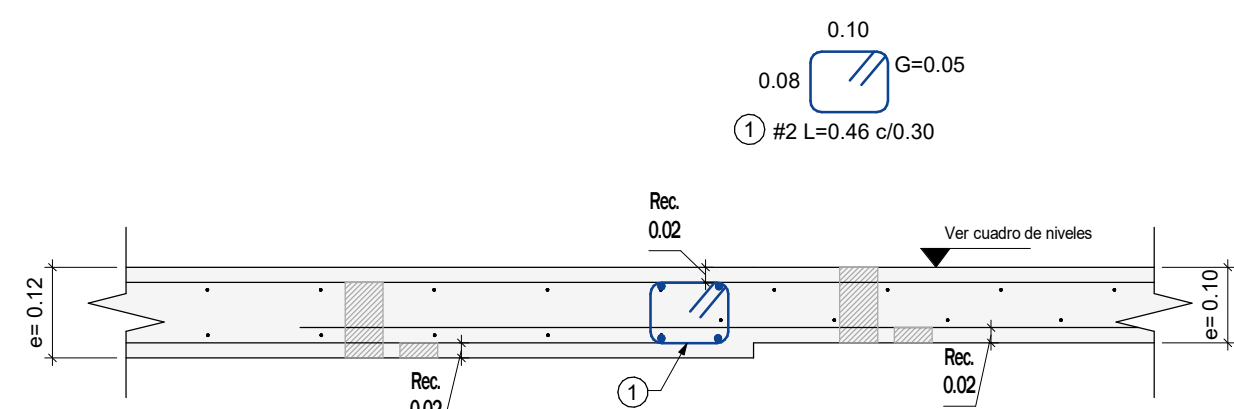


Es obligatorio el uso de distanciador para garantizar la correcta posición del refuerzo

DETALLES TÍPICOS - CAMBIO DE SECCIÓN
Escala 1 : 10


Nota: en el perímetro del piso tener en cuenta refuerzo indicado en plano N° 13.00 - Muros de fachada

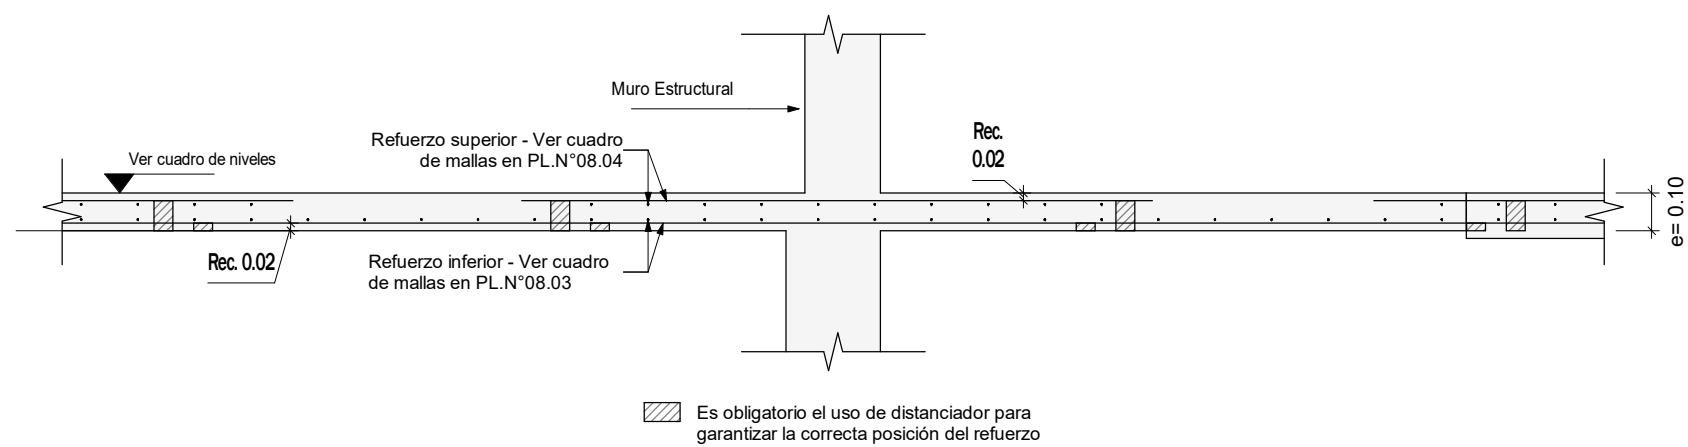


CORTE TÍPICO PLACA ÁEREA e=0.10
Escala 1 : 20

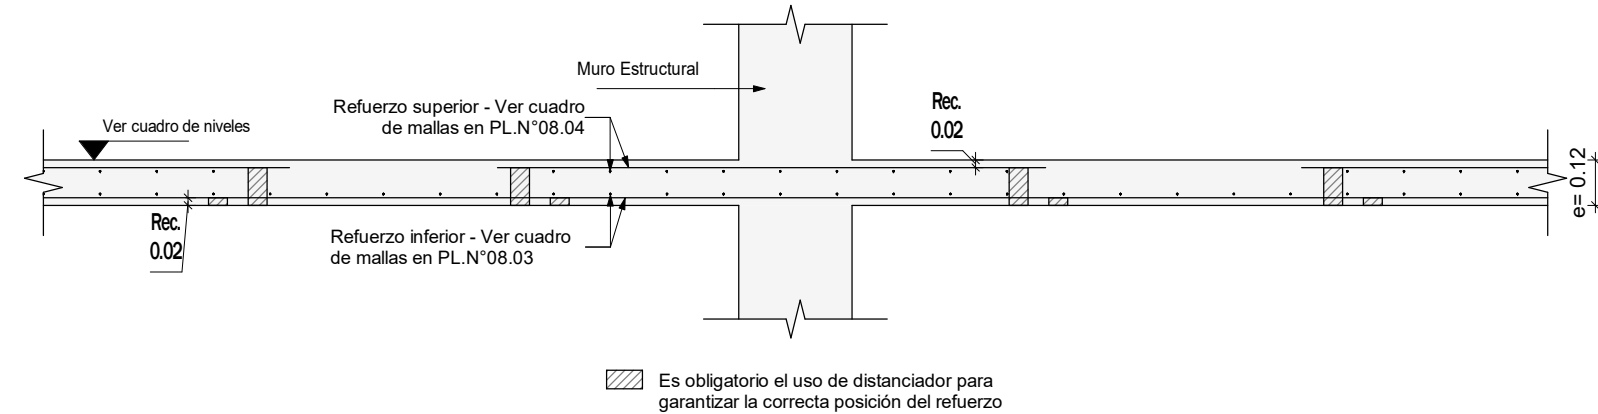

CORTE TÍPICO PLACA ÁEREA e=0.12
Escala 1 : 20

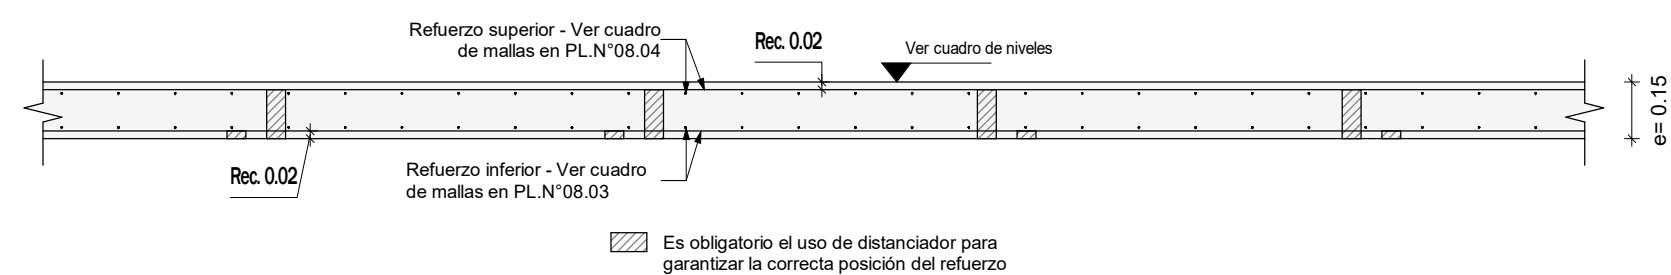

CORTE TÍPICO PLACA ÁEREA e=0.15
Escala 1 : 20

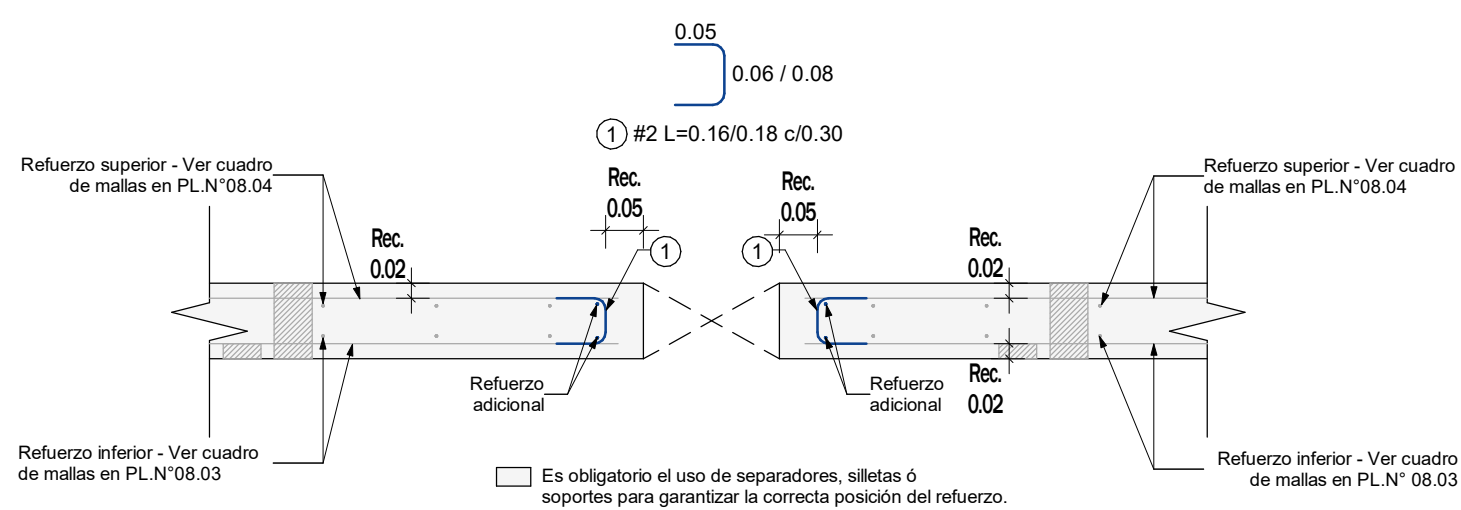

DETALLE TÍPICO - UBICACIÓN REFUERZO ADICIONAL
Escala 1 : 10

CUADRO NIVELES PISO 23 A PISO 28	
PISO	NIVEL (NE.)
PISO 23	58.30
PISO 24	60.95
PISO 25	63.60
PISO 26	66.25
PISO 27	68.90
PISO 28	71.55

CONVENCIONES	
	Indica dinteles
	Indica placa e=0.10
	Indica placa e=0.12
	Indica placa e=0.15
	Indica muro e=0.15
	Indica muro e=0.20
	Indica muro e=0.30
	Indica muro e=0.35
	Indica muro e=0.40

NOTAS:
1. Ver detalles generales en PL. N°01.02
2. Ver plantas de localización e identificación de dinteles en PL. N° 08.01
3. Ver despieces de dinteles en PL. N° 10.00 a 10.04

CONCRETO: LOSAS Y DINTELES			
* DE PISO 1 A PISO 8	* DE PISO 9 A PISO 15	* DE PISO 16 A PISO 22	* DE PISO 23 A CUBIERTA ASCENSOR Y ESCALERAS
f'c=35 MPa	f'c=32 MPa	f'c=25 MPa	f'c=21 MPa
f'c=350 kg/cm²	f'c=315 kg/cm²	f'c=245 kg/cm²	f'c=210 kg/cm²
f'c=5000 psi	f'c=4500 psi	f'c=3500 psi	f'c=3000 psi

VERSIÓN :

2

PLANO N°

08.02



GERENTE DE PROYECTO
ROBERTO AYCARDI F.
MAT. 2520257258 CND

INGENIERO
CARLOS ANDRÉS WILCHES C.

MODELADOR
DANIEL CASTELLANOS

MODIFICACIONES	FECHA
Emisión Inicial	28-02-2025
Ajuste borde de placa ejes D-6 y D-10	26-02-2026



LA SCALA

LA SCALA_EST_TOR-1

TORRE 1

CALLE 170 CON AV. BOYACA

PLANTA DE REFUERZO ADICIONAL PISO
TIPO 3 (PISO 23 A 28)

LA SCALA_EST_TOR-1_08.02_PT3-RADC

REVISOR ESTRUCTURAL

RAMÓN ANDRÉS ALVAREZ MANTILLA
MAT. 25202-346546 CND.

PLANO N°

08.02

VERSIÓN :

2