

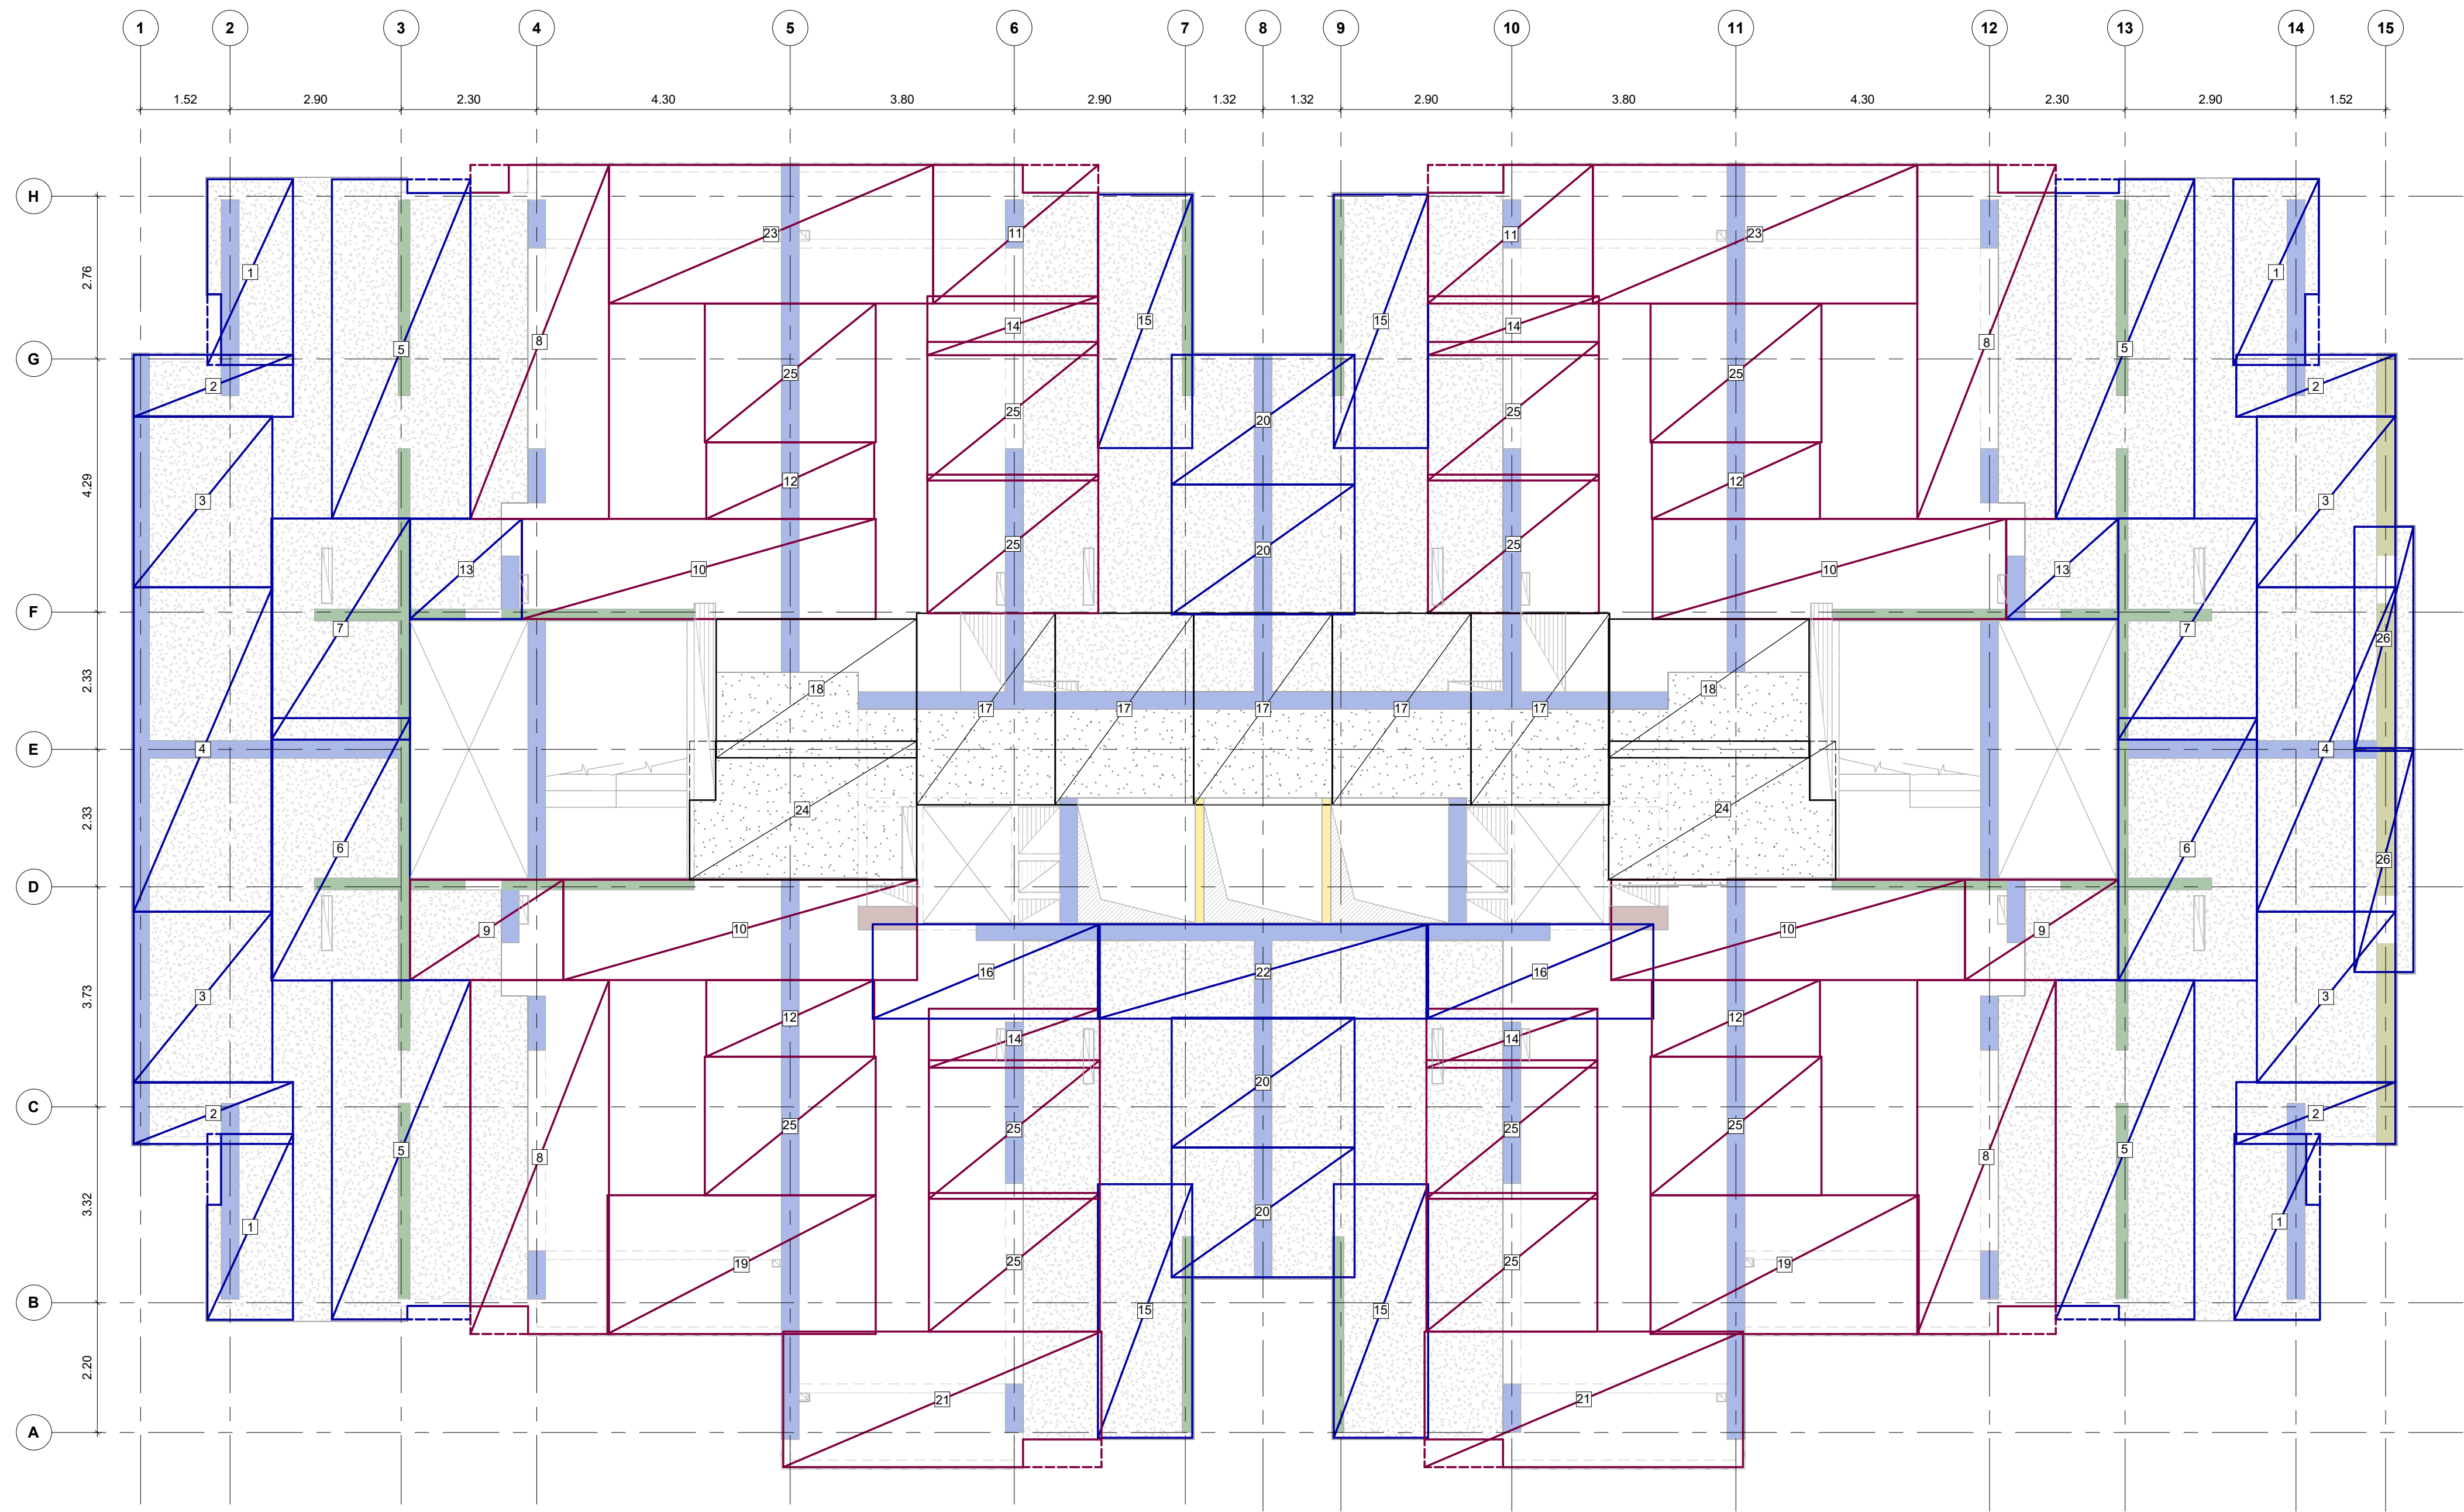


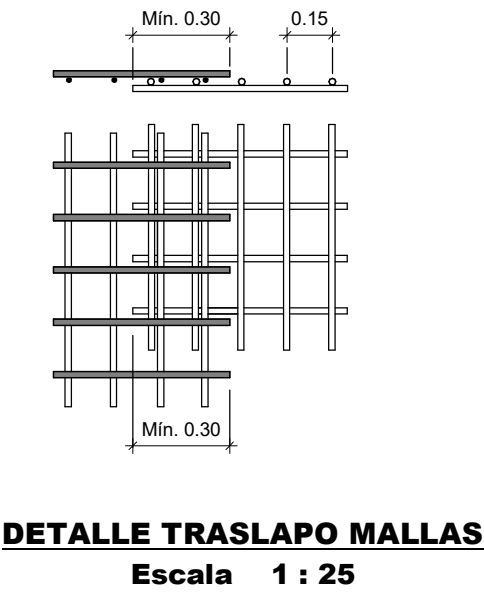


PLANTA DE REFUERZO SUPERIOR PISO TIPO 3 (PISO 23 A PISO 28)
Escala 1 : 75

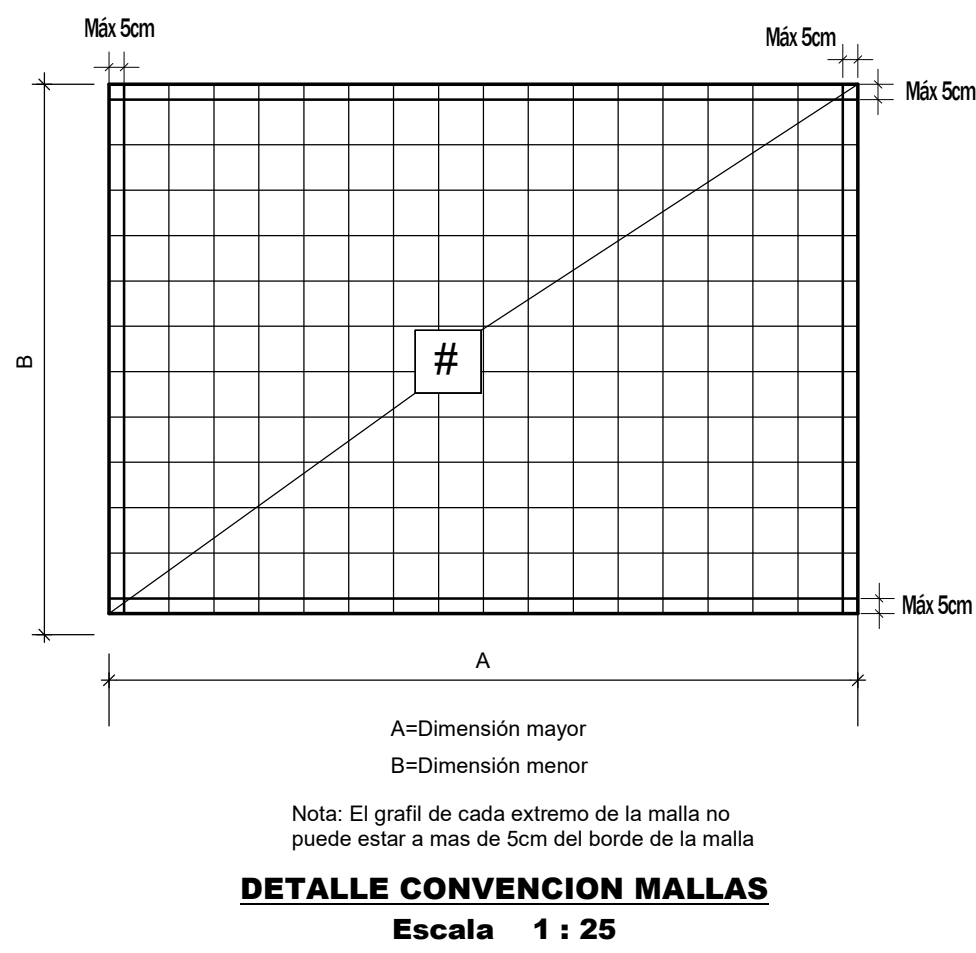

CUADRO DE MALLAS REFUERZO SUPERIOR PISO TIPO 3 (PISO 22 A PISO 28)								
TIPO	A (m)	B(m)	ÁREA (m²)	CANT.	REFUERZO		PESO / MALLA (Kg/m²)	PESO (Kg)
					REFUERZO A	REFUERZO B		
1	3.15	1.45	5 m²	4	Ø6.0mm c/0.15	Ø6.0mm c/0.15	2.993	55
2	2.70	1.05	3 m²	4	Ø6.0mm c/0.15	Ø6.0mm c/0.15	2.993	34
3	2.90	2.35	7 m²	4	Ø6.0mm c/0.15	Ø6.0mm c/0.15	2.993	82
4	5.50	2.35	13 m²	2	Ø6.0mm c/0.15	Ø6.0mm c/0.15	2.993	77
5	5.75	2.35	14 m²	4	Ø6.0mm c/0.15	Ø6.0mm c/0.15	3.518	190
6	4.45	2.35	10 m²	2	Ø6.0mm c/0.15	Ø6.0mm c/0.15	2.993	63
7	3.75	2.35	9 m²	2	Ø6.0mm c/0.15	Ø6.0mm c/0.15	2.993	53
8	6.00	2.35	14 m²	4	Ø6.5mm c/0.15	Ø6.5mm c/0.15	3.518	198
9	2.60	1.70	4 m²	2	Ø6.5mm c/0.15	Ø6.5mm c/0.15	3.518	31
10	6.00	1.70	10 m²	4	Ø6.5mm c/0.15	Ø6.5mm c/0.15	3.518	144
11	2.80	2.35	7 m²	2	Ø6.5mm c/0.15	Ø6.5mm c/0.15	3.518	46
12	2.85	1.30	4 m²	4	Ø6.5mm c/0.15	Ø6.5mm c/0.15	3.518	52
13	1.90	1.70	3 m²	2	Ø6.0mm c/0.15	Ø6.0mm c/0.15	2.993	19
14	2.90	1.00	3 m²	4	Ø6.5mm c/0.15	Ø6.5mm c/0.15	3.518	41
15	4.30	1.60	7 m²	4	Ø6.0mm c/0.15	Ø6.0mm c/0.15	2.993	82
16	3.85	1.60	6 m²	2	Ø6.0mm c/0.15	Ø6.0mm c/0.15	2.993	37
17	3.25	2.35	8 m²	5	Ø7.5mm c/0.15	Ø7.5mm c/0.15	4.674	178
18	3.40	2.35	8 m²	2	Ø7.5mm c/0.15	Ø7.5mm c/0.15	4.674	75
19	4.55	2.35	11 m²	2	Ø6.5mm c/0.15	Ø6.5mm c/0.15	3.518	75
20	3.10	2.20	7 m²	4	Ø6.0mm c/0.15	Ø6.0mm c/0.15	2.993	82
21	5.40	2.30	12 m²	2	Ø6.5mm c/0.15	Ø6.5mm c/0.15	3.518	87
22	5.50	1.60	9 m²	1	Ø6.0mm c/0.15	Ø6.0mm c/0.15	2.993	27
23	5.50	2.35	13 m²	2	Ø6.5mm c/0.15	Ø6.5mm c/0.15	3.518	91
24	3.85	2.35	9 m²	2	Ø7.5mm c/0.15	Ø7.5mm c/0.15	4.674	85
25	2.90	2.35	7 m²	12	Ø6.5mm c/0.15	Ø6.5mm c/0.15	3.518	288
26	3.80	1.00	4 m²	2	Ø6.0mm c/0.15	Ø6.0mm c/0.15	2.993	23
TOTAL : 84				84				2214

CUADRO NIVELES PISO 23 A PISO 28	
PISO	NIVEL(NE.)
PISO 23	58.30
PISO 24	60.95
PISO 25	63.60
PISO 26	66.25
PISO 27	68.90
PISO 28	71.55

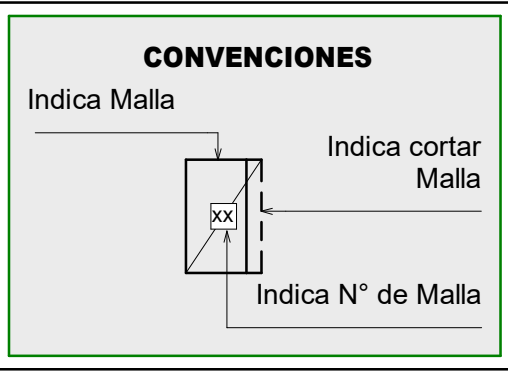

CONVENCIONES	
	Indica dinteles
	Indica placa e=0.10
	Indica placa e=0.12
	Indica placa e=0.15
	Indica muros en concreto e=0.15
	Indica muros en concreto e=0.25
	Indica muros en concreto e=0.30
	Indica muros en concreto e=0.35
	Indica muros en concreto e=0.40

CONCRETO: LOSAS Y DINTELES			
* DE PISO 9 A PISO 8	* DE PISO 8 A PISO 15	* DE PISO 16 A PISO 22	* DE PISO 23 A CUBIERTA ASCENSOR Y ESCALERAS
f'c=35 MPa	f'c=32 MPa	f'c=25 MPa	f'c=21 MPa
f'c=350 kg/cm²	f'c=315 kg/cm²	f'c=245 kg/cm²	f'c=210 kg/cm²
f'c=5000 psi	f'c=4500 psi	f'c=3500 psi	f'c=3000 psi