


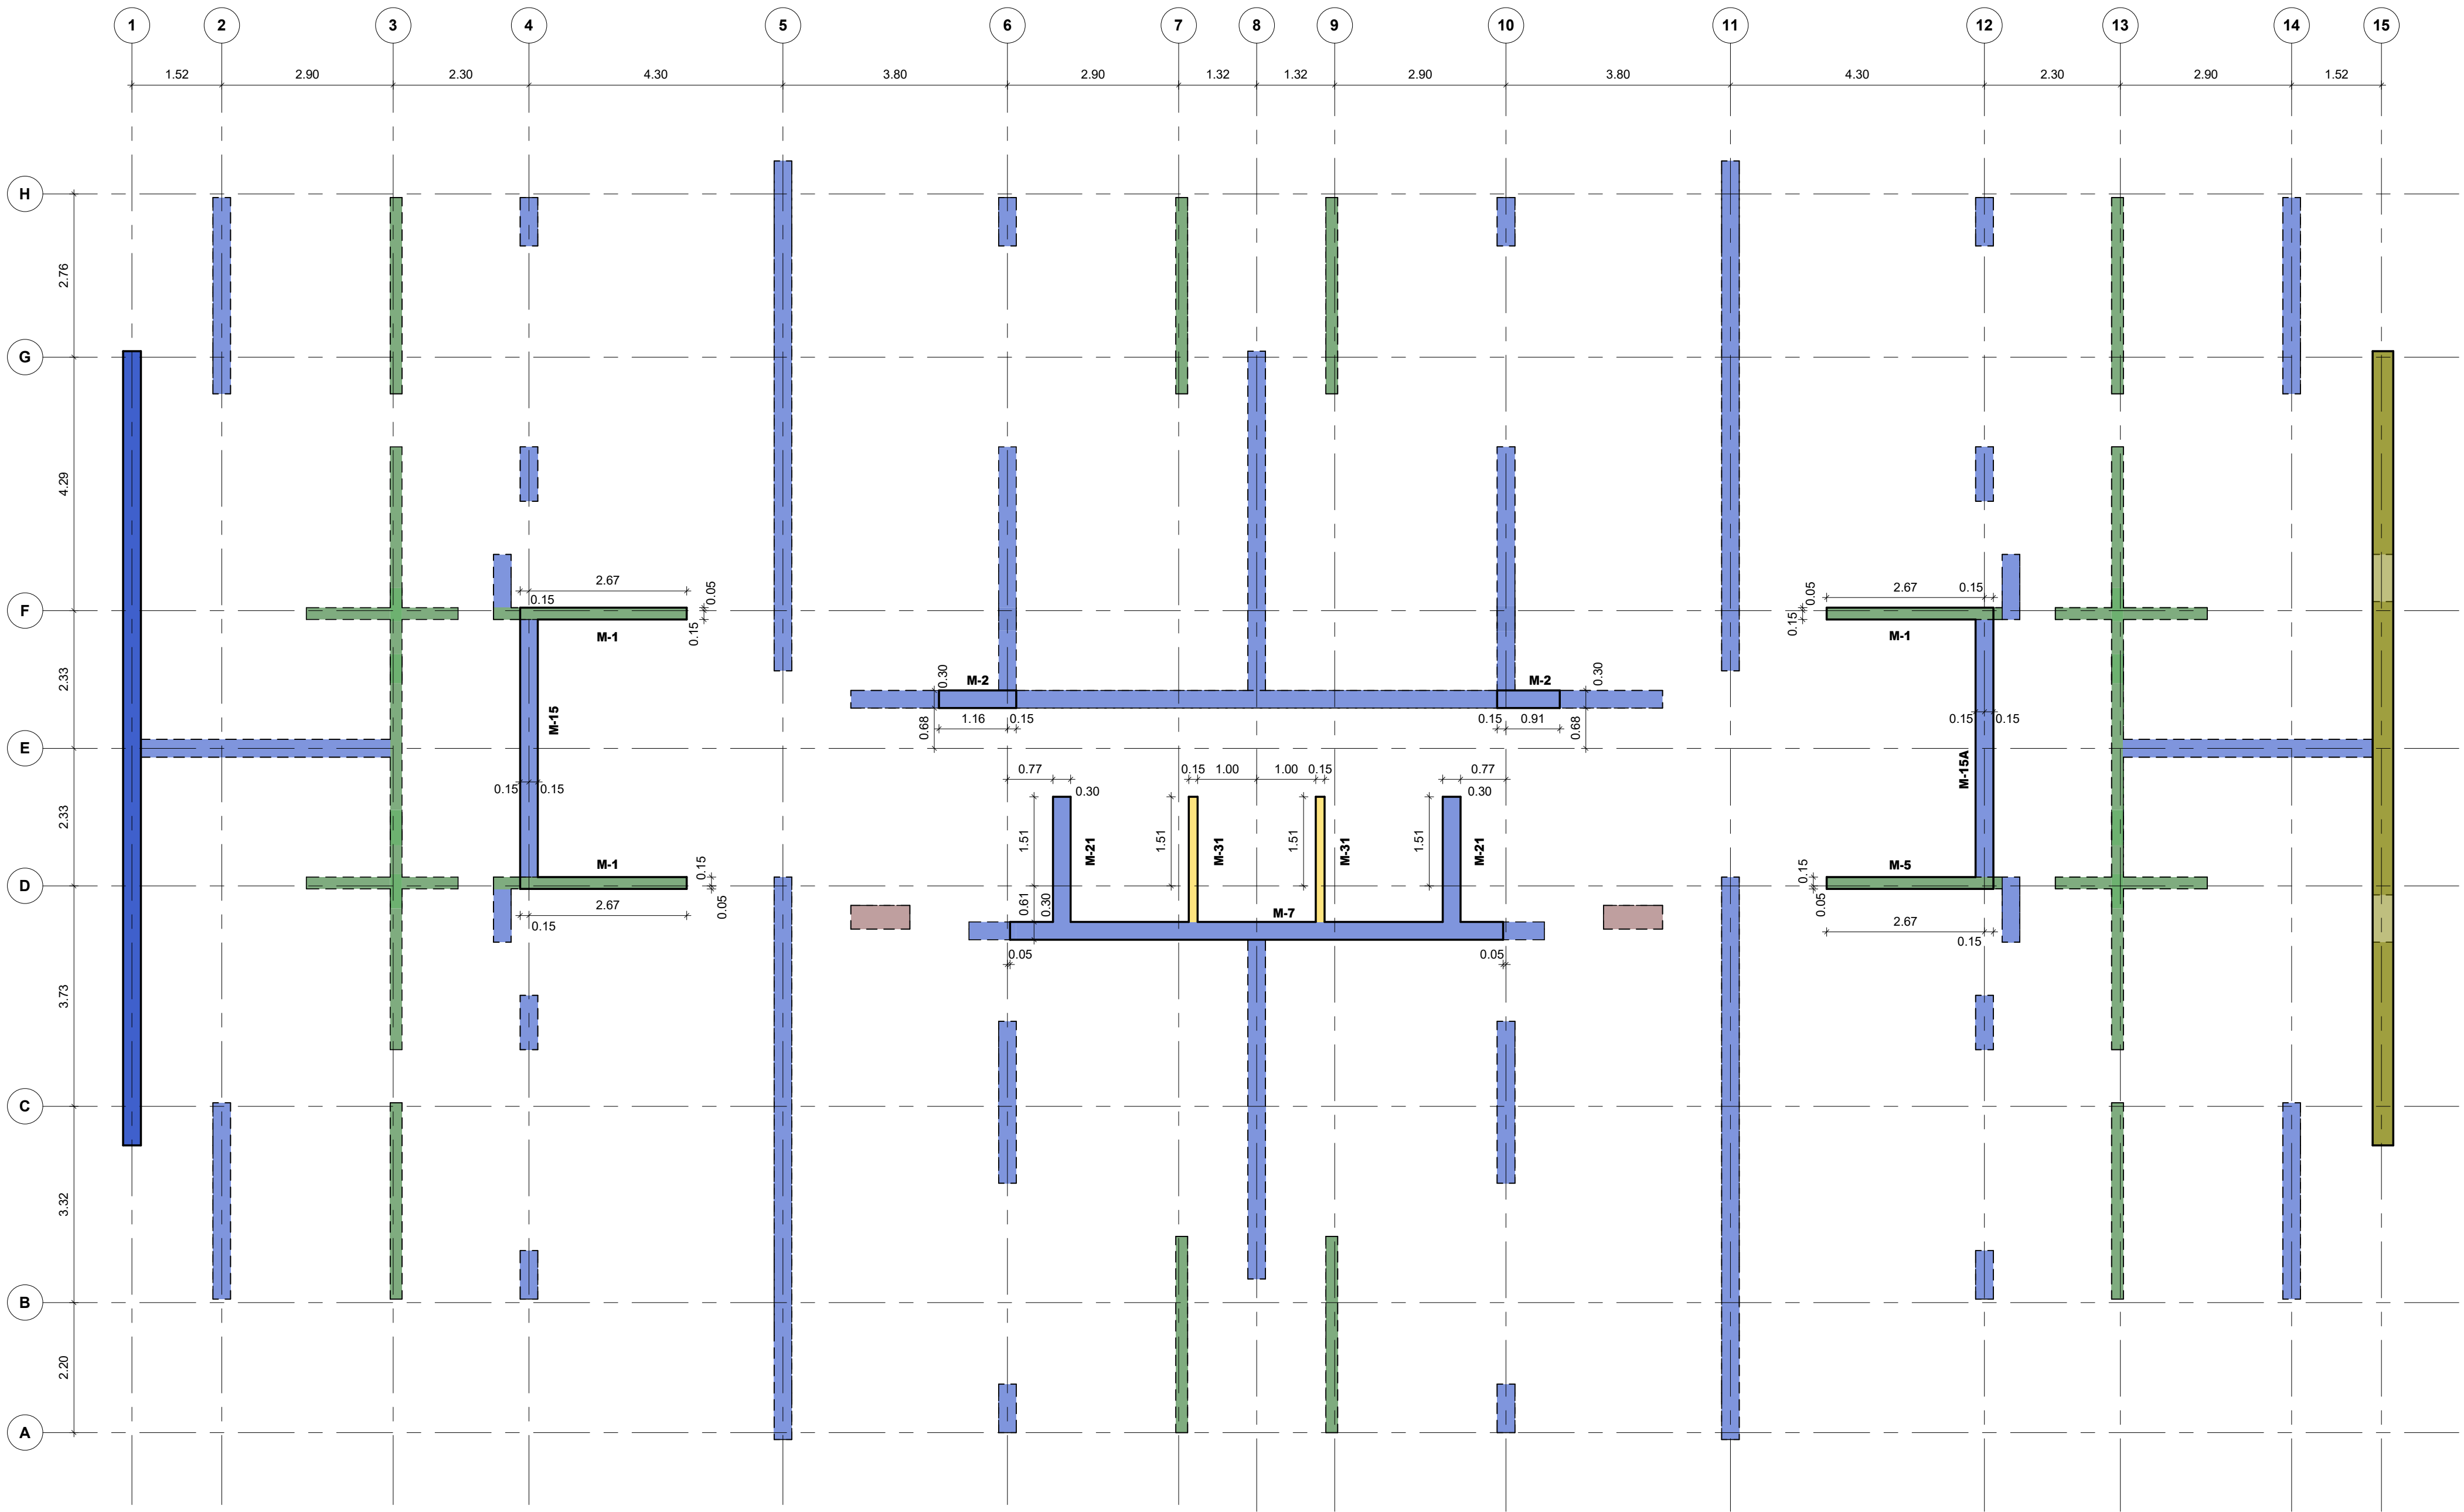

PLANTA LOCALIZACIÓN DE MUROS CUBIERTA
Escala 1 : 75

CONCRETO:			
MUROS			
* DE CIMENTACIÓN A PISO 8	* DE PISO 8 A PISO 15	* DE PISO 15 A PISO 22	* DE PISO 22 A CUBIERTA ASCENSOR Y ESCALERAS
f_c=49 MPa	f_c=42 MPa	f_c=35 MPa	f_c=28 MPa
f_c=490 kg/cm²	f_c=420 kg/cm²	f_c=350 kg/cm²	f_c=280 kg/cm²
f_c=7000 psi	f_c=6000 psi	f_c=5000 psi	f_c=4000 psi

CONVENCIONES	
M-#	Indica N° de Muro
	Indica muro e=0.15
	Indica muro e=0.20
	Indica muro e=0.30
	Indica muro e=0.40
	Indica muro e=0.35 que muere
	Indica muro e=0.25 que muere
	Indica muro e=0.30 que muere
	Indica muro e=0.40 que muere
NOTAS	
1. Ver detalles generales en PL. N°01.02	
2. Ver despieces de muros en PL. N° 11.00 a PL. N°11.21	
3. Ver detalles de muros en PL. N° 11.22	

MODIFICACIONES	FECHA
Emisión Inicial	28-02-2025
Ajuste longitud muro M-2 eje 6	26-02-2026



LA SCALA

LA SCALA_EST_TOR-1

TORRE 1

CALLE 170 CON AV. BOYACA

PLANTA LOCALIZACIÓN DE MUROS DE CUBIERTA

LA SCALA_EST_TOR-1_09.00_LCM-CUB