


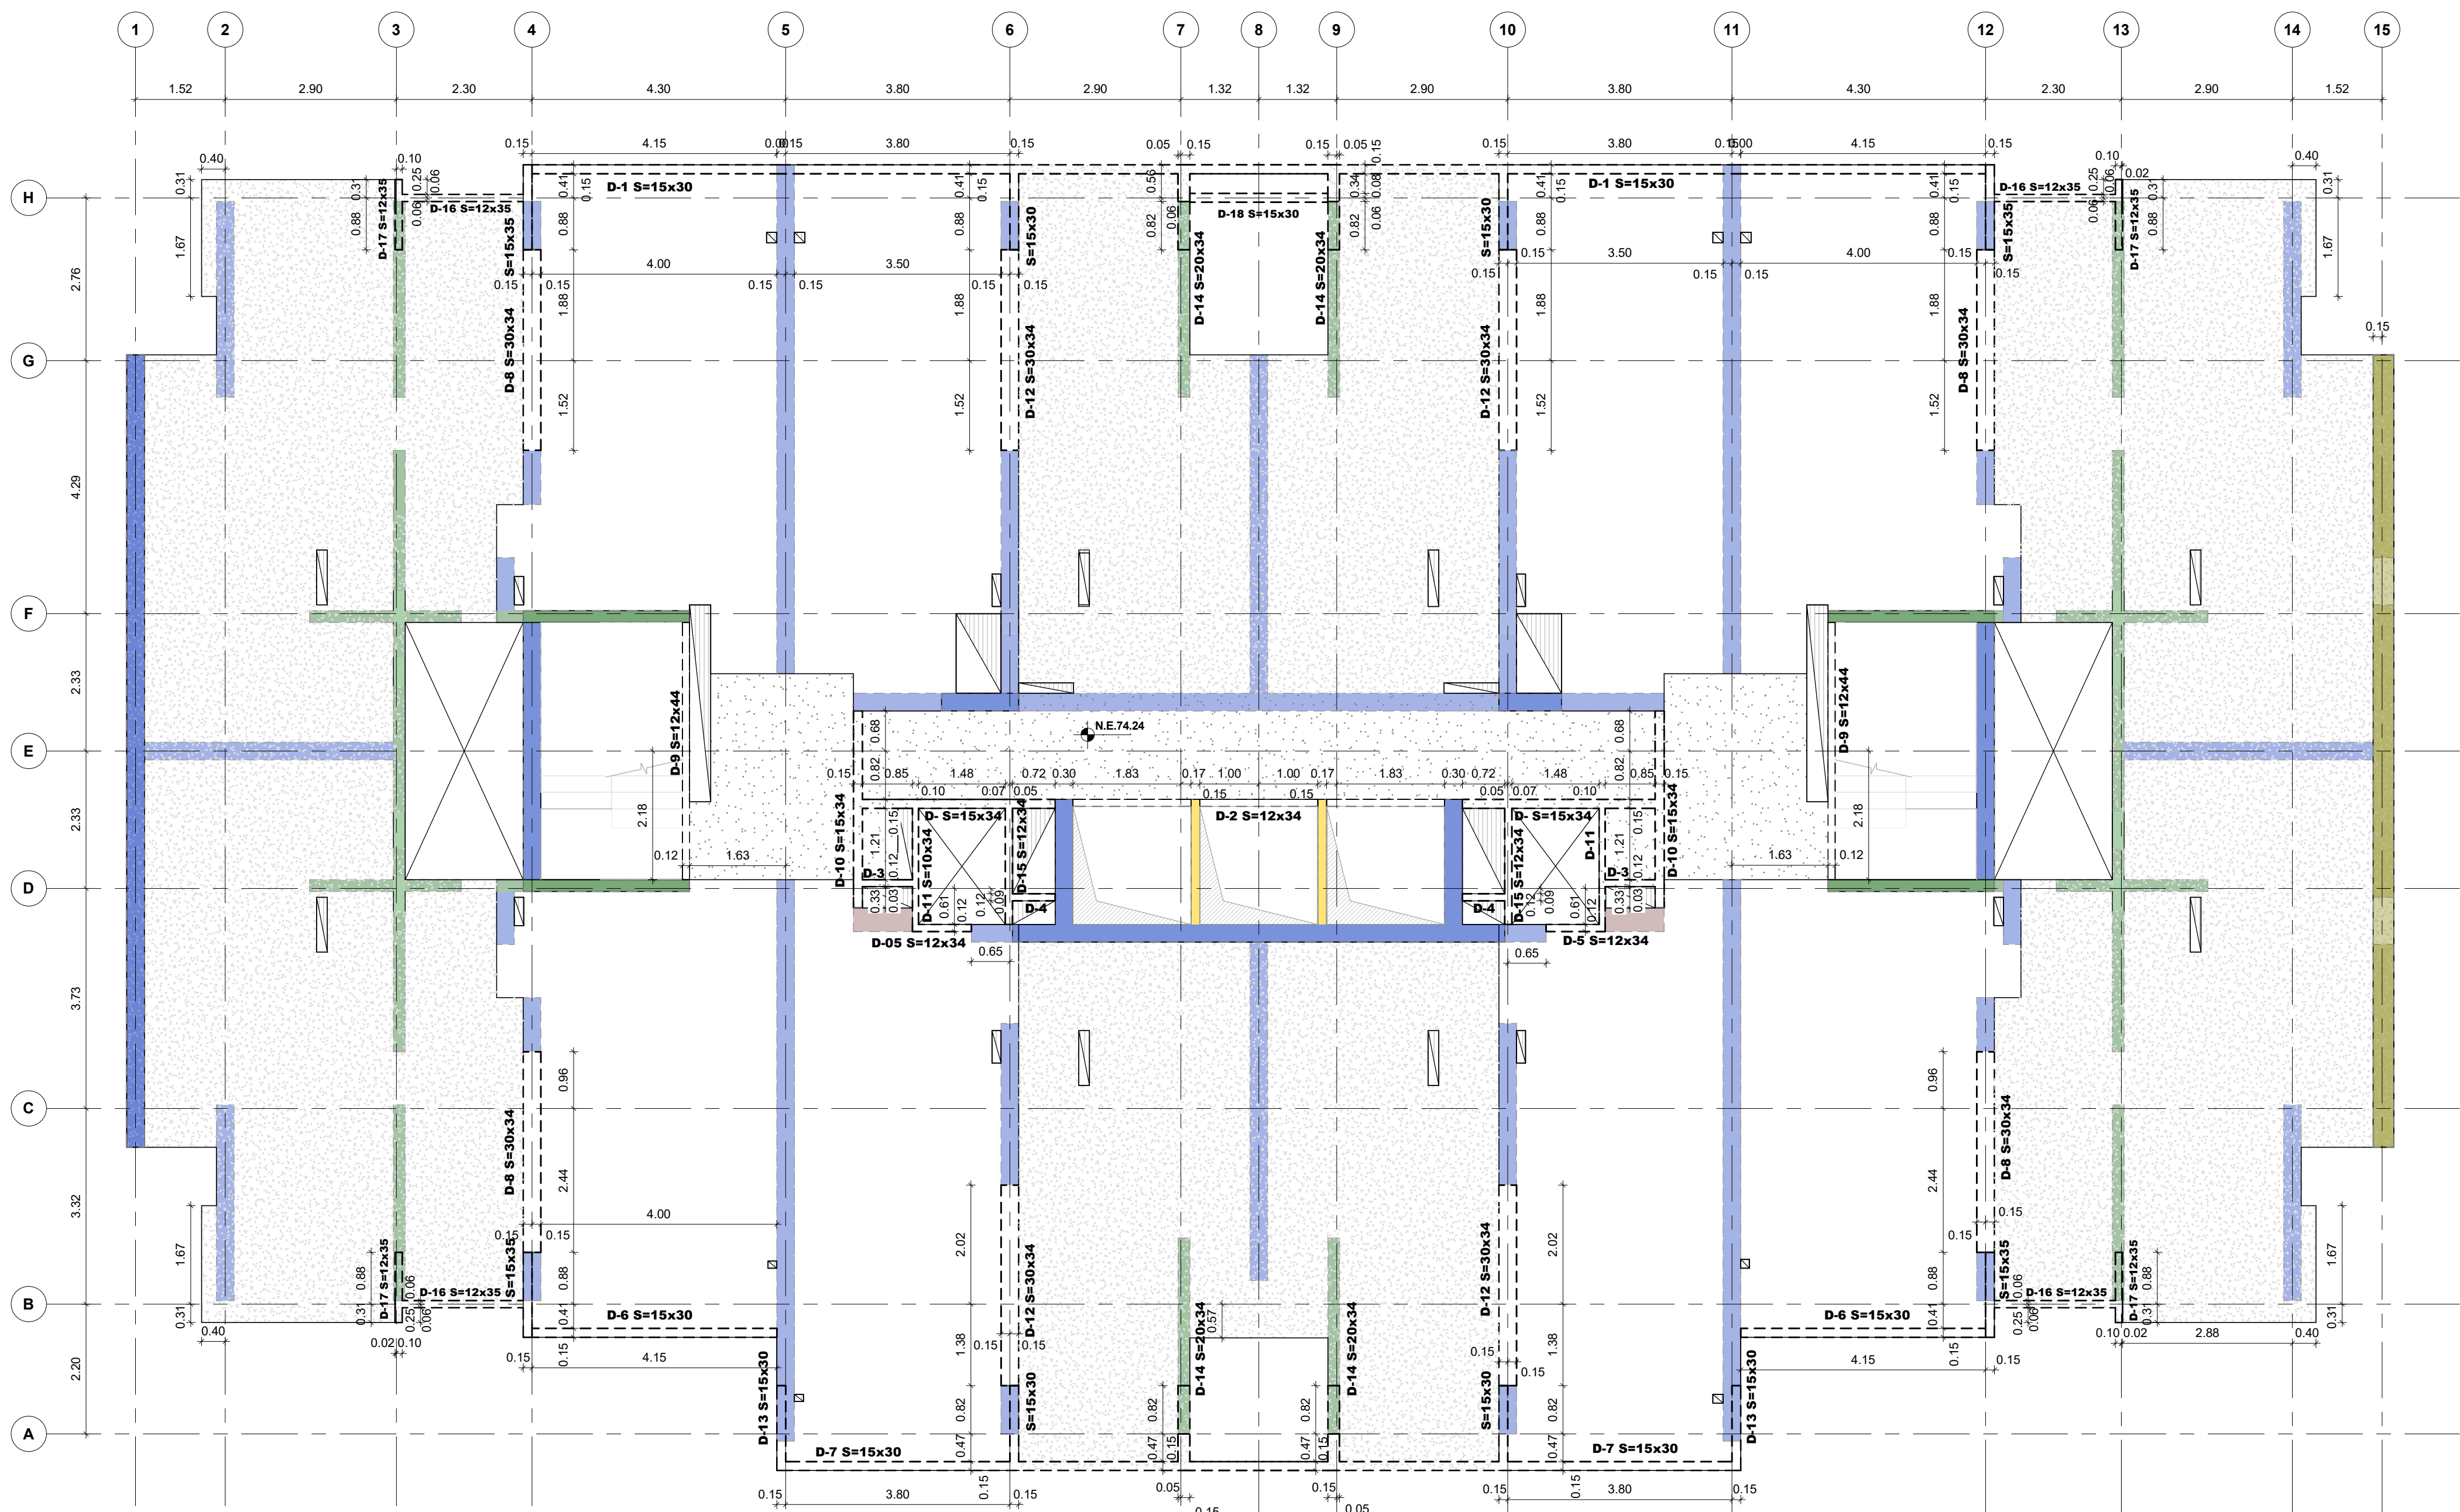

PLANTA LOCALIZACIÓN DE DINTELES CUBIERTA
Escala 1 : 75

CONCRETO:			
LOSAS Y DINTELES			
* DE PISO 1 A PISO 8	* DE PISO 9 A PISO 15	* DE PISO 16 A PISO 22	* DE PISO 23 A CUBIERTA ASCENSOR Y ESCALERAS
f_c=35 MPa	f_c=32 MPa	f_c=25 MPa	f_c=21 MPa
f_c=350 kg/cm²	f_c=315 kg/cm²	f_c=245 kg/cm²	f_c=210 kg/cm²
f_c=5000 psi	f_c=4500 psi	f_c=3500 psi	f_c=3000 psi

CONVENCIONES	
	Indica dinteles
D-#	Indica N° de dintel
	Indica muro e=0.15
	Indica muro e=0.20
	Indica muro e=0.30
	Indica muro e=0.40
	Indica muro e=0.35 que muere
	Indica muro e=0.25 que muere
	Indica muro e=0.30 que muere
	Indica muro e=0.40 que muere
	Indica placa e=0.14
	Indica placa e=0.16
	Indica placa e=0.19
NOTAS	
1. Ver detalles generales en PL. N°01.02	
2. Ver despieces de dinteles en PL N° 10.00 a 10.04	

VERSIÓN :

2

PLANO N°

09.01

GERENTE DE PROYECTO
ROBERTO AYCARDI F.
MAT. 2520257258 CND

INGENIERO
CARLOS ANDRÉS WILCHES C.

MODELADOR
DANIEL CASTELLANOS

MODIFICACIONES		FECHA
Emisión Inicial		28-02-2025
Ajuste dinteles		26-02-2026



LA SCALA

LA SCALA_EST_TOR-1

TORRE 1

CALLE 170 CON AV. BOYACA

PLANTA LOCALIZACIÓN E IDENTIFICACIÓN
DE DINTELES DE CUBIERTA

LA SCALA_EST_TOR-1_09.01_LDINT-CUB

REVISOR ESTRUCTURAL

RAMÓN ÁNDRES ALVAREZ MANTILLA
MAT. 25202-346546 CND.

PLANO N°

09.01

VERSIÓN :

2

