




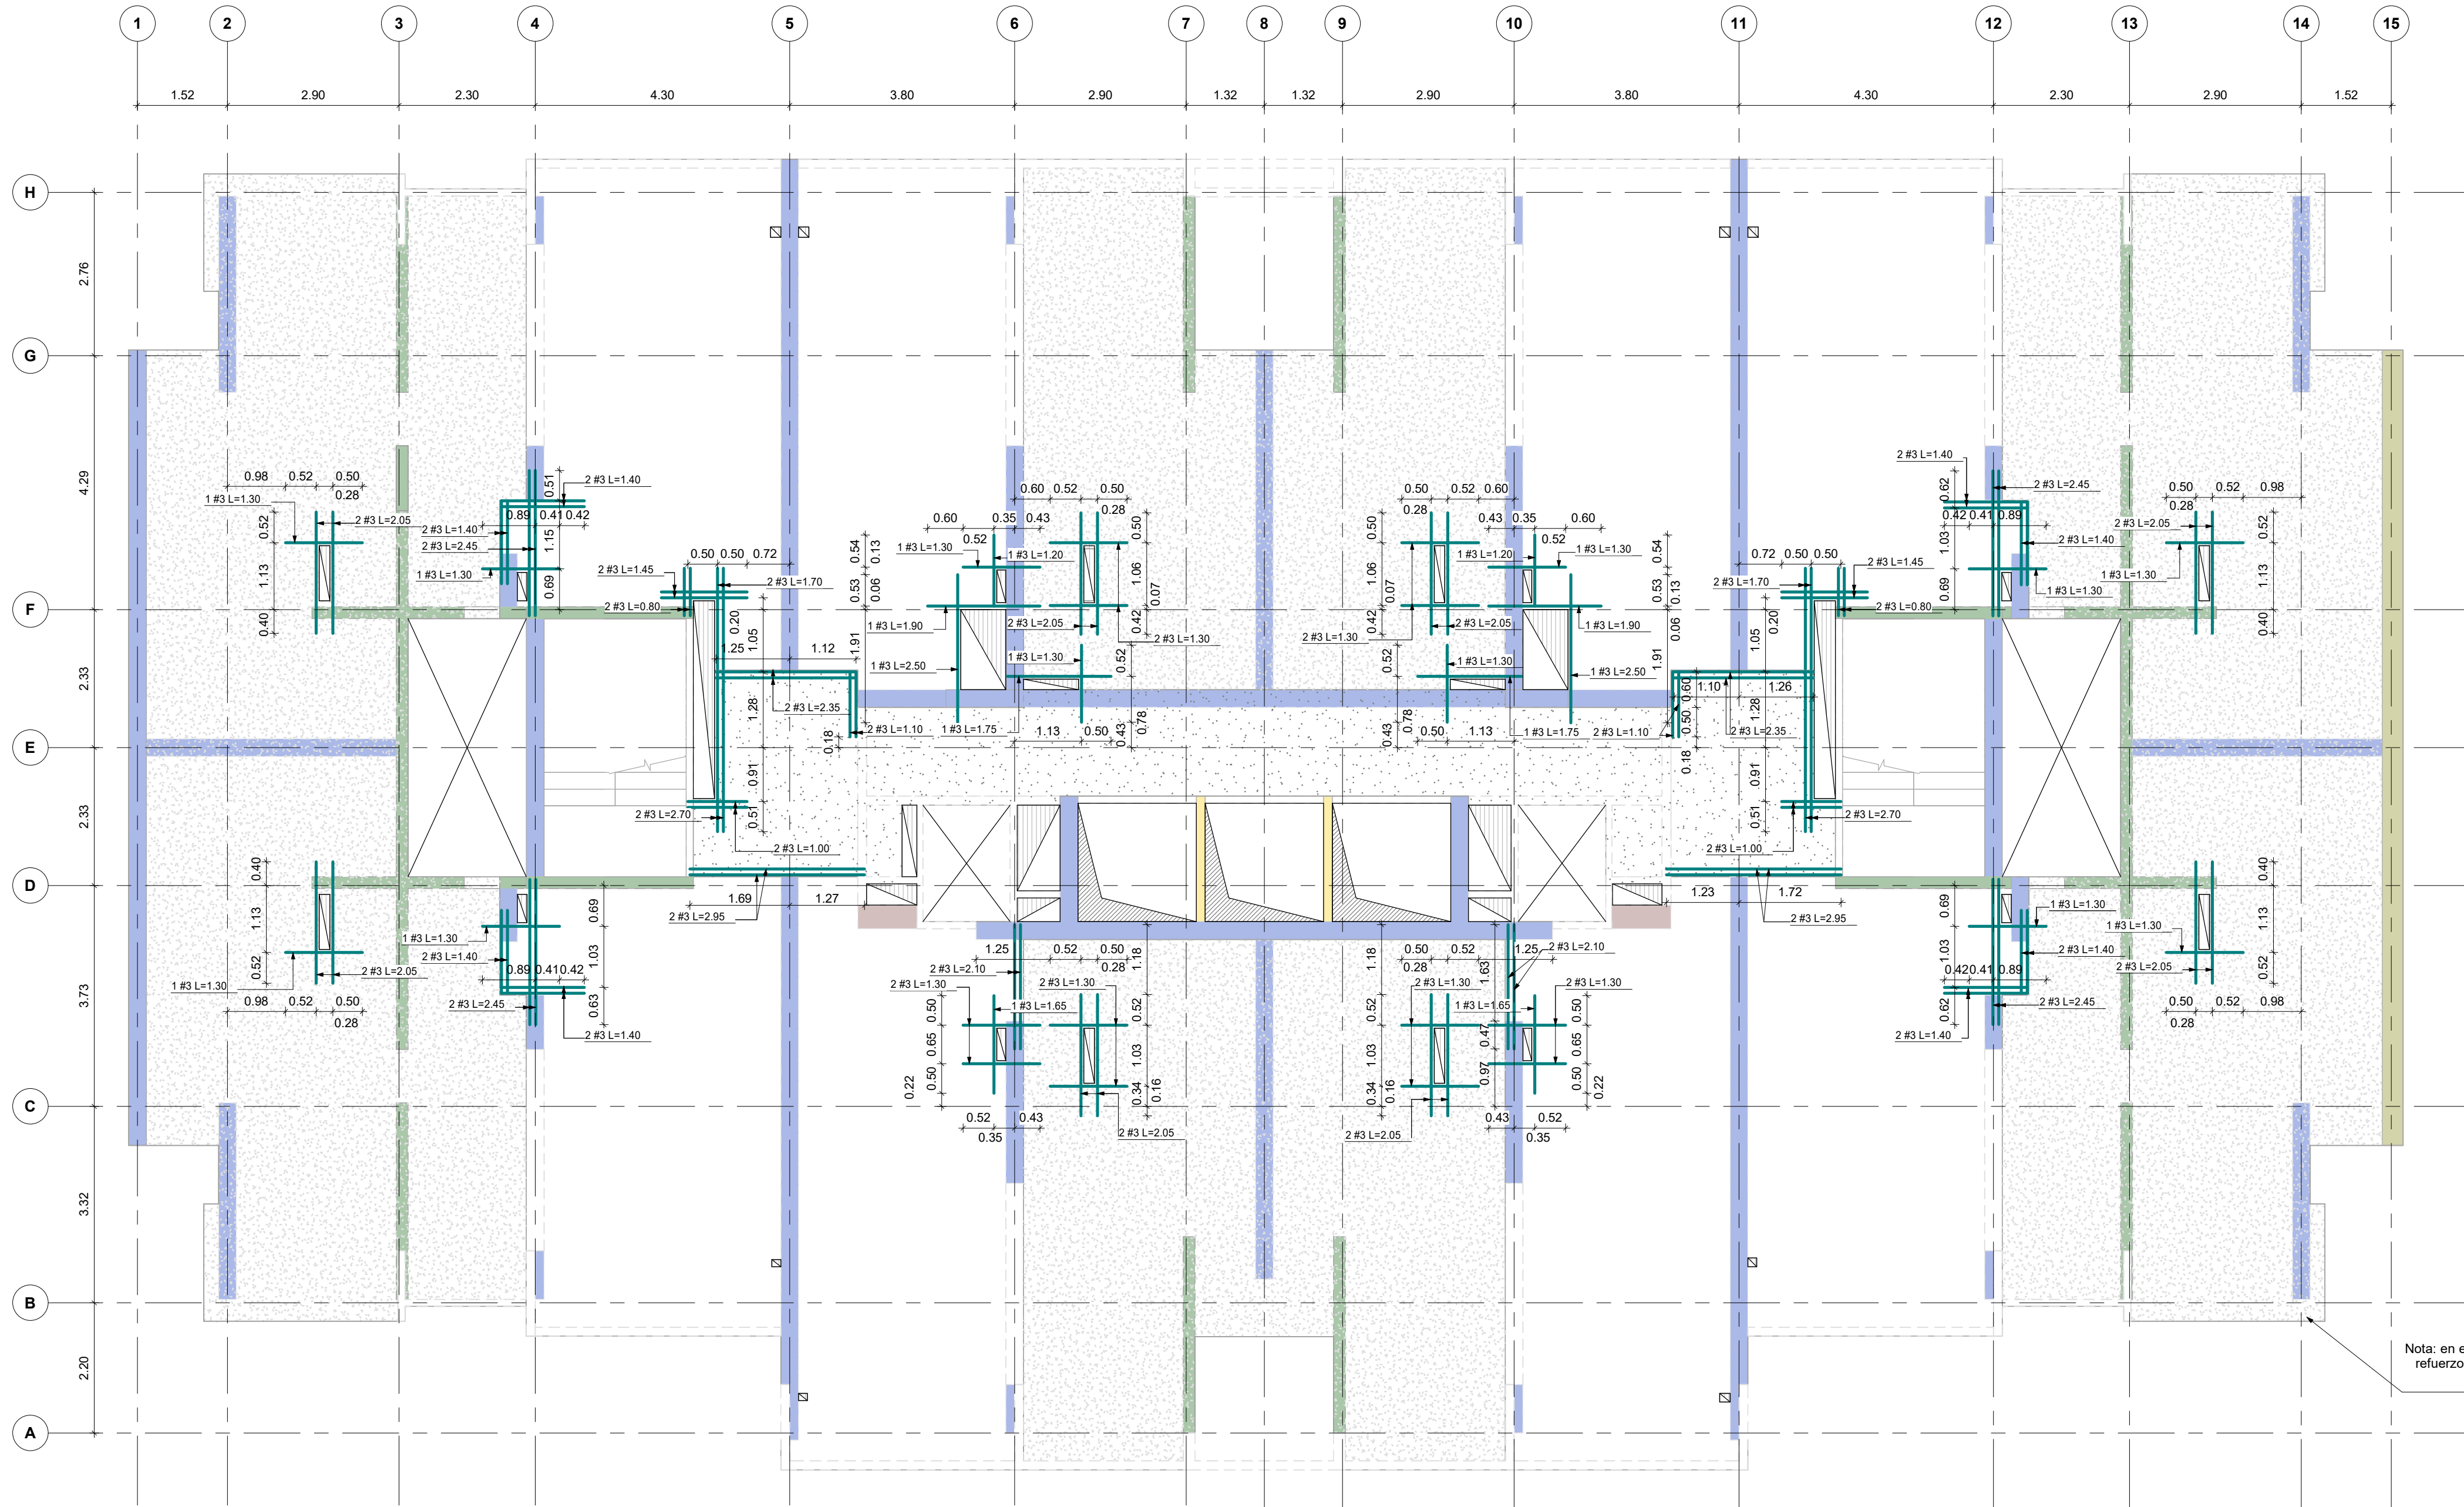


PLANTA DE REFUERZO ADICIONAL (INFERIOR Y SUPERIOR) CUBIERTA
Escala 1 : 75


Nota: en el perímetro del piso tener en cuenta
refuerzo indicado en plano N° 13.00 - Muros
de fachada

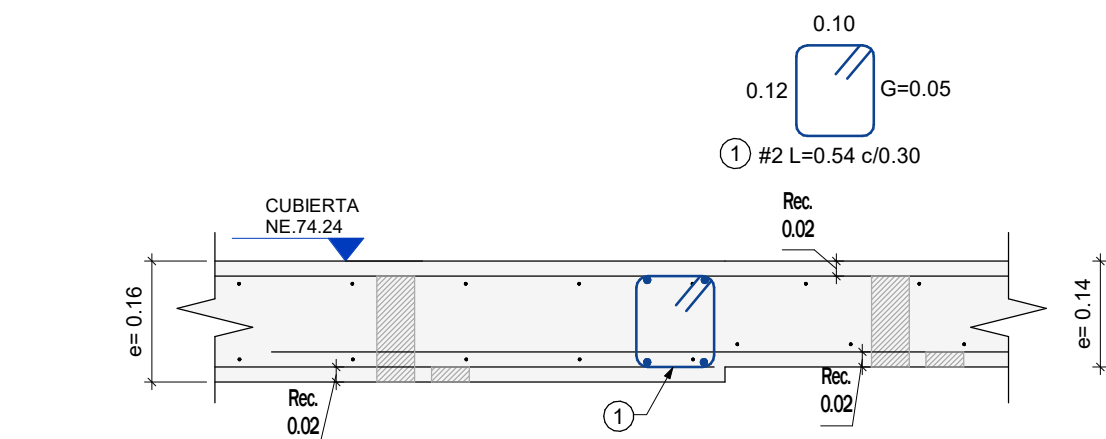


Es obligatorio el uso de distanciador para
garantizar la correcta posición del refuerzo

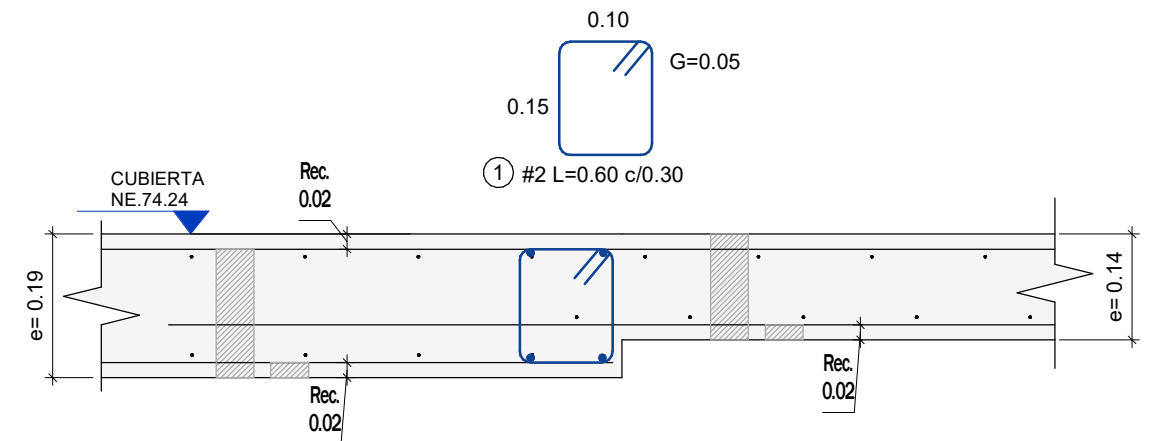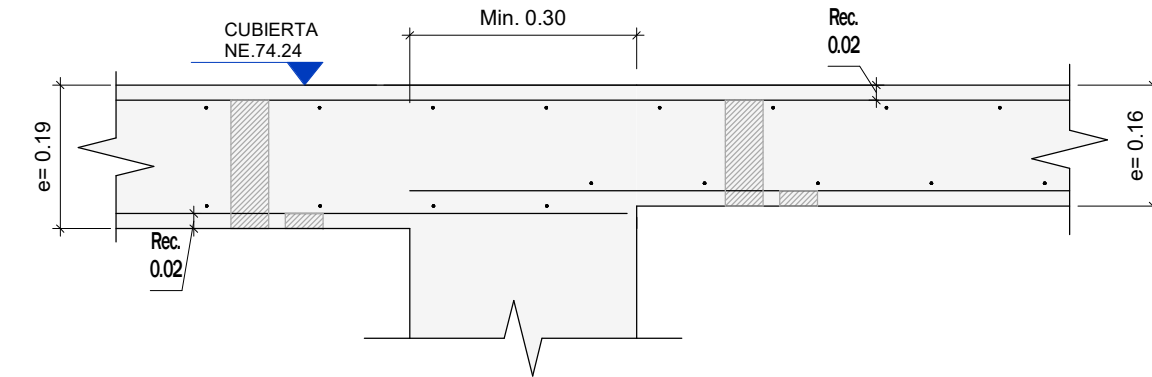


DETALLES TÍPICOS - CAMBIO DE SECCIÓN
Escala 1 : 10

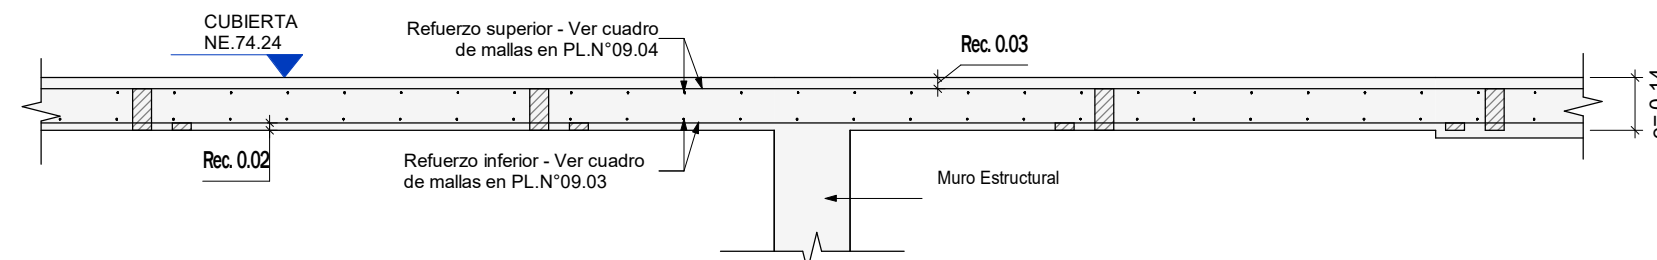


CORTE TÍPICO PLACA AÉREA e=0.14
Escala 1 : 20

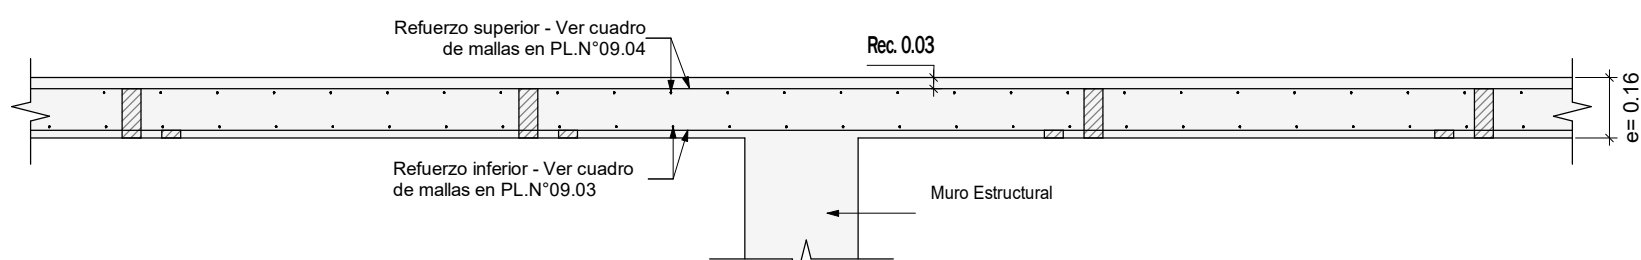

CORTE TÍPICO PLACA AÉREA e=0.16
Escala 1 : 20

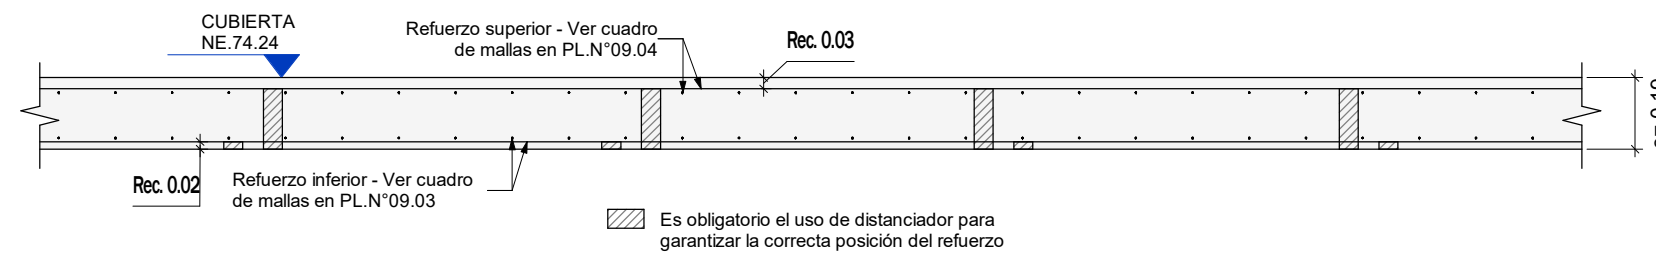

CORTE TÍPICO PLACA AÉREA e=0.19
Escala 1 : 20

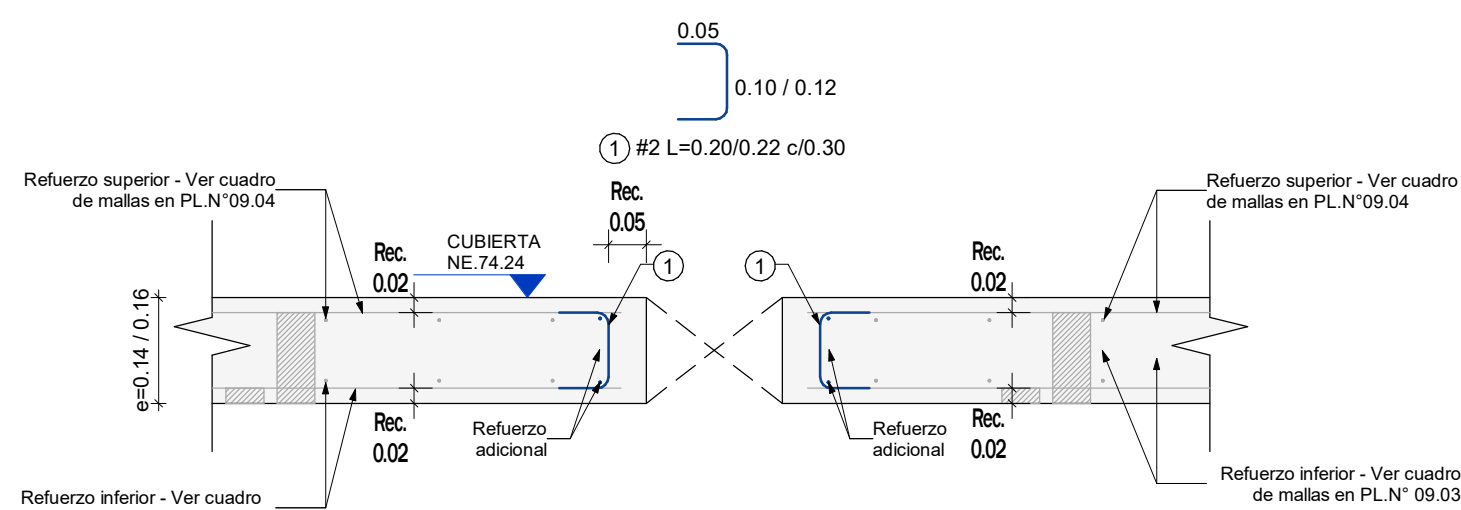

DETALLE TÍPICO - UBICACIÓN REFUERZO ADICIONAL
Escala 1 : 10

CONVENCIONES			
	Indica dinteles		Indica placa e=0.14
	Indica placa e=0.16		Indica placa e=0.19
	Indica muro e=0.15		Indica muro e=0.20
	Indica muro e=0.30		Indica muro e=0.40
	Indica muro e=0.35 que muere		Indica muro e=0.25 que muere
	Indica muro e=0.30 que muere		Indica muro e=0.40 que muere

NOTAS:
1. Ver detalles generales en PL. N°01.02
2. Ver planta de localización e identificación de dinteles en PL. N° 09.01
3. Ver despieces de dinteles en PL. N° 10.00 a 10.04

CONCRETO: LOSAS Y DINTELES			
* DE PISO 1 A PISO 8	* DE PISO 9 A PISO 15	* DE PISO 16 A PISO 22	* DE PISO 23 A CUBIERTA ASCENSOR Y ESCALERAS
f'c=35 MPa	f'c=32 MPa	f'c=25 MPa	f'c=21 MPa
f'c=350 kg/cm²	f'c=315 kg/cm²	f'c=245 kg/cm²	f'c=210 kg/cm²
f'c=5000 psi	f'c=4500 psi	f'c=3500 psi	f'c=3000 psi

VERSIÓN :

2

PLANO N°

09.02

GERENTE DE PROYECTO
ROBERTO AYCARDI F.
MAT. 2520257258 CND

INGENIERO
CARLOS ANDRÉS WILCHES C.

MODELADOR
DANIEL CASTELLANOS

MODIFICACIONES	FECHA
Emisión Inicial	28-02-2025
Ajuste borde de placa	26-02-2026



LA SCALA

LA SCALA_EST_TOR-1

TORRE 1

CALLE 170 CON AV. BOYACA

PLANTA DE REFUERZO ADICIONAL
CUBIERTA

LA SCALA_EST_TOR-1_09.02_CUB-RADC

REVISOR ESTRUCTURAL

RAMÓN ANDRÉS ALVAREZ MANTILLA
MAT. 25202-346546 CND.

PLANO N°

VERSIÓN :

09.02

2