



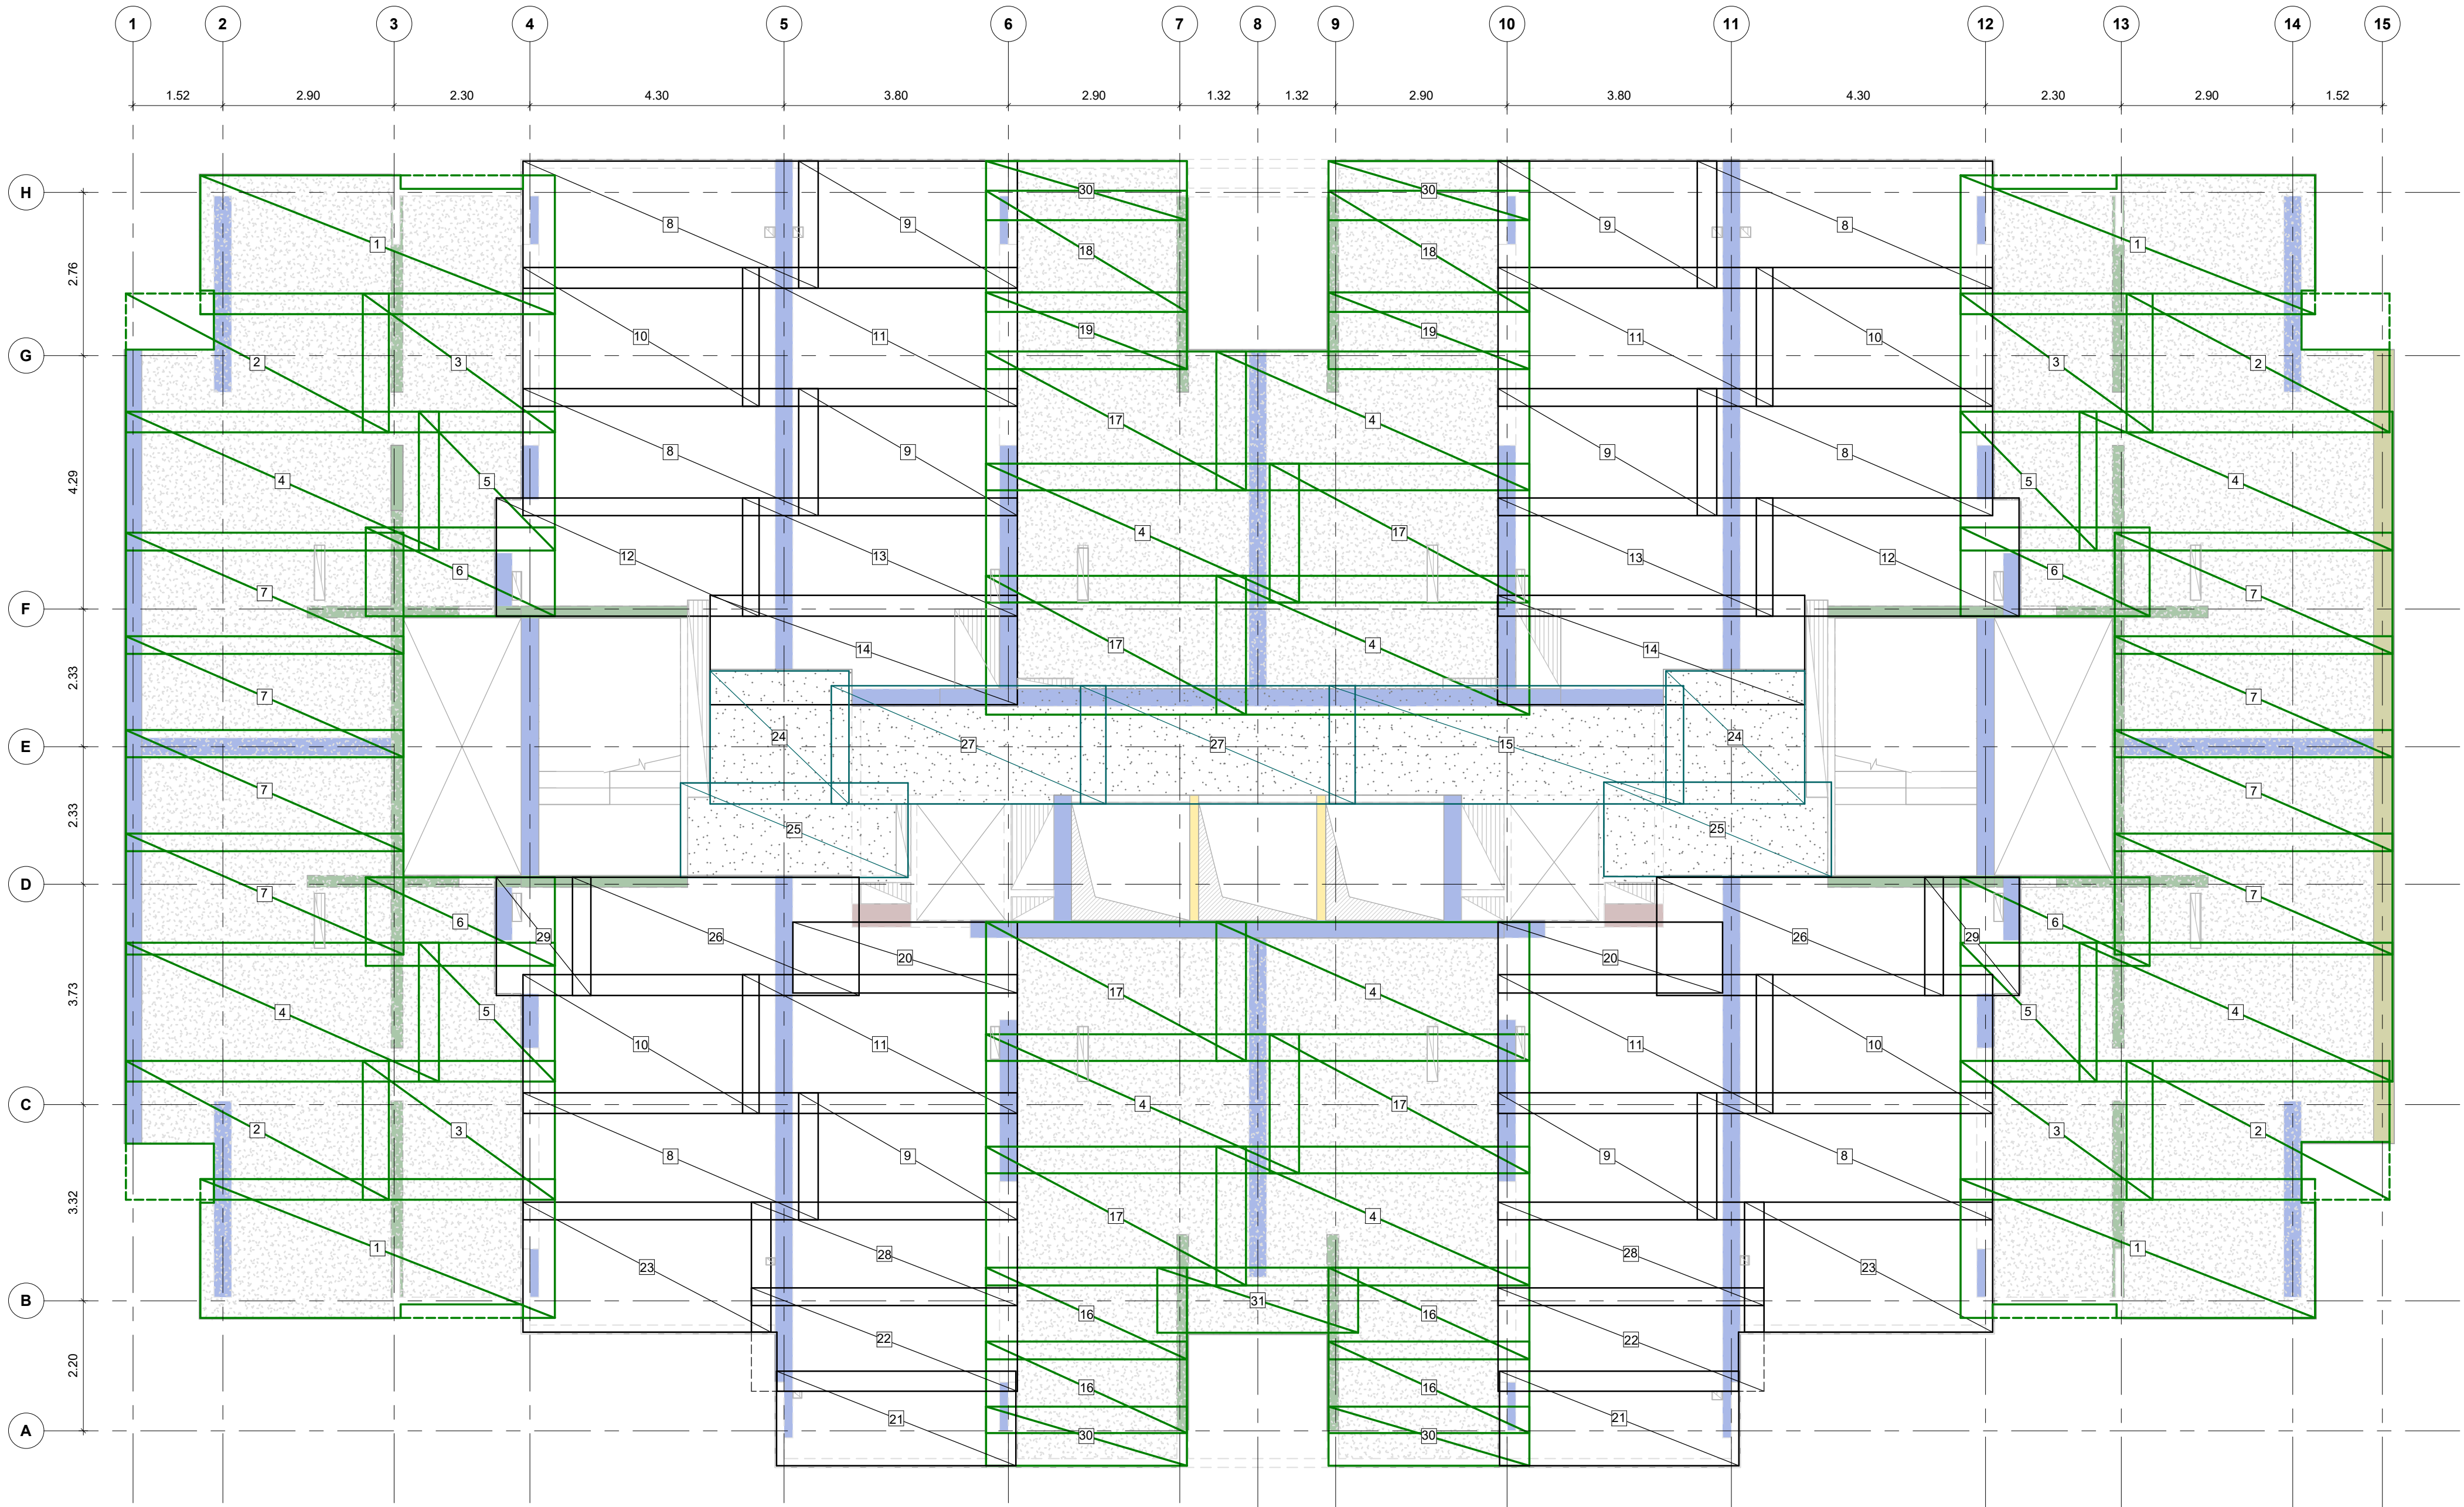


PLANTA DE REFUERZO INFERIOR CUBIERTA N.E. 74.20
Escala 1 : 75

CUADRO DE MALLAS REFUERZO INFERIOR CUBIERTA								
TIPO	A (m)	B(m)	ÁREA (m²)	CANT.	REFUERZO		PESO / MALLA (Kg/m²)	PESO (Kg)
					REFUERZO A	REFUERZO B		
1	6.00	2.35	14 m²	4	Ø7.0mm c/0.15	Ø7.0mm c/0.15	4.071	230
2	4.45	2.35	10 m²	4	Ø7.0mm c/0.15	Ø7.0mm c/0.15	4.071	170
3	3.25	2.35	8 m²	4	Ø7.0mm c/0.15	Ø7.0mm c/0.15	4.071	124
4	5.30	2.35	12 m²	10	Ø7.0mm c/0.15	Ø7.0mm c/0.15	4.071	507
5	2.35	2.30	5 m²	4	Ø7.0mm c/0.15	Ø7.0mm c/0.15	4.071	88
6	3.20	1.50	5 m²	4	Ø7.0mm c/0.15	Ø7.0mm c/0.15	4.071	78
7	4.70	2.05	10 m²	8	Ø7.0mm c/0.15	Ø7.0mm c/0.15	4.071	314
8	5.00	2.15	11 m²	6	Ø7.5mm c/0.15	Ø7.5mm c/0.15	4.674	301
9	3.70	2.15	8 m²	6	Ø7.5mm c/0.15	Ø7.5mm c/0.15	4.674	223
10	4.00	2.35	9 m²	4	Ø7.5mm c/0.15	Ø7.5mm c/0.15	4.674	176
11	4.65	2.35	11 m²	4	Ø7.5mm c/0.15	Ø7.5mm c/0.15	4.674	204
12	4.45	2.00	9 m²	2	Ø7.5mm c/0.15	Ø7.5mm c/0.15	4.674	83
13	4.65	2.00	9 m²	2	Ø7.5mm c/0.15	Ø7.5mm c/0.15	4.674	87
14	5.20	1.85	10 m²	2	Ø7.5mm c/0.15	Ø7.5mm c/0.15	4.674	90
15	6.00	2.00	12 m²	1	Ø8.5mm c/0.15	Ø8.5mm c/0.15	6.007	72
16	3.40	1.55	5 m²	4	Ø7.0mm c/0.15	Ø7.0mm c/0.15	4.071	86
17	4.40	2.35	10 m²	6	Ø7.0mm c/0.15	Ø7.0mm c/0.15	4.071	253
18	3.40	2.05	7 m²	2	Ø7.0mm c/0.15	Ø7.0mm c/0.15	4.071	57
19	3.40	1.30	4 m²	2	Ø7.0mm c/0.15	Ø7.0mm c/0.15	4.071	36
20	3.80	1.20	5 m²	2	Ø7.5mm c/0.15	Ø7.5mm c/0.15	4.674	43
21	4.05	1.60	6 m²	2	Ø7.5mm c/0.15	Ø7.5mm c/0.15	4.674	61
22	4.50	1.75	8 m²	2	Ø7.5mm c/0.15	Ø7.5mm c/0.15	4.674	74
23	4.20	2.20	9 m²	2	Ø7.5mm c/0.15	Ø7.5mm c/0.15	4.674	86
24	2.35	2.25	5 m²	2	Ø8.5mm c/0.15	Ø8.5mm c/0.15	6.007	64
25	3.85	1.60	6 m²	2	Ø8.5mm c/0.15	Ø8.5mm c/0.15	6.007	74
26	4.85	2.00	10 m²	2	Ø7.5mm c/0.15	Ø7.5mm c/0.15	3.518	68
27	4.65	2.00	9 m²	2	Ø8.5mm c/0.15	Ø8.5mm c/0.15	6.007	112
28	4.50	1.75	8 m²	2	Ø7.5mm c/0.15	Ø7.5mm c/0.15	4.674	74
29	1.60	2.00	3 m²	2	Ø7.5mm c/0.15	Ø7.5mm c/0.15	3.518	23
30	3.40	1.00	3 m²	4	Ø7.0mm c/0.15	Ø7.0mm c/0.15	4.071	55
31	3.40	1.10	4 m²	1	Ø7.0mm c/0.15	Ø7.0mm c/0.15	4.071	15
TOTAL : 104				104				3927

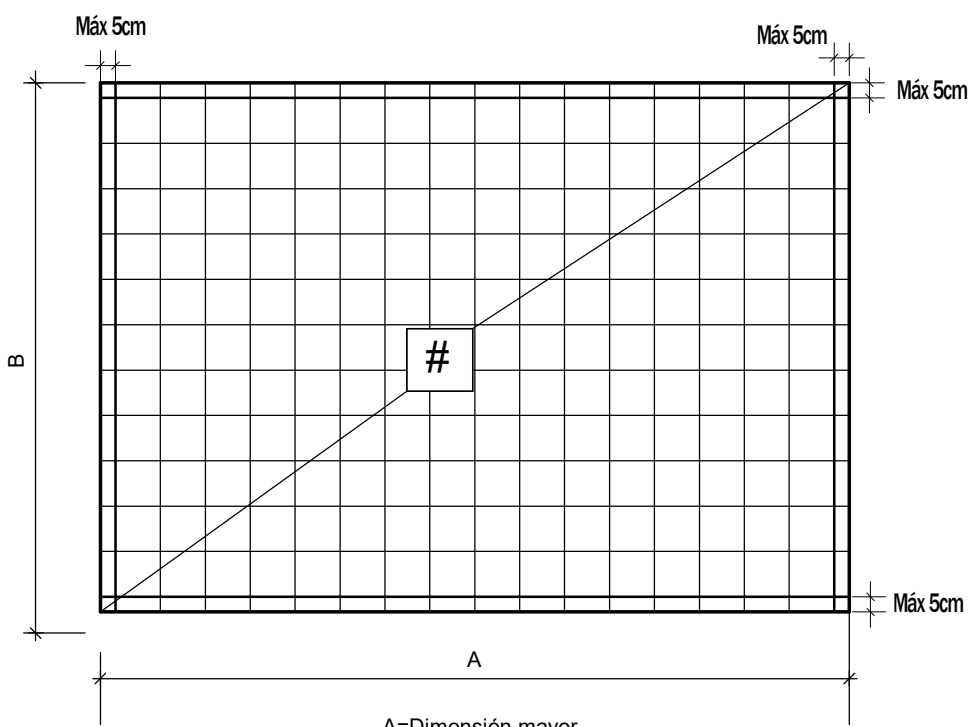

DETALLE CONVENCION MALLAS
Escala 1 : 25

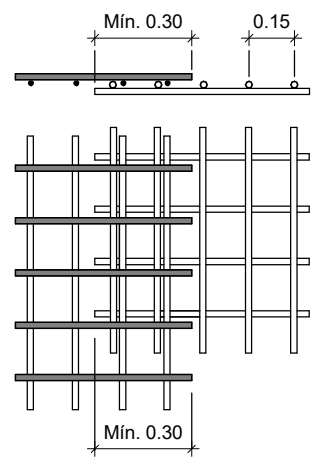

DETALLE TRASLAPO MALLAS
Escala 1 : 25

NOTAS:
1. Ver detalles generales en el PL. N° 01.02
2. Ver planta de refuerzo adicional en PL. N° 09.02
3. Ver planta de refuerzo superior en PL. N° 09.04
4. Las dimensiones de las mallas deben ser verificadas por el constructor.

CONCRETO: LOSAS Y DITELES			
* DE PISO 1 A PISO 8	* DE PISO 9 A PISO 15	* DE PISO 16 A PISO 22	* DE PISO 23 A CUBIERTA ASCENSOR Y ESCALERAS
f_c=35 MPa	f_c=32 MPa	f_c=25 MPa	f_c=21 MPa
f_c=350 kg/cm²	f_c=315 kg/cm²	f_c=245 kg/cm²	f_c=210 kg/cm²
f_c=5000 psi	f_c=4500 psi	f_c=3500 psi	f_c=3000 psi

CONVENCIONES	
Indica Malla	Indica cortar Malla
Indica N° de Malla	

CONVENCIONES	
Indica dinteles	Indica placa e=0.14
Indica placa e=0.16	Indica placa e=0.19
Indica muros en concreto e=0.15	Indica muros en concreto e=0.30
Indica muros en concreto e=0.35	Indica muros en concreto e=0.40

PLANO N° 09.03

VERSIÓN : 2

GERENTE DE PROYECTO
ROBERTO AYCARDI F.
MAT. 2520257258 CND

INGENIERO
CARLOS ANDRÉS WILCHES C.

MODELADOR
DANIEL CASTELLANOS

MODIFICACIONES	FECHA
Emisión Inicial	28-02-2025
Ajuste borde de placa	26-02-2026



LA SCALA

LA SCALA_EST_TOR-1

TORRE 1

CALLE 170 CON AV. BOYACA

PLANTA DE REFUERZO INFERIOR
CUBIERTA

LA SCALA_EST_TOR-1_09.03_CUB-RINF

REVISOR ESTRUCTURAL

RAMÓN ANDRÉS ALVAREZ MANTILLA
MAT. 25202-346546 CND.

PLANO N°

09.03

VERSIÓN :

2