



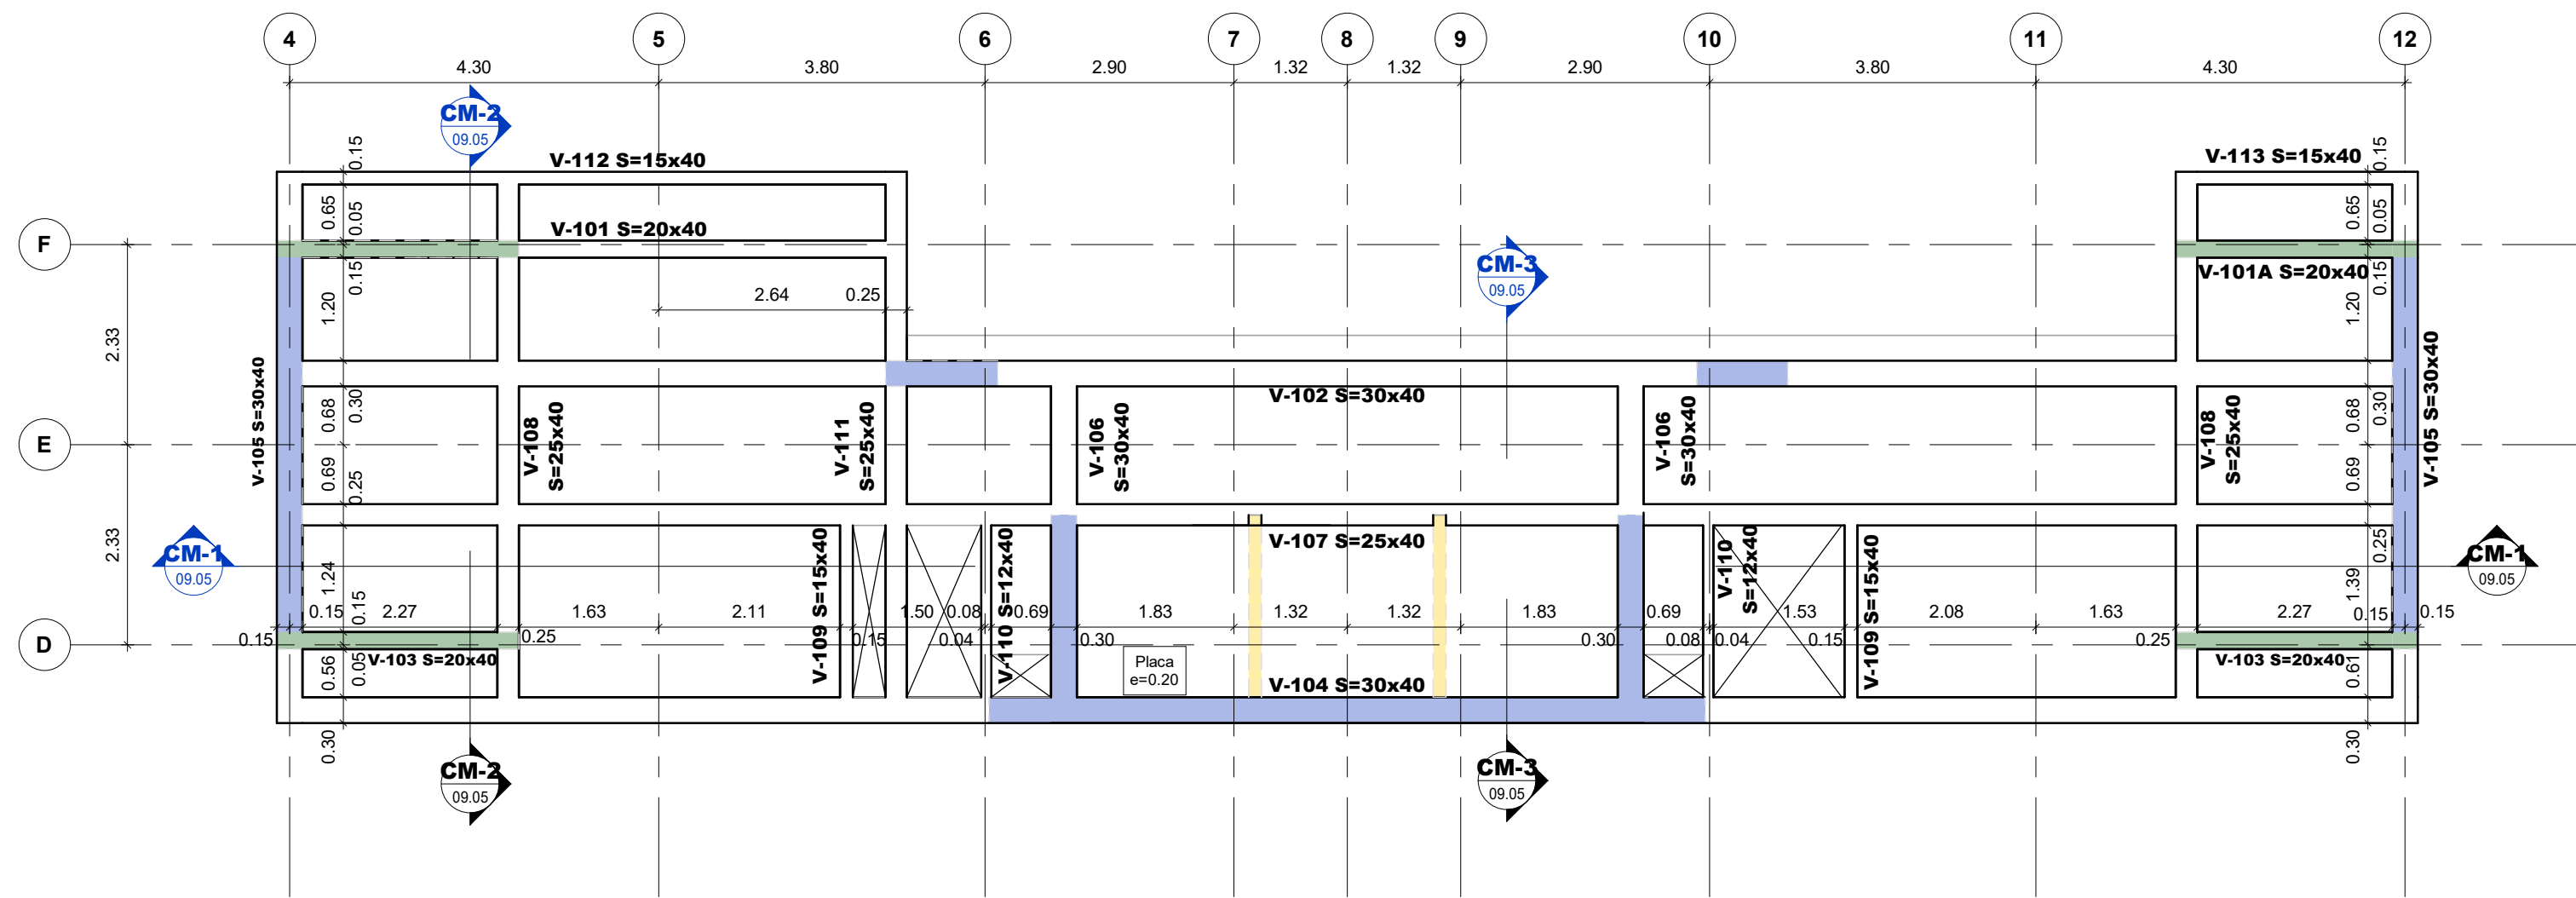


PLANTA CUBIERTA FOSO DE ASCENSOR Y DE ESCALERAS N.E. 76.75
Escala 1 : 75

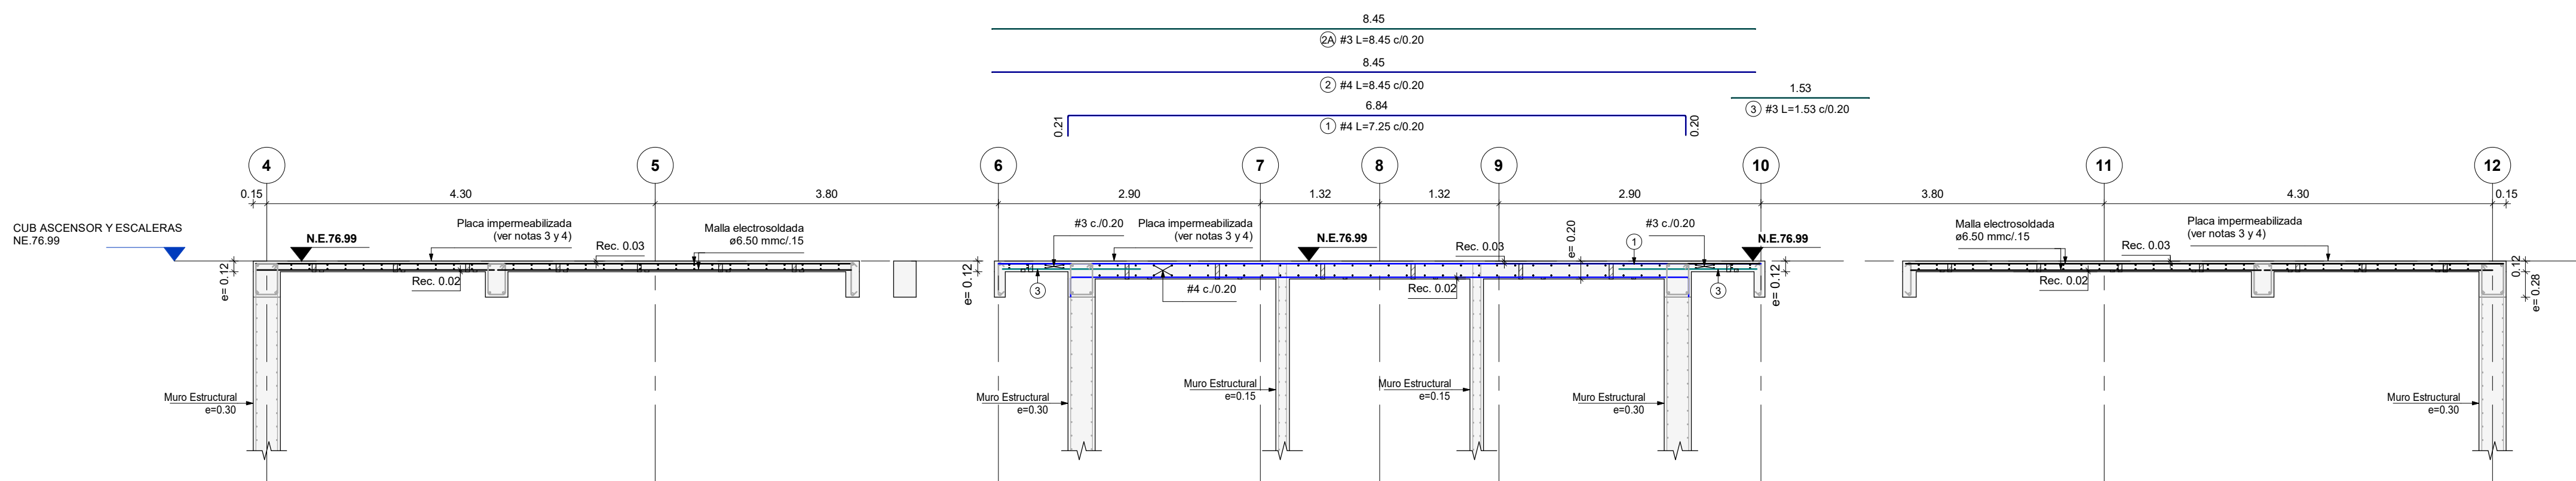


Es obligatorio el uso de separadores, alfileres ó soportes para garantizar la correcta posición del refuerzo.

CORTE CM-1
Escala 1 : 50

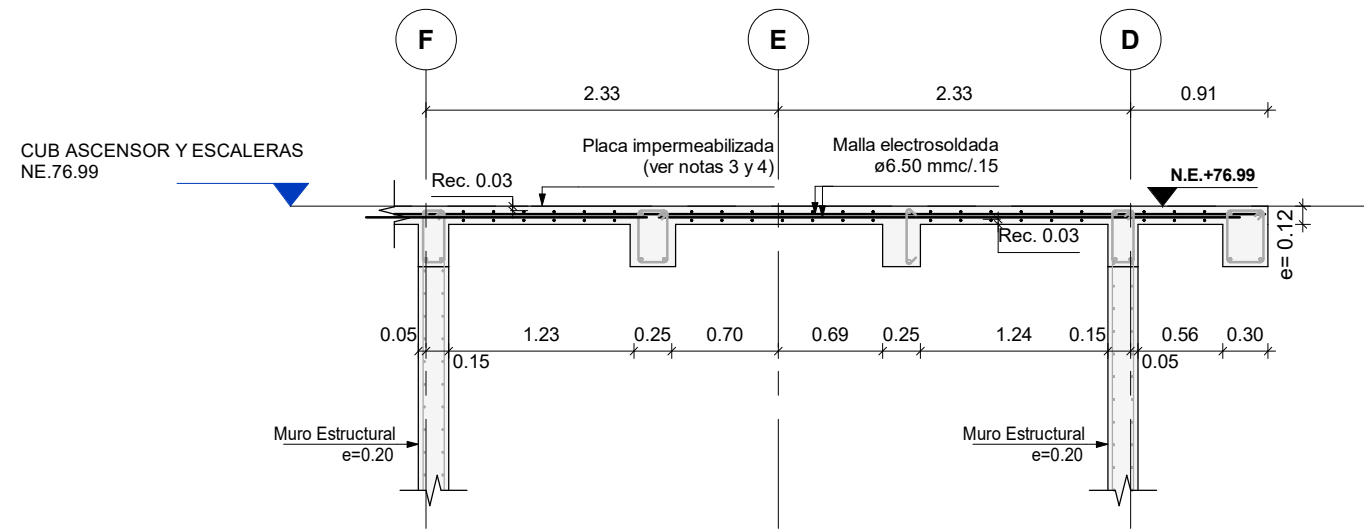


Es obligatorio el uso de separadores, alfileres ó soportes para garantizar la correcta posición del refuerzo.

CORTE CM-2
Escala 1 : 50

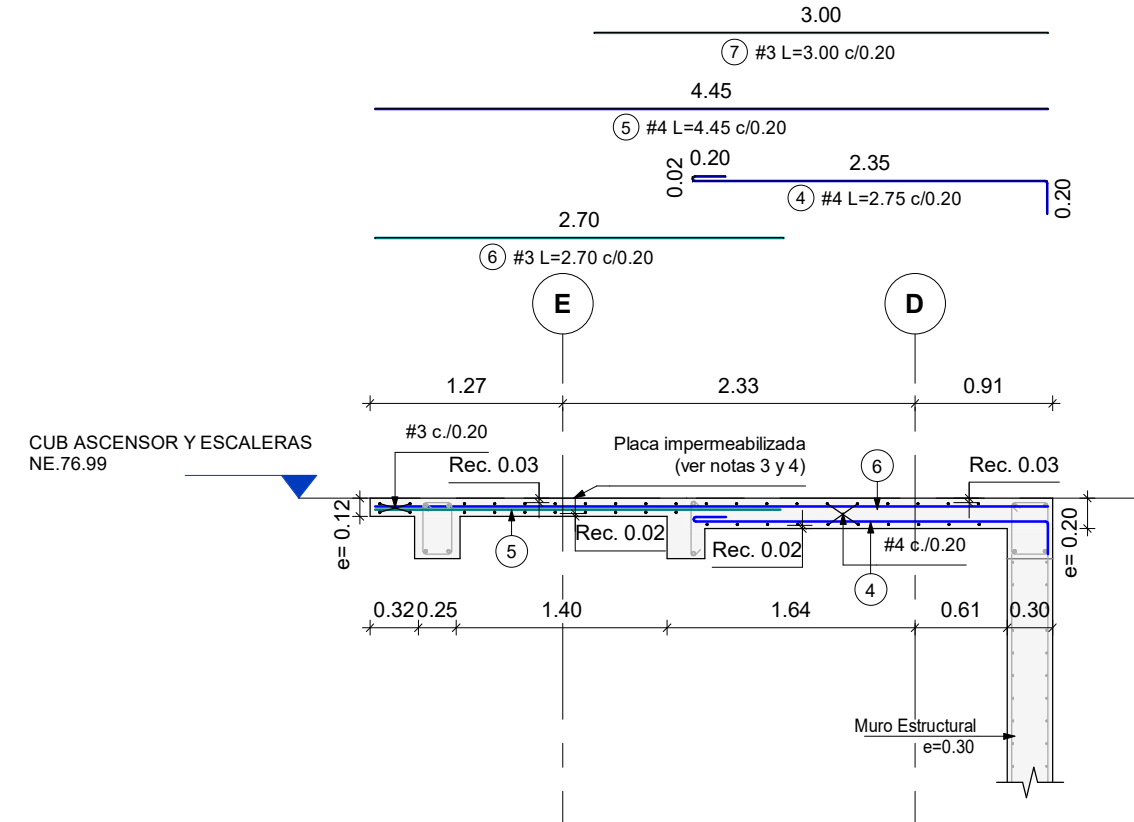

Es obligatorio el uso de separadores, alfileres ó soportes para garantizar la correcta posición del refuerzo.

CORTE CM-3
Escala 1 : 50

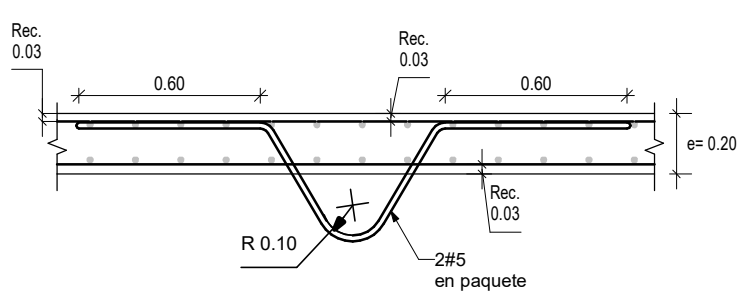

DETALLE GANCHO DE IZAJE ASCENSOR
Escala 1 : 25

CONCRETO:

LOSAS Y DIENTES

* DE PISO 1 A PISO 8	* DE PISO 9 A PISO 15	* DE PISO 16 A PISO 22	* DE PISO 23 A CUBIERTA ASCENSOR Y ESCALERAS
f'c=35 MPa f'c=350 kg/cm² f'c=5000 psi	f'c=32 MPa f'c=315 kg/cm² f'c=4500 psi	f'c=25 MPa f'c=245 kg/cm² f'c=3500 psi	f'c=21 MPa f'c=210 kg/cm² f'c=3000 psi

NOTA:

- Ver detalles generales en PL. N° 01.02
- Ver despiece de muros en PL N° 11.00 a 11.21
- Se debe garantizar un tiempo mínimo de curado intensivo de por lo menos 15 días
- Debe estudiarse e implementarse algún sistema de aislamiento térmico de la losa de concreto
- Ver despieces de dinteles en PL N° 10.00 a 10.04

CONVENCIONES

M-#	Indica Tipo de Muro
Indica dinteles	
Indica placa e=0.20	
Indica muro e=0.15 que muere	
Indica muro e=0.25 que muere	
Indica muro e=0.30 que muere	
Indica muro e=0.40 que muere	

VERSIÓN :

2

PLANO N°

09.05



GERENTE DE PROYECTO

ROBERTO AYCARDI F.
MAT. 2520257258 CND

INGENIERO

CARLOS ANDRÉS WILCHES C.

MODELADOR

DANIEL CASTELLANOS

MODIFICACIONES

FECHA

Emisión Inicial	28-02-2025
Actualización borde de placa por cambios arquitectónicos	26-02-2026



LA SCALA

LA SCALA_EST_TOR-1

TORRE 1

CALLE 170 CON AV. BOYACA

PLANTA DE CUBIERTA ASCENSOR Y
CUBIERTA DE ESCALERAS

LA SCALA_EST_TOR-1_09.05_CUB-MAQ

REVISOR ESTRUCTURAL

RAMÓN ANDRÉS ALVAREZ MANTILLA
MAT. 25202-346546 CND.

PLANO N°

09.05

VERSIÓN :

2