


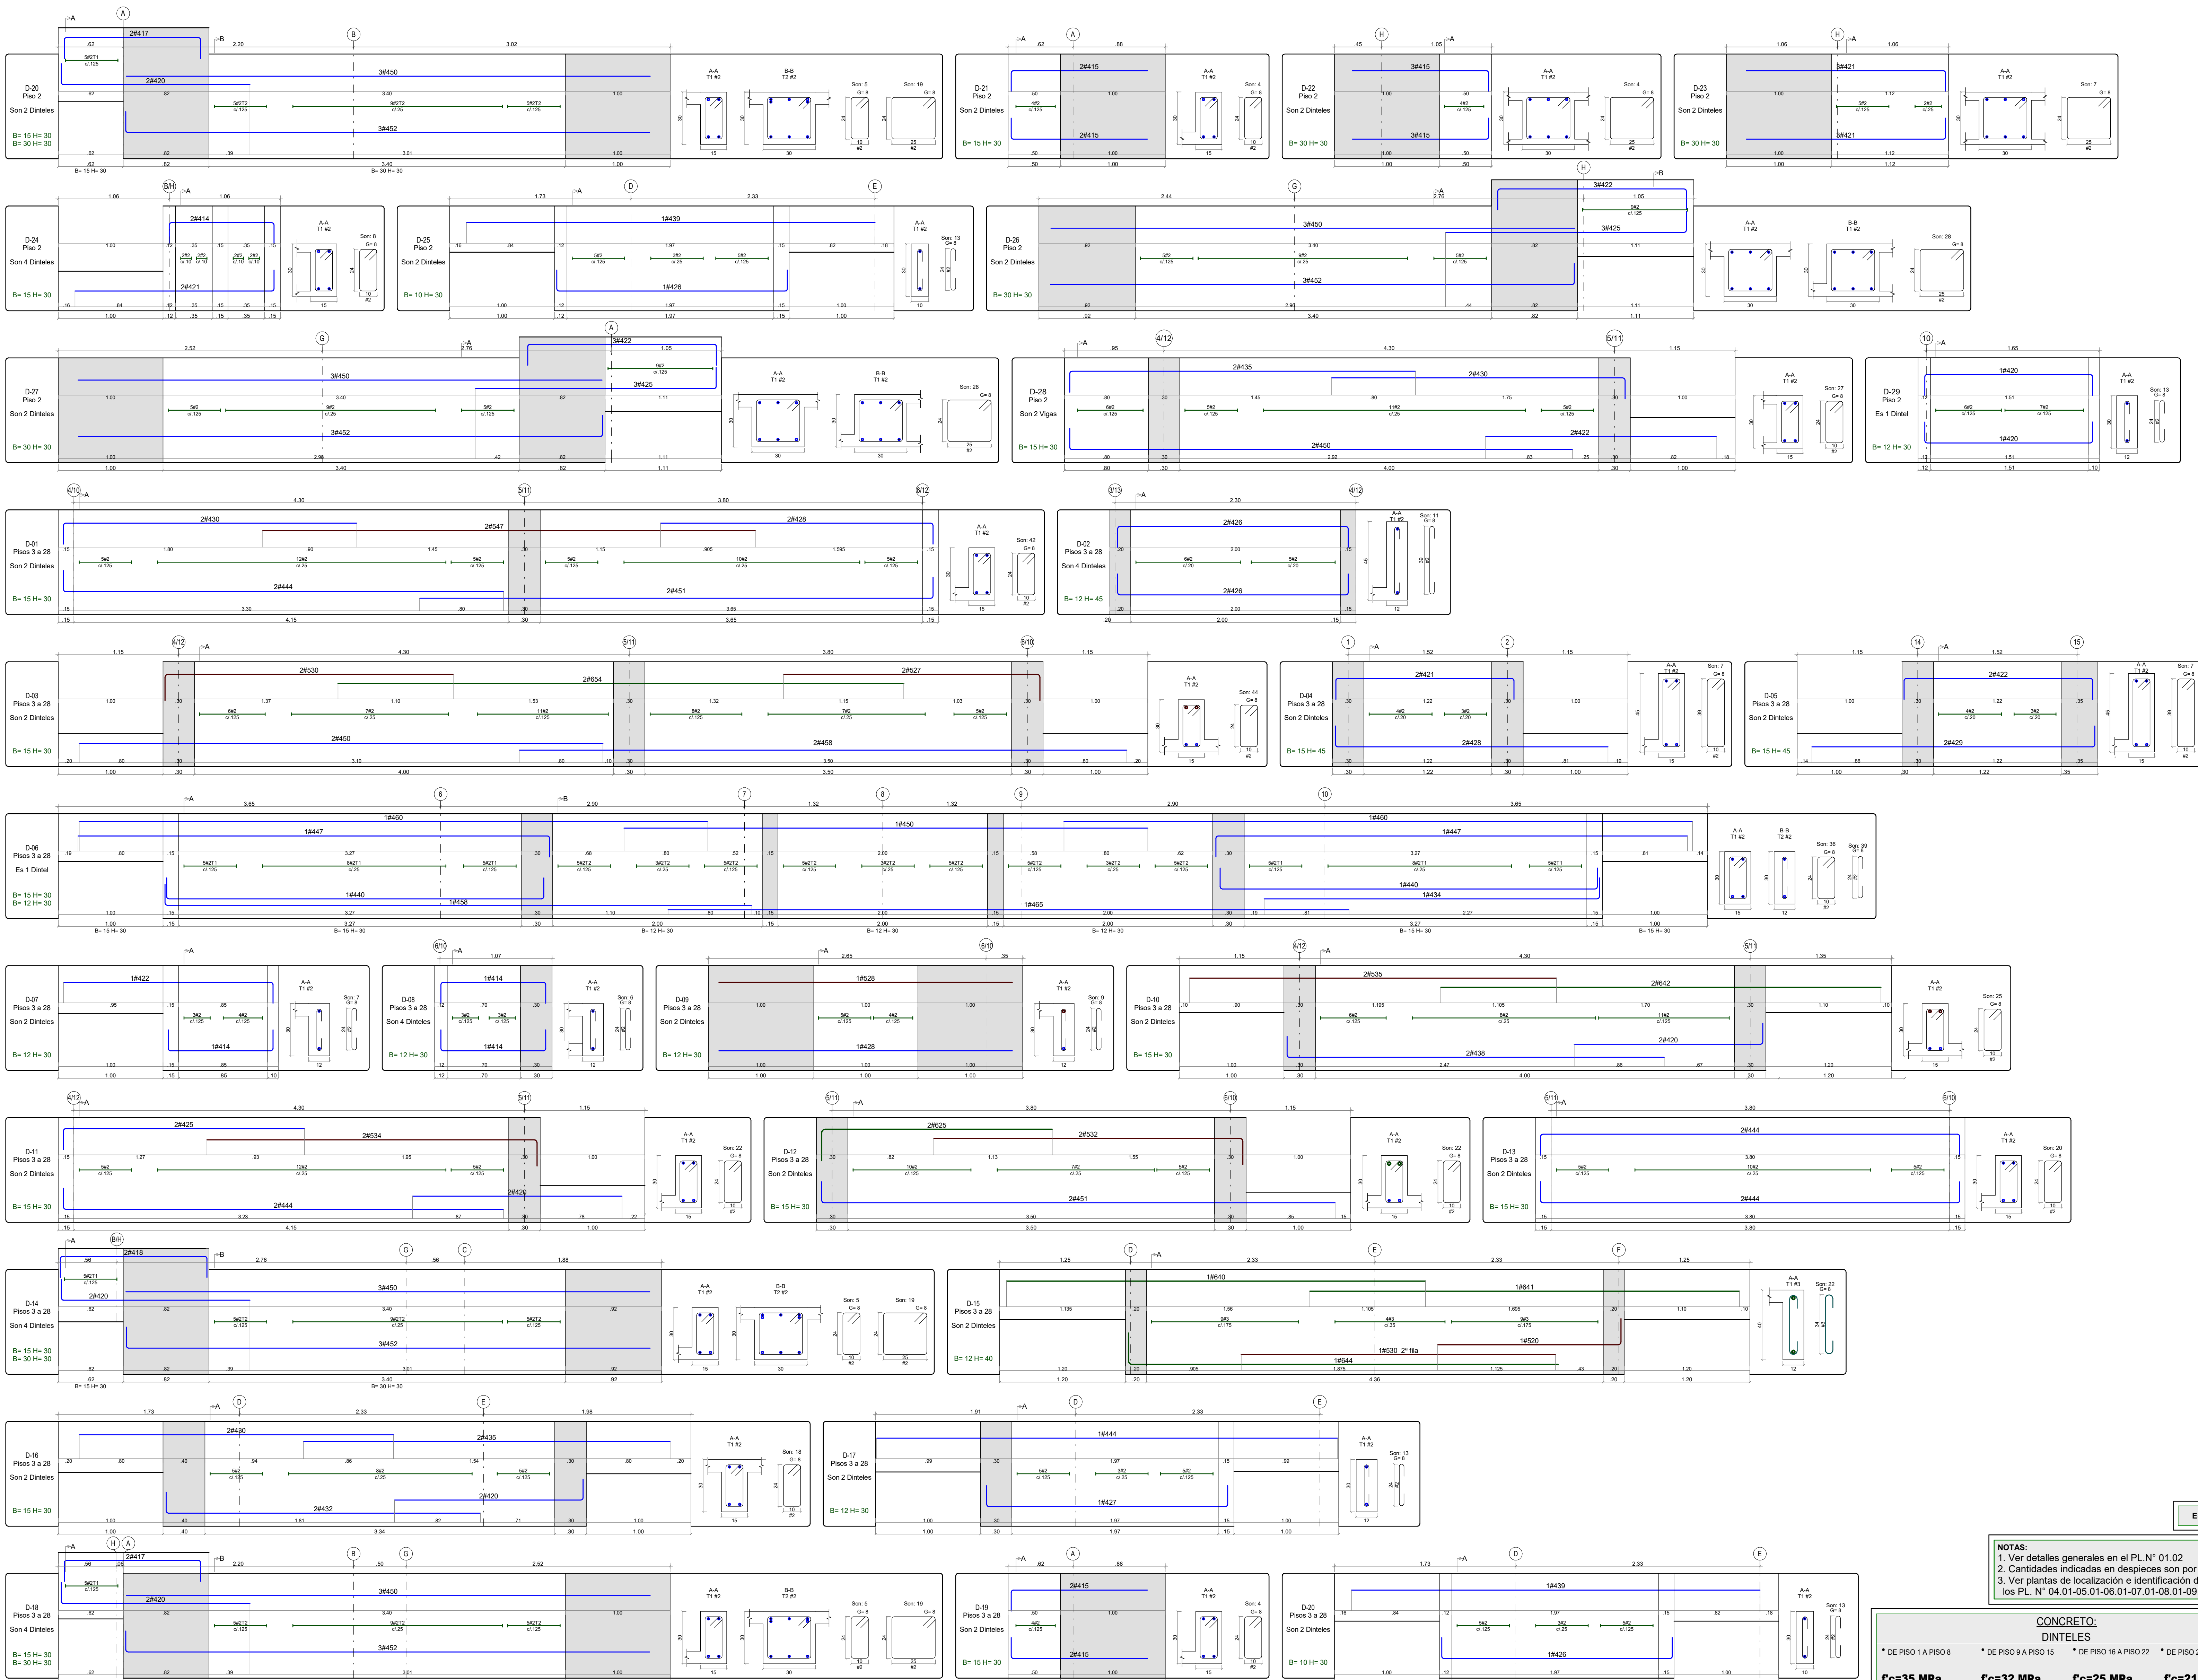

VERSIÓN :

2

PLANO N°

10.02

GERENTE DE PROYECTO

ROBERTO AYCARDI F.  
MAT. 2520257258 CND

INGENIERO

CARLOS ANDRÉS WILCHES C.

MODELADOR

DANIEL CASTELLANOS

MODIFICACIONES

FECHA

|                                                           |            |
|-----------------------------------------------------------|------------|
| Emisión Inicial                                           | 28-02-2025 |
| Se incluye despiece de dintel D-28 y ajuste cantidad D-24 | 26-02-2026 |
|                                                           |            |
|                                                           |            |



LA SCALA

LA SCALA\_EST\_TOR-1

TORRE I

CALLE 170 CON AV. BOYACA

DESPIECE DE DINTELES

LA SCALA\_EST\_TOR-1\_10.02\_DINT-03

REVISOR ESTRUCTURAL

RAMÓN ANDRÉS ALVAREZ MANTILLA  
MAT. 25202-346546 CND.

PLANO N°

VERSIÓN :

10.02

2



NOTAS:  
1. Ver detalles generales en el PLN° 01.02  
2. Cantidades indicadas en despieces son por piso  
3. Ver plantas de localización e identificación de dinteles en los PL. N° 04.01-05.01-06.01-07.01-08.01-09.01 y 09.05

CONCRETO:

DINTELES

|                      |                       |                        |                         |
|----------------------|-----------------------|------------------------|-------------------------|
| * DE PISO 1 A PISO 8 | * DE PISO 9 A PISO 15 | * DE PISO 16 A PISO 22 | * DE PISO 23 A CUBIERTA |
| f'c=35 MPa           | f'c=32 MPa            | f'c=25 MPa             | f'c=21 MPa              |
| f'c=350 kg/cm²       | f'c=315 kg/cm²        | f'c=245 kg/cm²         | f'c=210 kg/cm²          |
| f'c=5000 psi         | f'c=4500 psi          | f'c=3500 psi           | f'c=3000 psi            |