


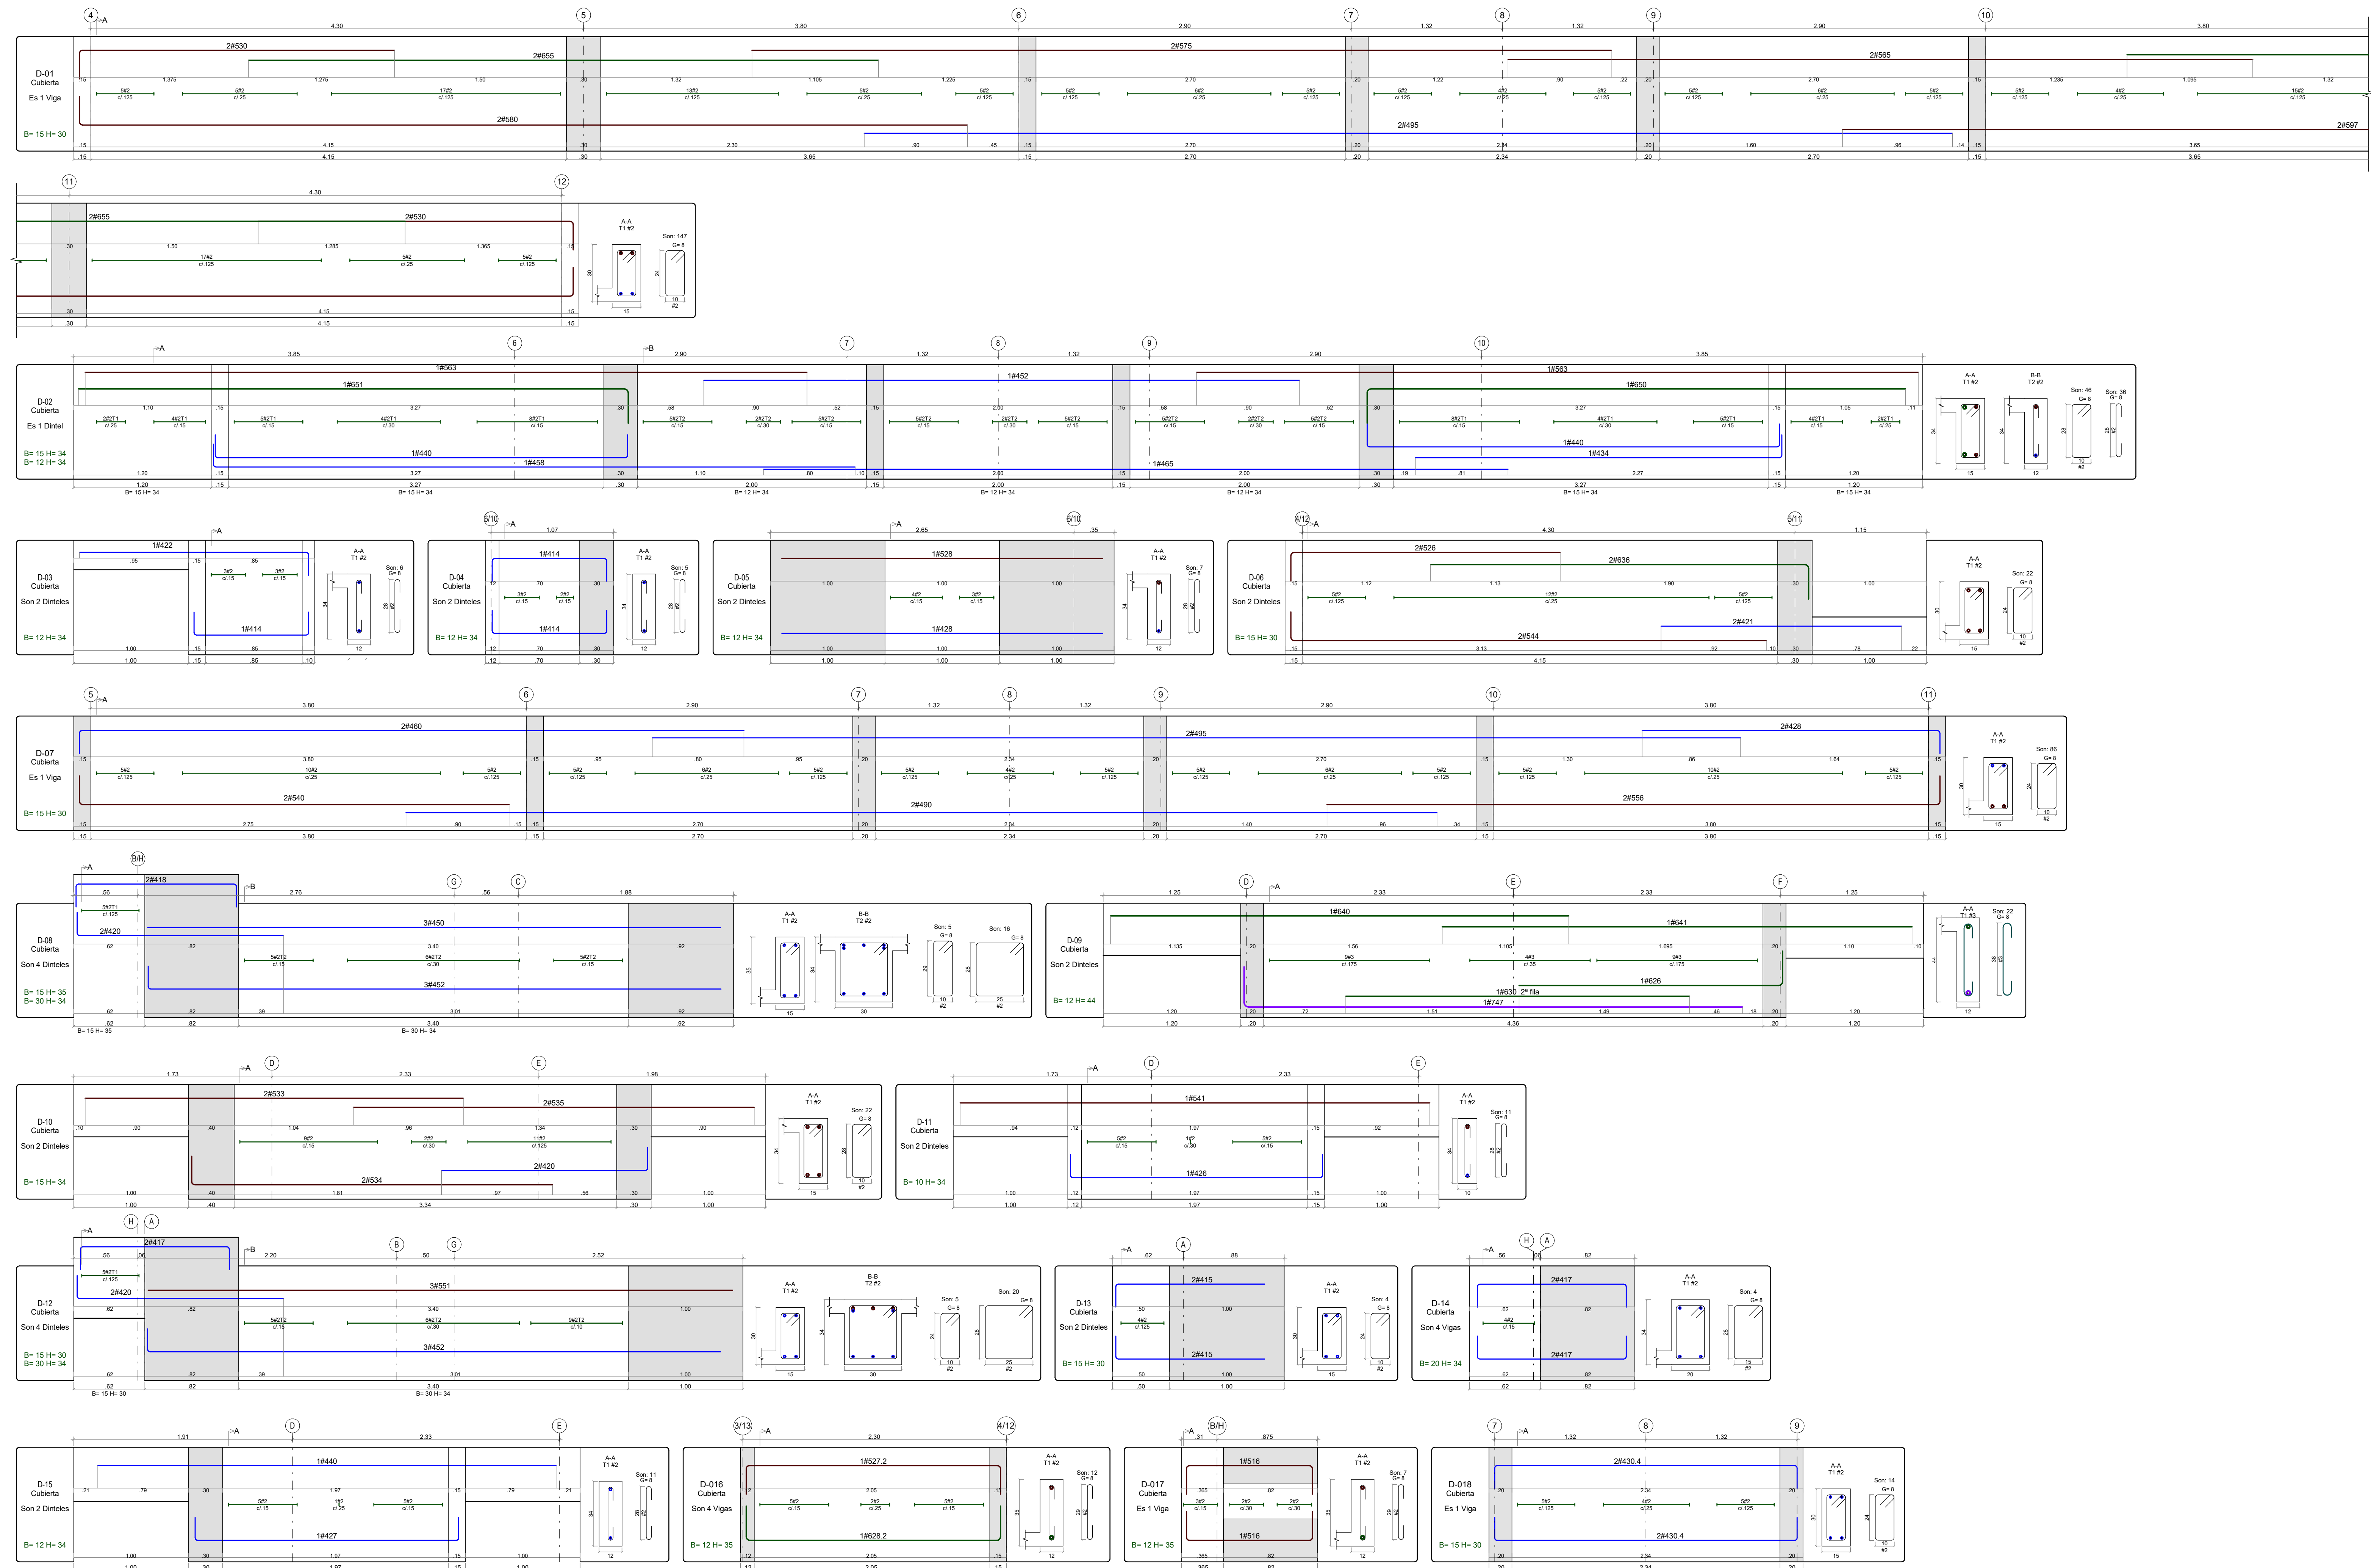

ESCALA 1:25

NOTAS:
1. Ver detalles generales en el PL. N° 01.02
2. Cantidades indicadas en despieces son por piso
3. Ver plantas de localización e identificación de dinteles en los PL. N° 04.01-05.01-06.01-07.01-08.01-09.01 y 09.05

CONCRETO:
DINTELES

* DE PISO 1 A PISO 8	* DE PISO 9 A PISO 15	* DE PISO 16 A PISO 22	* DE PISO 23 A CUBIERTA
f_c=35 MPa	f_c=32 MPa	f_c=25 MPa	f_c=21 MPa
f_c=350 kg/cm²	f_c=315 kg/cm²	f_c=245 kg/cm²	f_c=210 kg/cm²
f_c=5000 psi	f_c=4500 psi	f_c=3500 psi	f_c=3000 psi

VERSIÓN :

2

PLANO N°

10.03

Aycardi
Estructural

GERENTE DE PROYECTO

ROBERTO AYCARDI F.
MAT. 2520257258 CND

INGENIERO

CARLOS ANDRÉS WILCHES C.

MODELADOR

DANIEL CASTELLANOS

MODIFICACIONES

Emisión Inicial	FECHA
Ajuste dinteles	28-02-2025
	26-02-2026



LA SCALA

LA SCALA_EST_TOR-1

TORRE 1

CALLE 170 CON AV. BOYACA

DESPIECE DE DINTELES

LA SCALA_EST_TOR-1_10.03_DINT-D4

REVISOR ESTRUCTURAL

RAMÓN ANDRÉS ALVAREZ MANTILLA
MAT. 25202-346546 CND.

PLANO N°

VERSIÓN :

10.03

2