


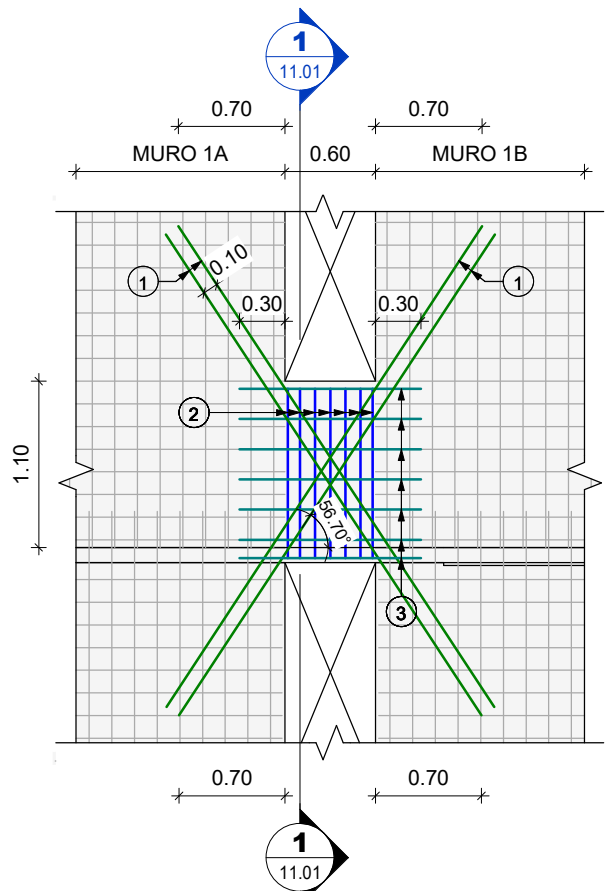
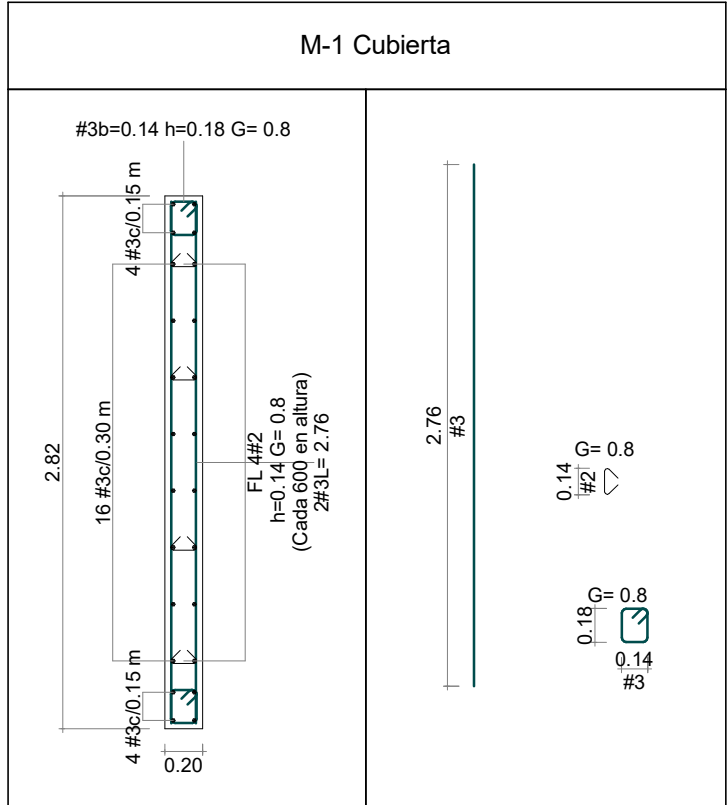
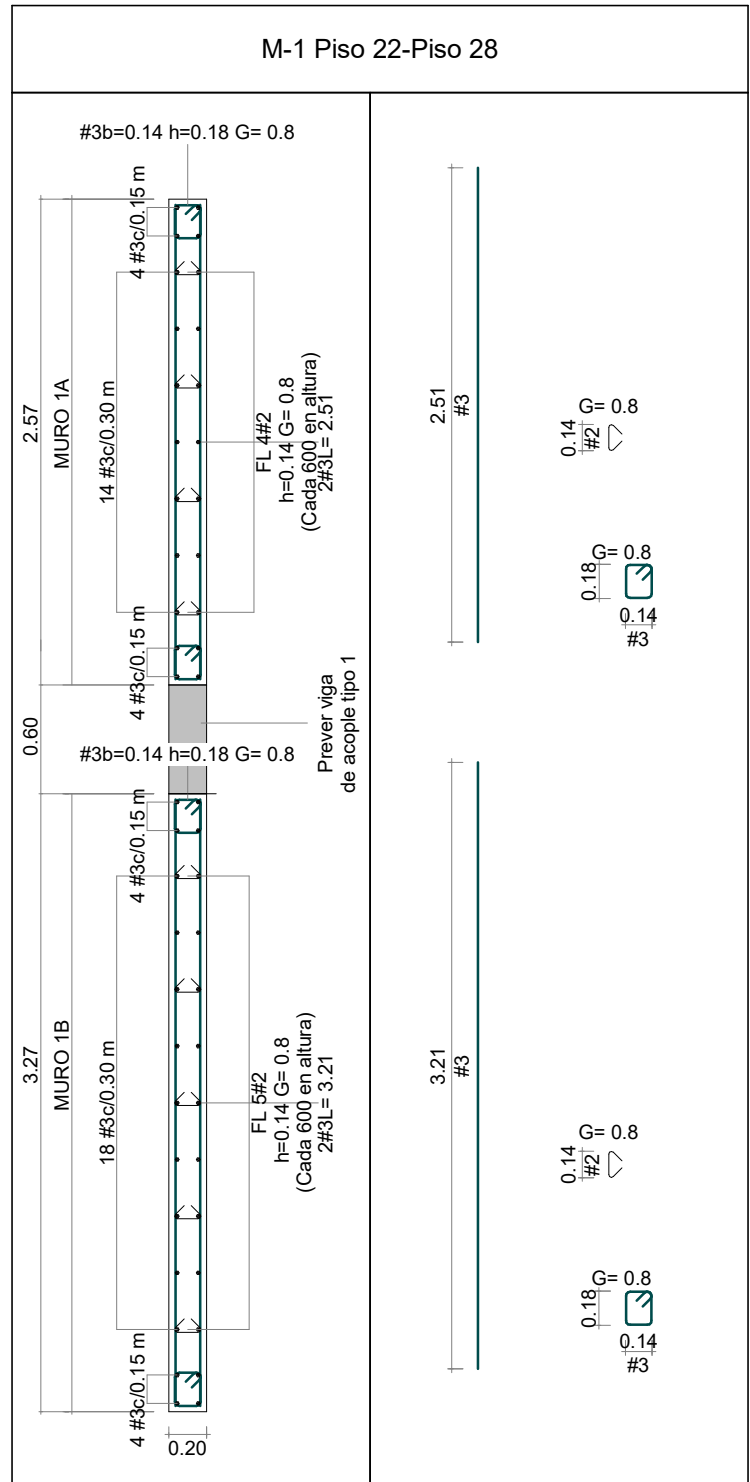
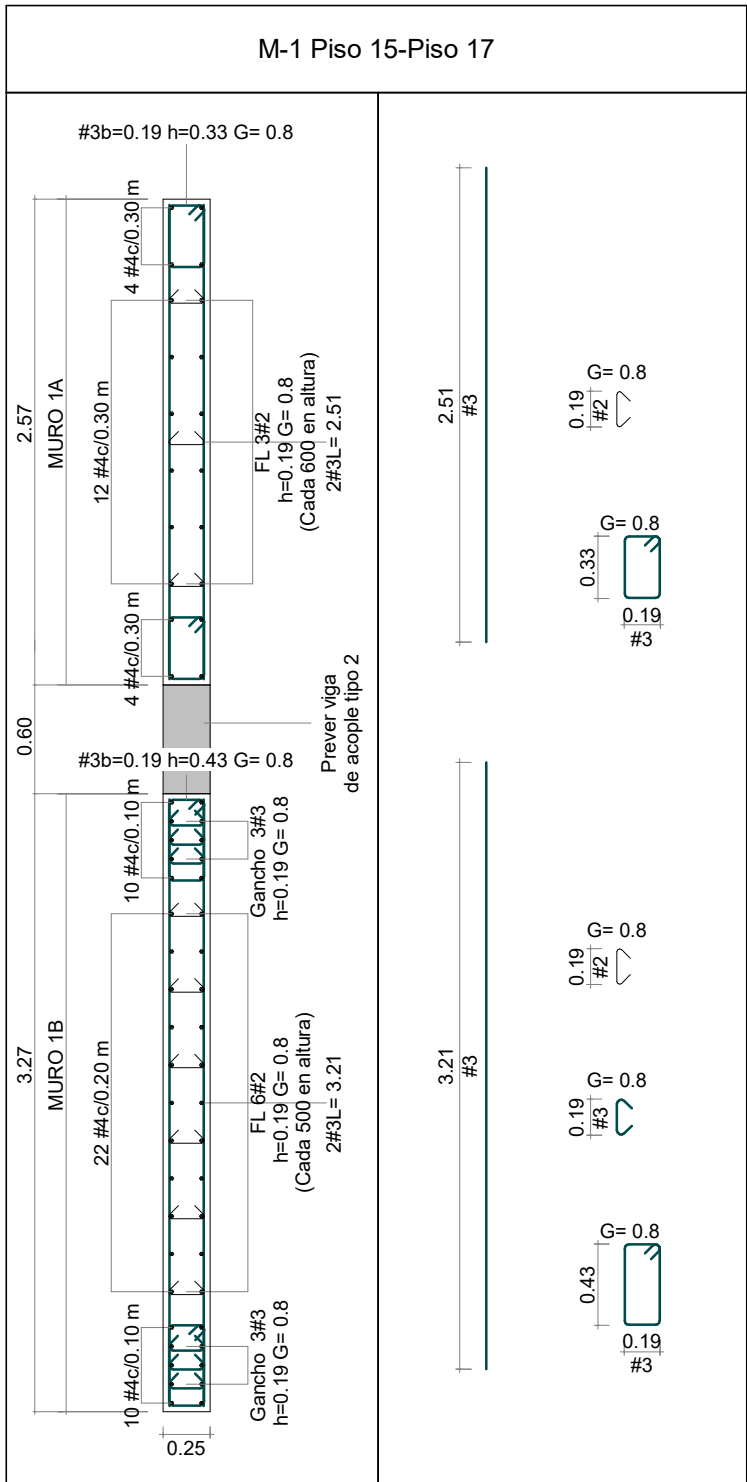
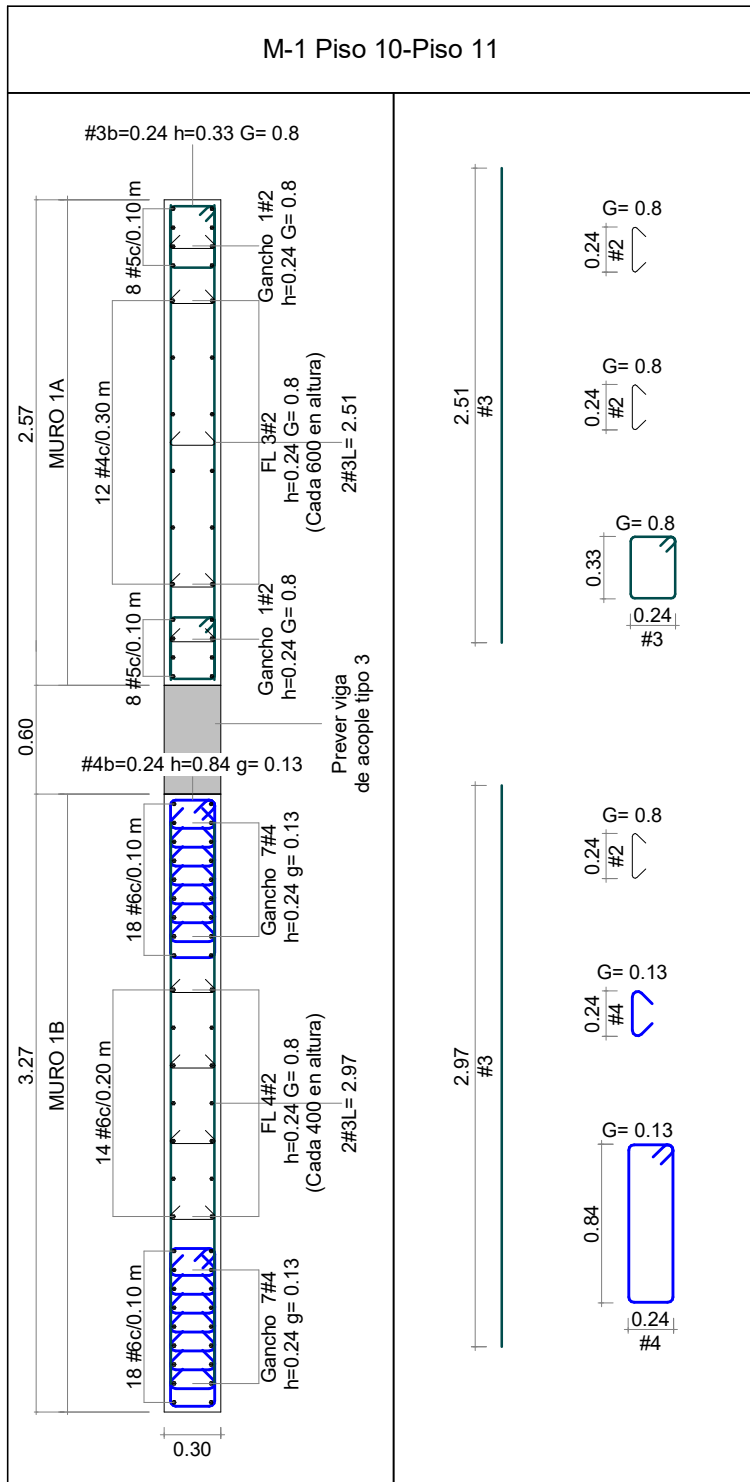
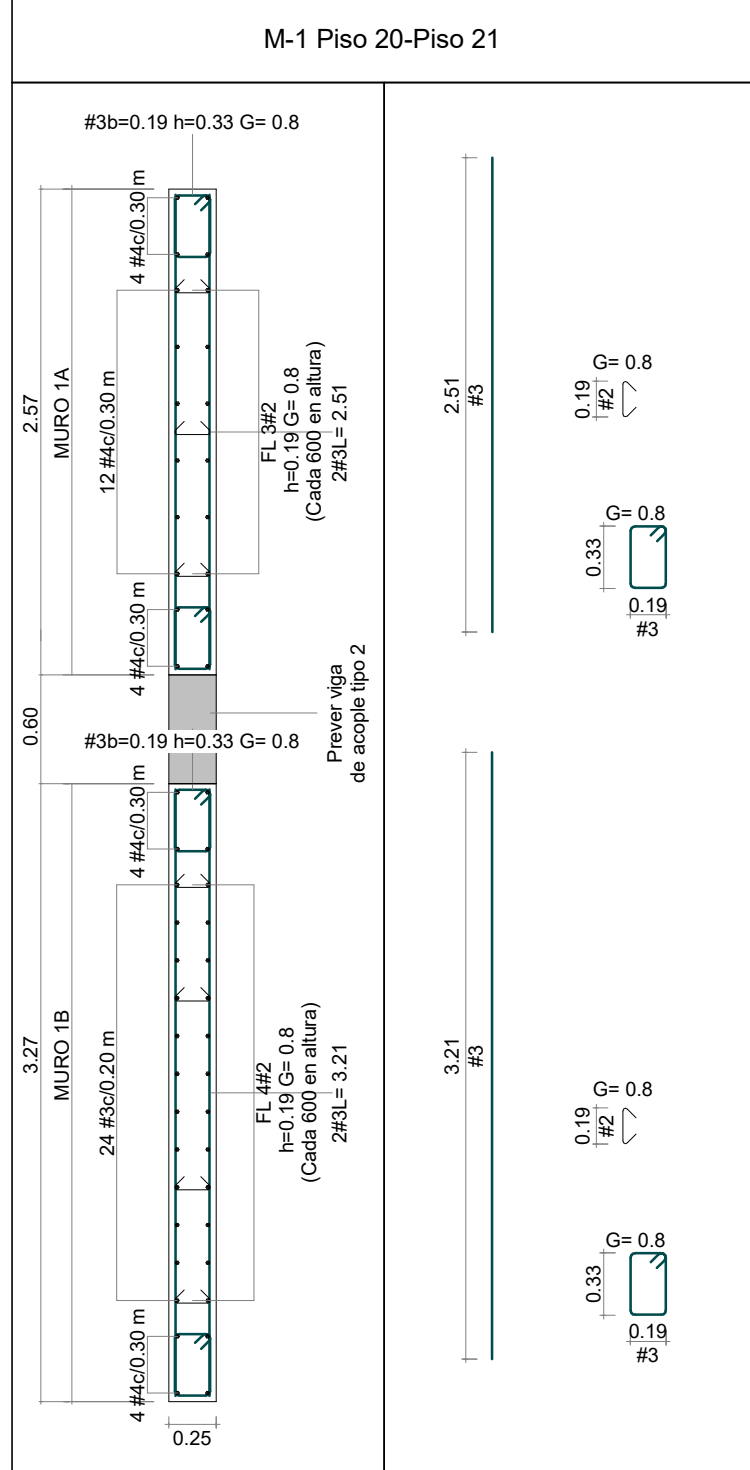
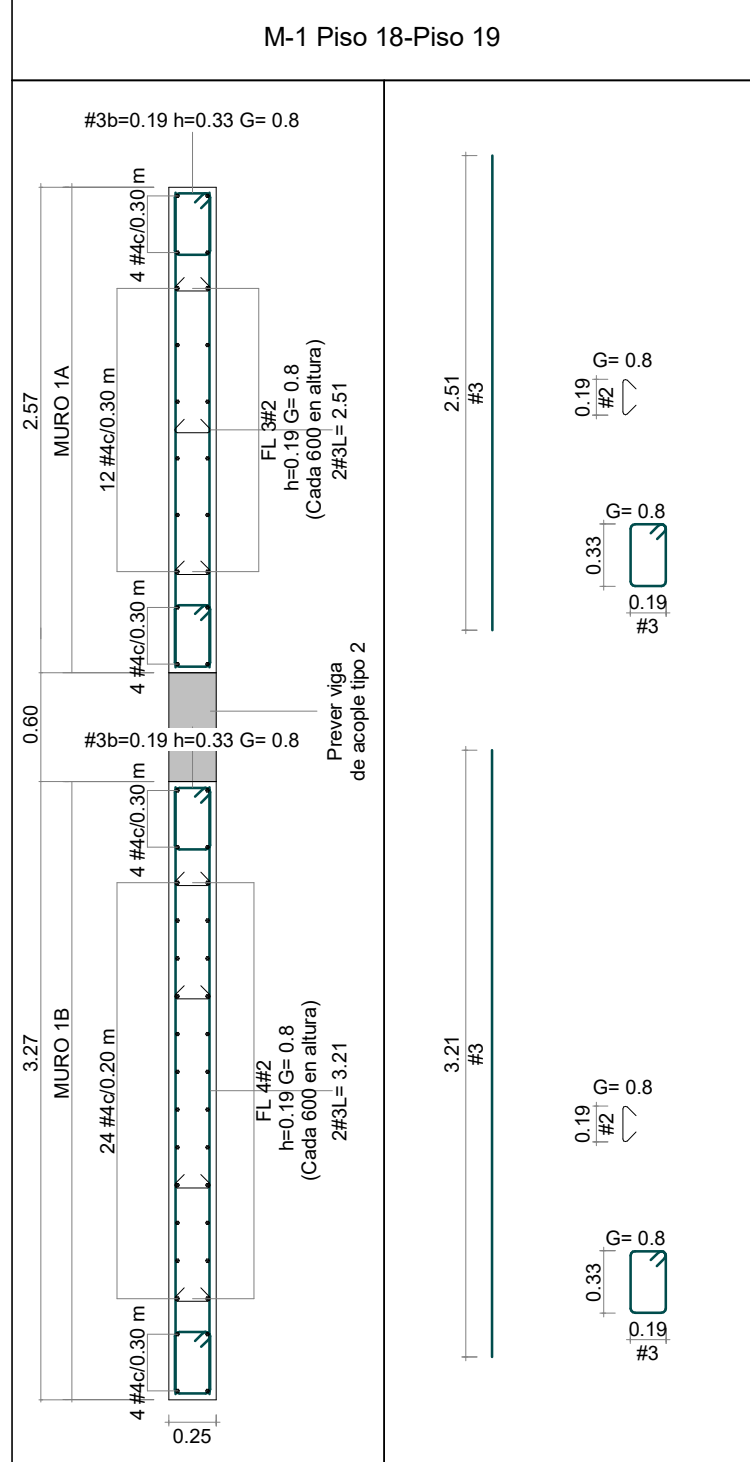
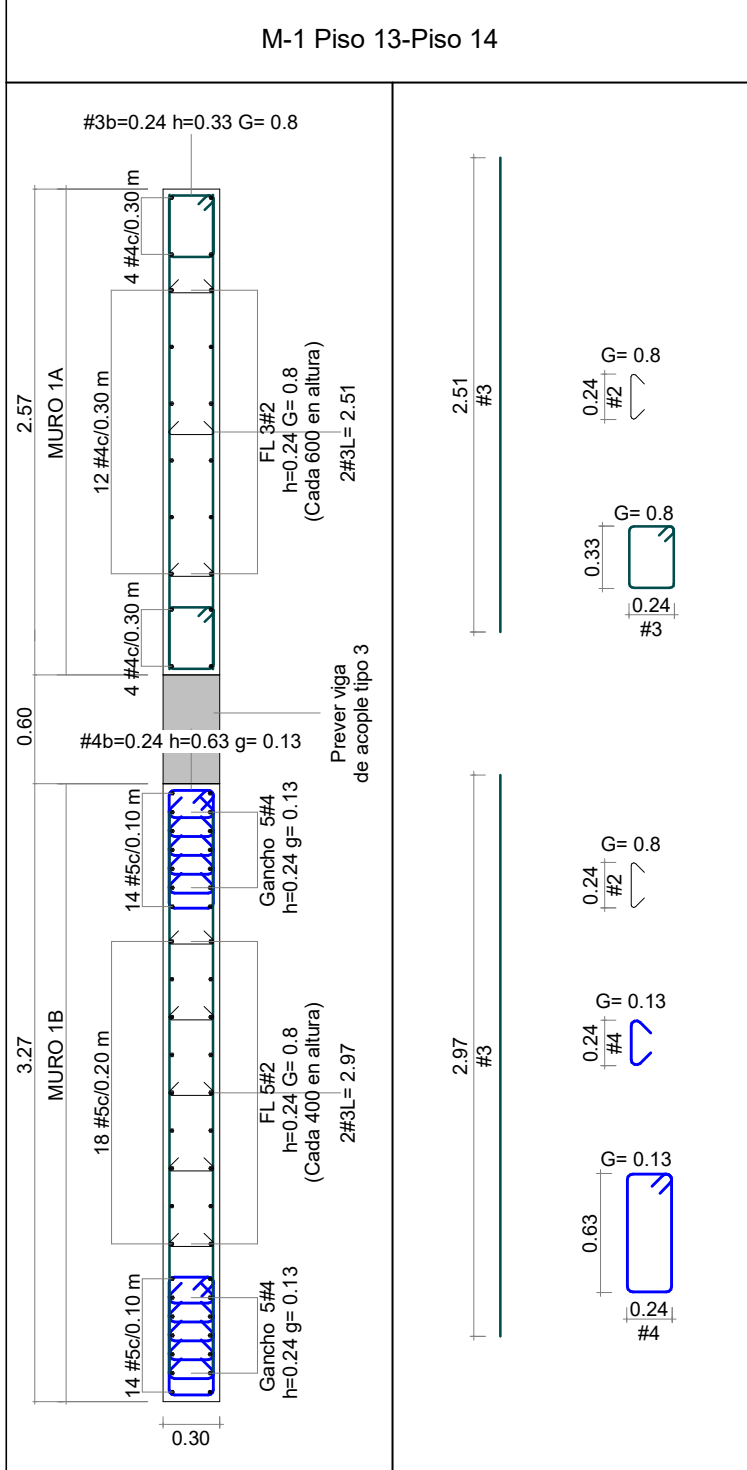
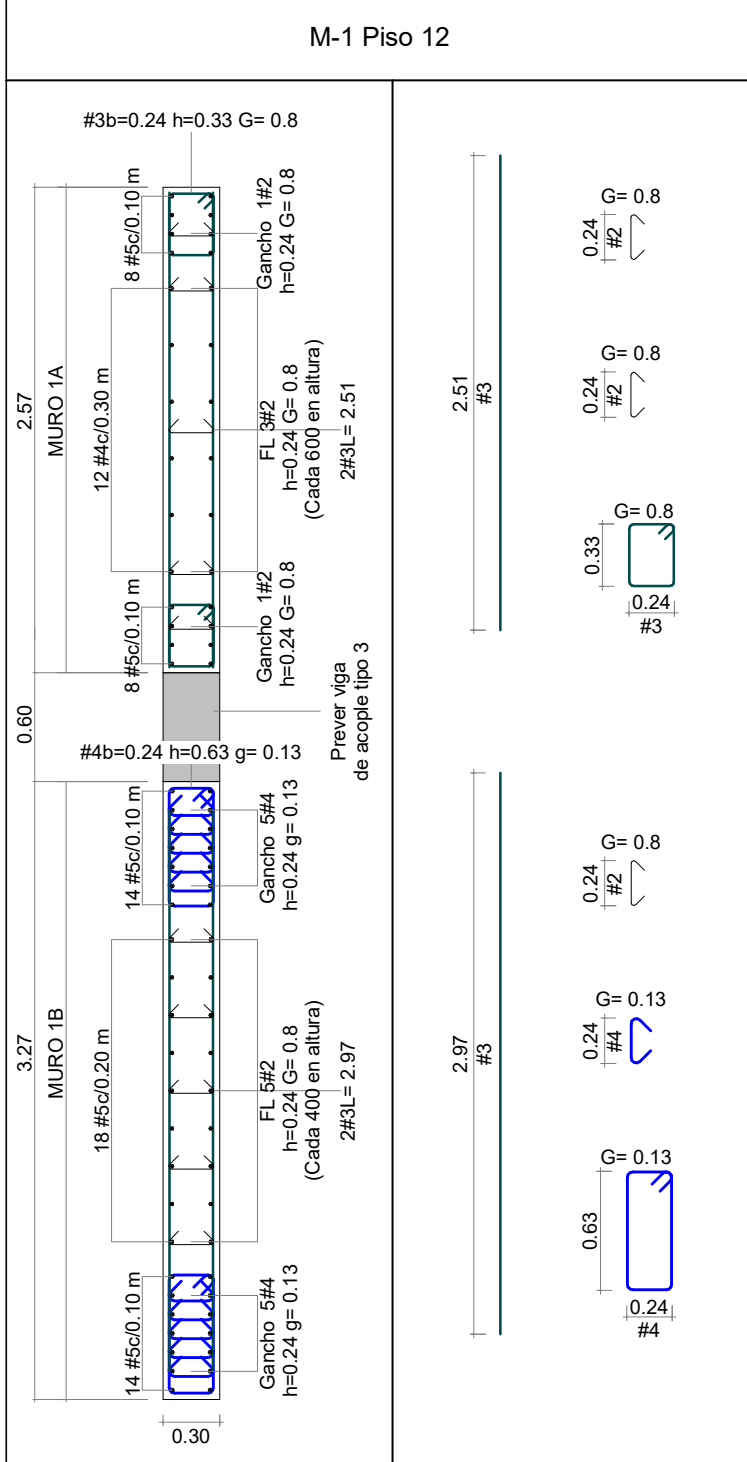
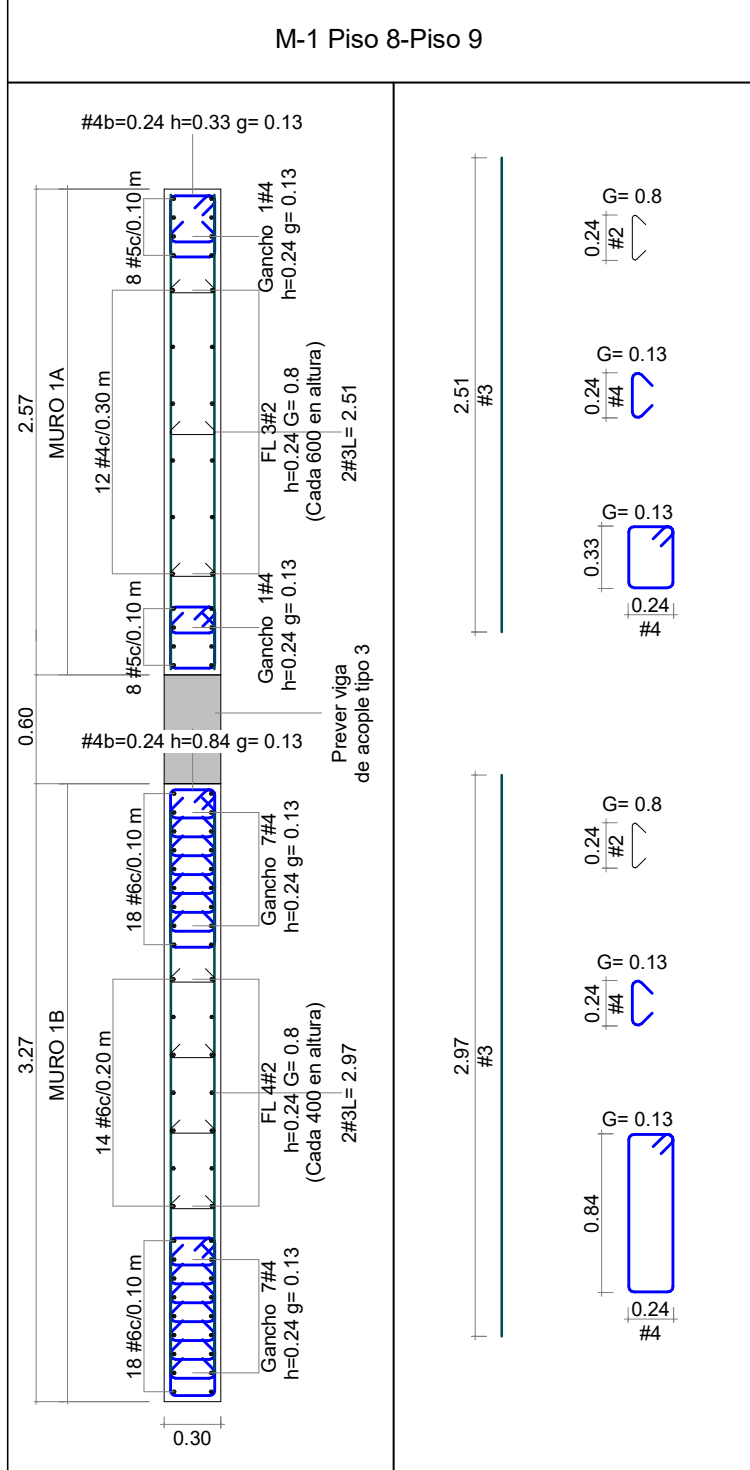
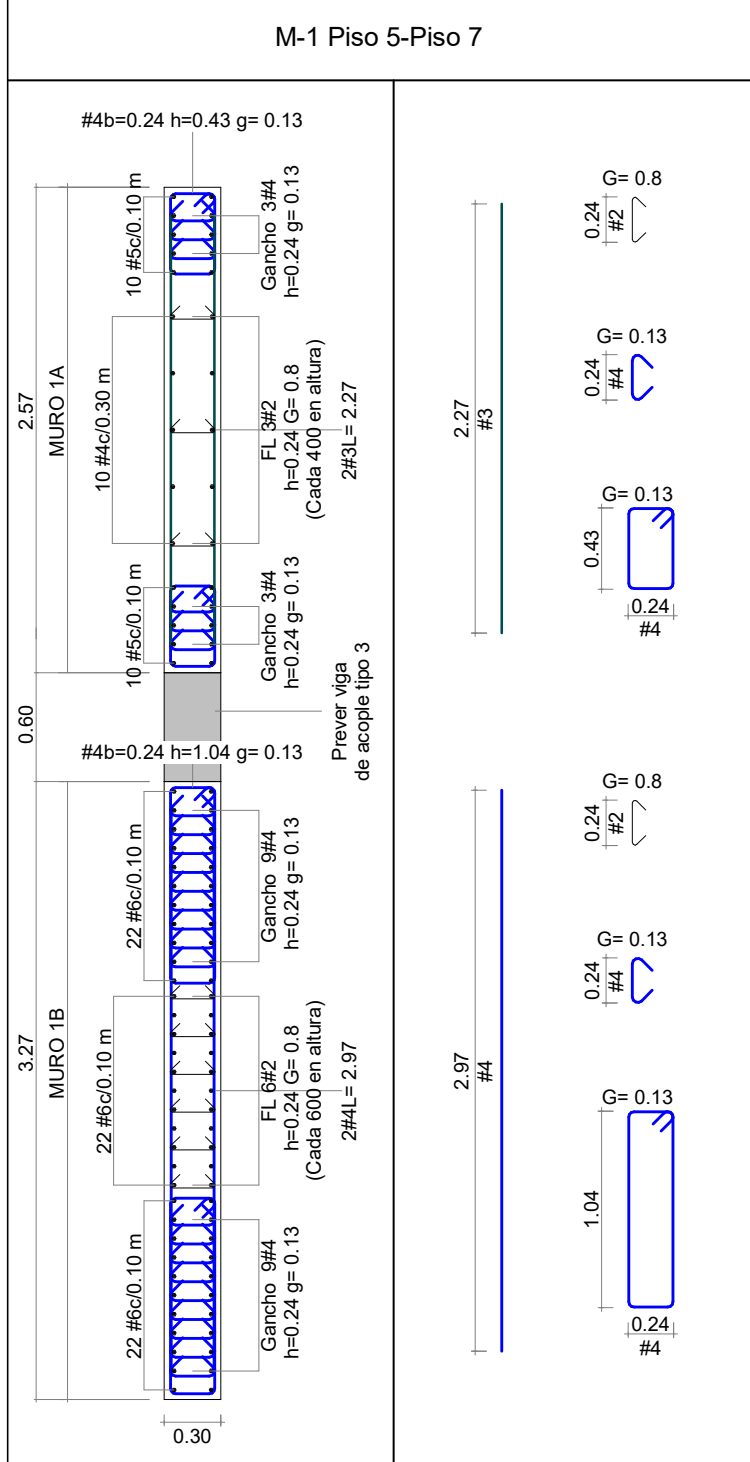
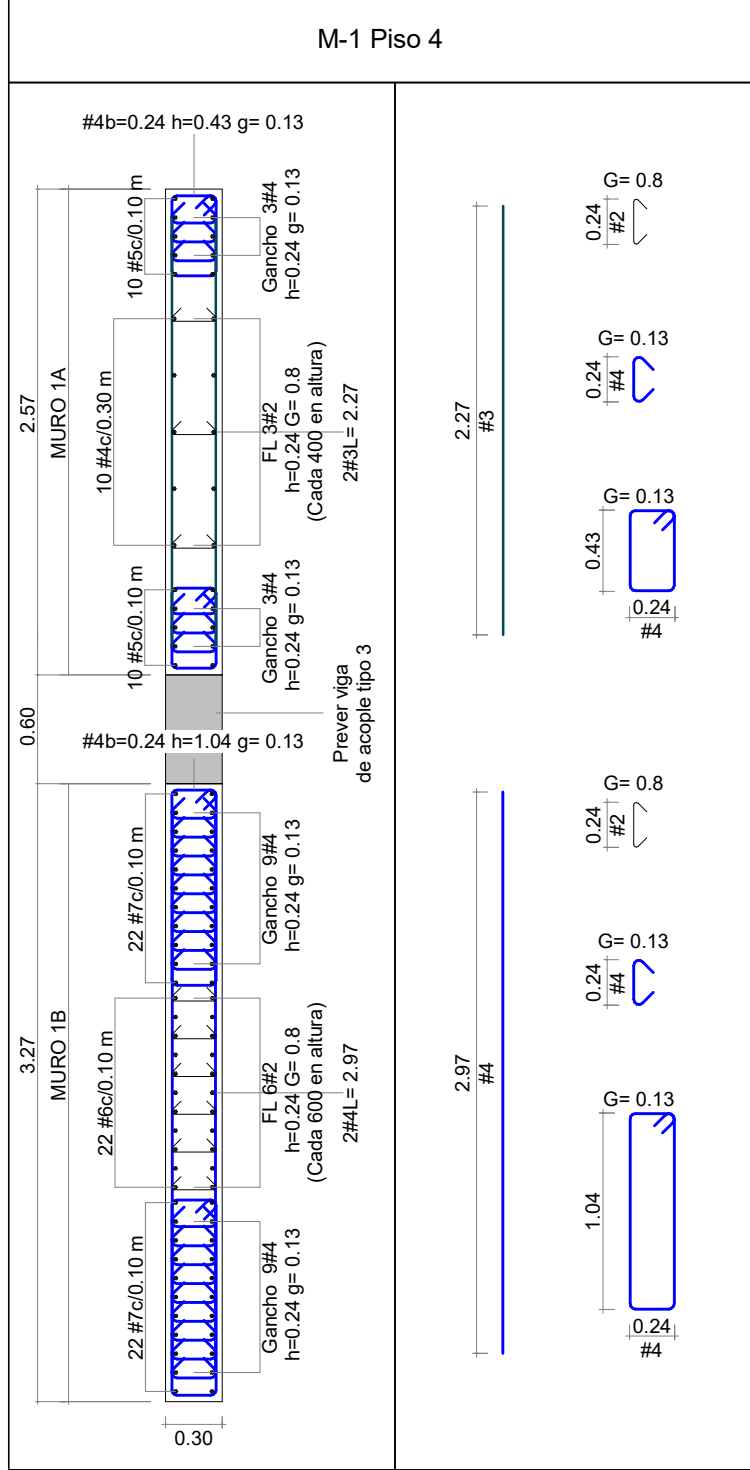
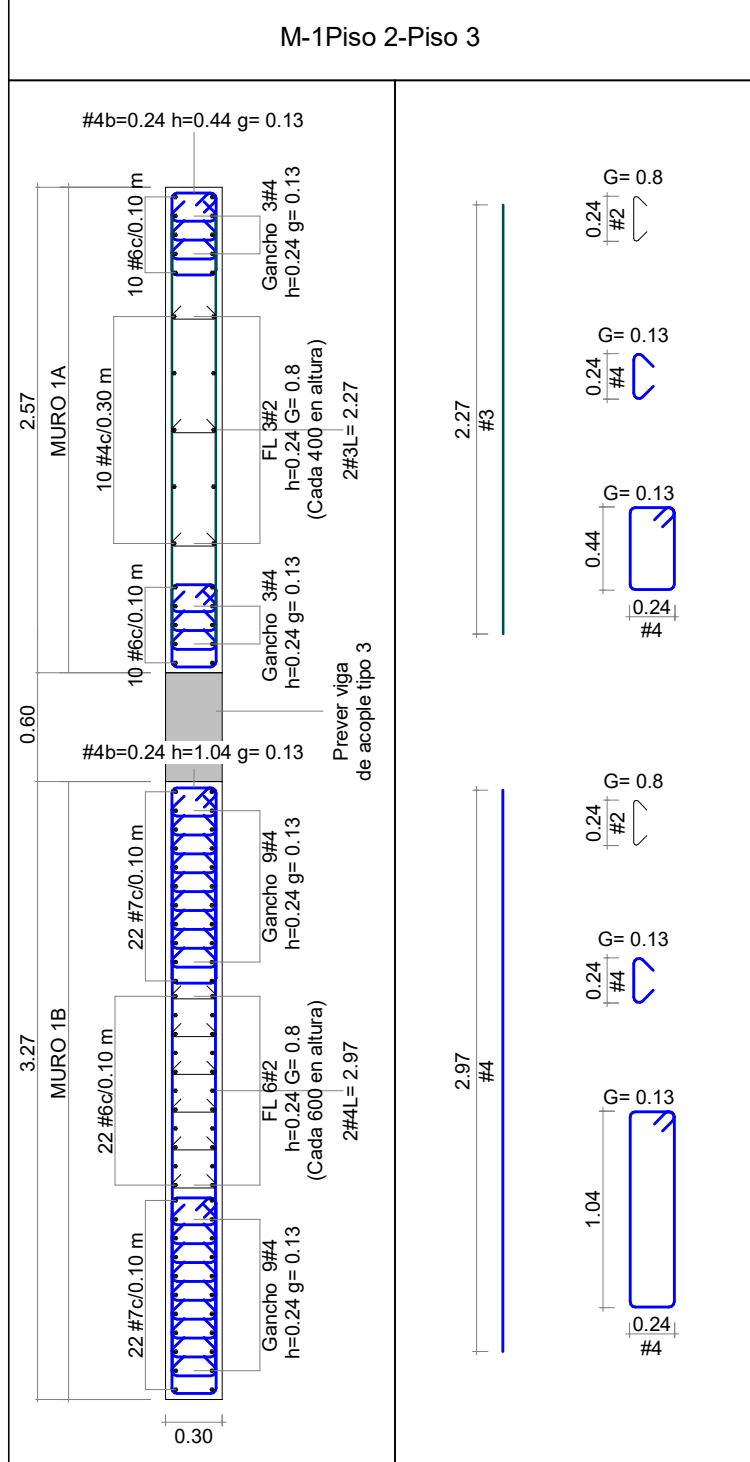
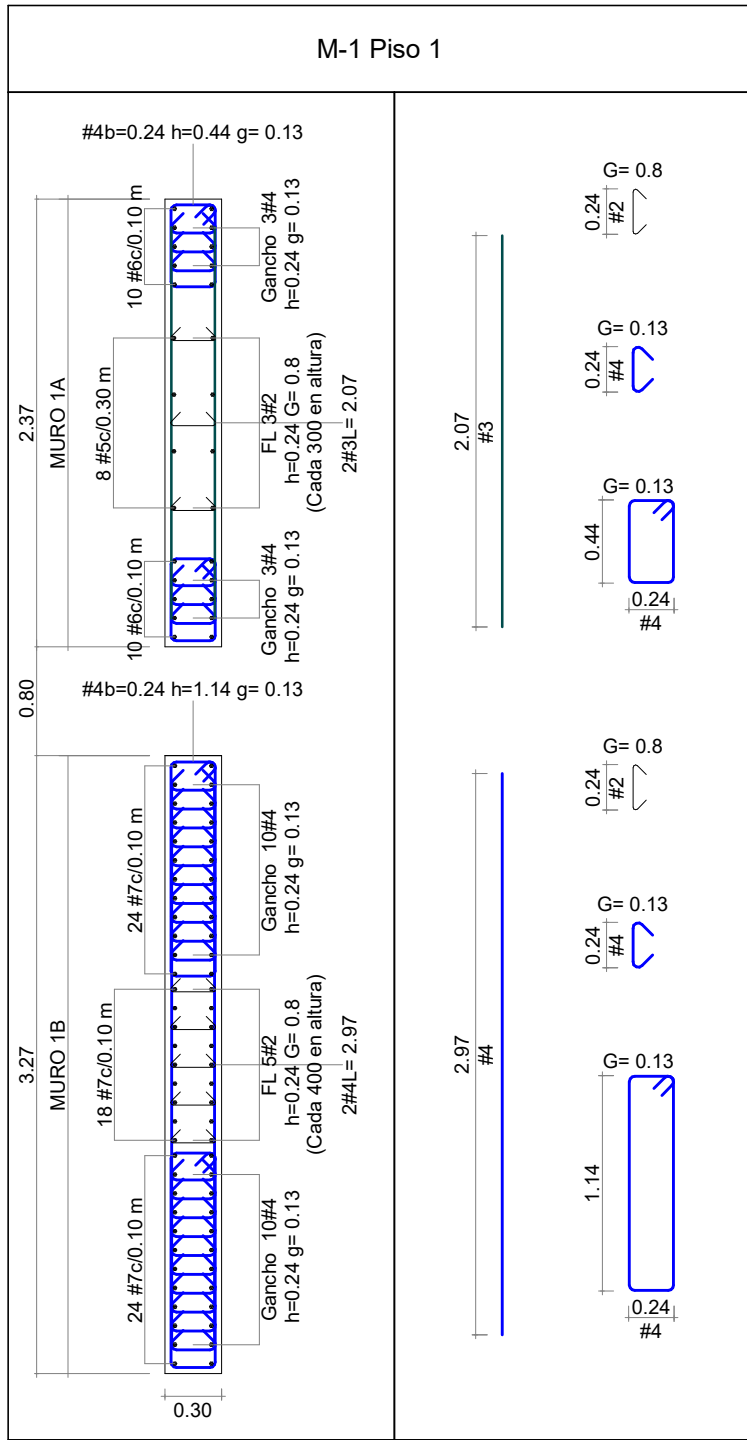


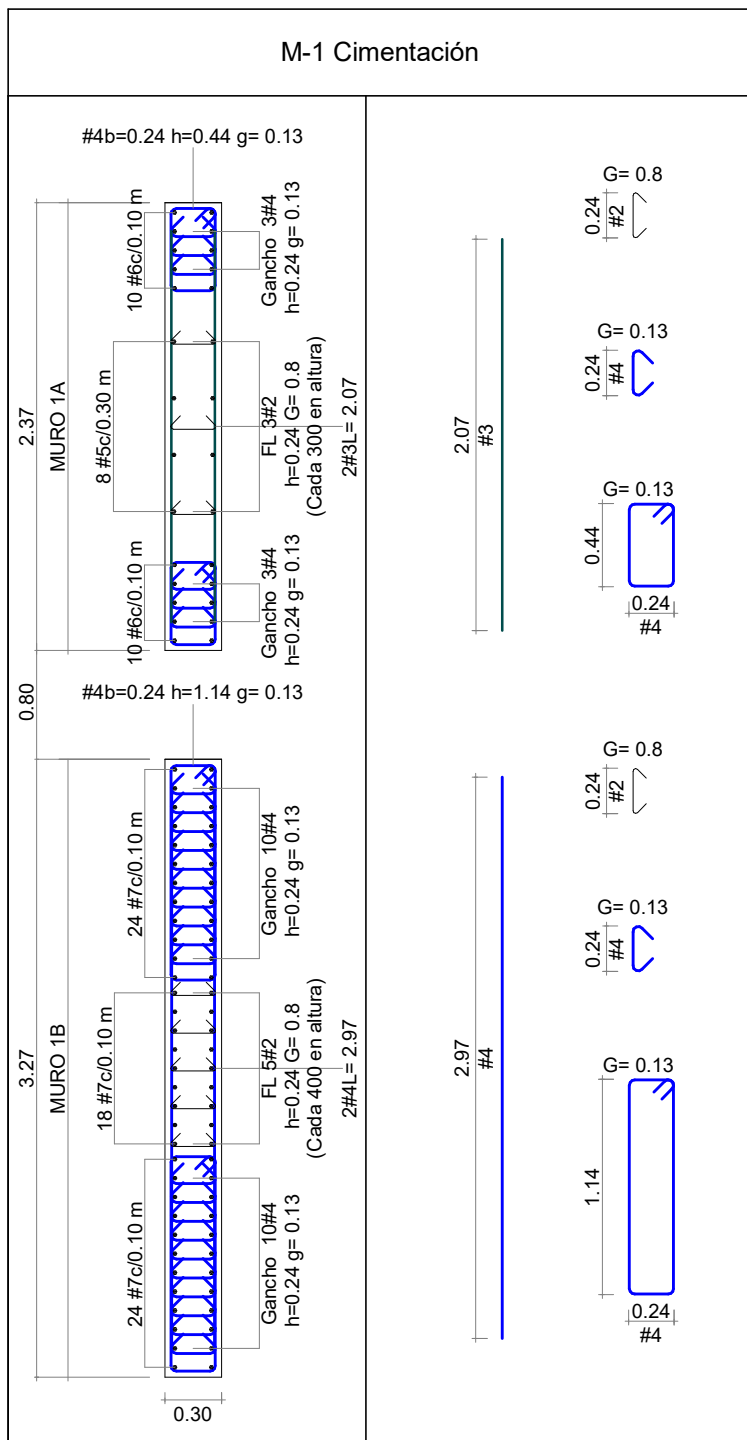


DETALLE 1 - VIGA DE ACOPLE
Escala 1 : 50

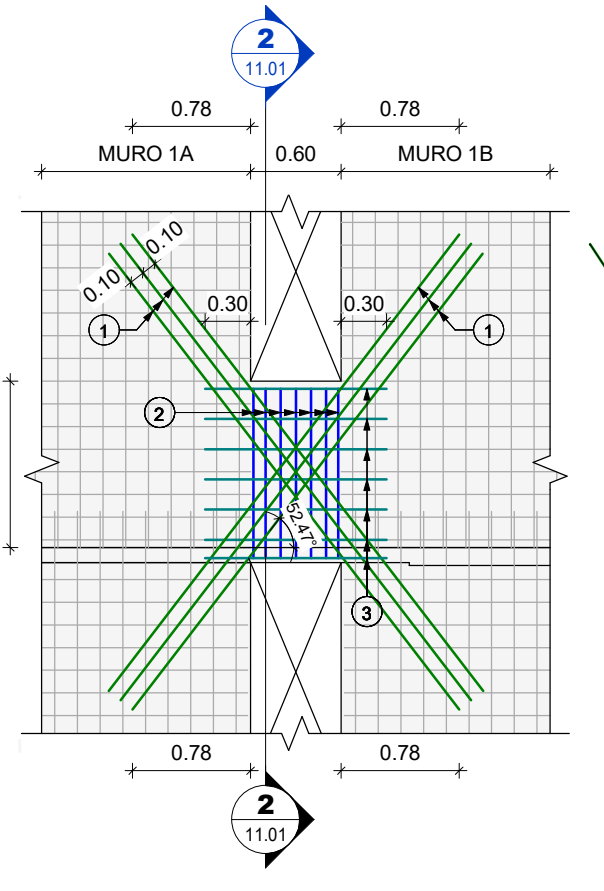


DETALLE 2 - VIGA DE ACOPLE
Escala 1 : 50

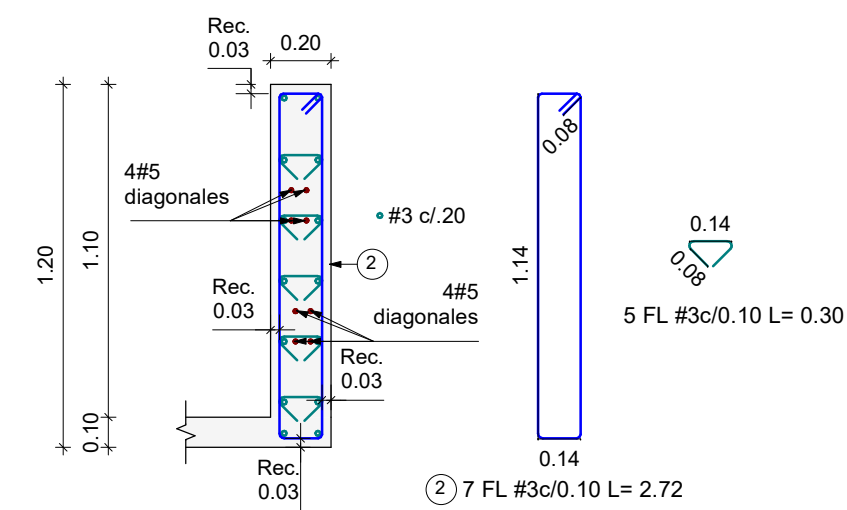

CORTE 1 - 1 VIGA DE ACOPLE TIPO 1 e=0.20
Escala 1 : 25

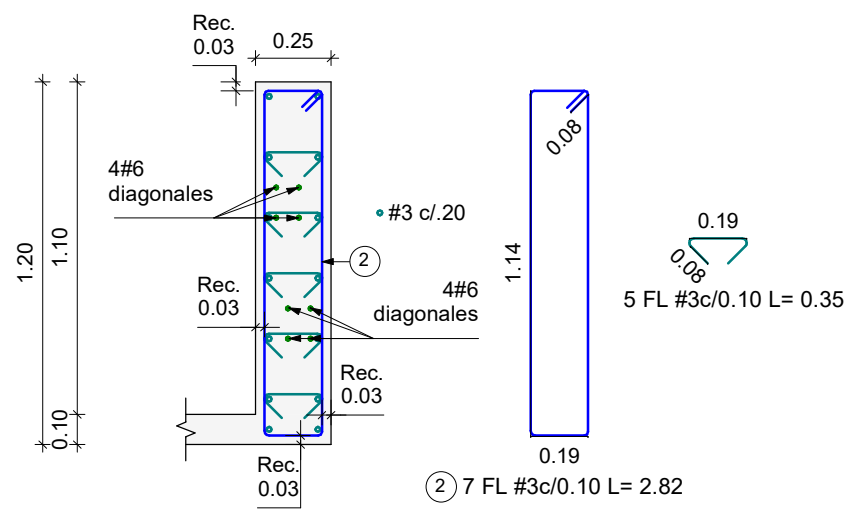

CORTE 1 - 1 VIGA DE ACOPLE TIPO 2 e=0.25
Escala 1 : 25

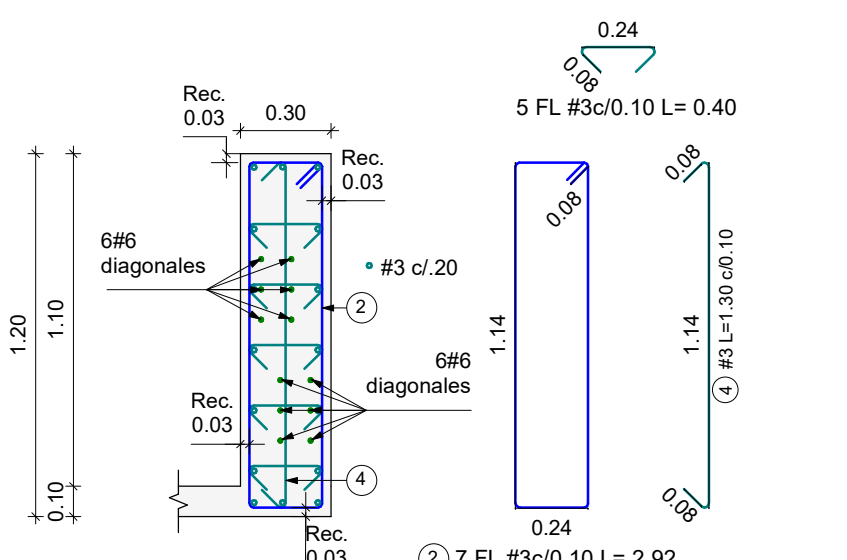

CORTE 2 - 2 VIGA DE ACOPLE TIPO 3 e=0.30
Escala 1 : 25

NOTAS:
1. Ver detalles generales en el PL.N° 01.02
2. Ver detalle de muros en el PL.N° 11.20
3. Ver plantas de localización e identificación de muros en los PL. N°03.00-04.00-05.00-06.00-07.00-08.00 y 09.00

ESCALA 1:125

VERSIÓN :

3

PLANO N°

11.01



GERENTE DE PROYECTO
ROBERTO AYCARDI F.
MAT. 2520257258 CND

INGENIERO
CARLOS ANDRÉS WILCHES C.

MODELADOR
DANIEL CASTELLANOS

MODIFICACIONES	FECHA
Emisión Inicial	28-02-2025
Ajuste longitudes refuerzos	03-10-2025
Ajuste refuerzo muros	26-02-2026



LA SCALA

LA SCALA_EST_TOR-1

TORRE 1

CALLE 170 CON AV. BOYACA

DESPIECE DE MUROS

LA SCALA_EST_TOR-1_11.01_MUR-02

REVISOR ESTRUCTURAL
RAMÓN ANDRÉS ALVAREZ MANTILLA
MAT. 25202-346546 CND.

PLANO N°

VERSIÓN :

11.01

3