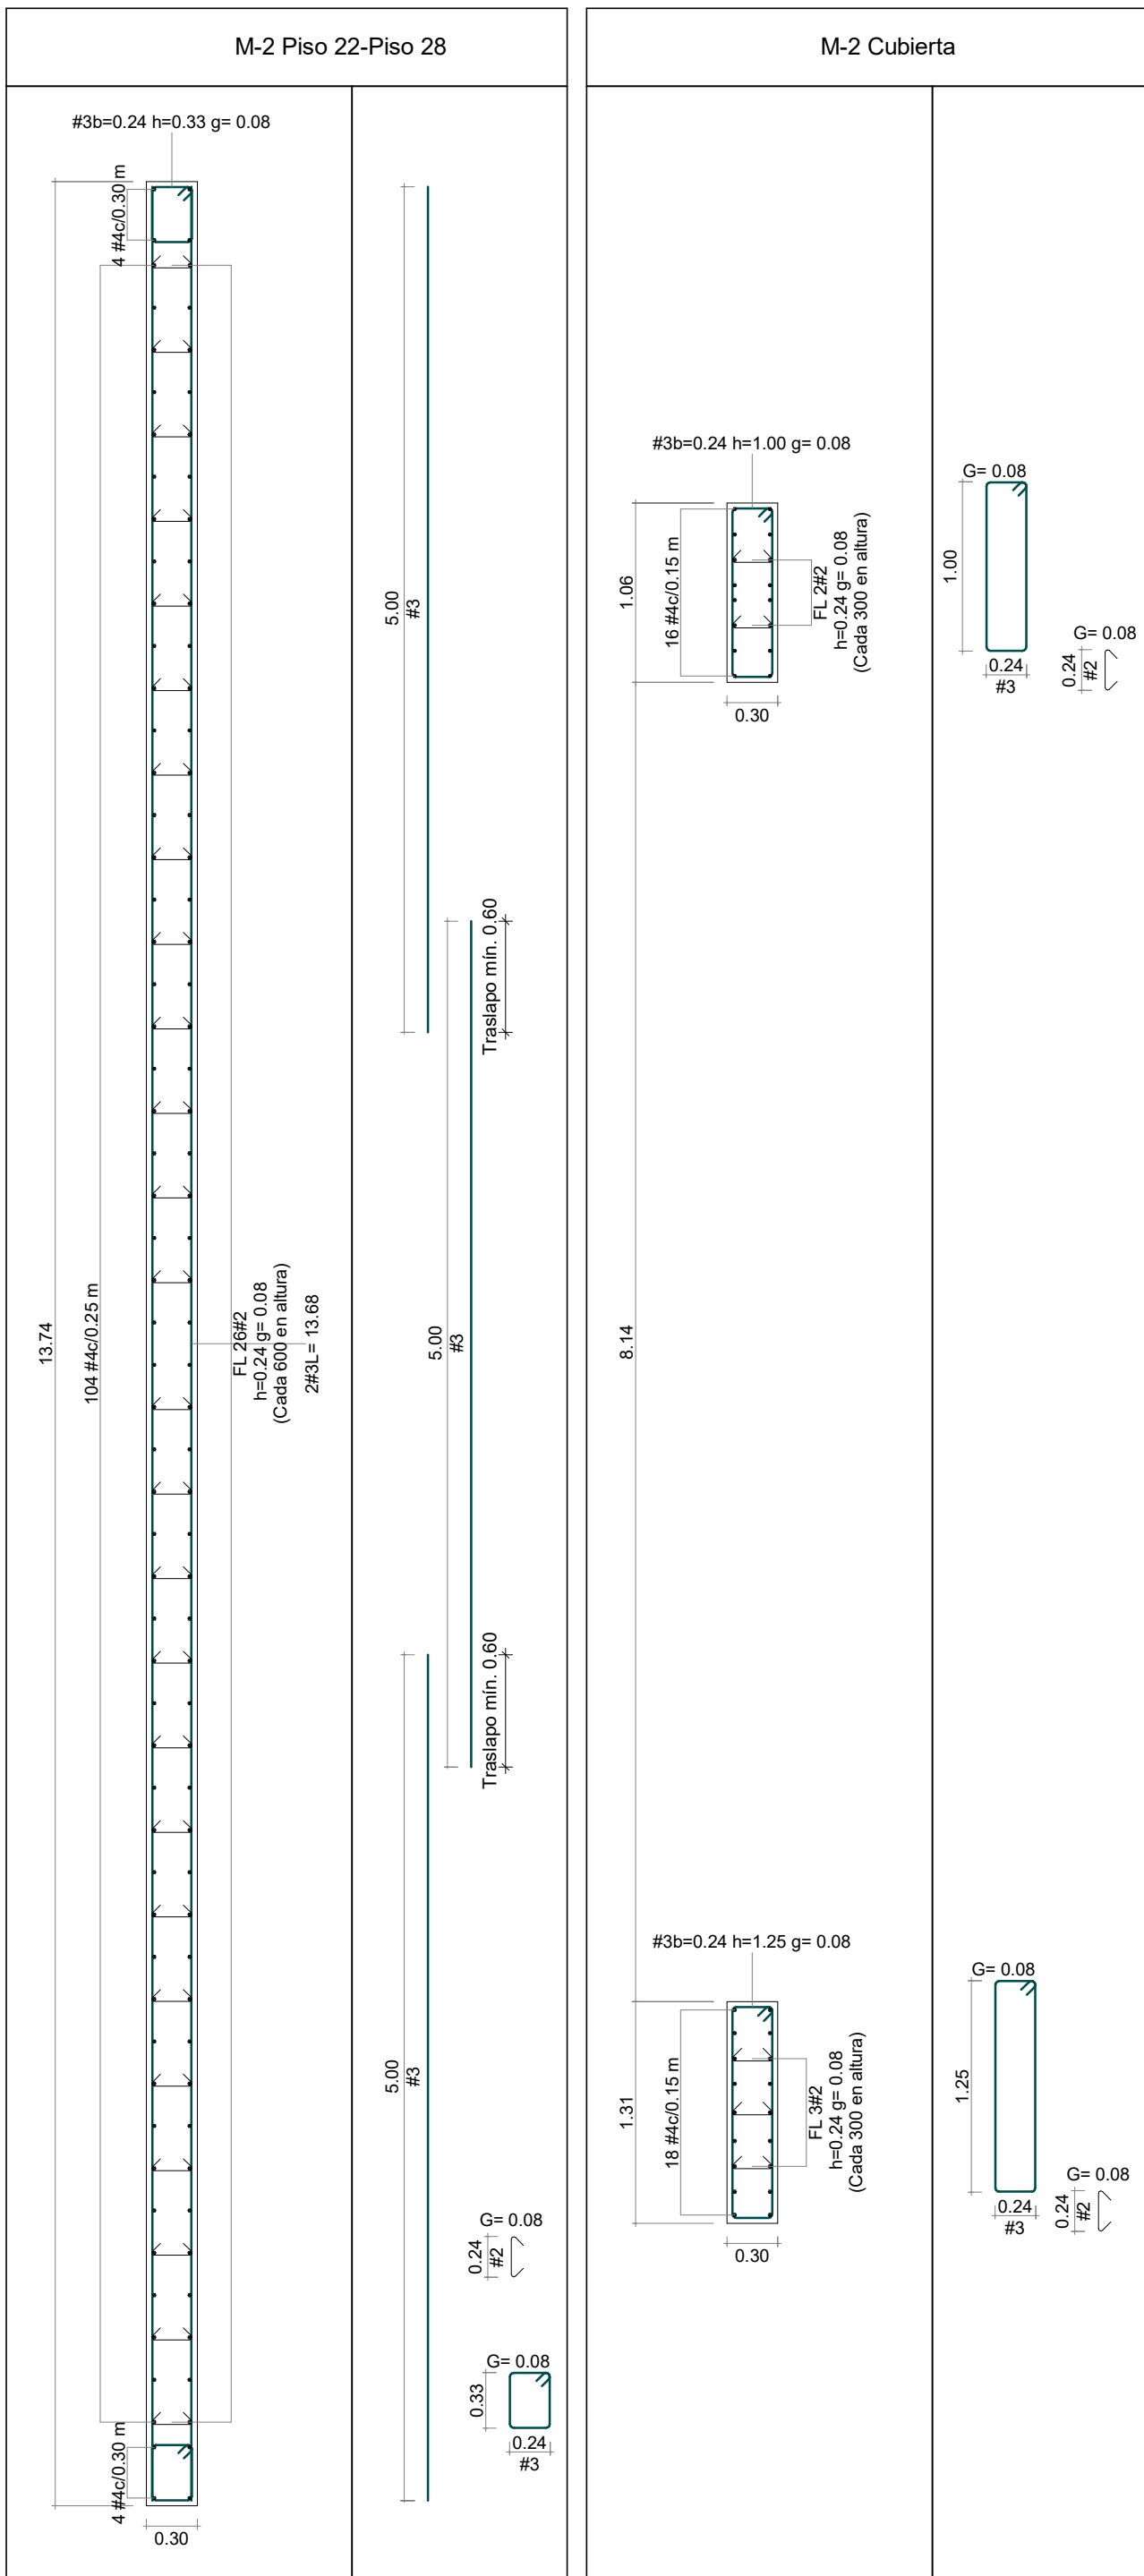
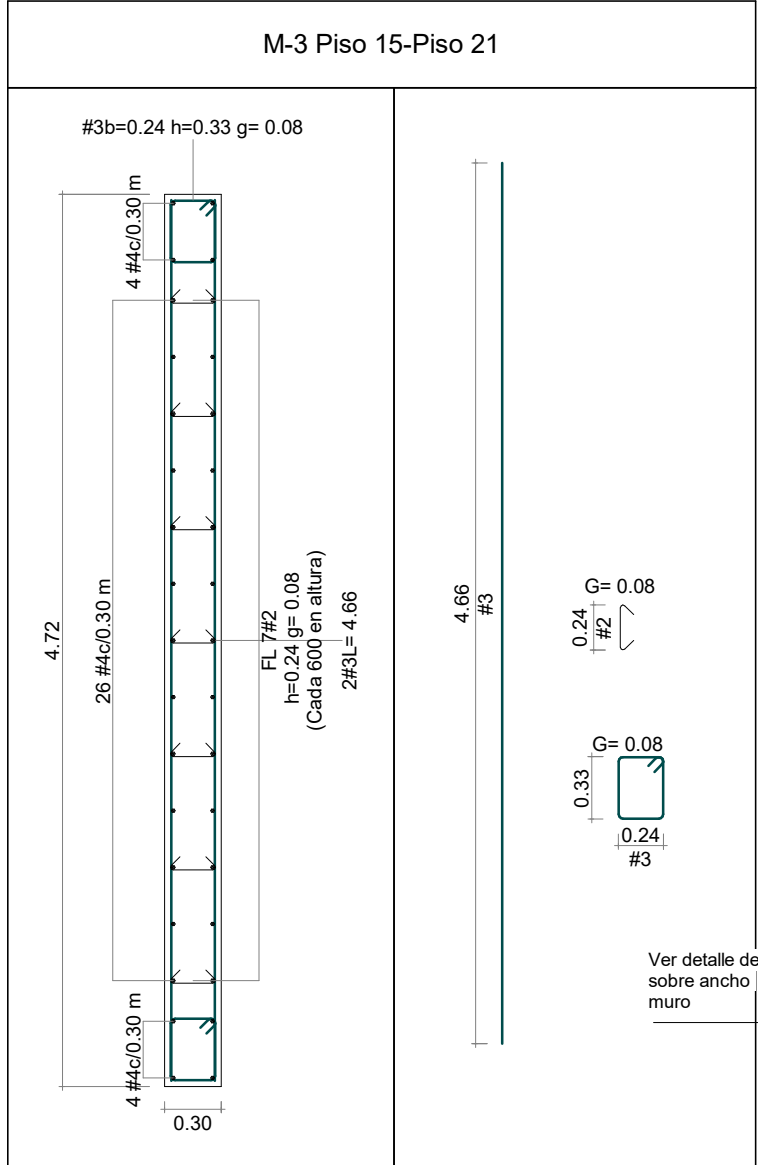
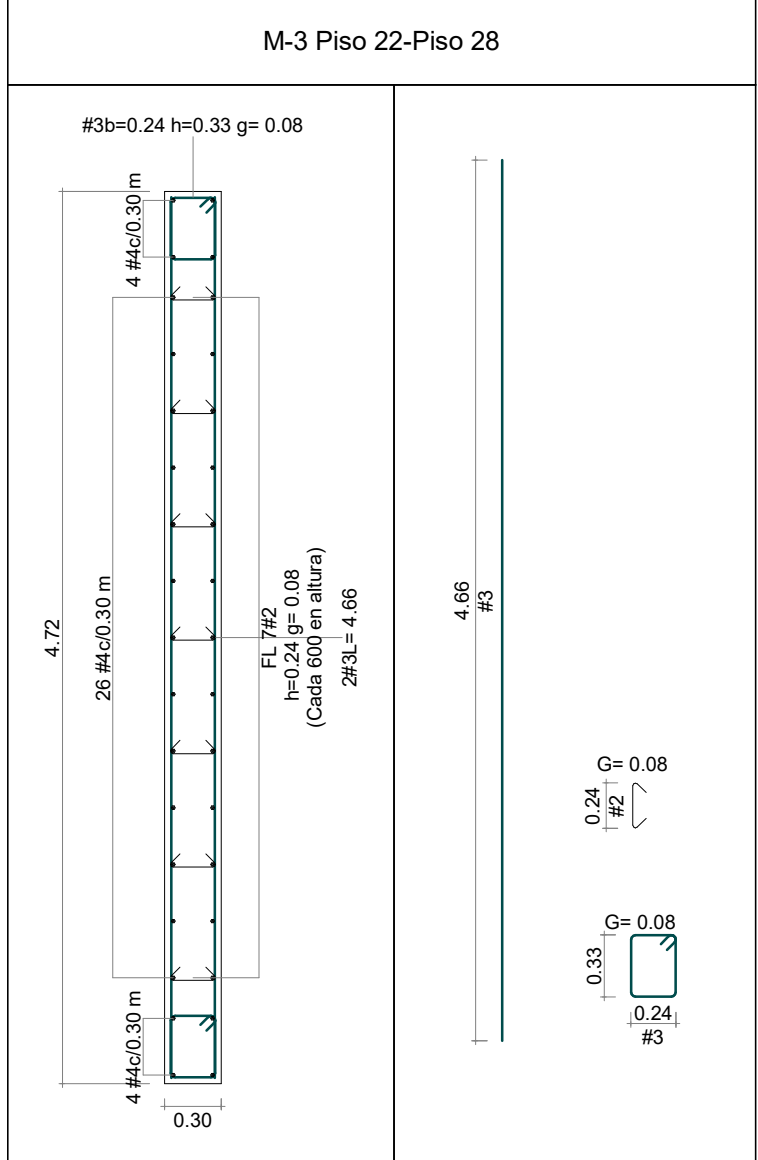
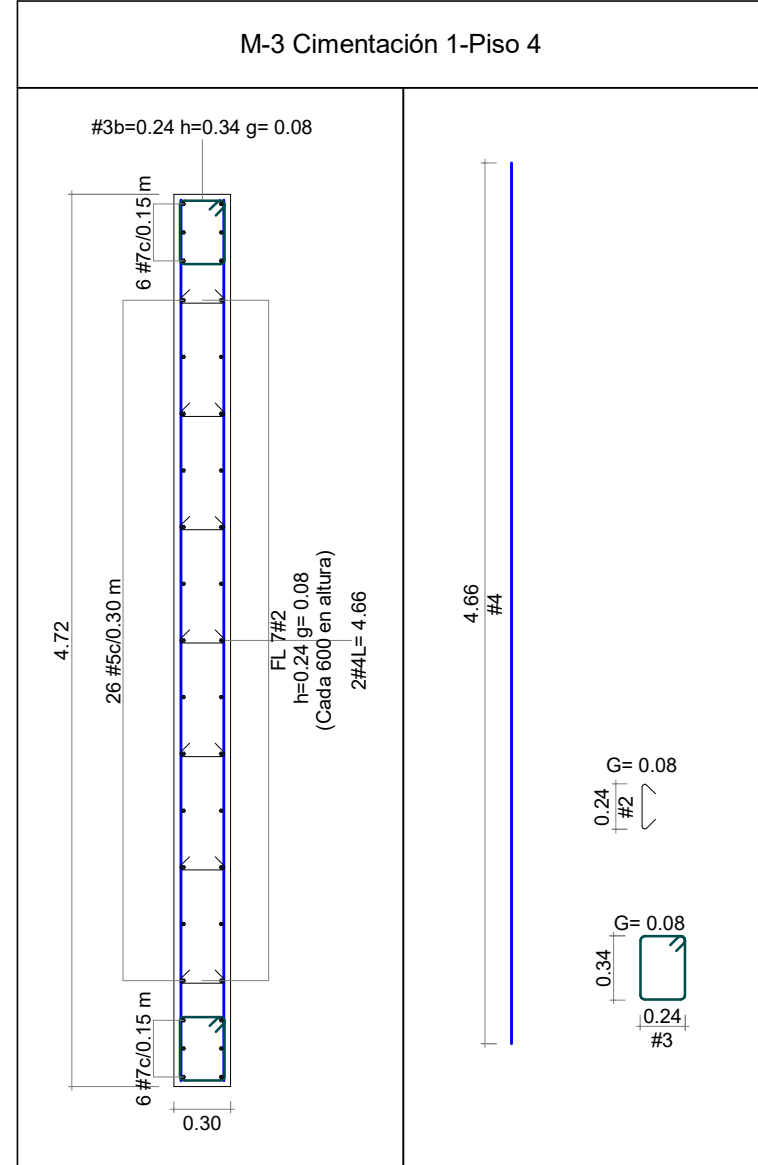
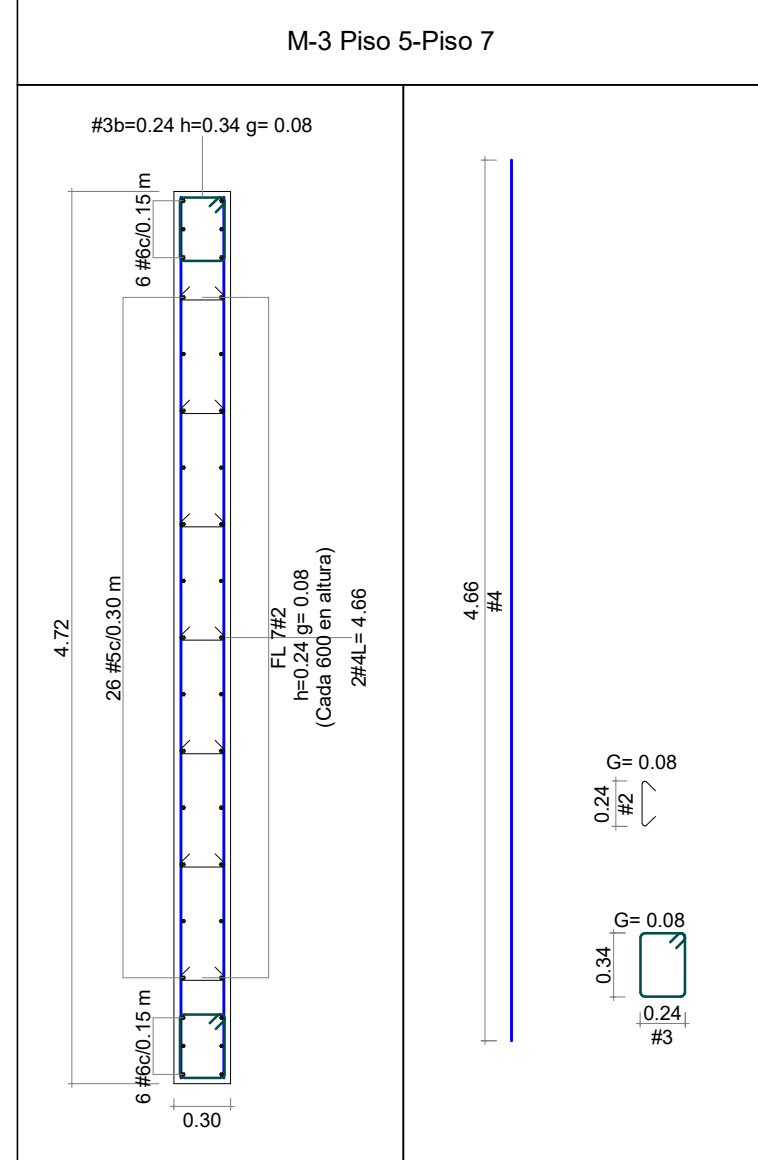
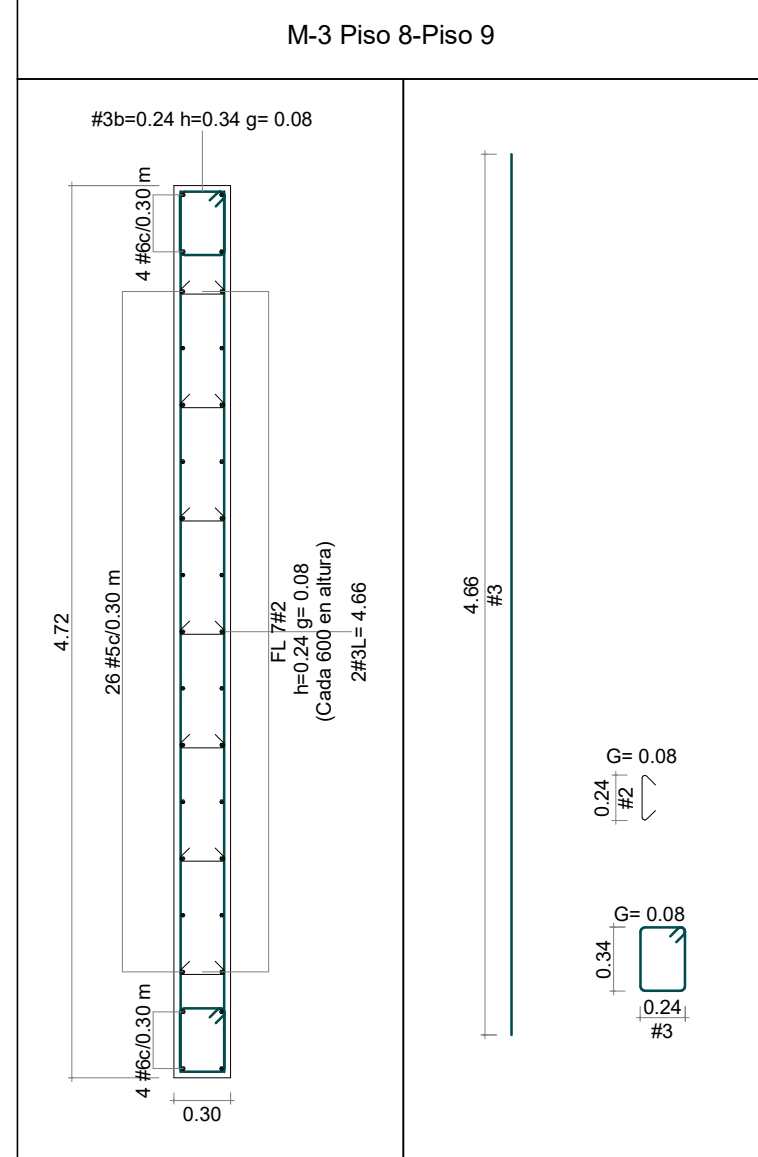
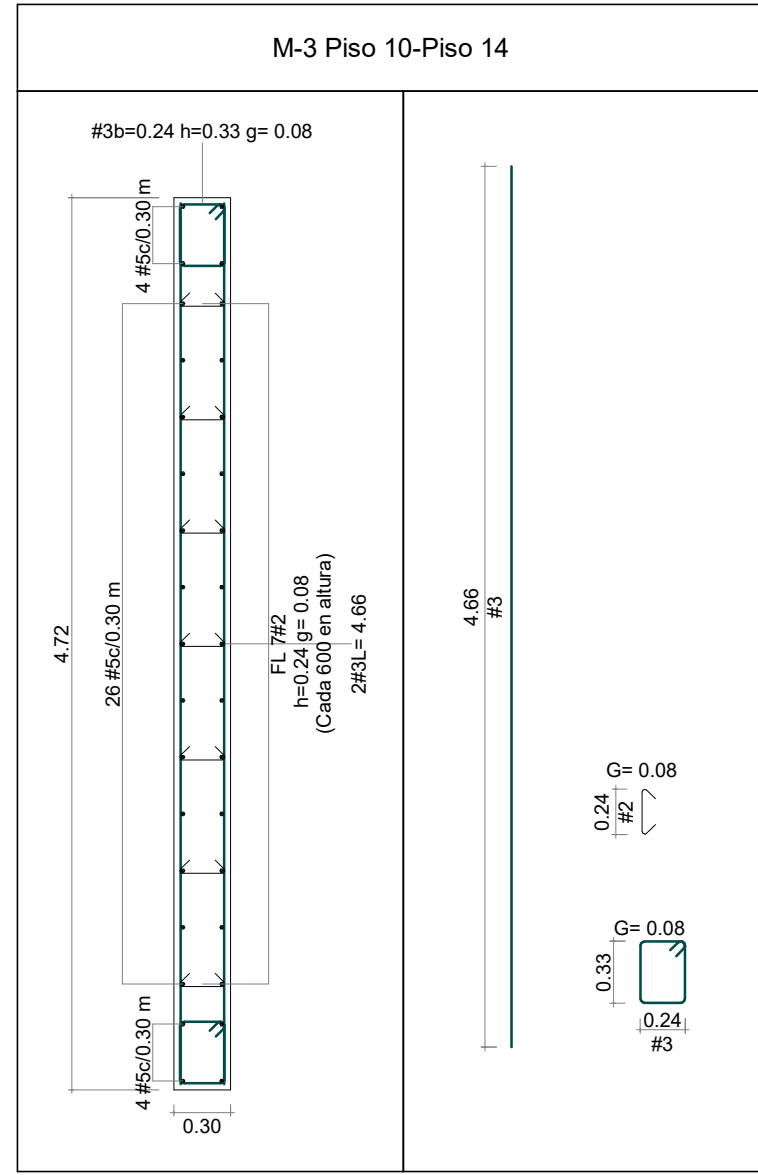
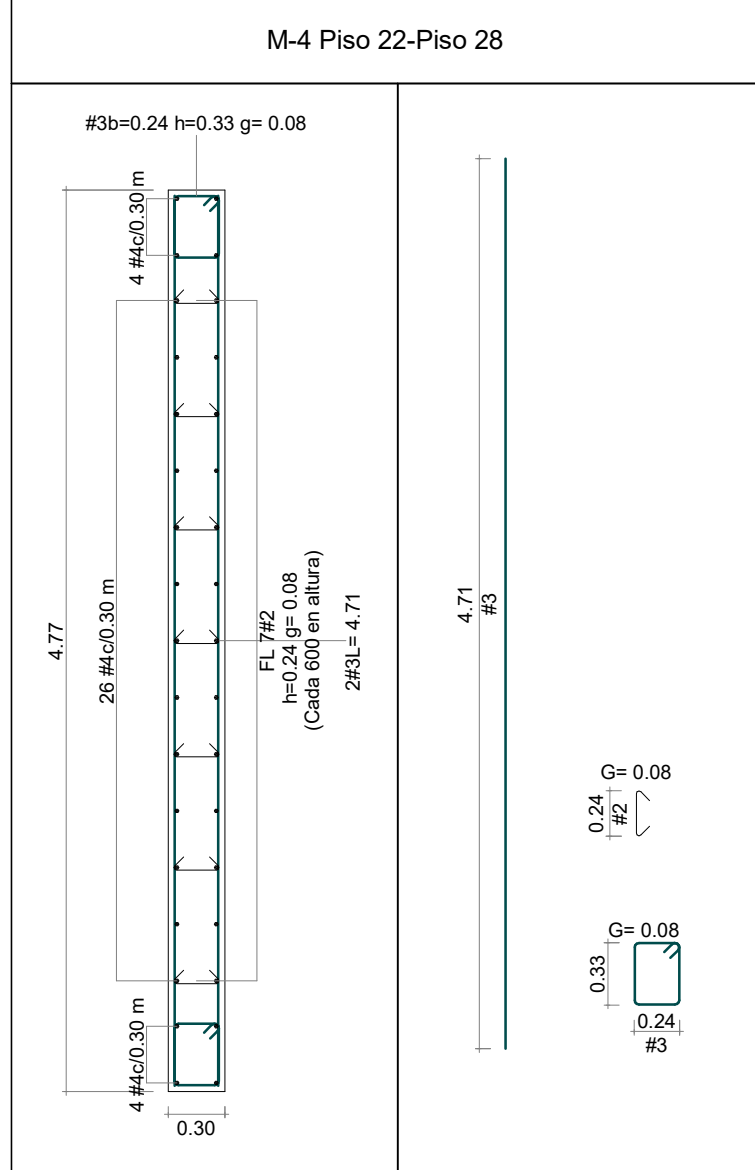
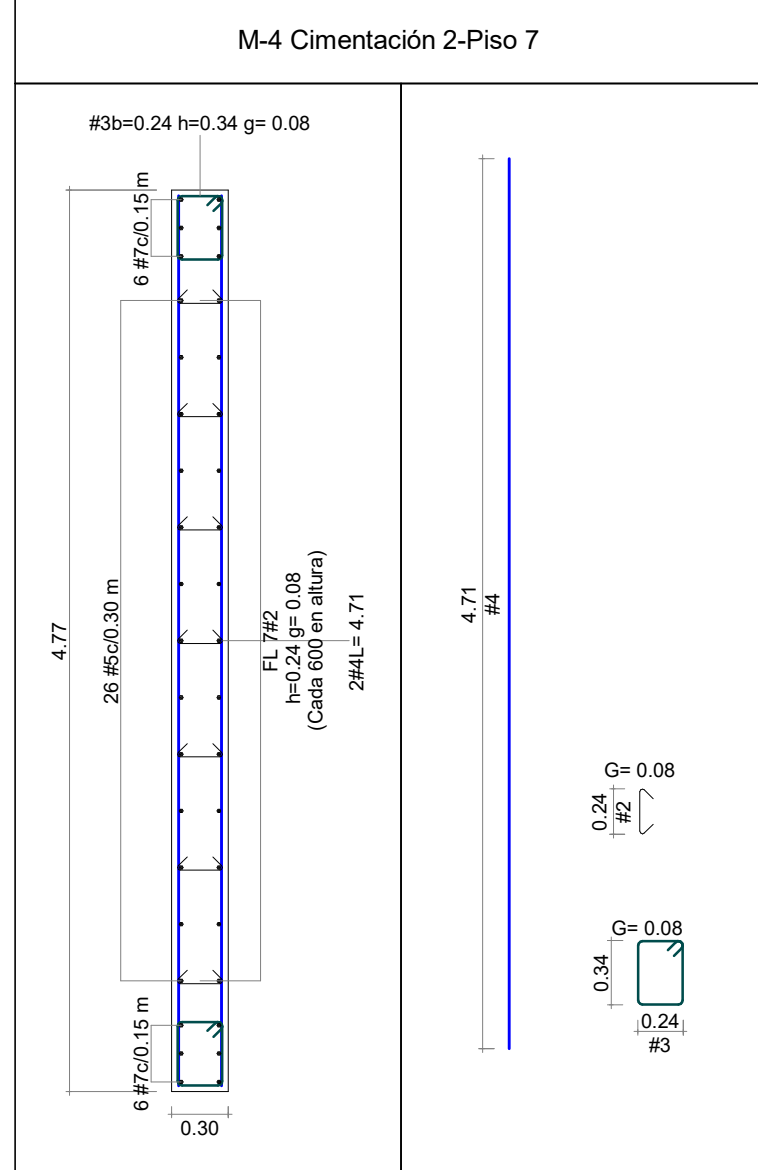
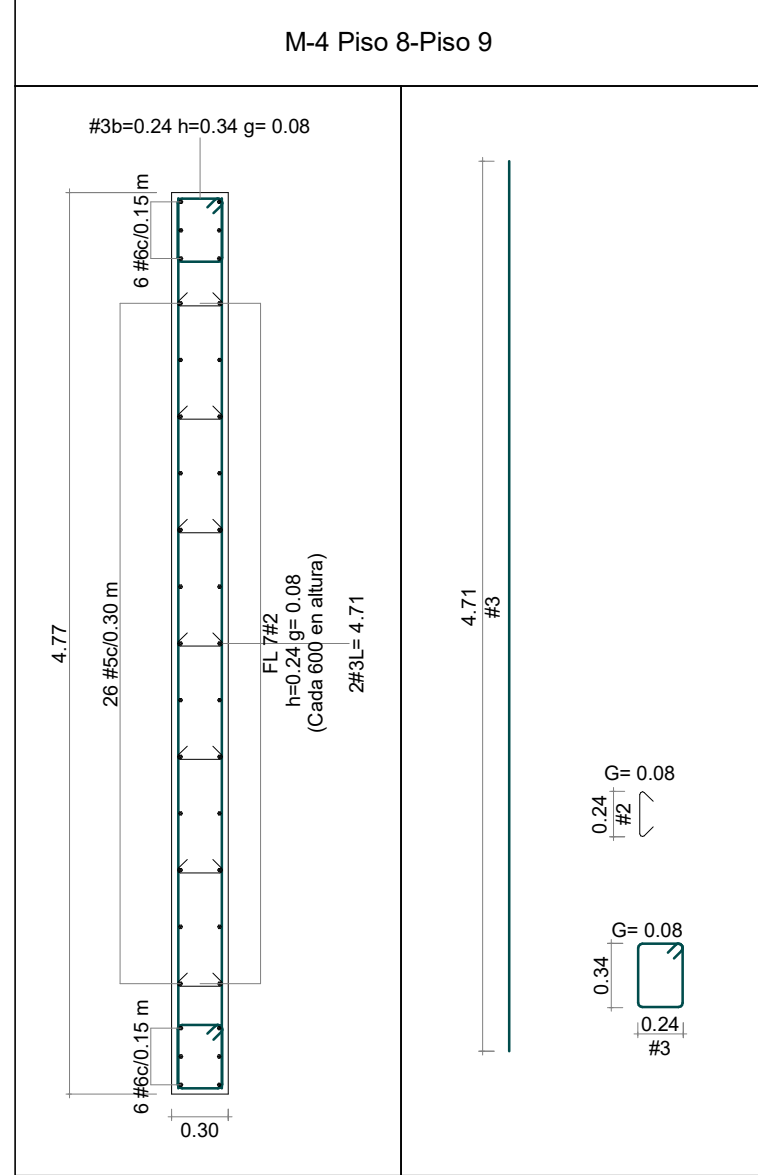
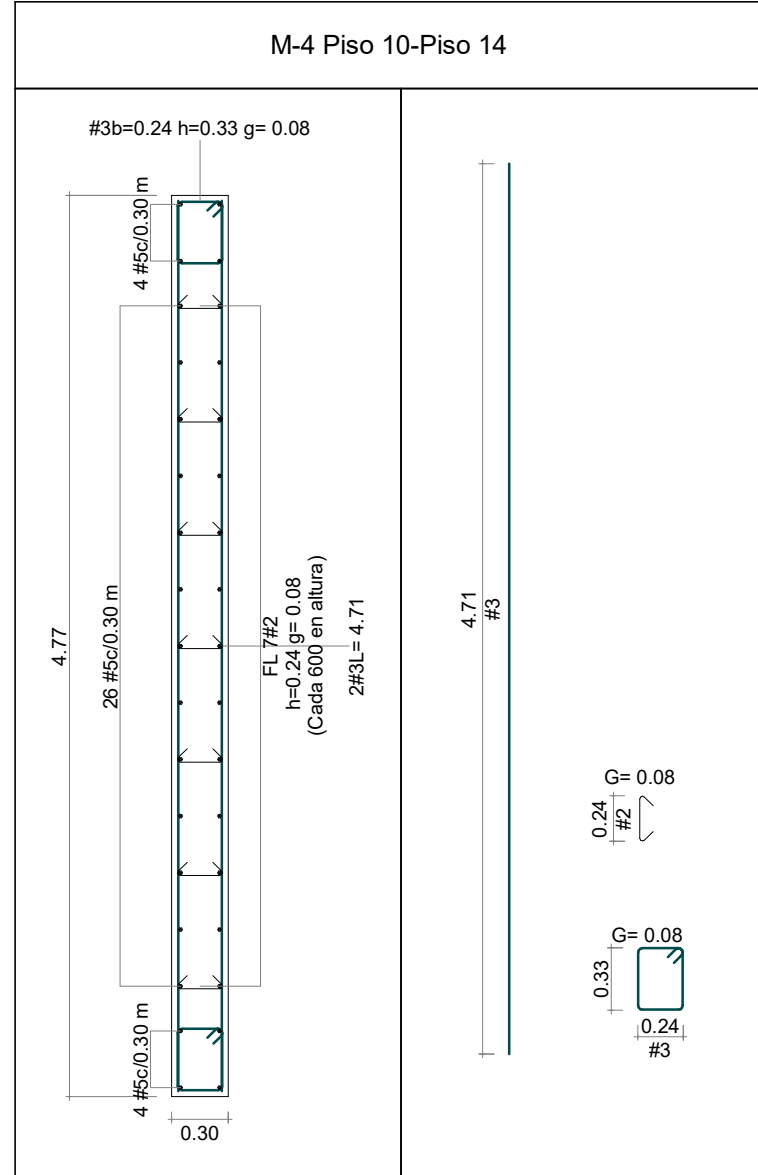
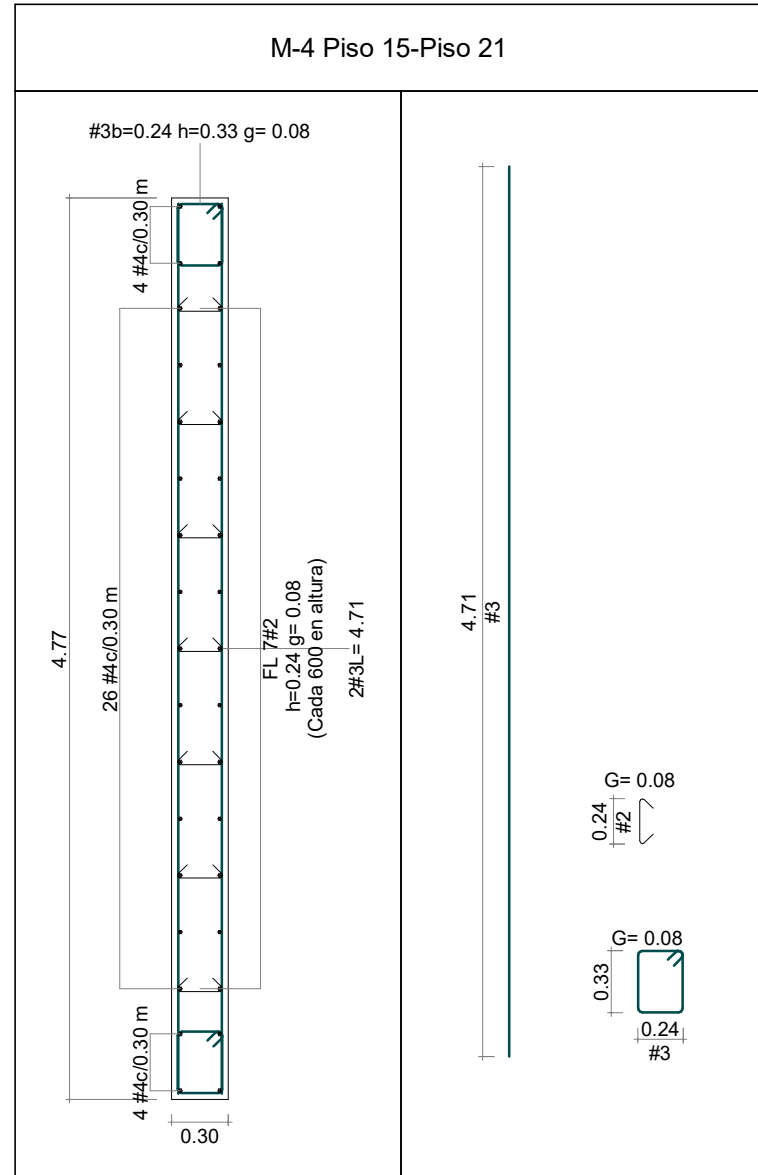


[illegible][illegible]

Technical drawing of a reinforced concrete column (Pilar) showing dimensions and reinforcement details.

Dimensions:

- Top section width: 0.50
- Top section height: 0.13
- Column diameter: 0.30
- Column height: 4.16
- Bottom section height: 0.30
- Bottom section width: 0.13

Reinforcement Details:

- Longitudinal bars: Ø16
- Stirrups: Ø8
- Reinforcement cage at top: 2Ø16
- Reinforcement cage at bottom: 2Ø16

Labels:

- ① (Top section)
- ② (Bottom section)
- SOBRE ANCHO (Over width)

DETALLE SOBRE ANCHO EN MURO M-4
Escala 1 : 25

CALLE 170 CON AV. BOYACA

DESPIECE DE MUROS

LA SCALA_EST_TOR-1_11.03_MUR-D4

REVISOR ESTRUCTURAL
N ANDRÉS ALVAREZ MANTILLA
MAT. 25202-346546 CND.

PLANO N°	VERSIÓN :
----------	-----------

11.03

4

VERSIÓN:

4

PLANO N°

11.03

GERENTE DE PROYECTO
ROBERTO AYCARDI F.
MAT. 2520257258 CNE

INGENIERO
CARLOS ANDRÉS WILCHES C.

MODELADOR
IVEL CASTELLANOS

MODIFICACIONES	FECHA
Emisión Inicial	28-02-2025
Ajuste longitudes refuerzos y se incluye detalle sobre ancho muro	03-10-2025
Actualización muro M-2	26-02-2026
Ajuste refuerzo muros	26-02-2026



LA SCALA

LA SCALA_EST_TOR-1

TORRE 1

CALLE 170 CON AV. BOYACA

DESPIECE DE MUROS

REVISOR ESTRUCTURAL
N ANDRES ALVAREZ MANTILLA
MAT. 25202-346546 CND.

PLANO N°

11.03

4

Aycardi
Estructural