

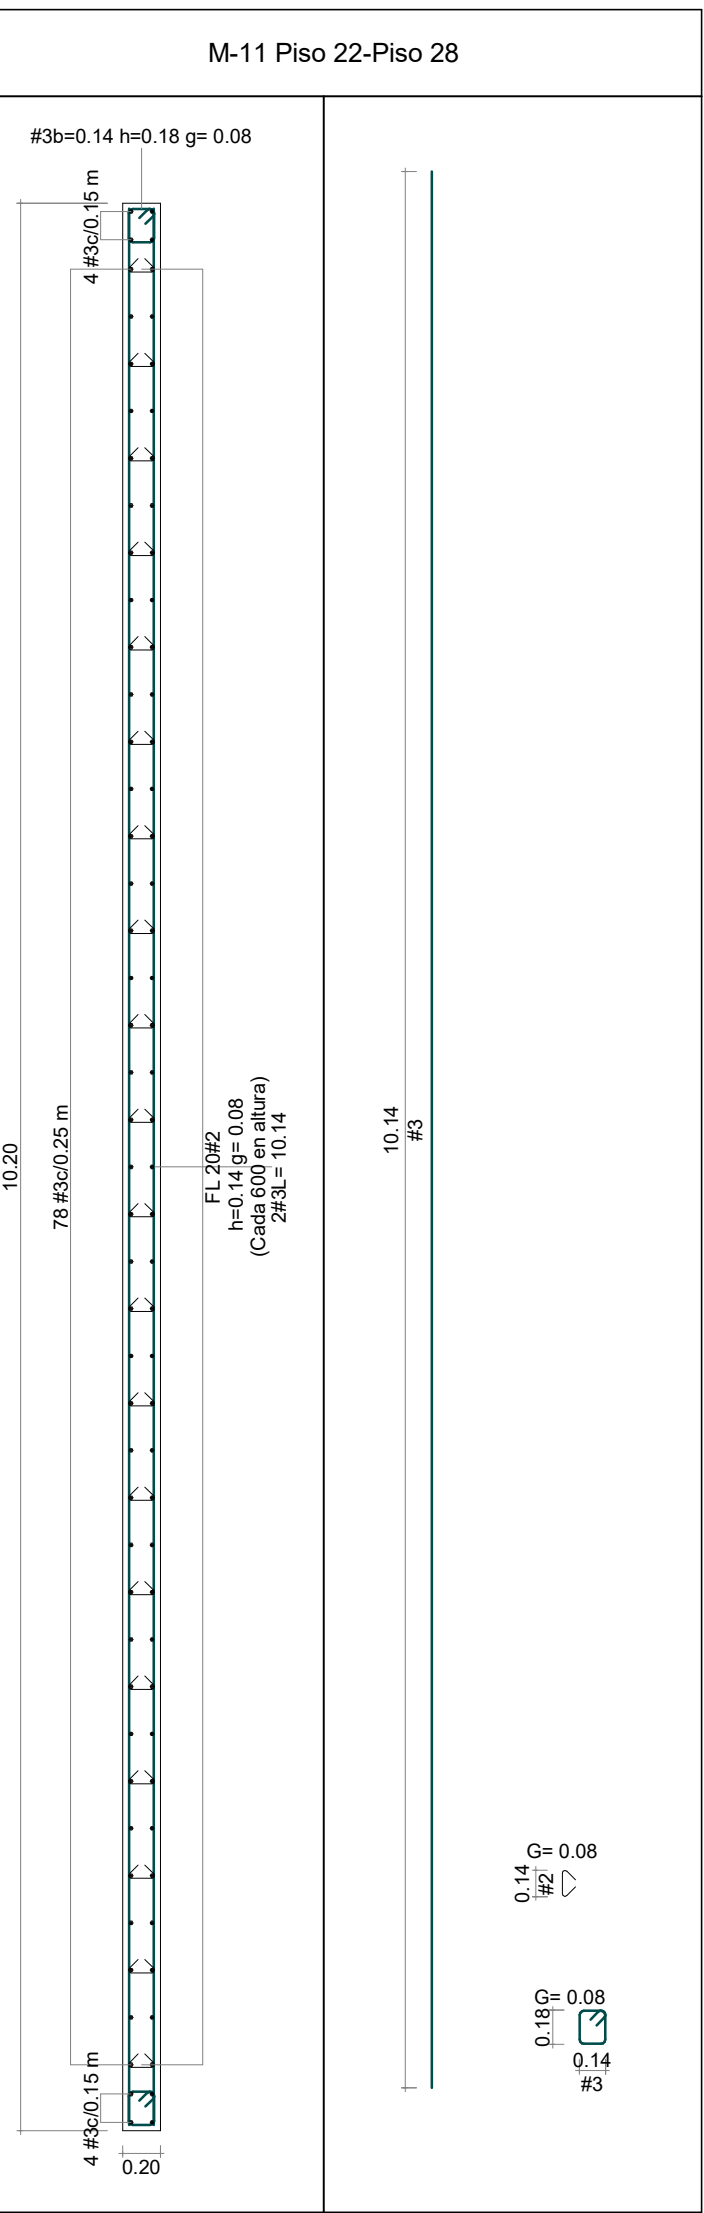
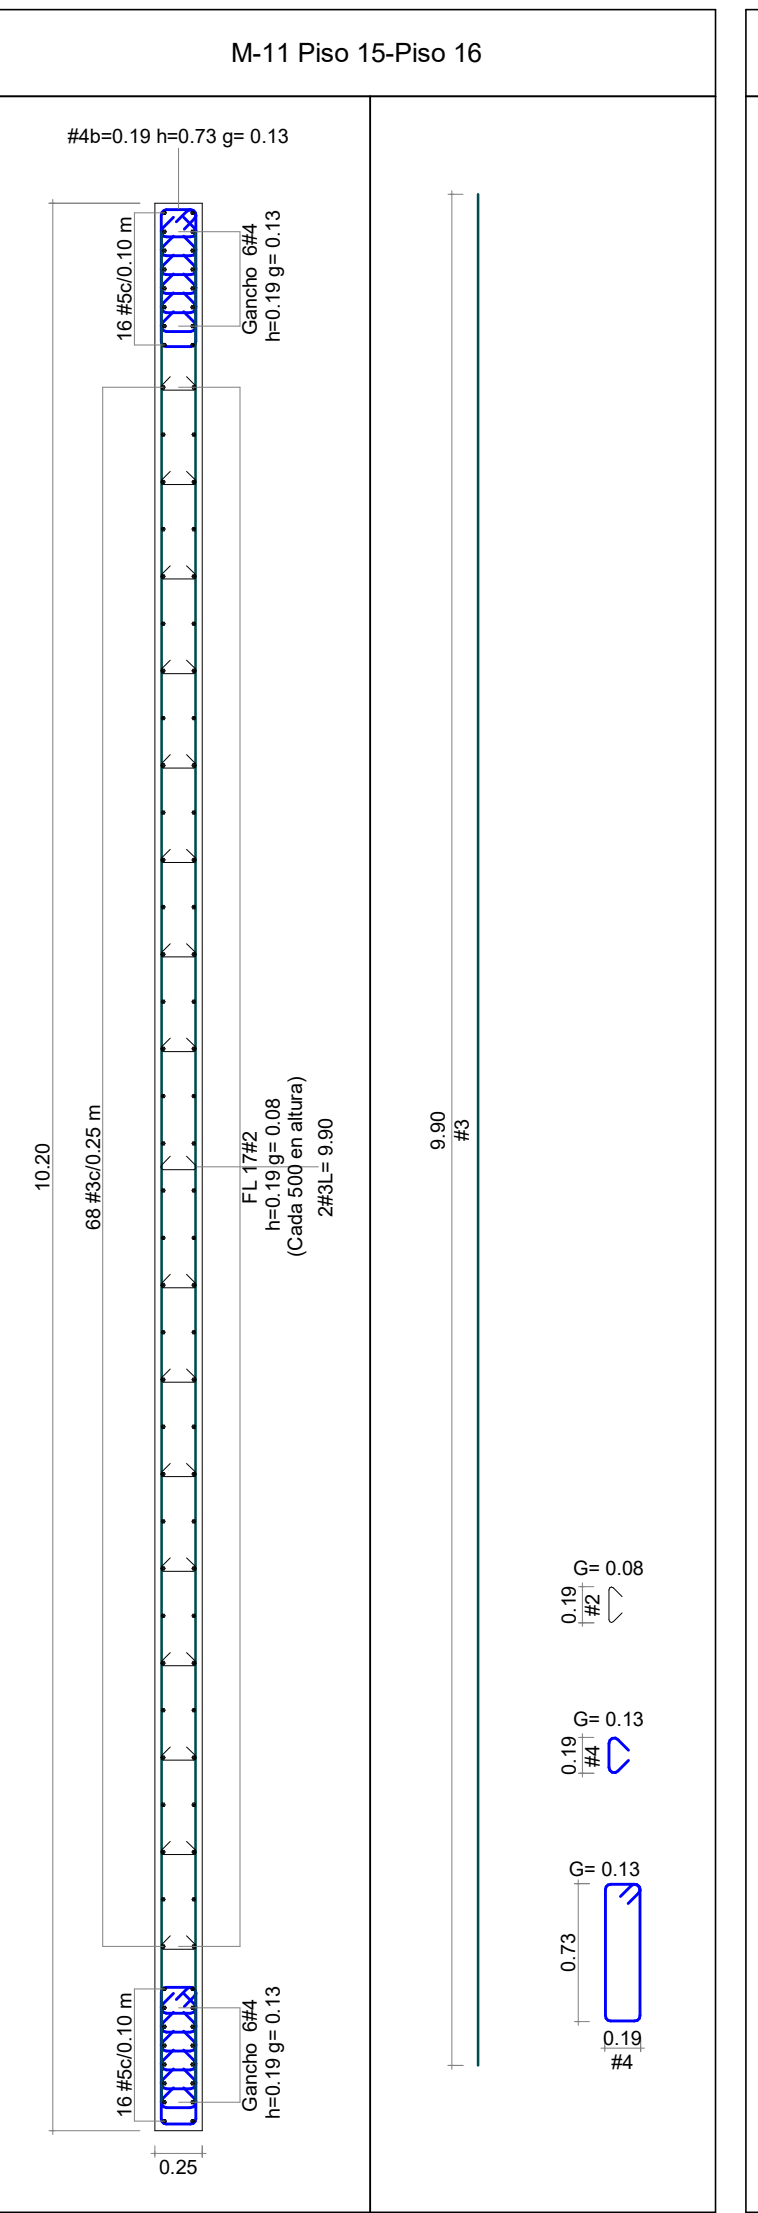
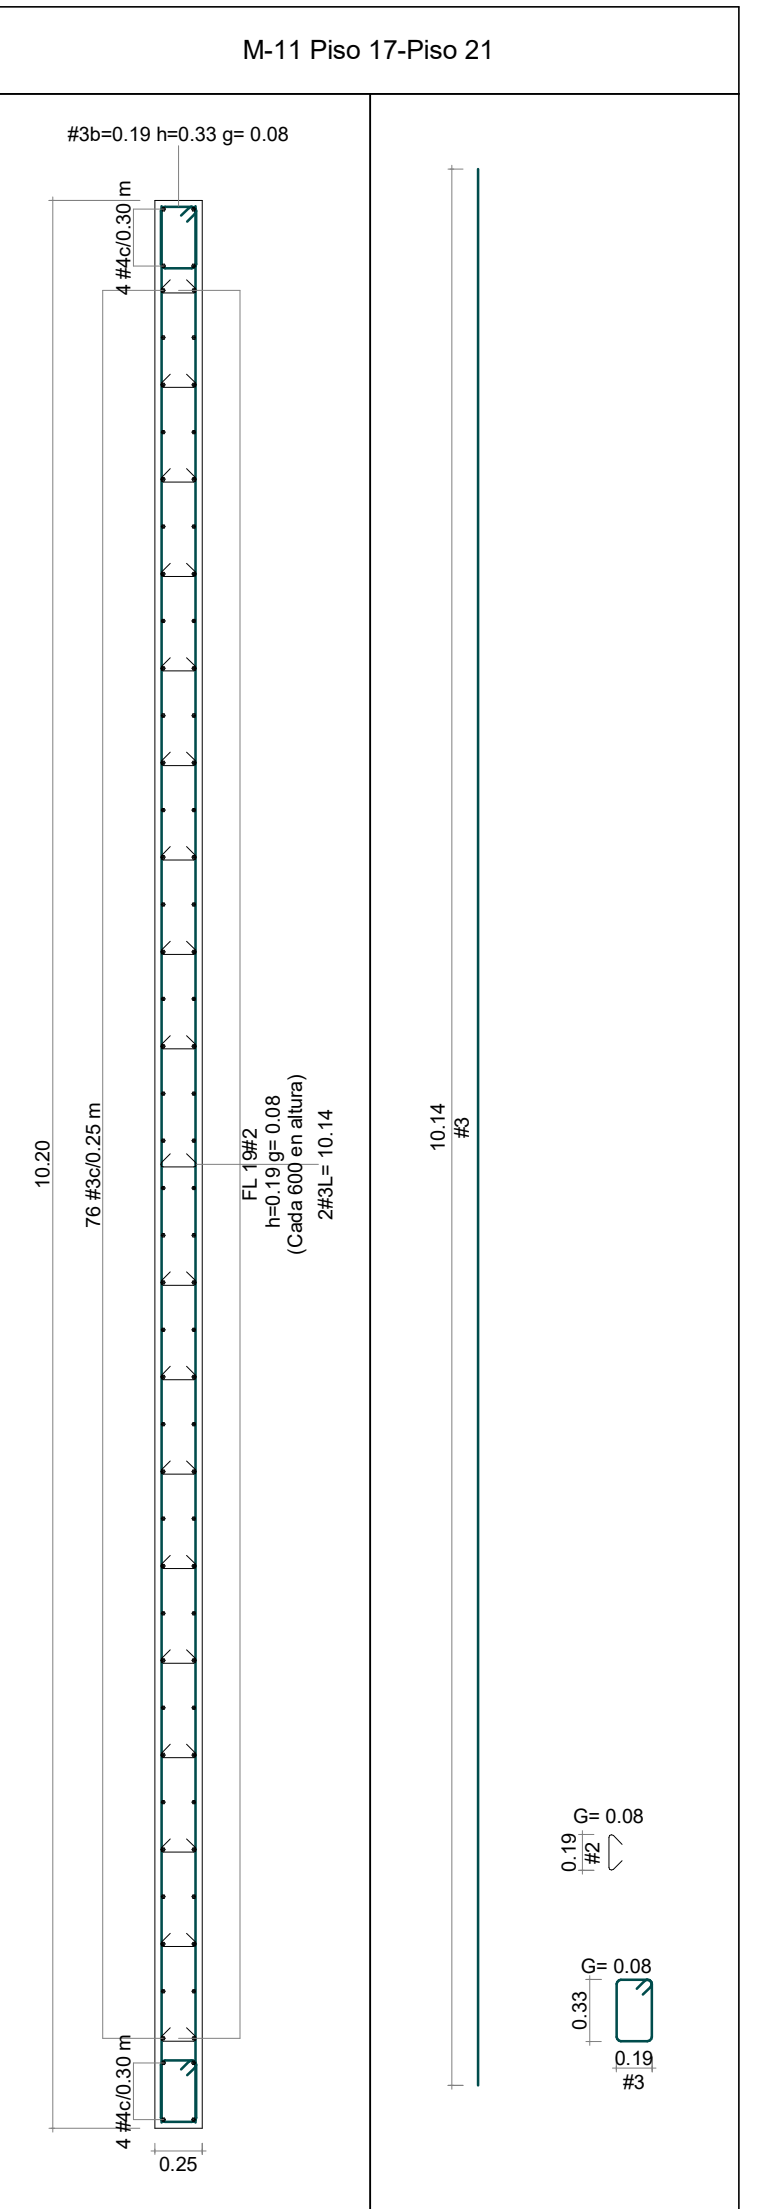
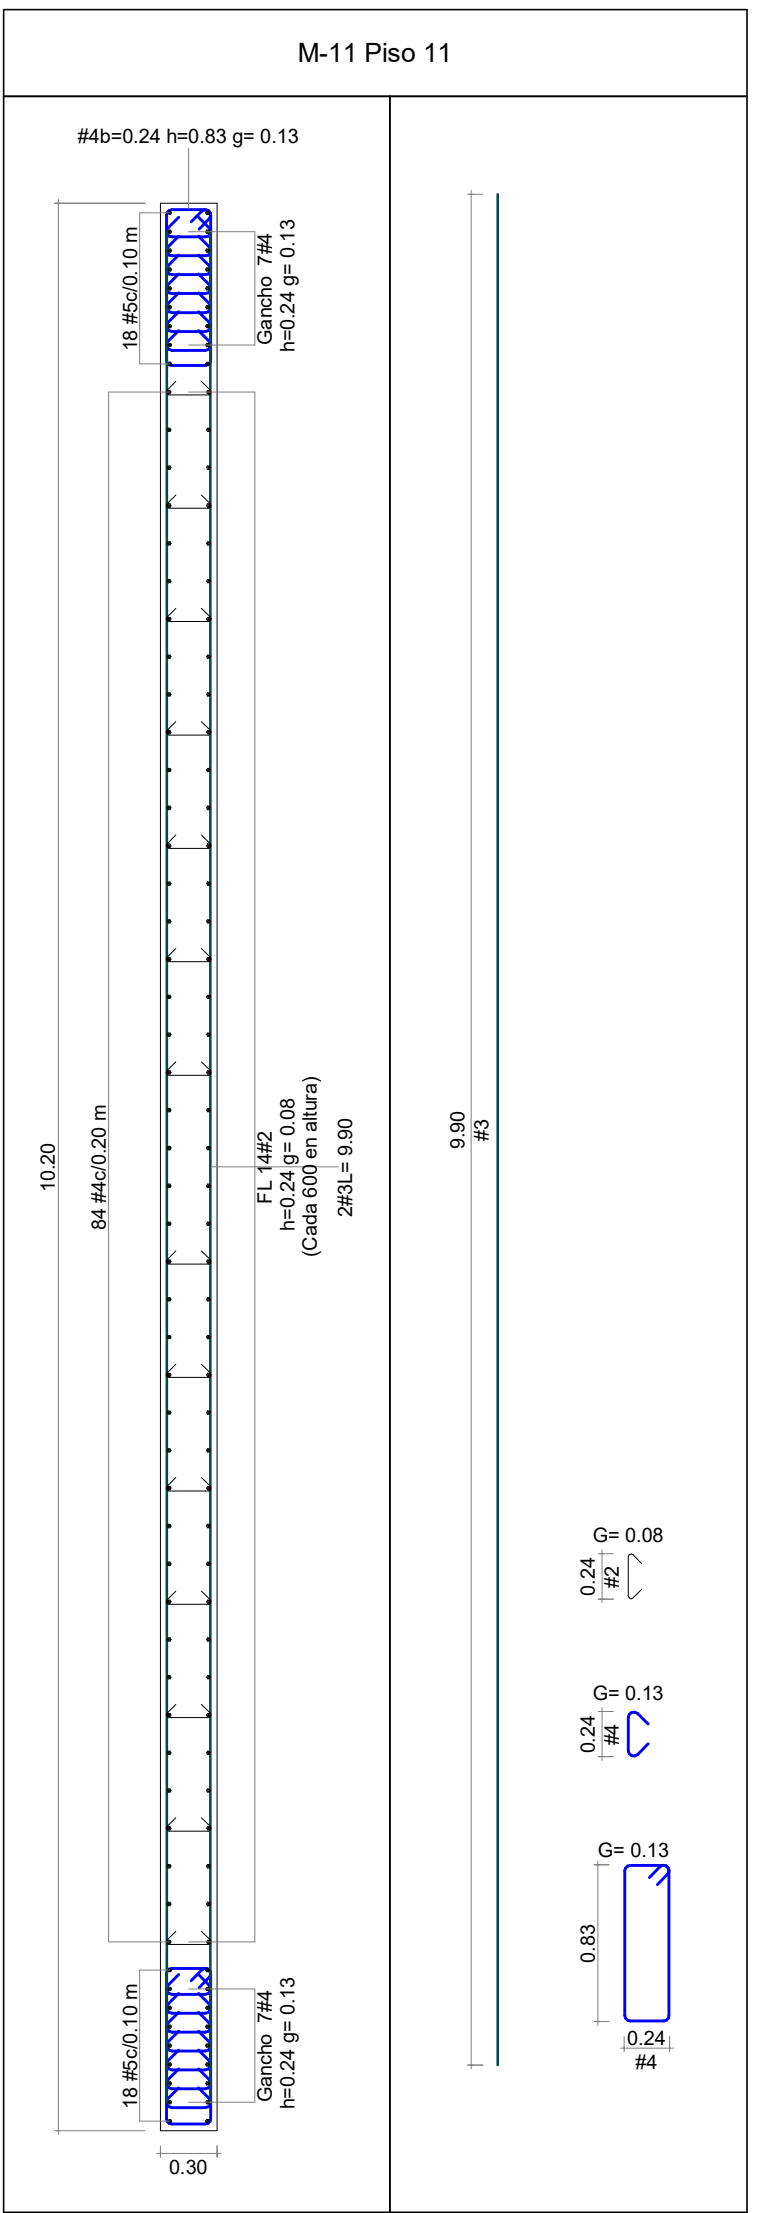
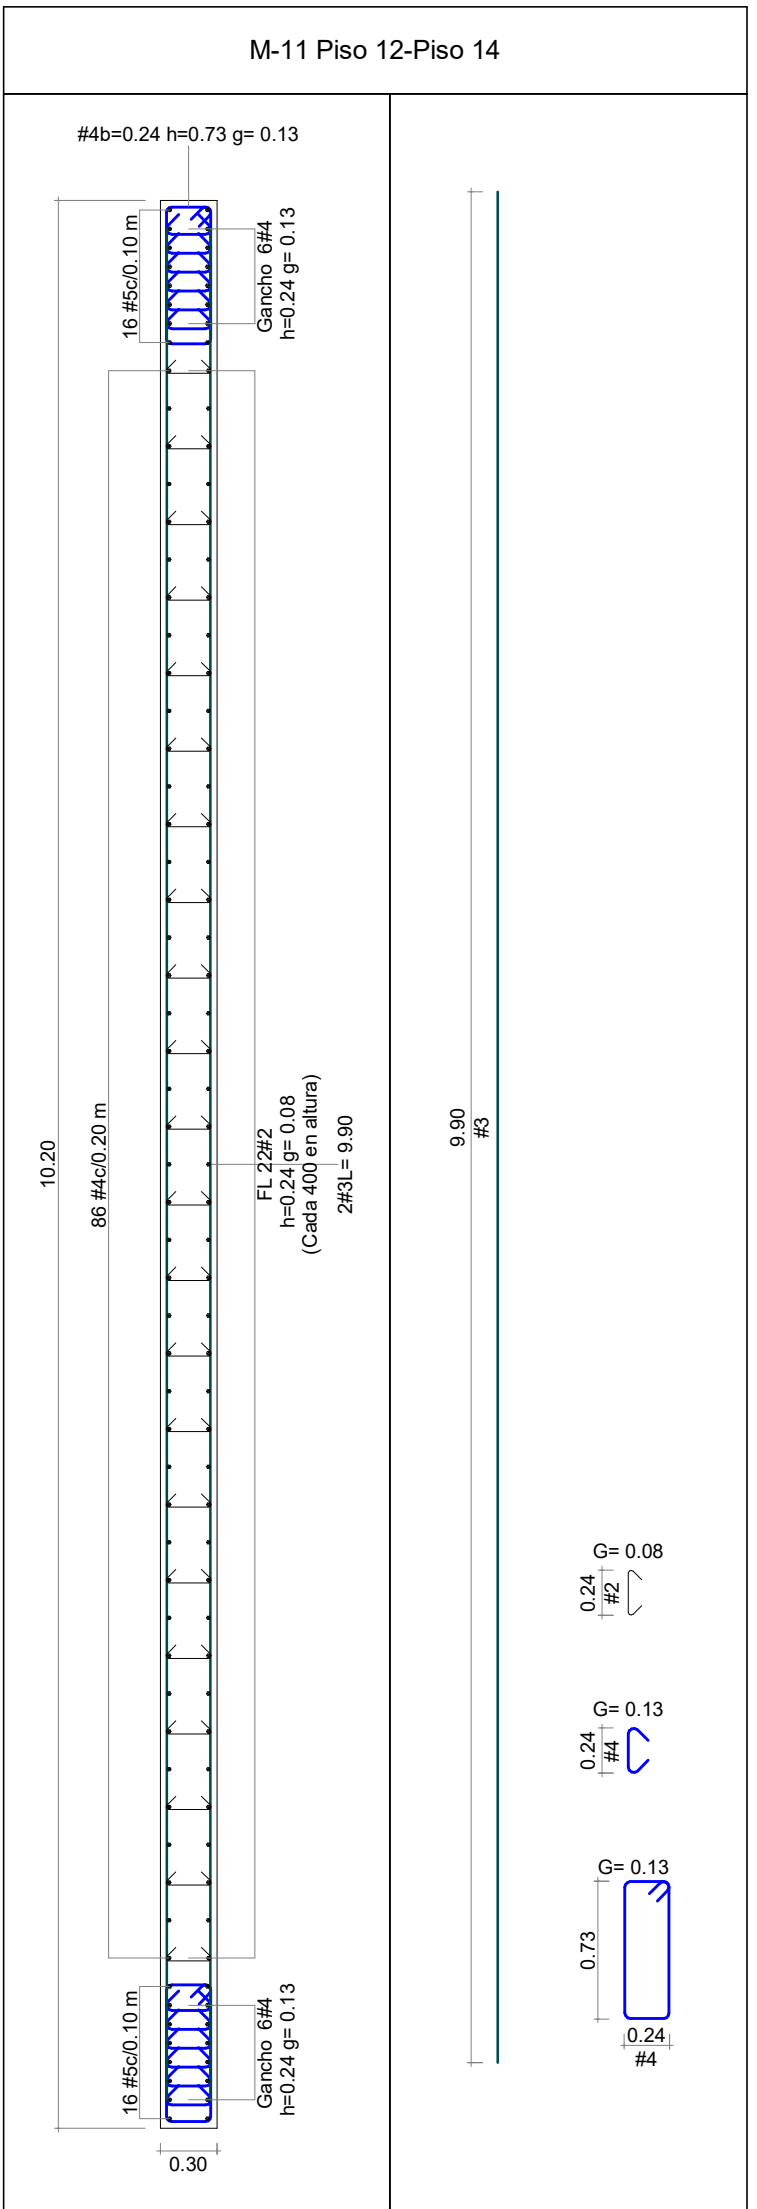
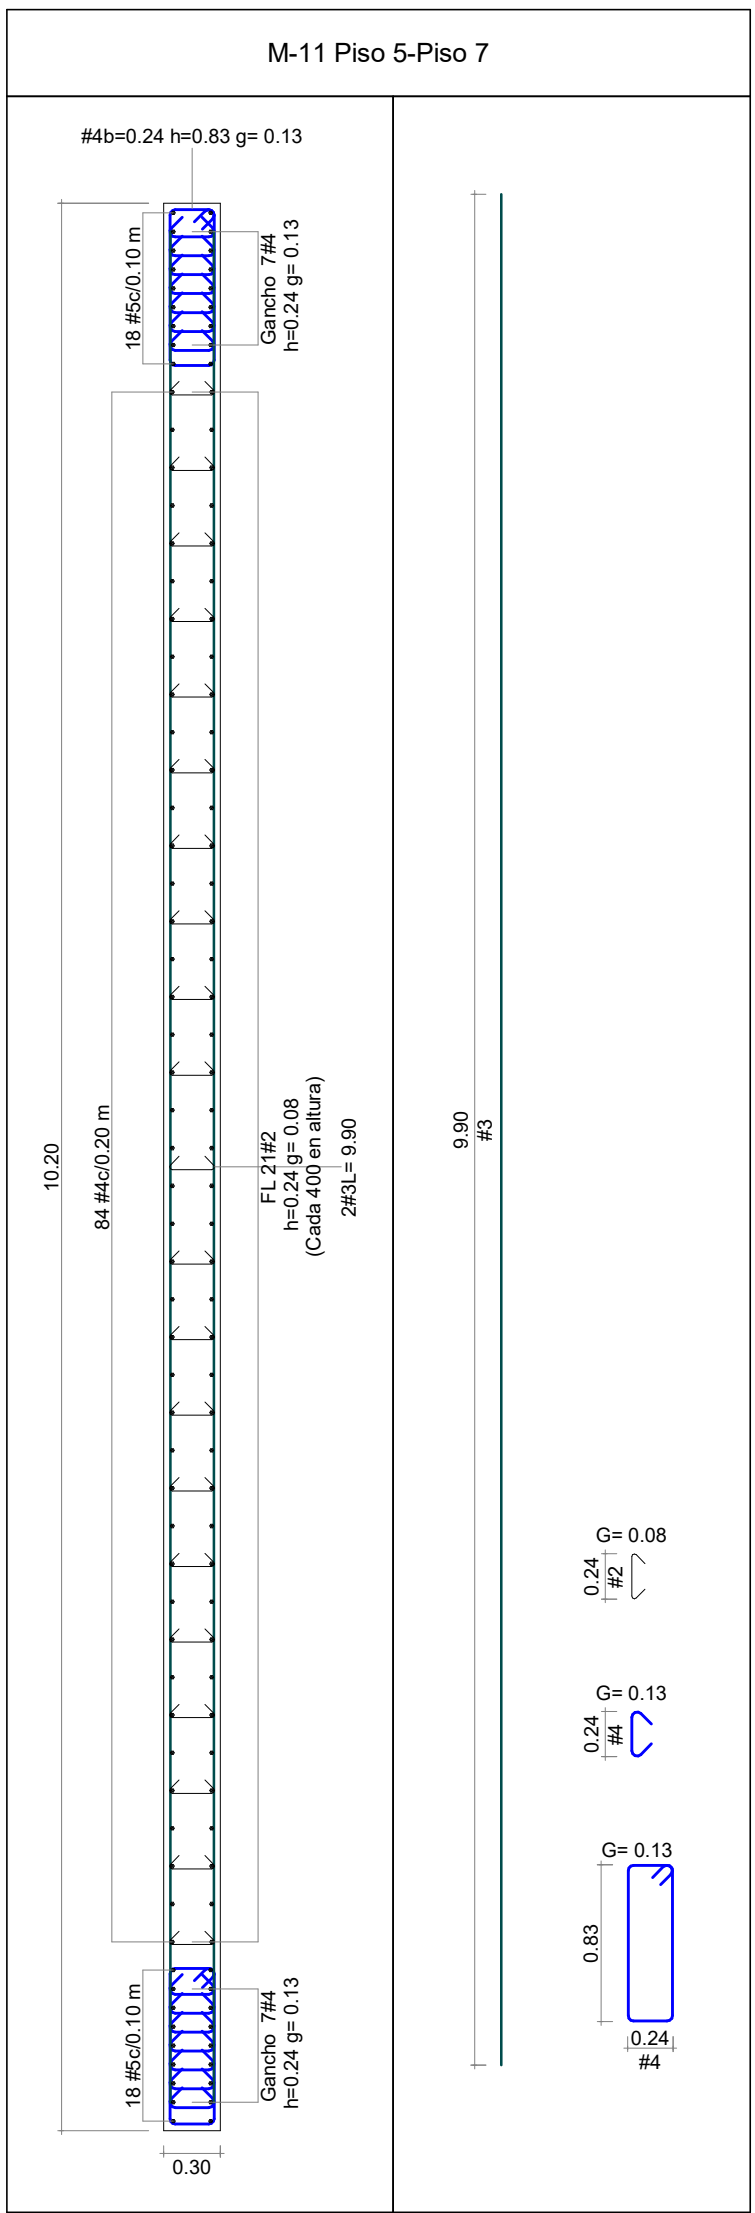
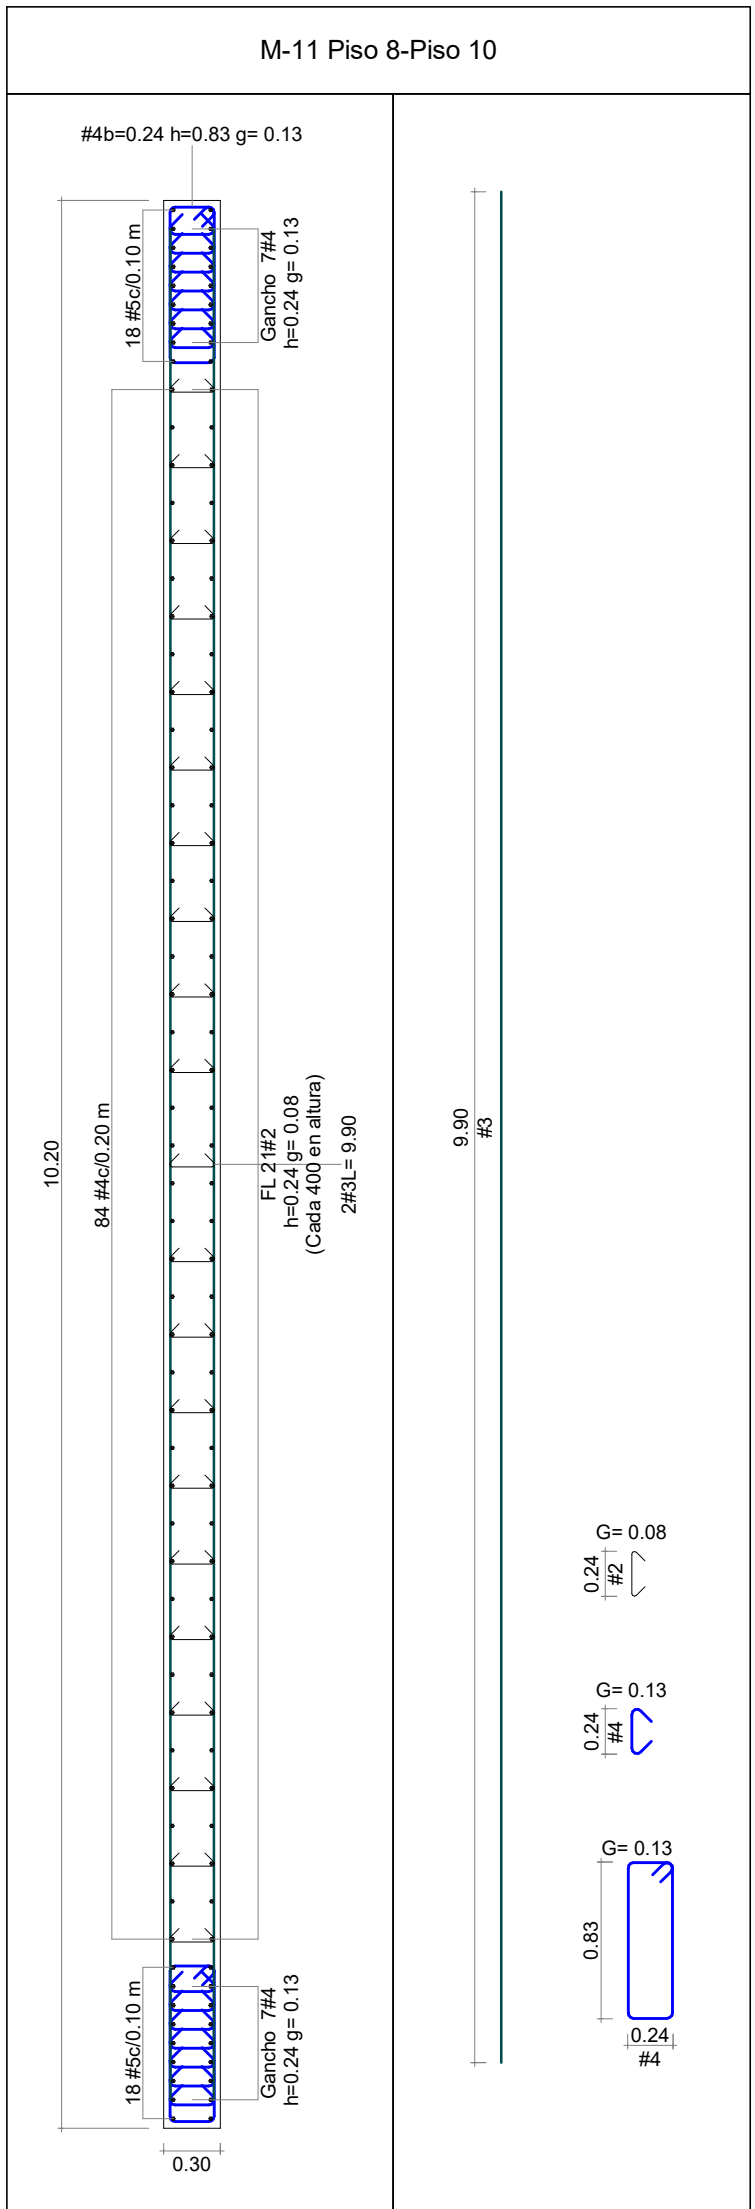
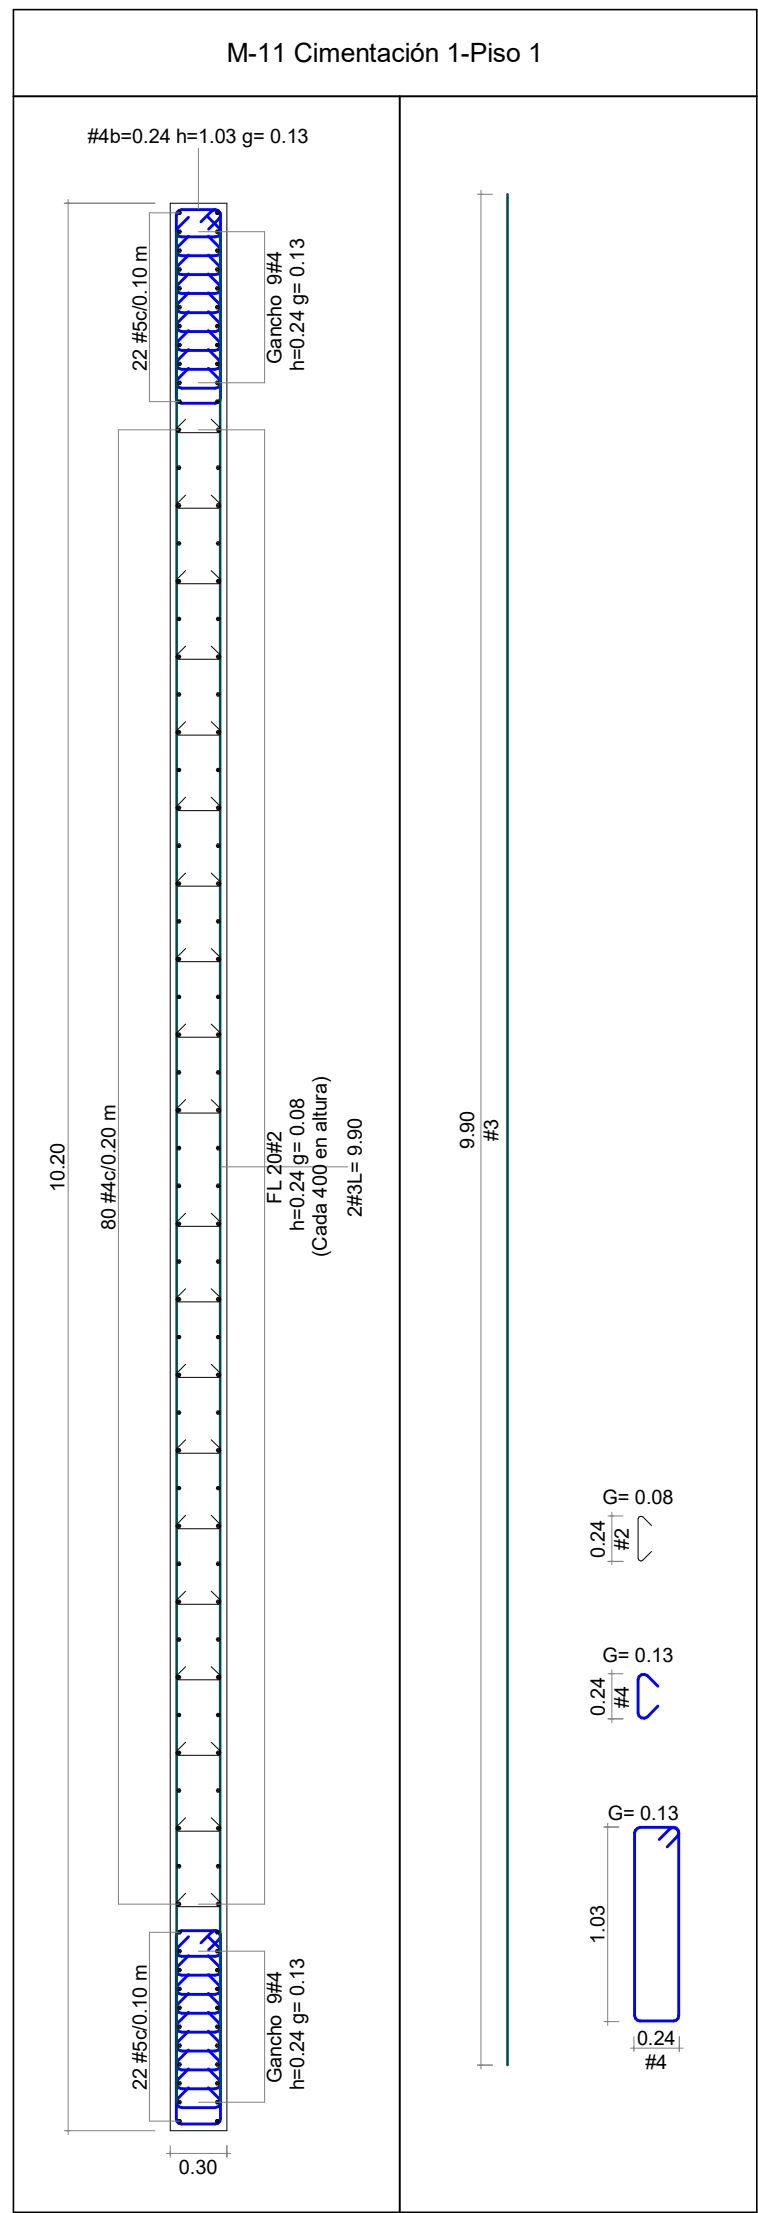


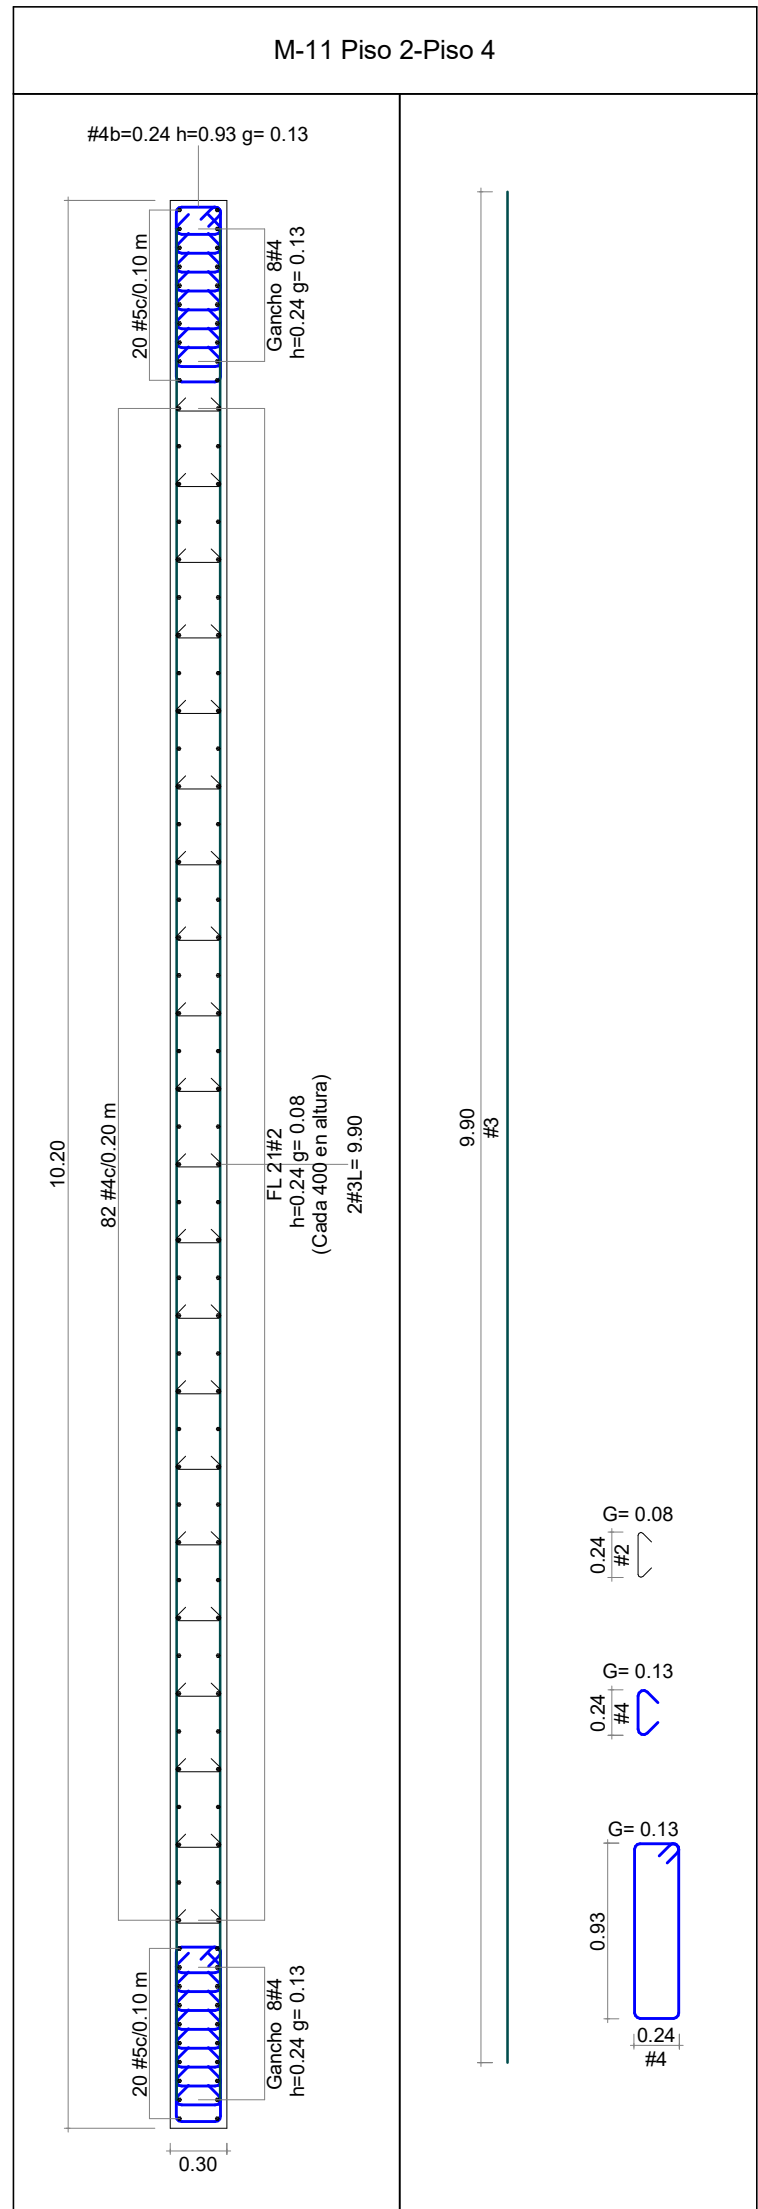


Ver detalle 1 en el
PLN° 11.22
Detalles cambio de
espesor en muros

Ver detalle 2 en el
PLN° 11.22
Detalles cambio de
espesor en muros

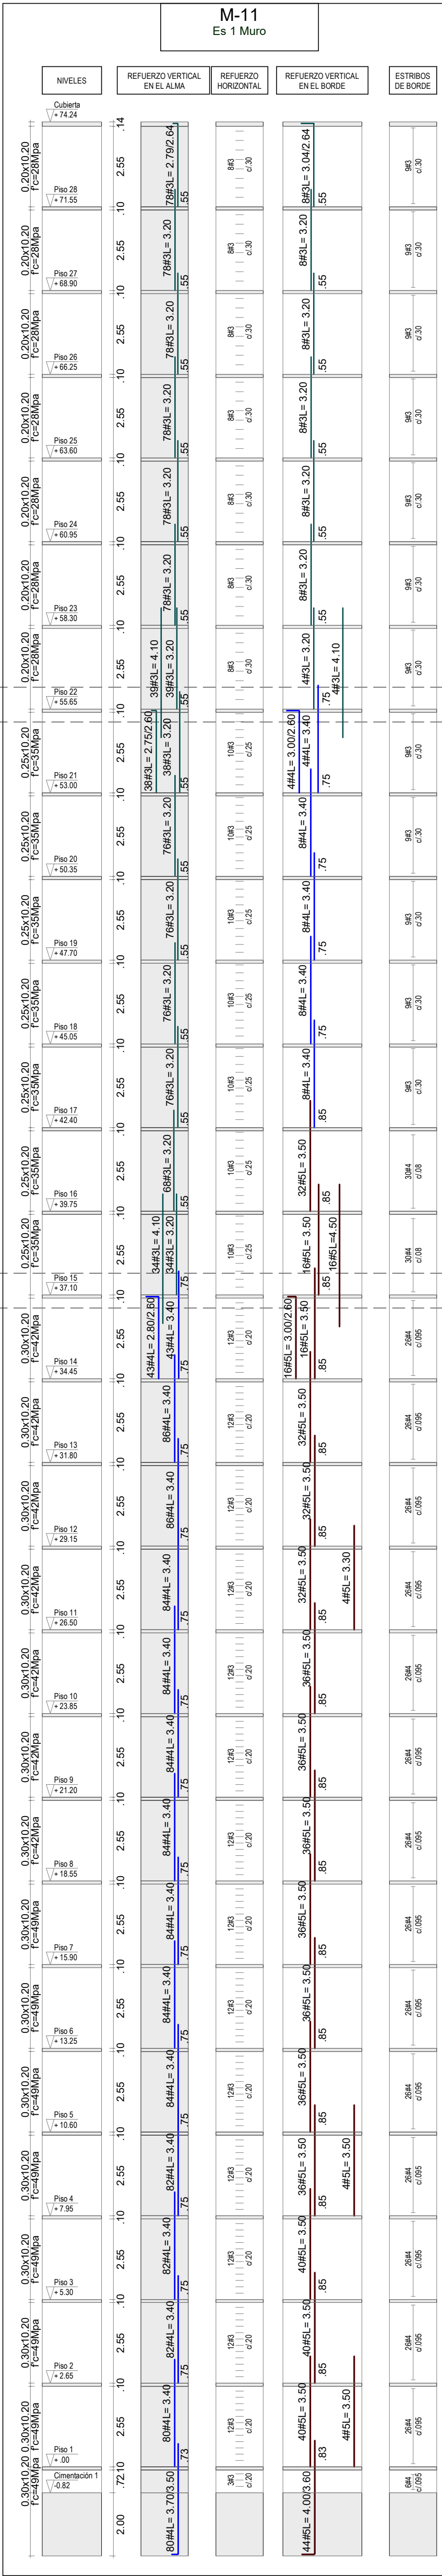

NOTAS:
1. Ver detalles generales en el PLN° 01.02
2. Ver detalles de muros en el PLN° 11.20
3. Ver plantas de localización e identificación de muros en los PL. N°03.00-04.00-05.00-06.00-07.00-08.00 y 09.00

ESCALA 1:125

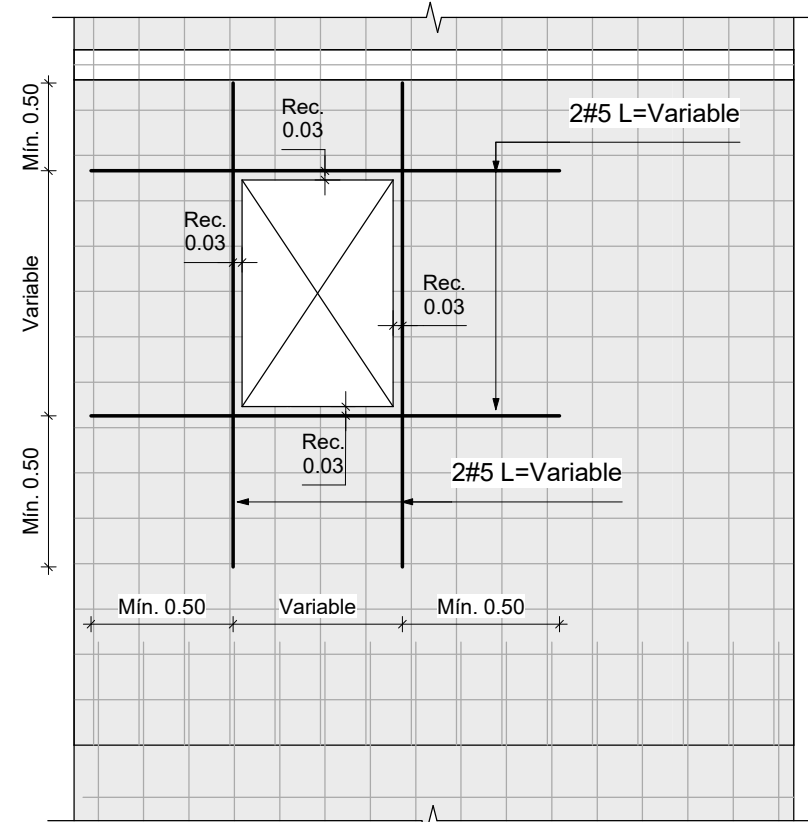

NOTA: EL REFUERZO INDICADO
ES POR CADA CARA DE MURO

PLANO N°
11.09

GERENTE DE PROYECTO
ROBERTO AYCARDI F.
MAT. 2520257258 CND

INGENIERO
CARLOS ANDRÉS WILCHES C.

MODELADOR
DANIEL CASTELLANOS

MODIFICACIONES	FECHA
Emisión Inicial	28-02-2025
Ajuste longitudes refuerzos	03-10-2025
Ajuste refuerzo muros	26-02-2026



LA SCALA

LA SCALA_EST_TOR-1

TORRE 1

CALLE 170 CON AV. BOYACA

DESPIECE DE MUROS

LA SCALA_EST_TOR-1_11.09_MUR-D10

REVISOR ESTRUCTURAL
RAMÓN ANDRÉS ALVAREZ MANTILLA
MAT. 25202-346546 CND.

PLANO N°

11.09

VERSIÓN :

3

Aycardi
Estructural