NOTAS:

1. Ver detalles generales en el PL.N° 01.02
2. Ver detalle de muros en el PL.N° 11.20
3. Ver plantas de localización e identificación de muros en los PL. N°03.00-04.00-05.00-06.00-07.00-08.00 y 09.00

ESCALA 1:125

M-15
Es 1 Muro

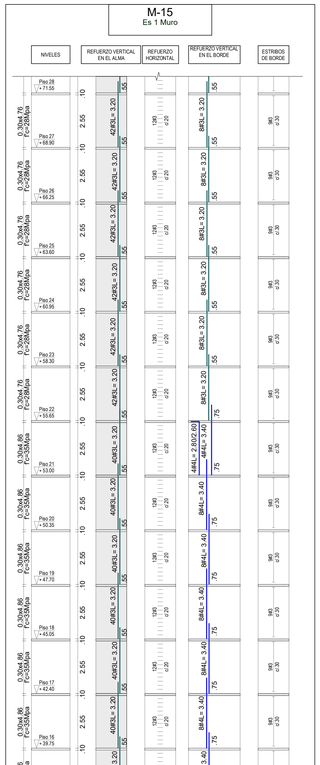

M-15
Es 1 Muro

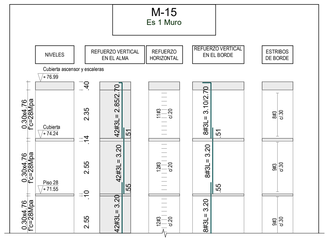

M-15 Piso 8-Piso 10

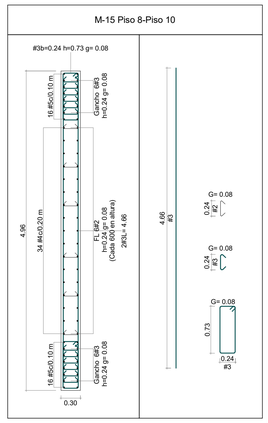

M-15 Piso 22-Cubierta

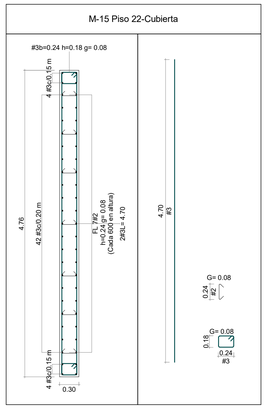

M-15 Piso 3-Piso 7

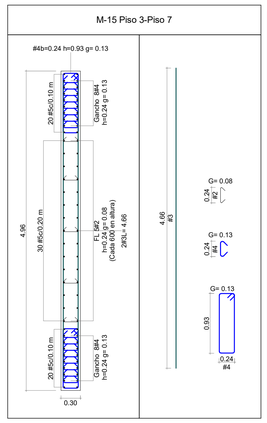

M-15 Piso 15-Piso 21

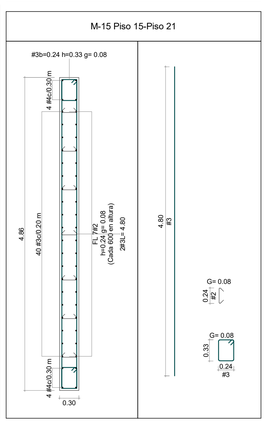

M-15 Cimentación 1-Piso 2

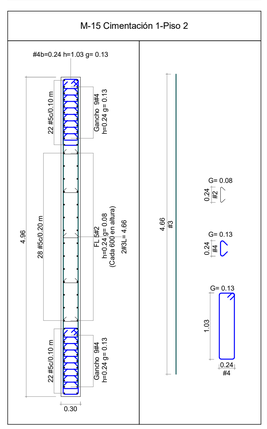

M-15 Piso 11-Piso 14

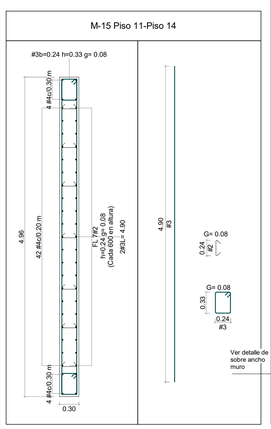

Ver detalle de sobre ancho muro

M-15A
Es 1 Muro

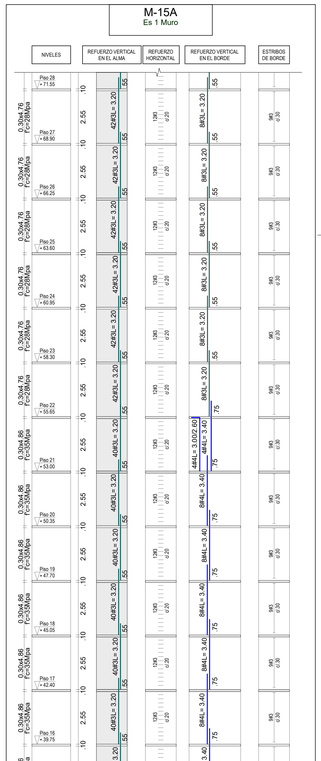

M-15A
Es 1 Muro

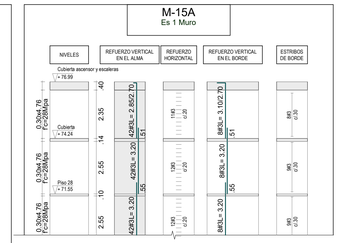

M-15A Piso 4-Piso 7

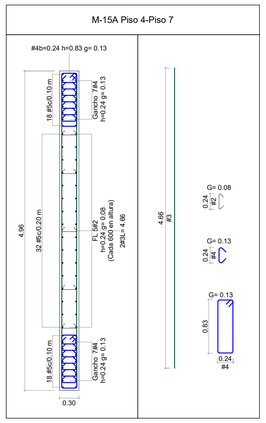

M-15A Piso 15-Piso 21

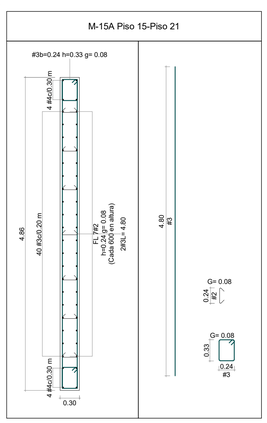

M-15A Piso 2-Piso 3

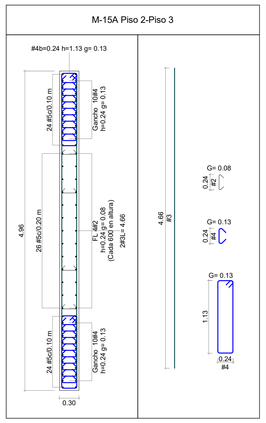

M-15A Piso 11-Piso 14

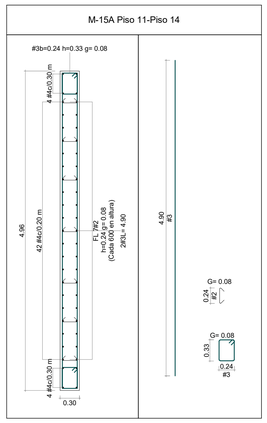

M-15A Cimentación 2-Piso 1

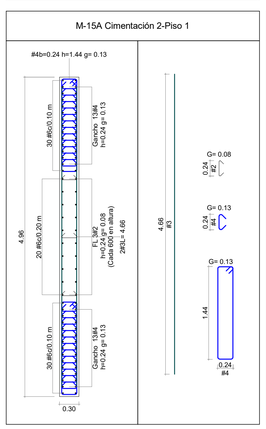

M-15A Piso 8-Piso 10

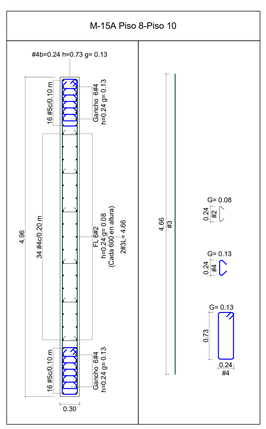

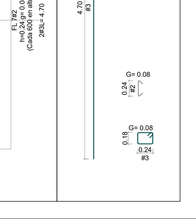

DETALLE SOBRE ANCHO EN MURO M-15A
Escala 1 : 25

M-15A Piso 22-Cubierta

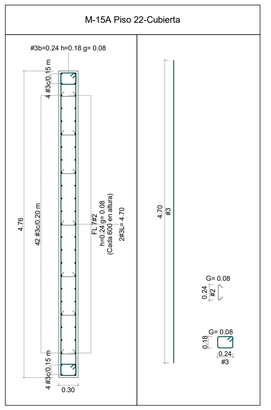

VERSIÓN : 3

PLANO N° 11.11

Aycardi Estructural

GERENTE DE PROYECTO
ROBERTO AYCARDI F.
MAT. 2520257258 CND

INGENIERO
CARLOS ANDRÉS WILCHES C.

MODELADOR
DANIEL CASTELLANOS

MODIFICACIONES	FECHA
Emisión Inicial	28-02-2025
Ajuste longitudes refuerzos y se incluye detalle sobre ancho muro	03-10-2025
Ajuste refuerzo muros	26-02-2026

MARVAL

LA SCALA

LA SCALA_EST_TOR-1

TORRE 1

CALLE 170 CON AV. BOYACA

DESPIECE DE MUROS

LA SCALA_EST_TOR-1 _11.11_MUR-D12

REVISOR ESTRUCTURAL
RAMÓN ÁNDRES ALVAREZ MANTILLA
MAT. 25202-346546 CND.

PLANO N° 11.11

VERSIÓN : 3