
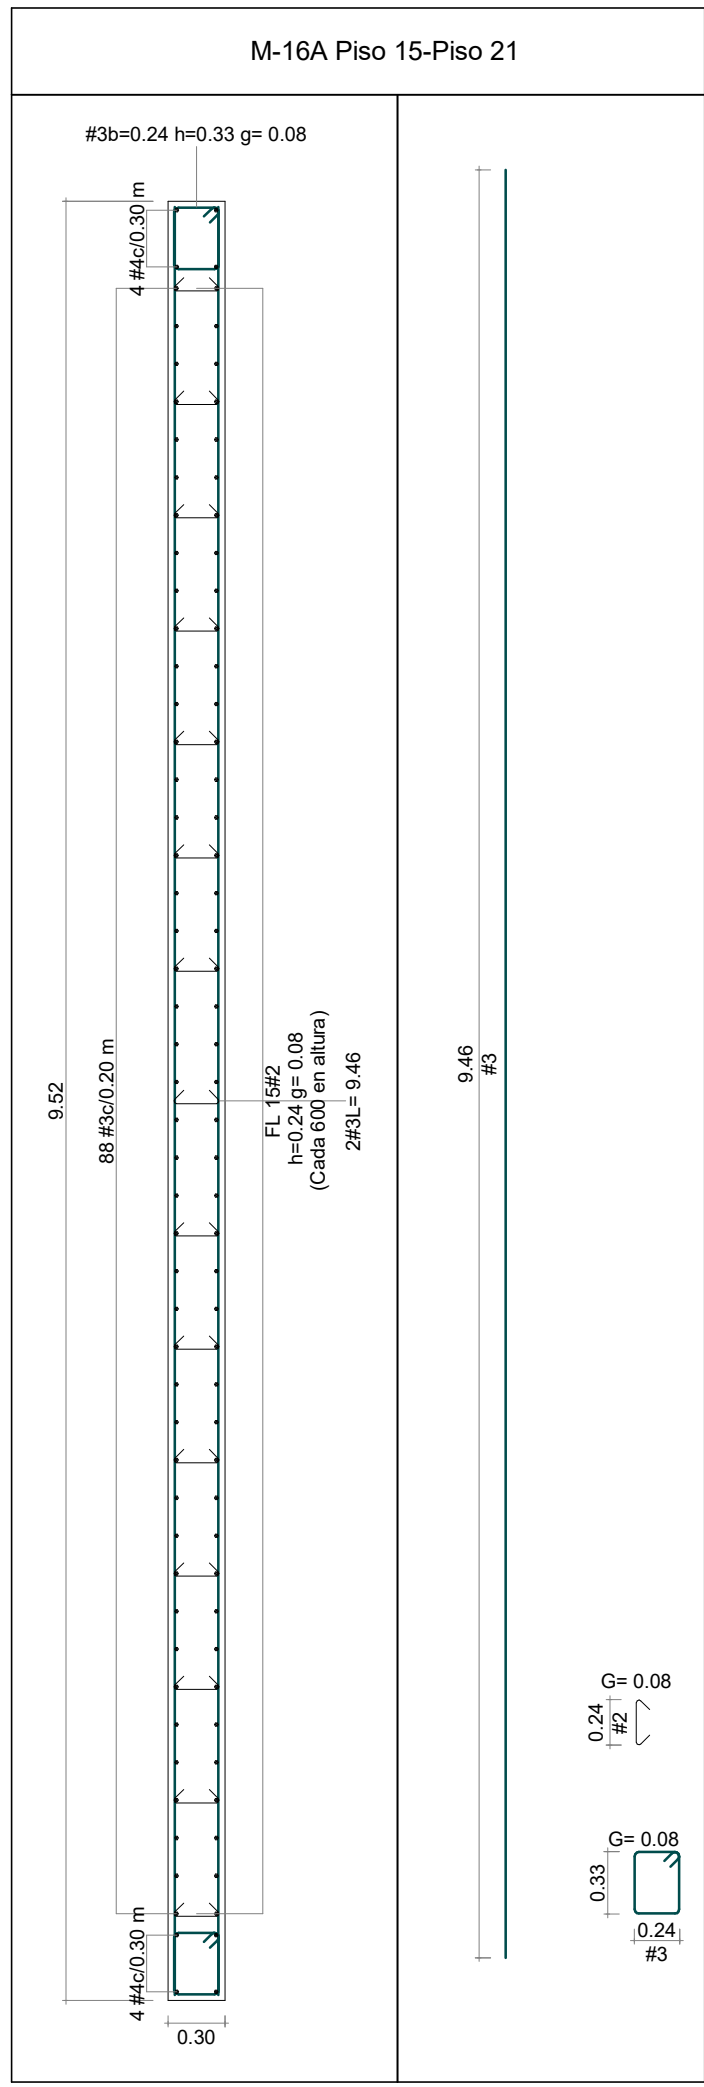
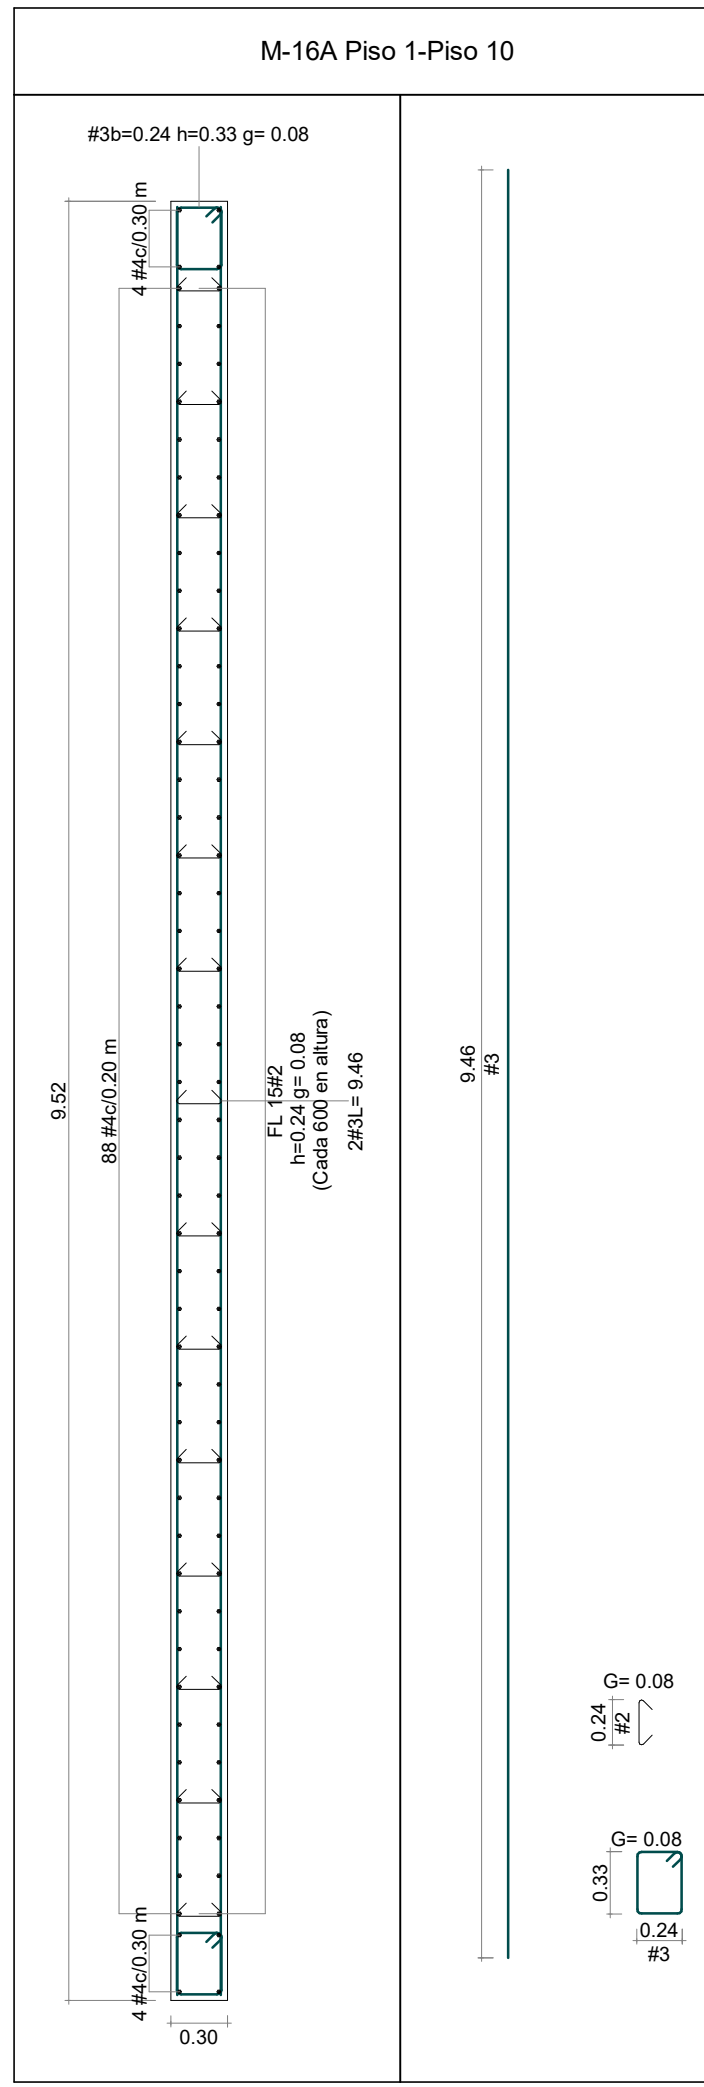
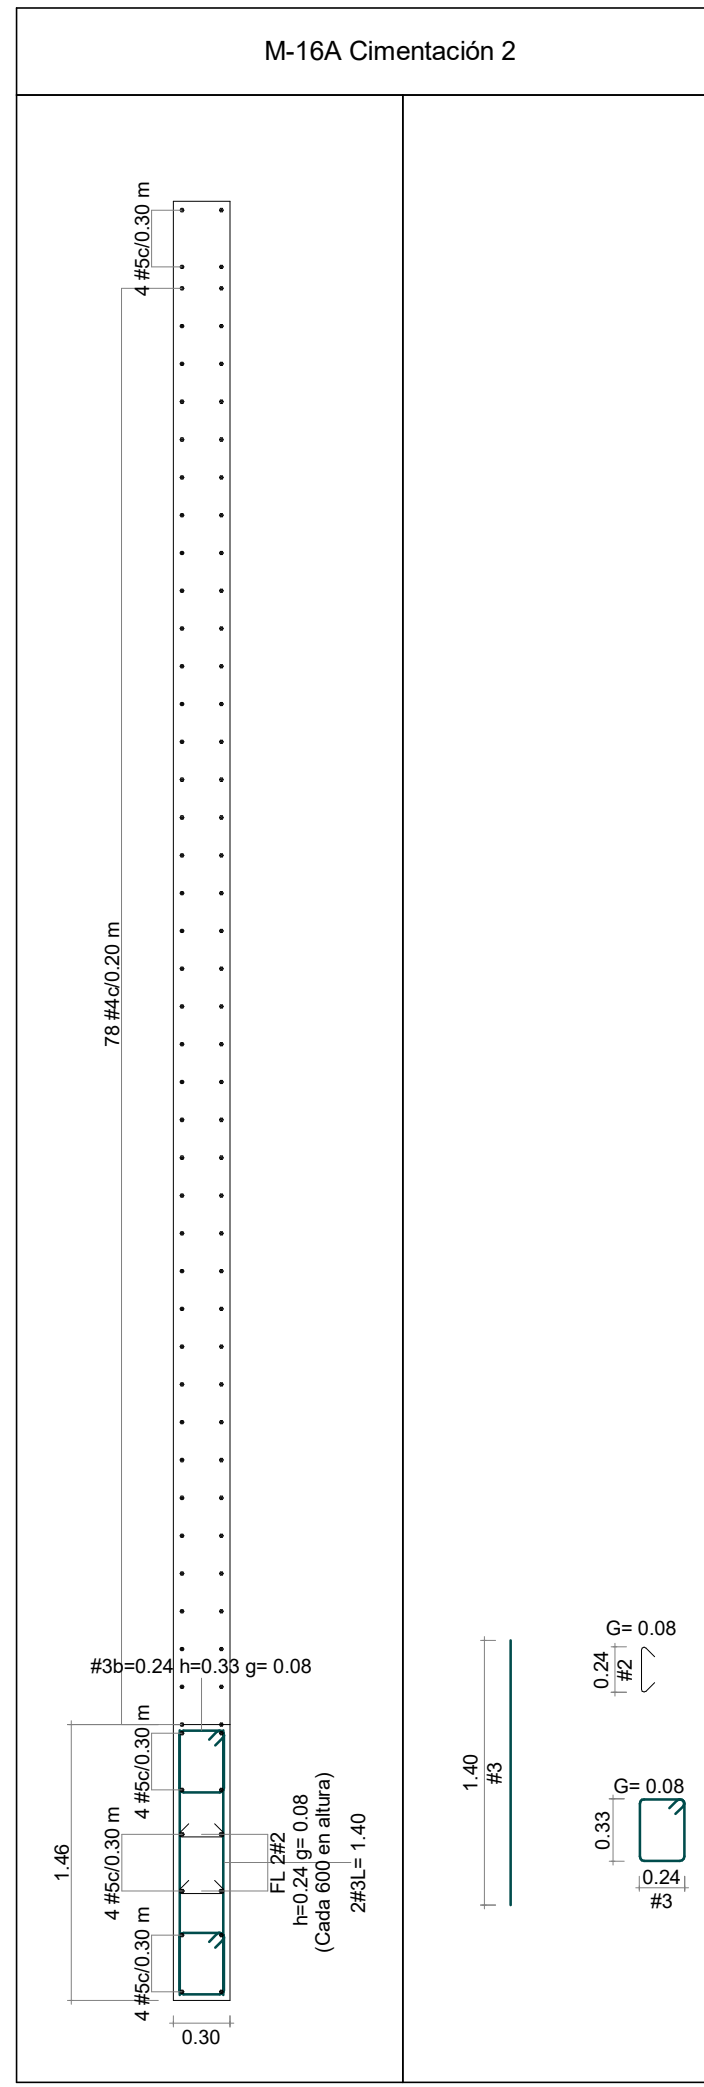
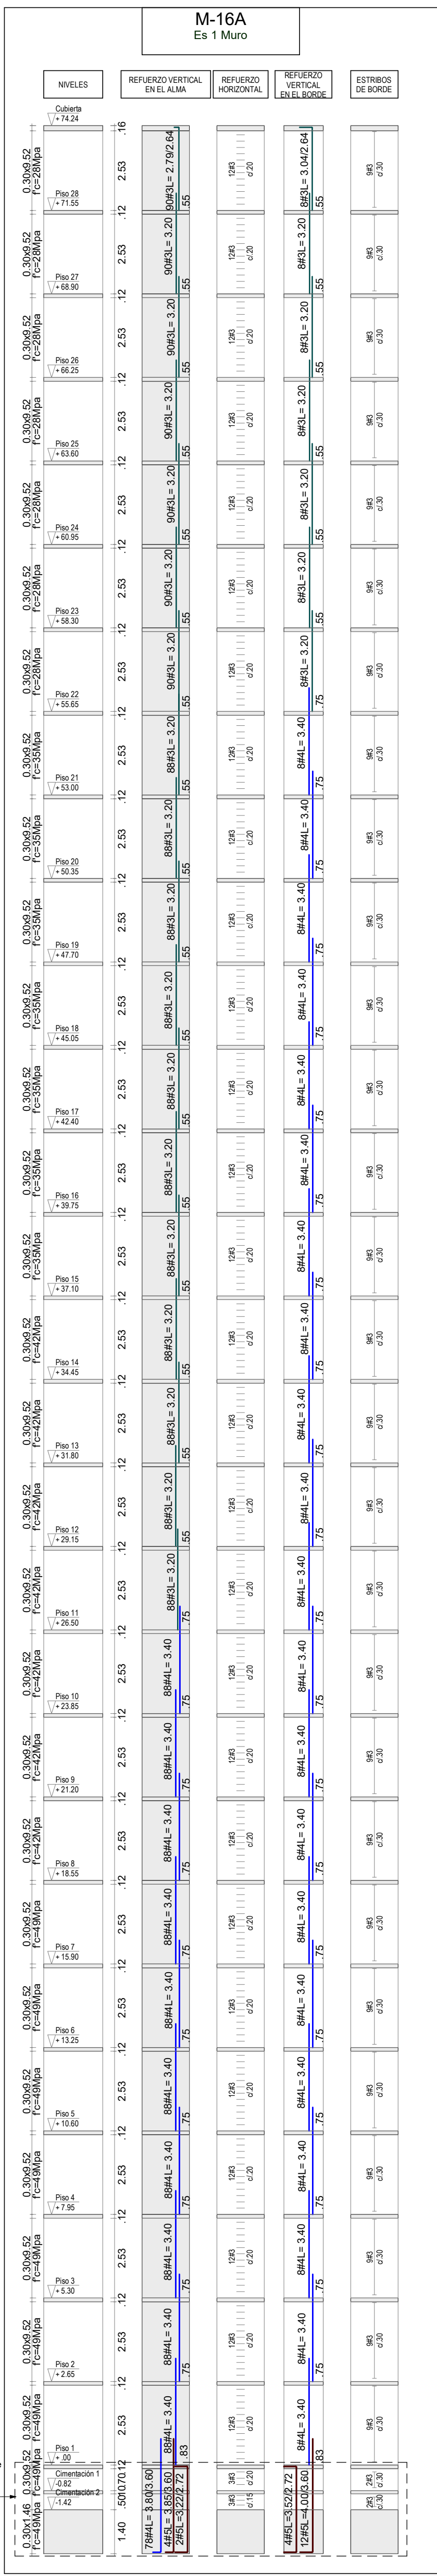
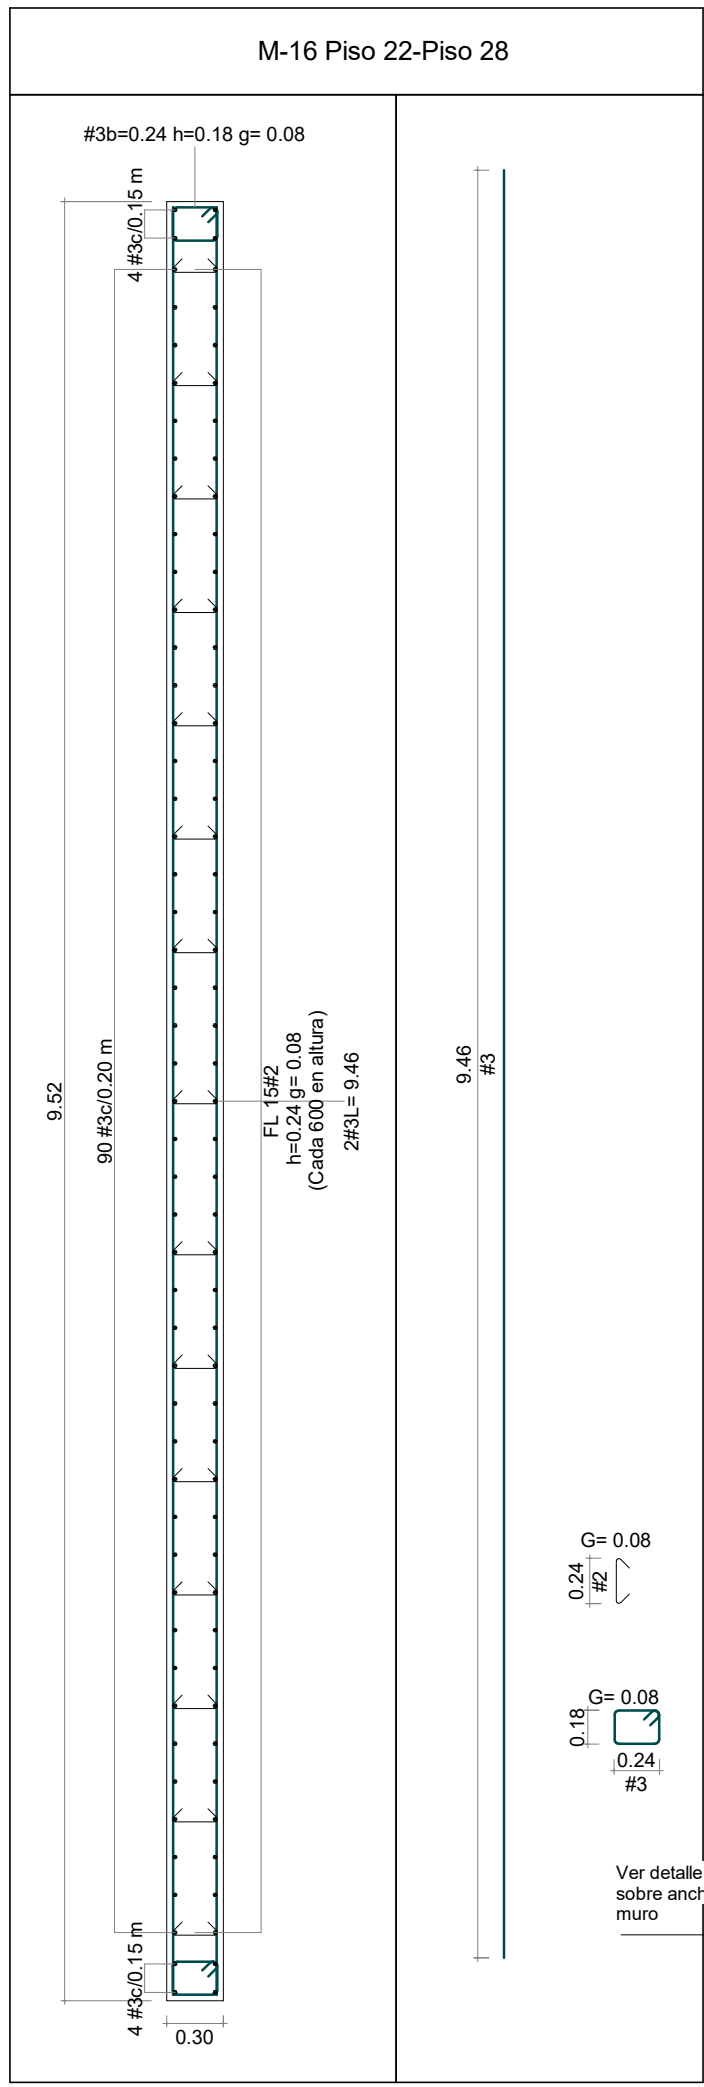
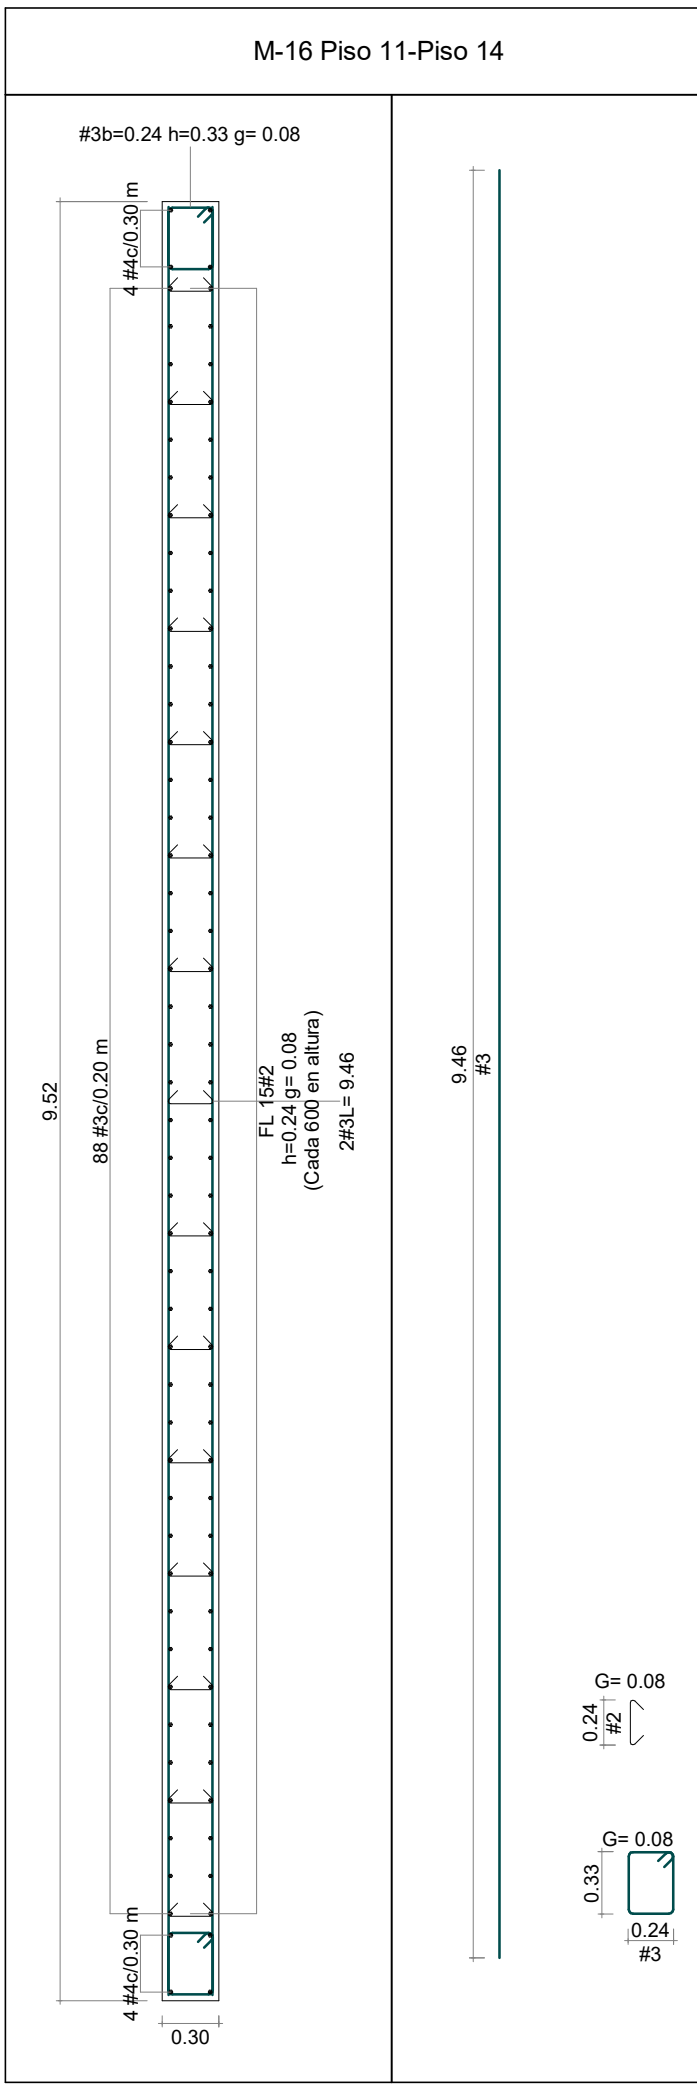
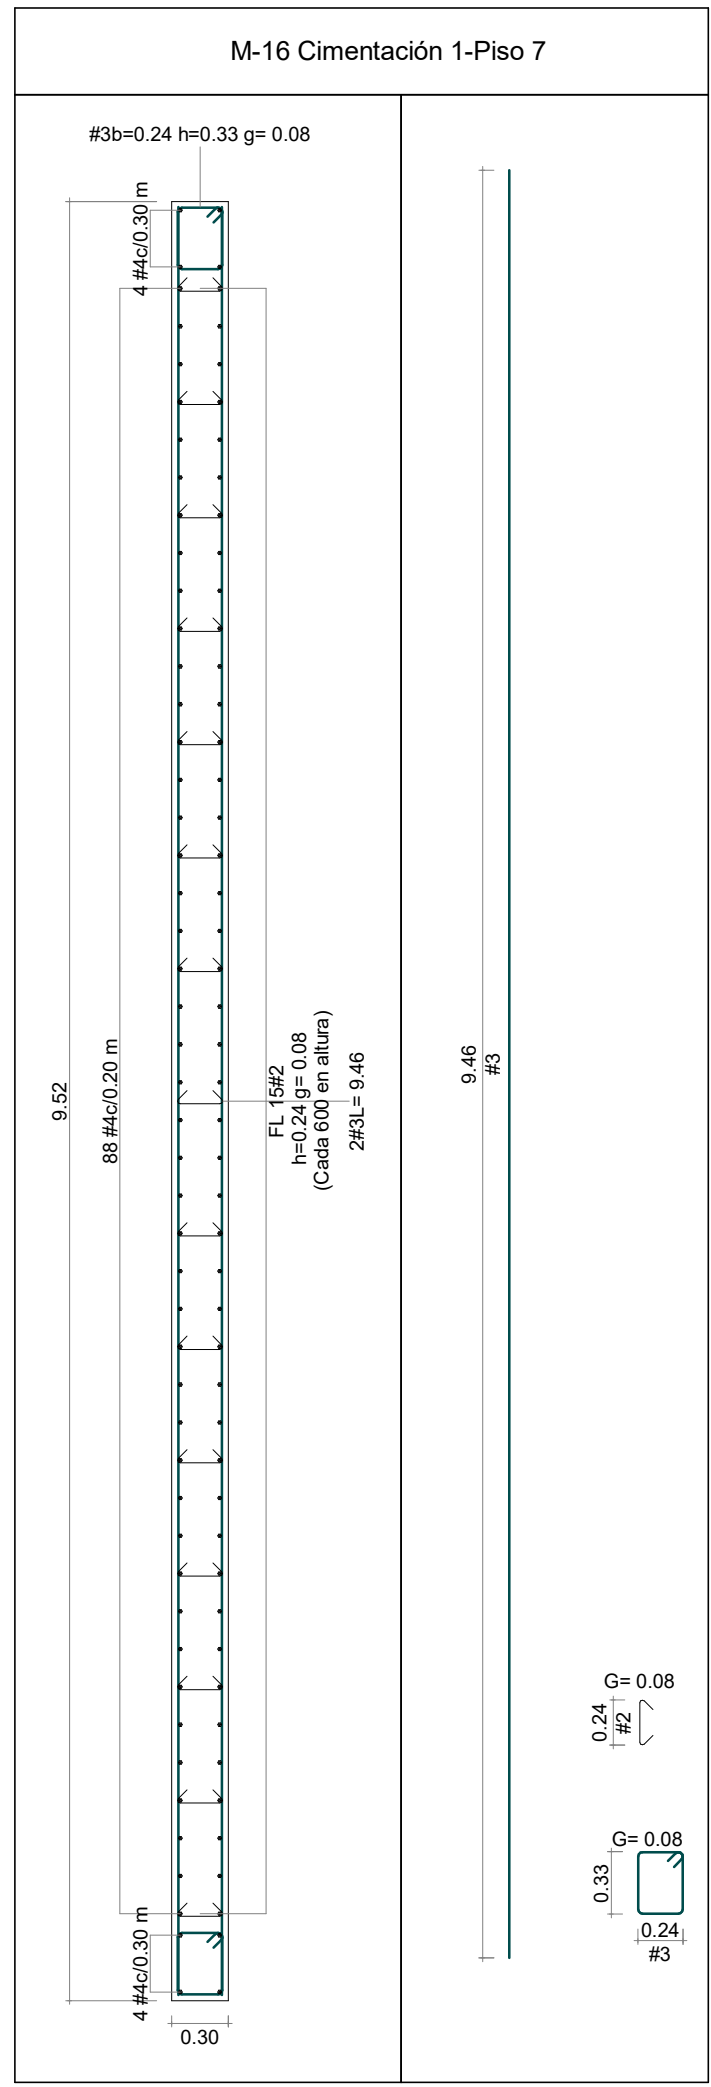


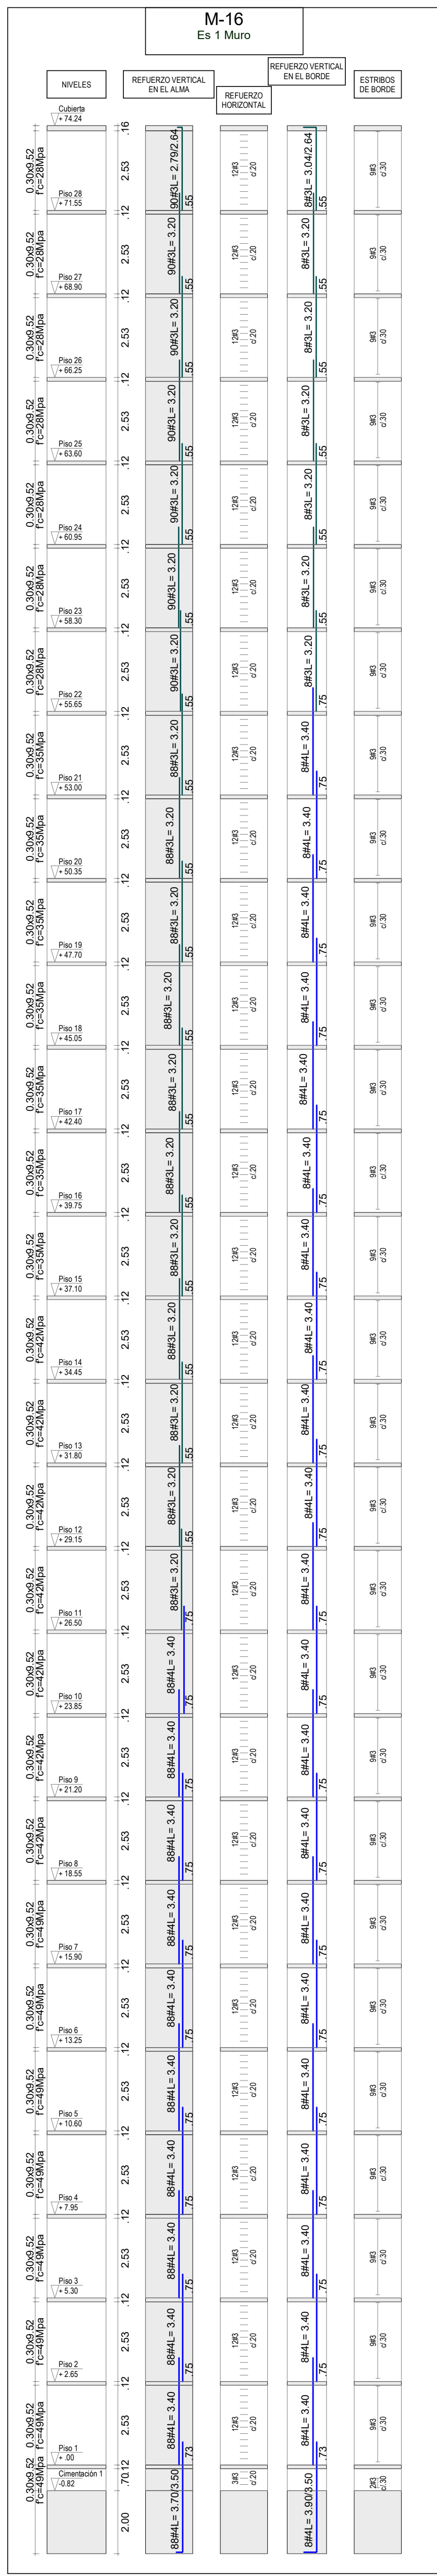

ESCALA 1:125