

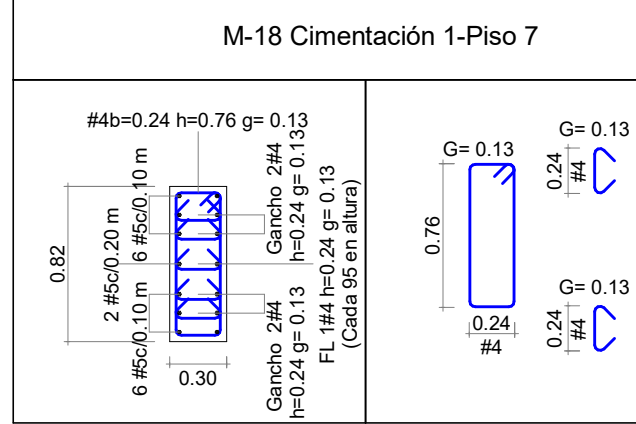
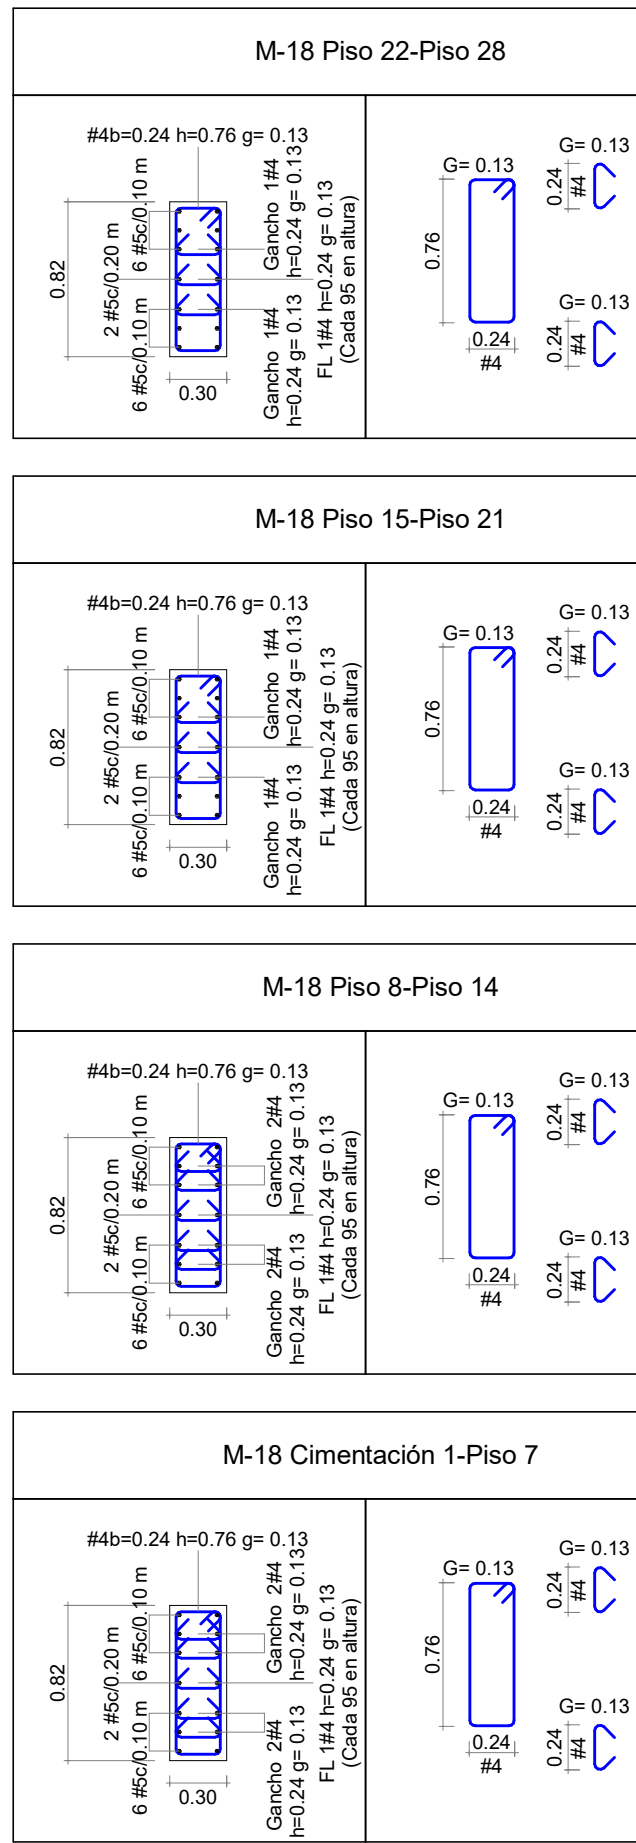
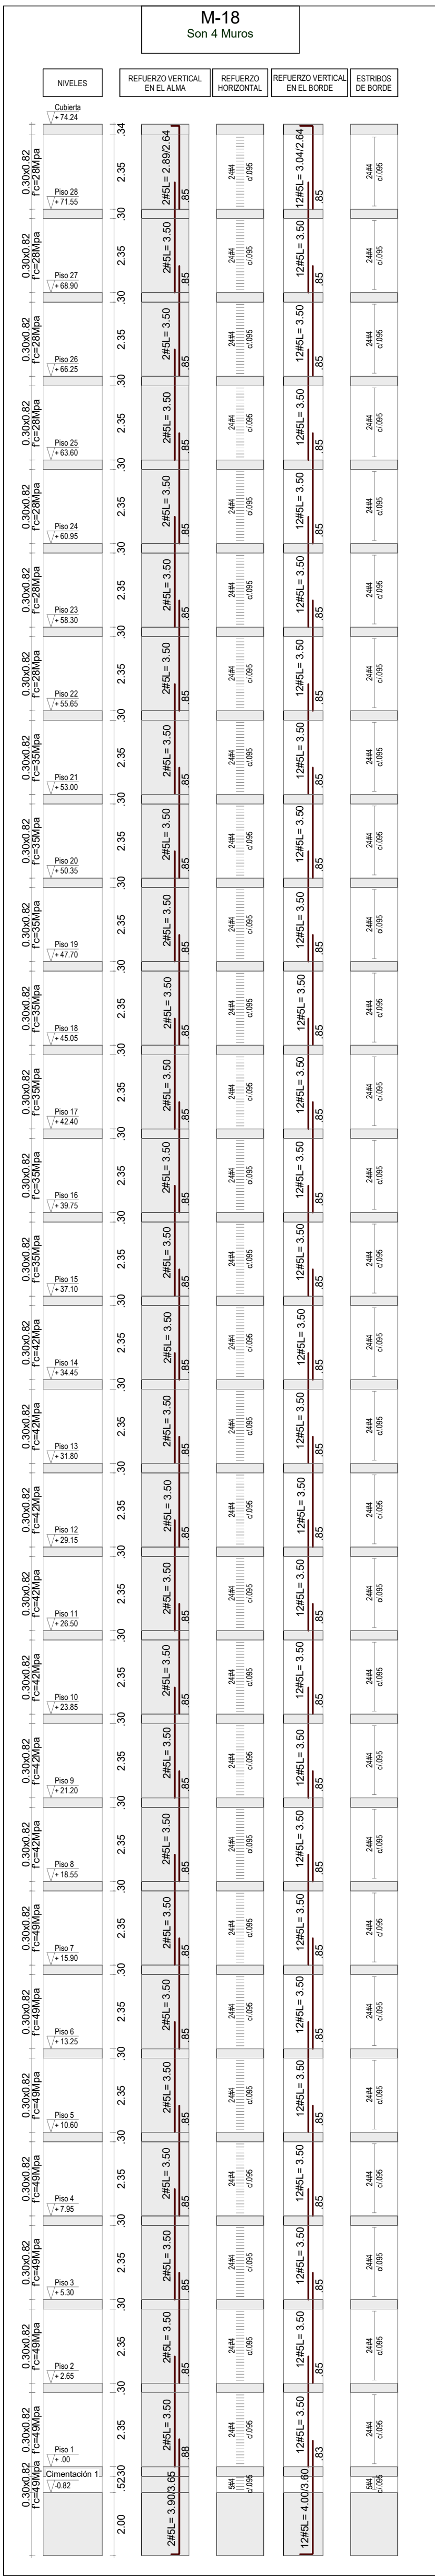
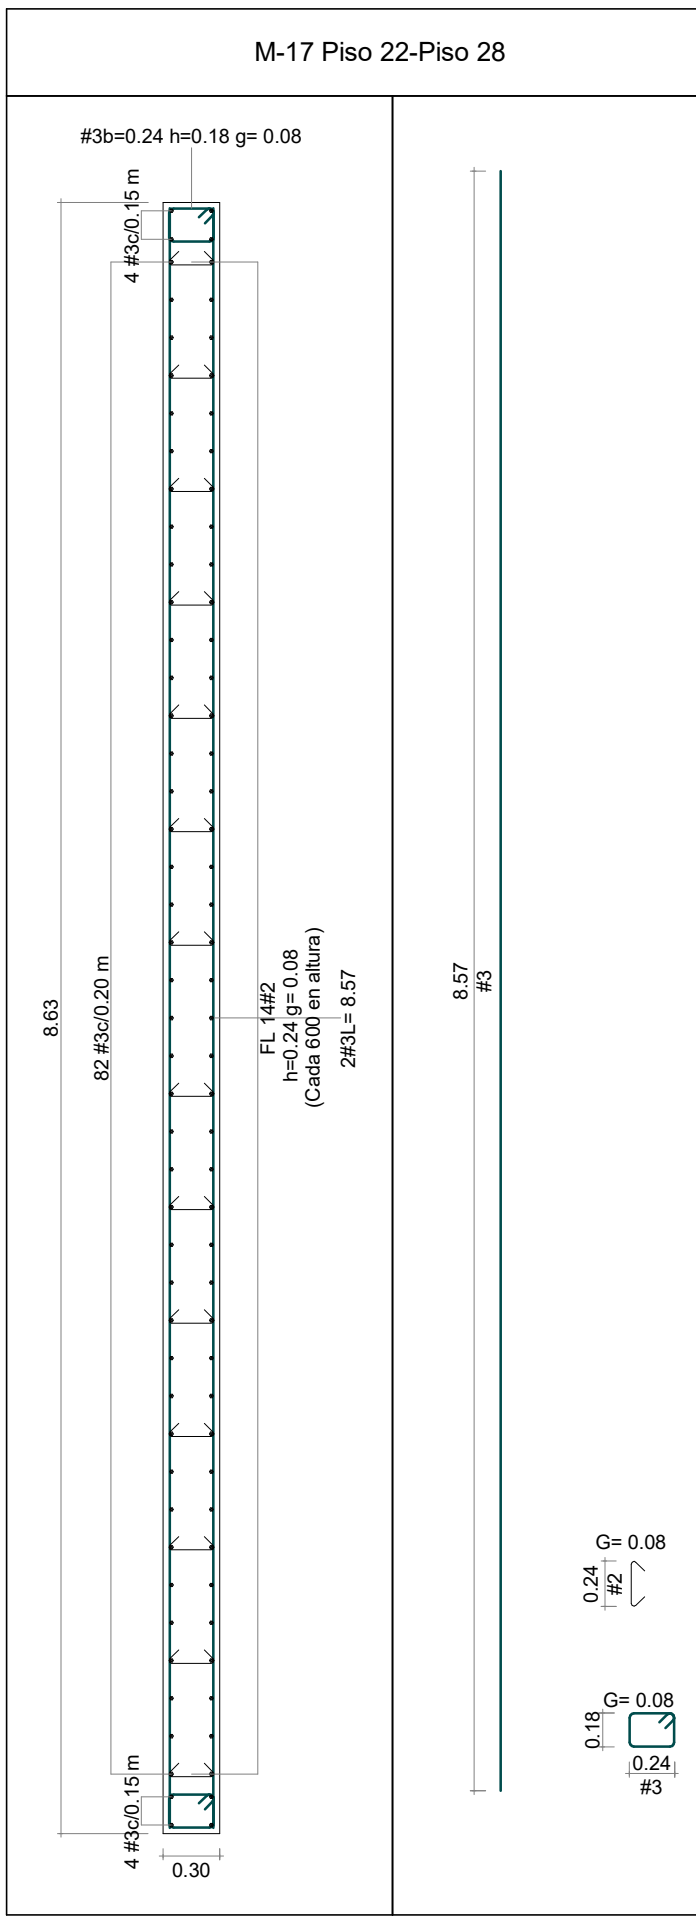


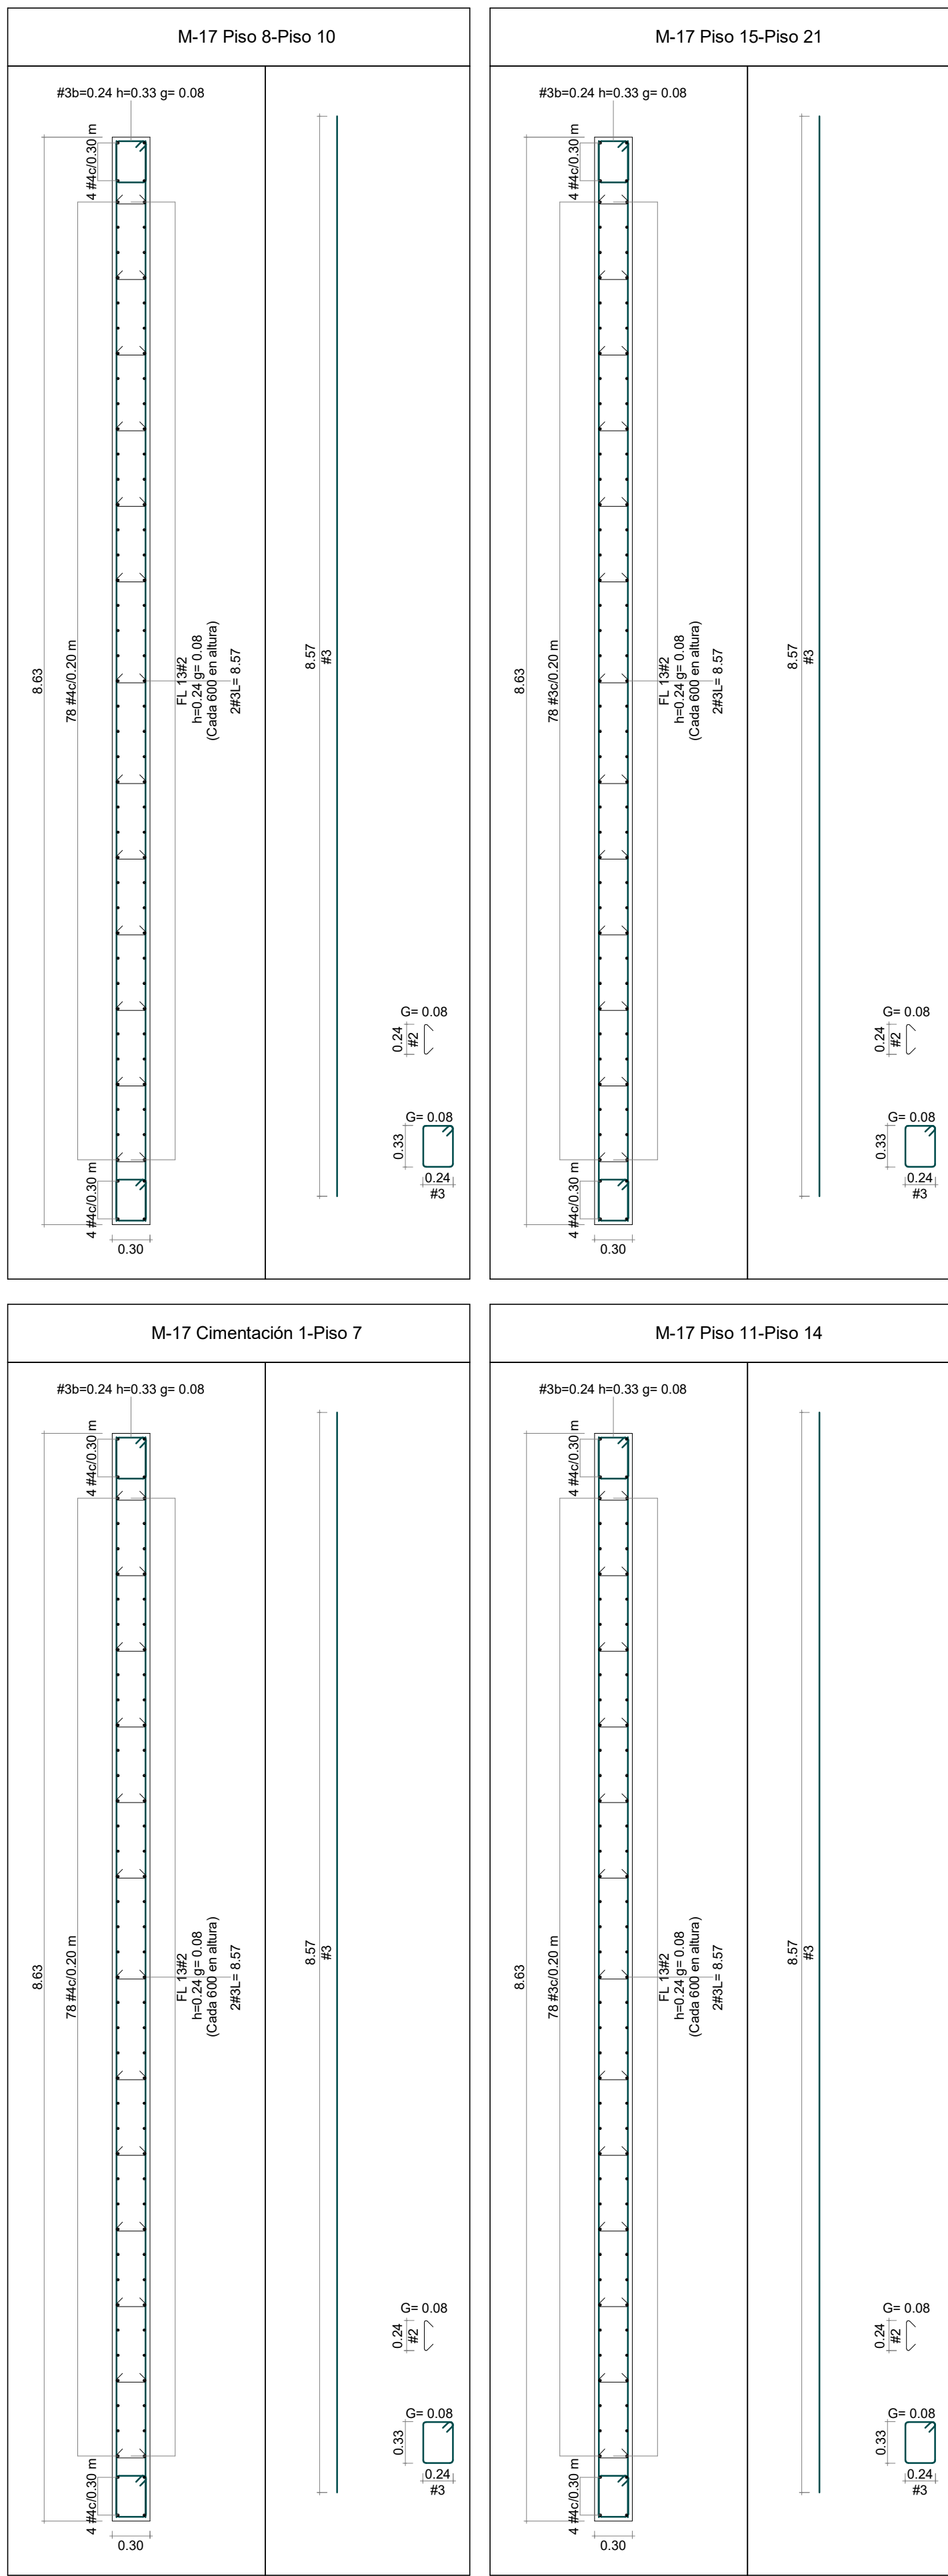

ESCALA 1:125

MODIFICACIONES	FECHA
Emisión Inicial	28-02-2025
Ajuste longitudes refuerzos	03-10-2025
Ajuste refuerzo muros	26-02-2026

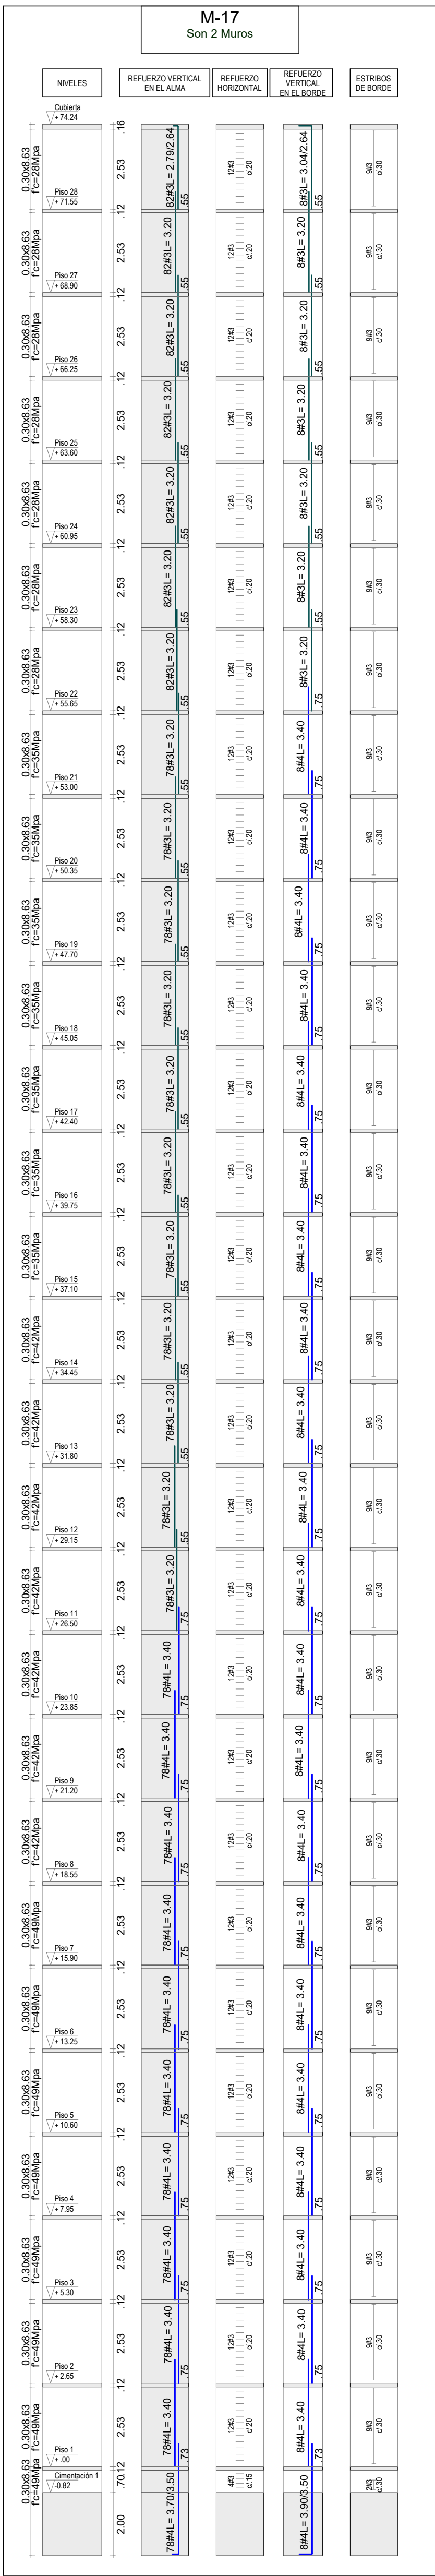