
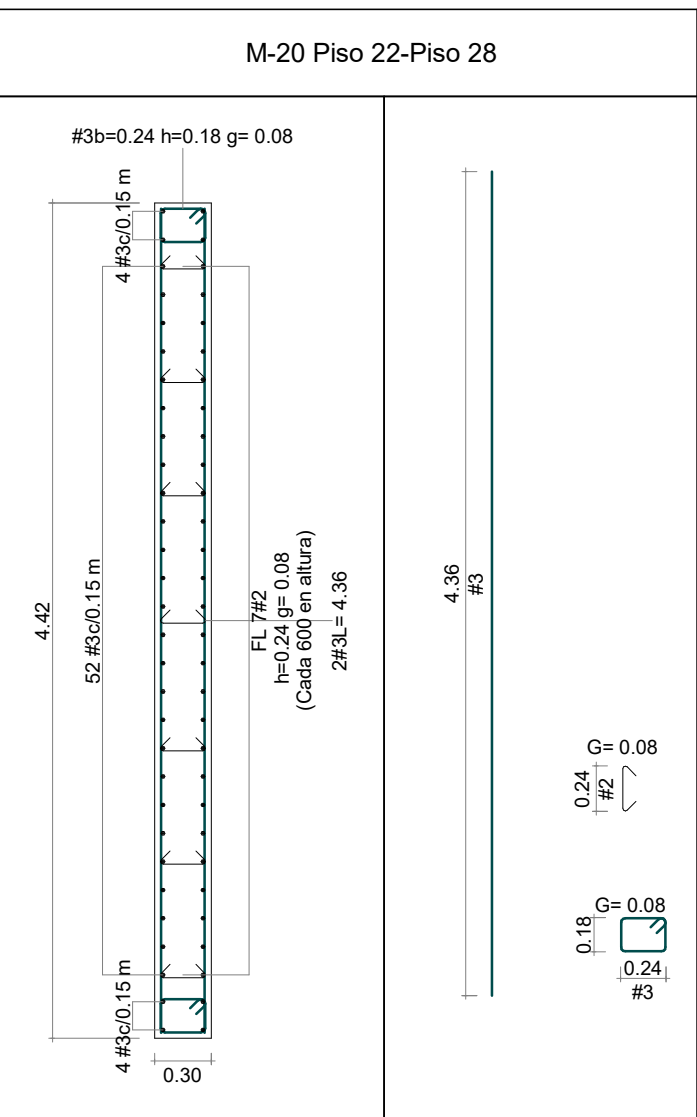
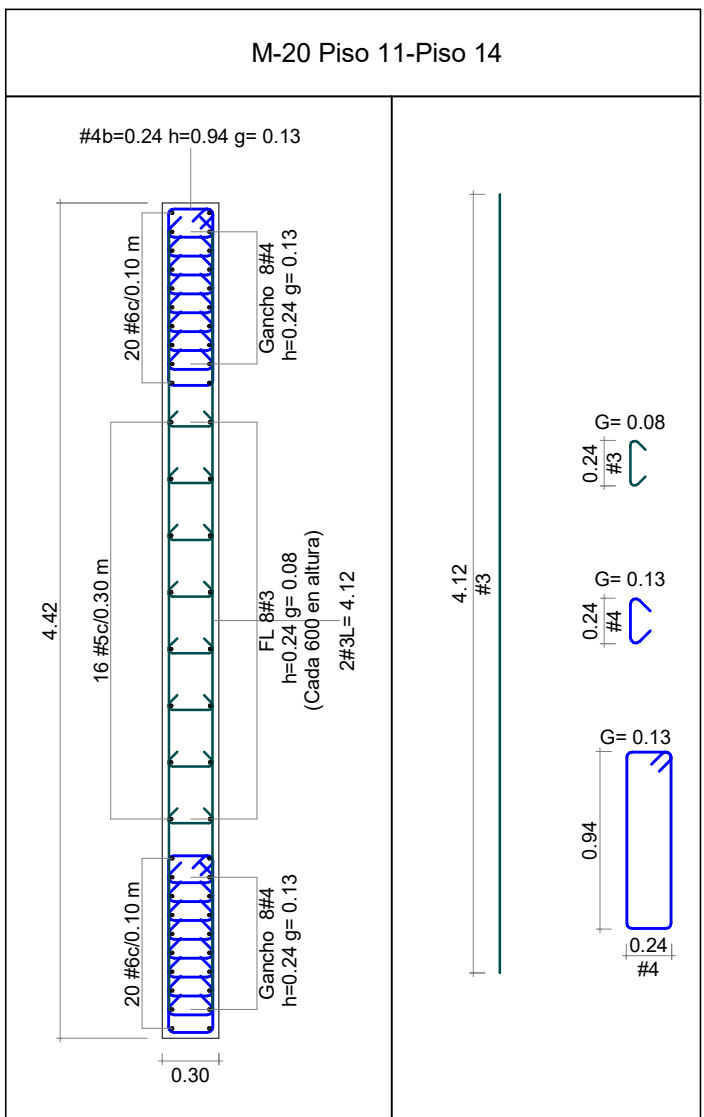
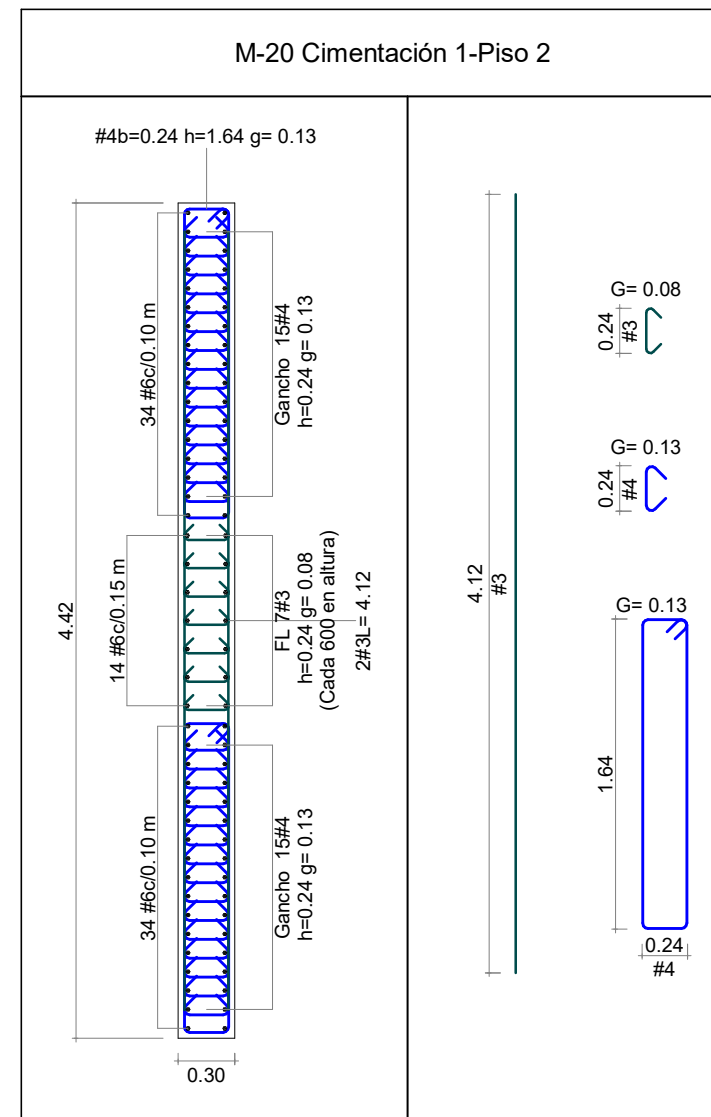
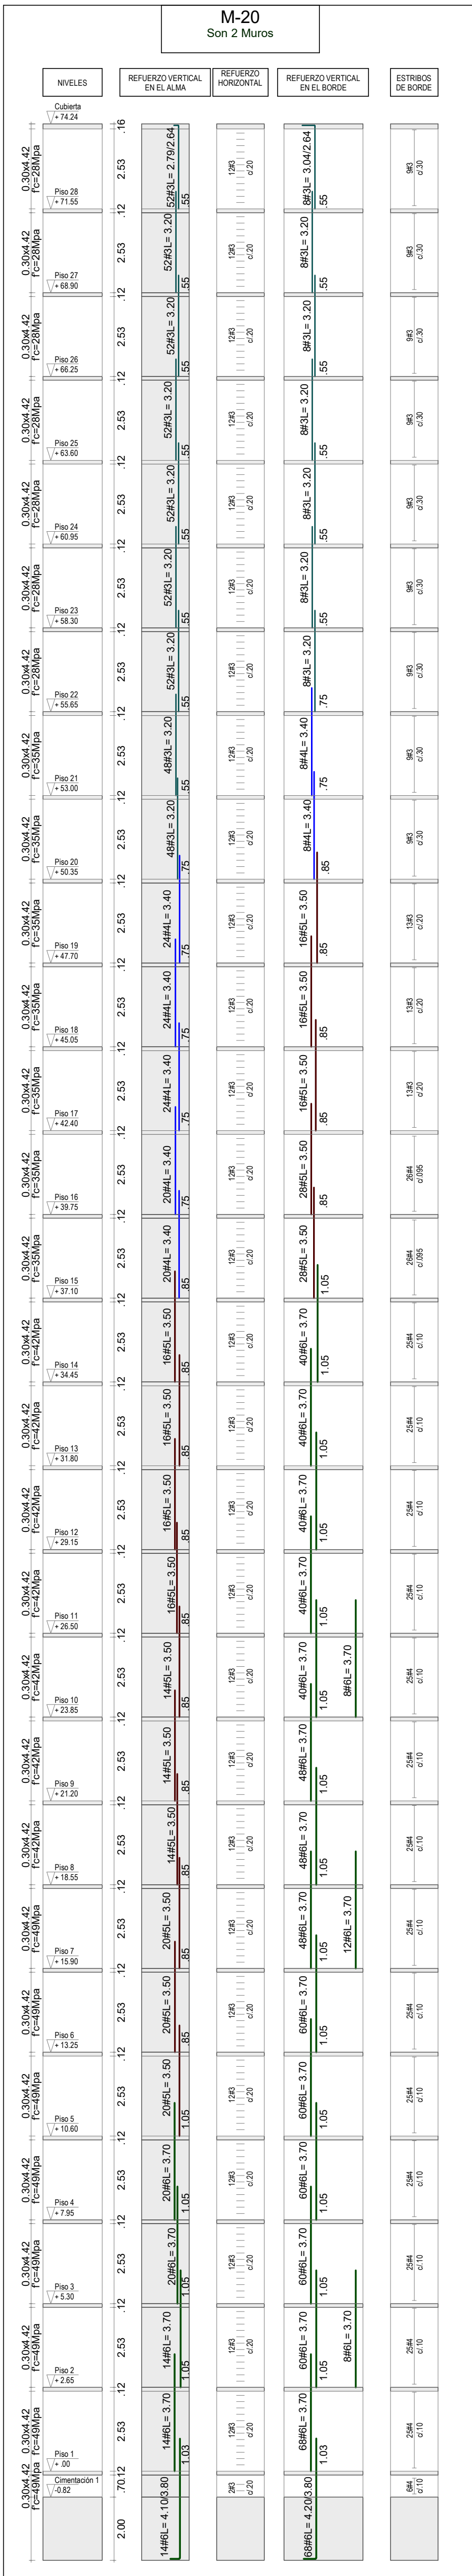
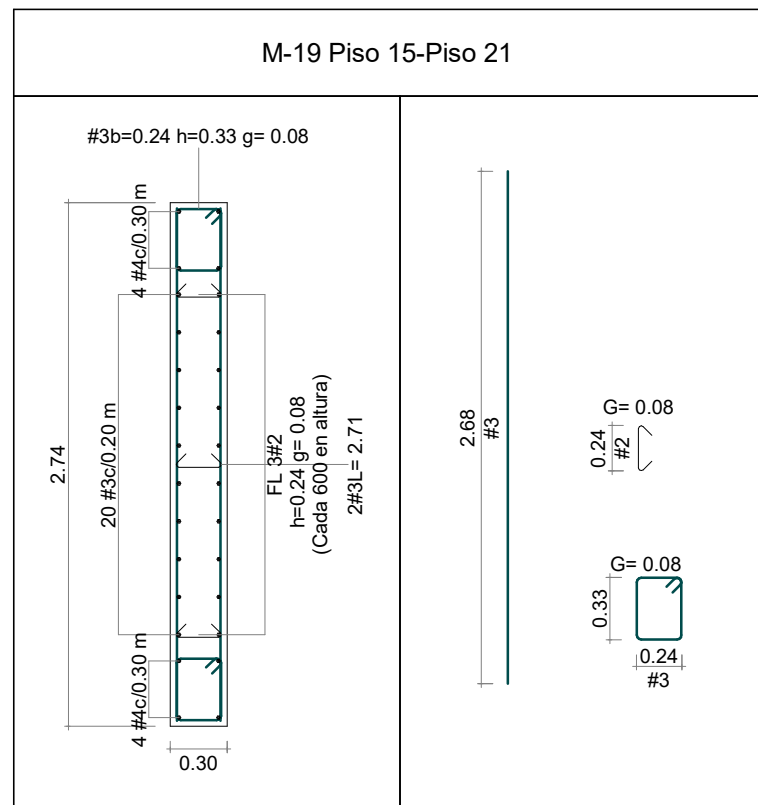
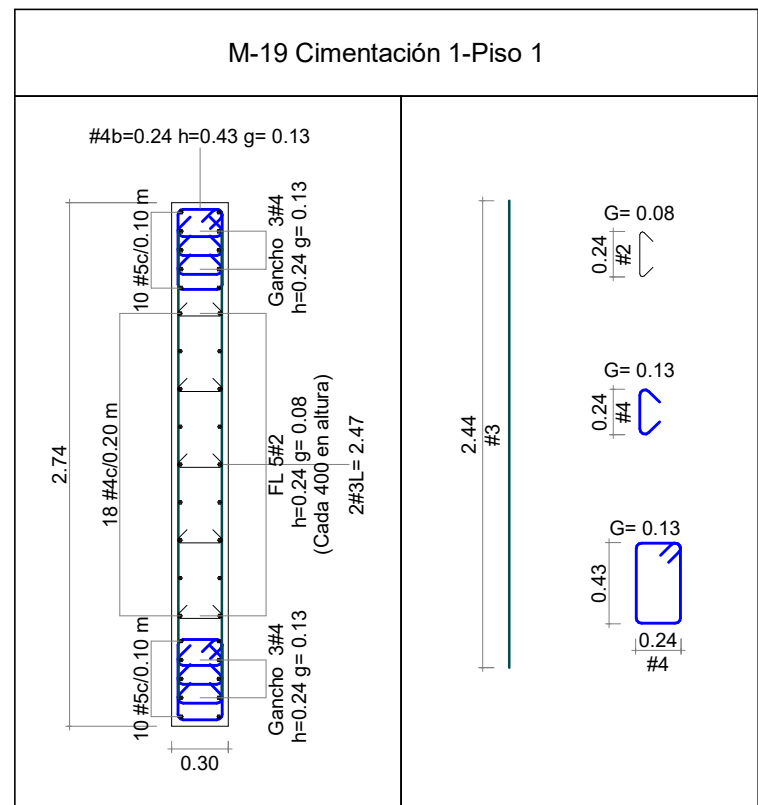


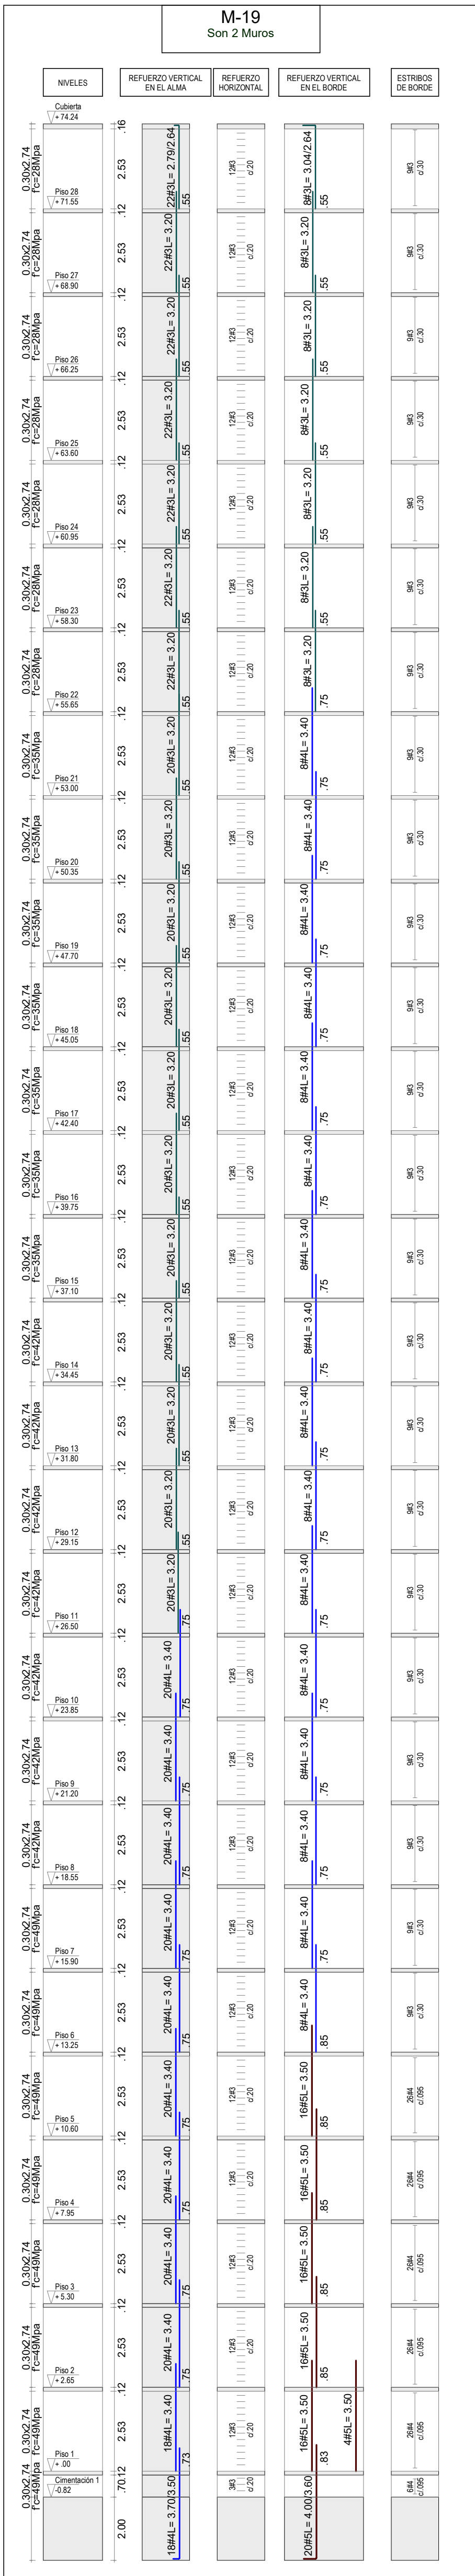

11.14

INGENIERO
CARLOS ANDRÉS WILCHES C.

MODELADOR
DANIEL CASTELLANOS

MODIFICACIONES	FECHA
Emisión Inicial	28-02-2025
Ajuste longitudes refuerzos	03-10-2025
Se actualiza longitud de muro M-19	04-11-2025
Ajuste refuerzo muros	26-02-2026



LA SCALA_EST_TOR-1

TORRE 1

CALLE 170 CON AV. BOYACA

DESPIECE DE MUROS

LA SCALA_EST_TOR-1_11.14_MUR-D15

REVISOR ESTRUCTURAL
RAMÓN ÁNDRES ALVAREZ MANTILLA
MAT. 25202-346546 CND.

PLANO Nº

VERSIÓN :

11.14

4