



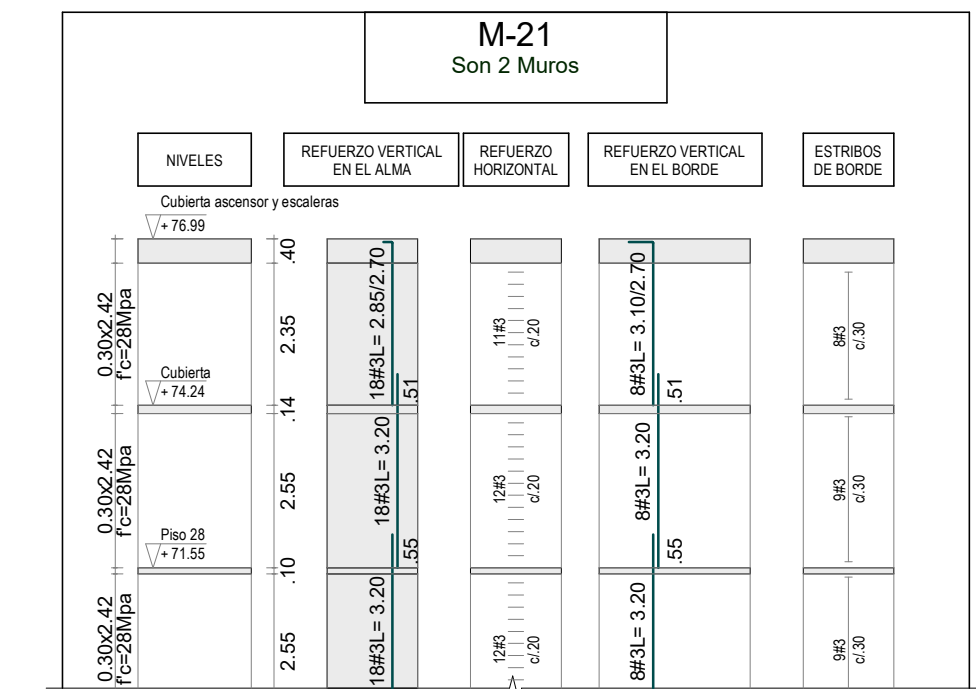


Ver detalle de
sobre ancho muro

Ver detalle doblez









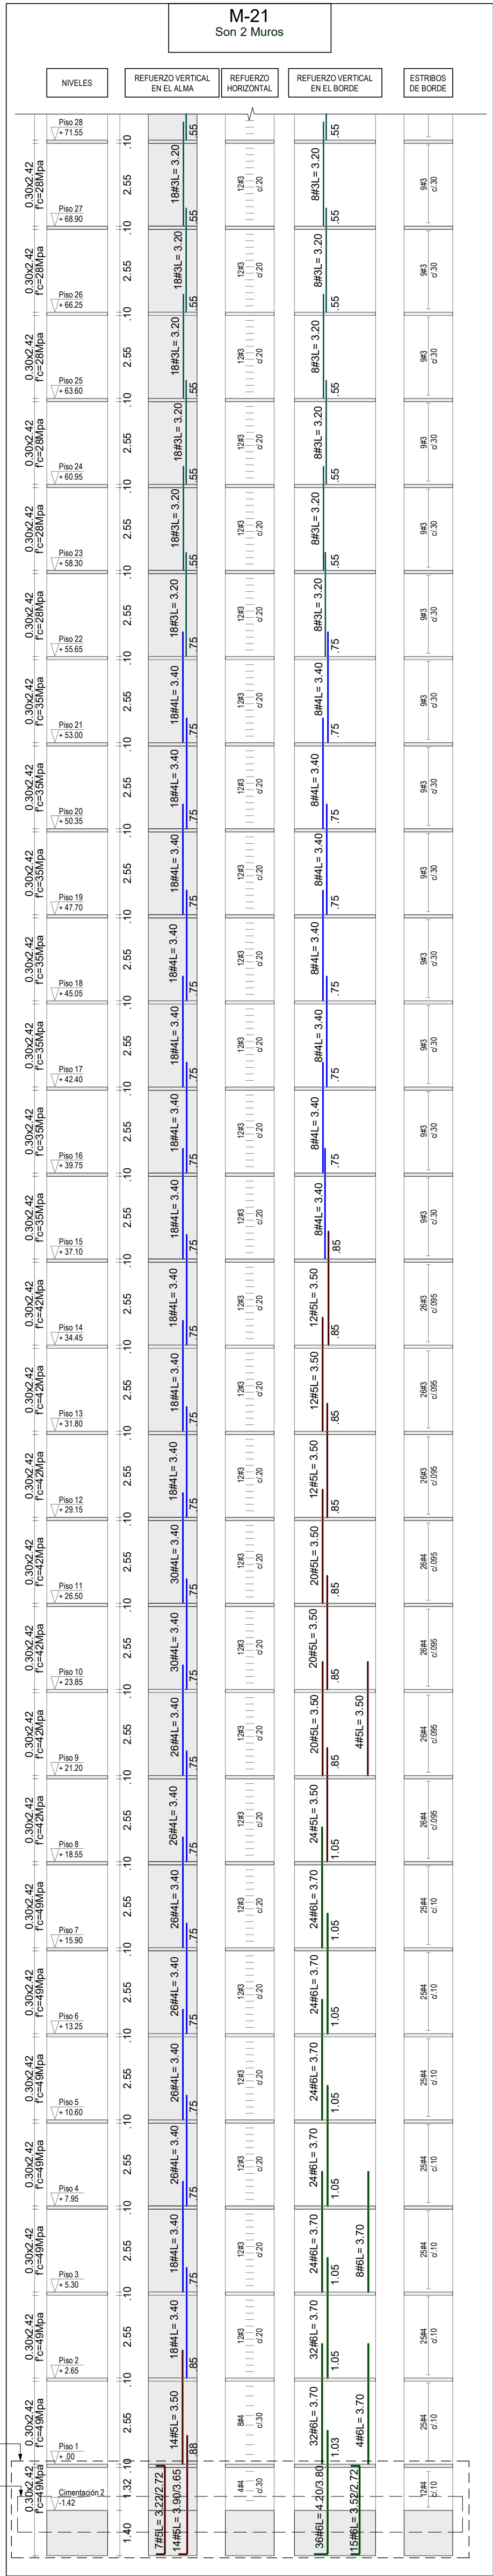


DETALLE SOBRE ANCHO EN MURO M-21
Escala 1 : 25

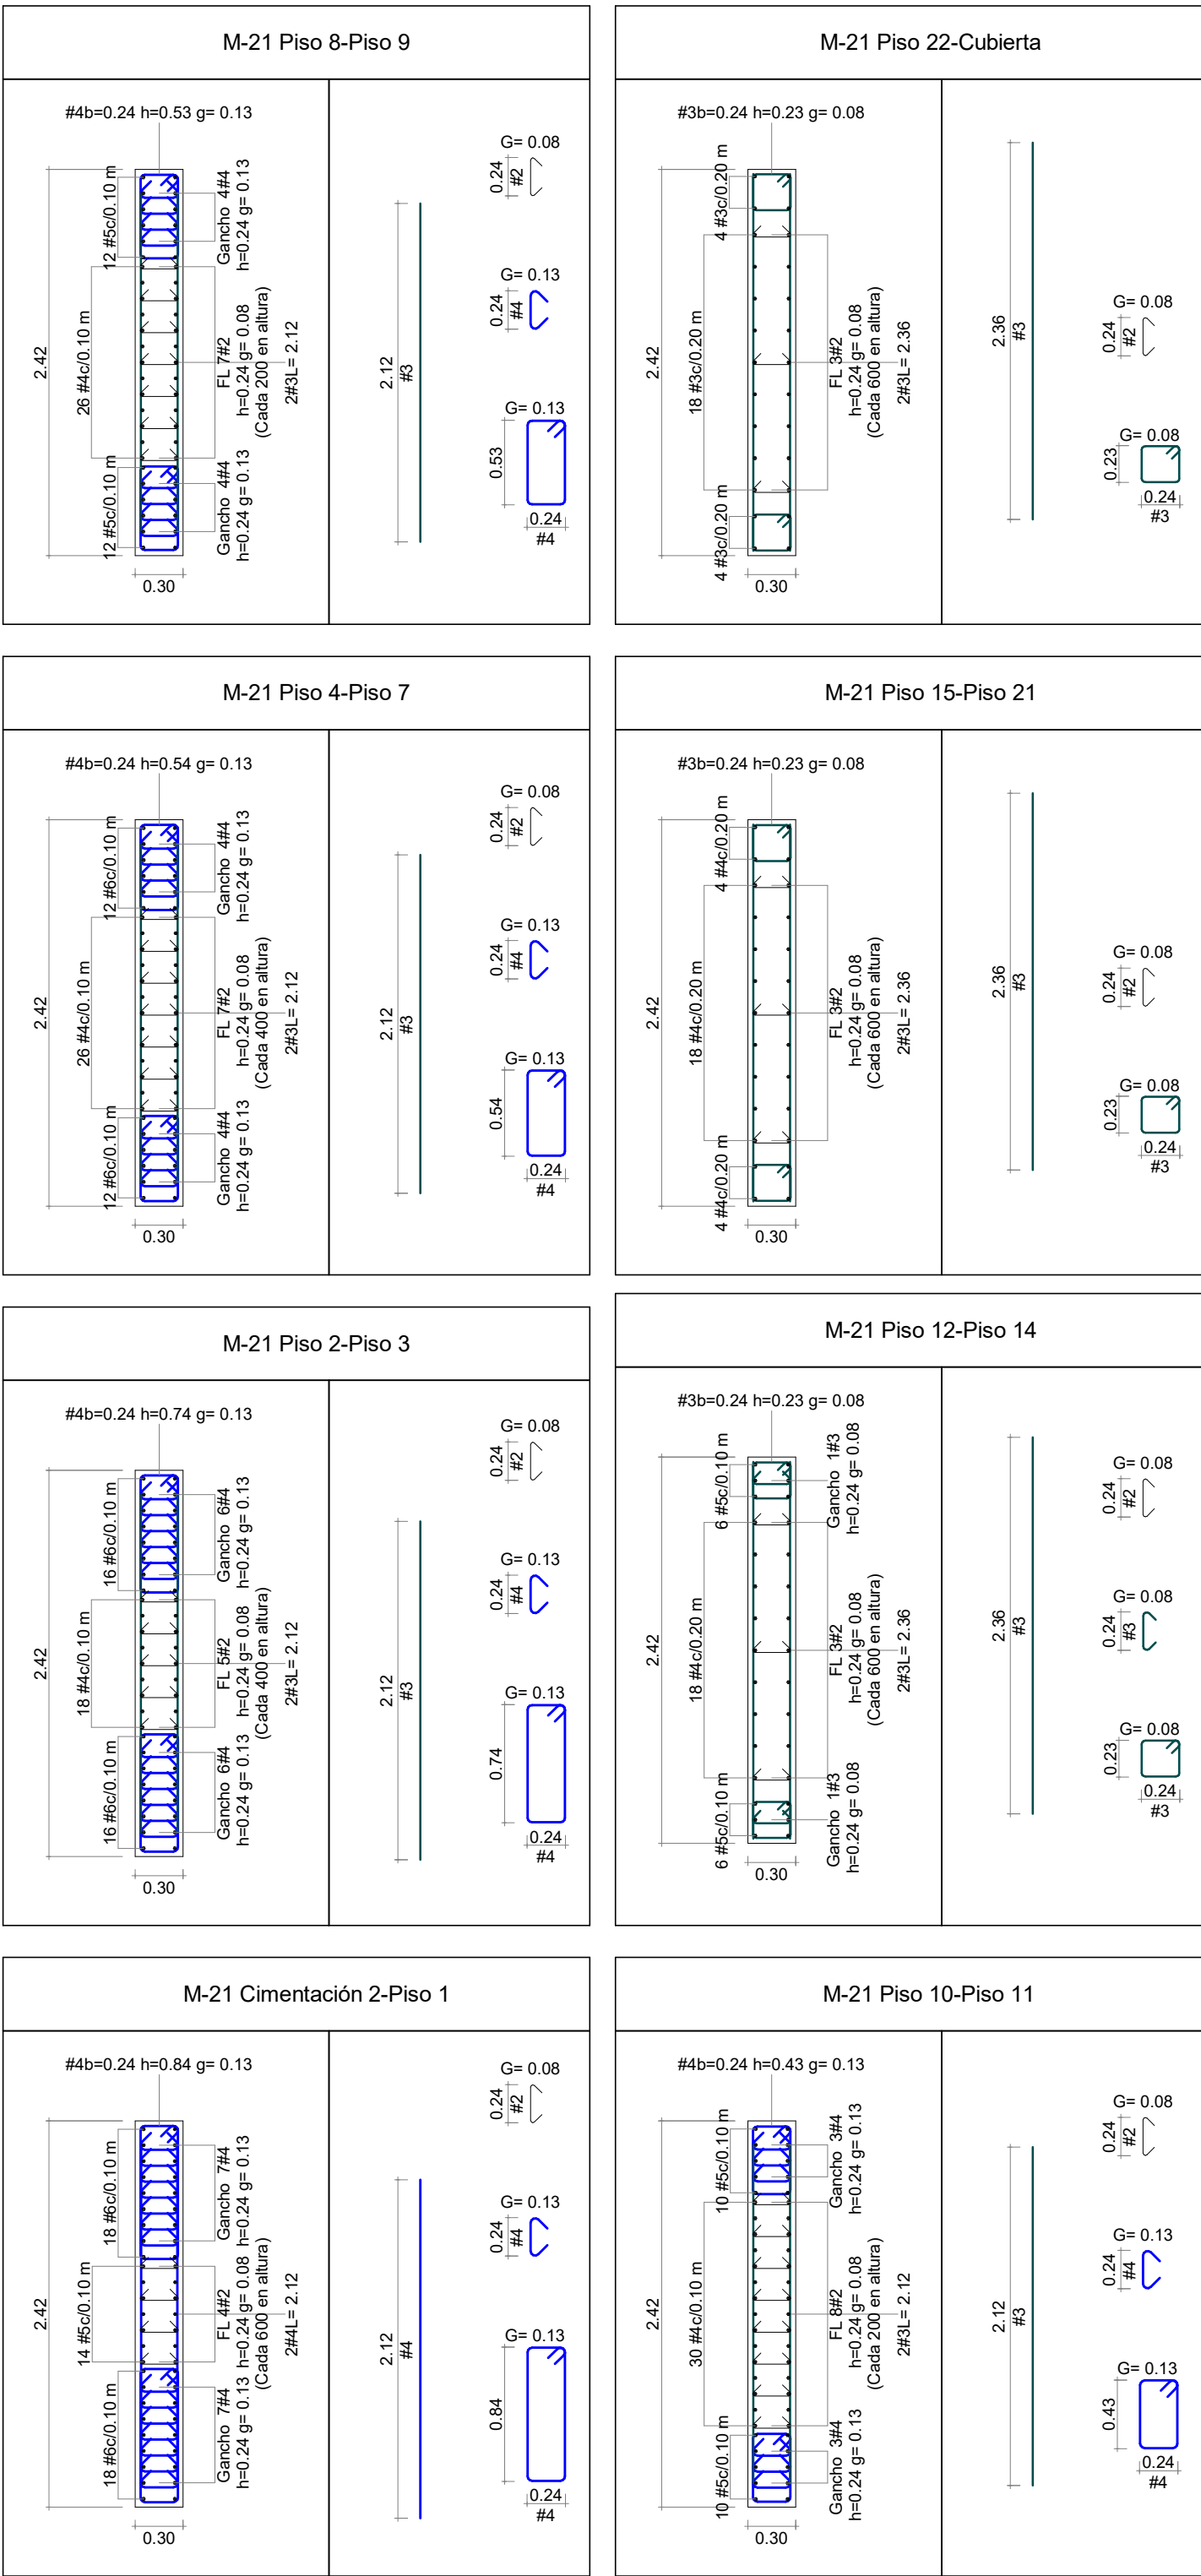

Ver detalle 1 en el
PL.N° 11.22

Ver detalle 2 en el
PL.N° 11.22

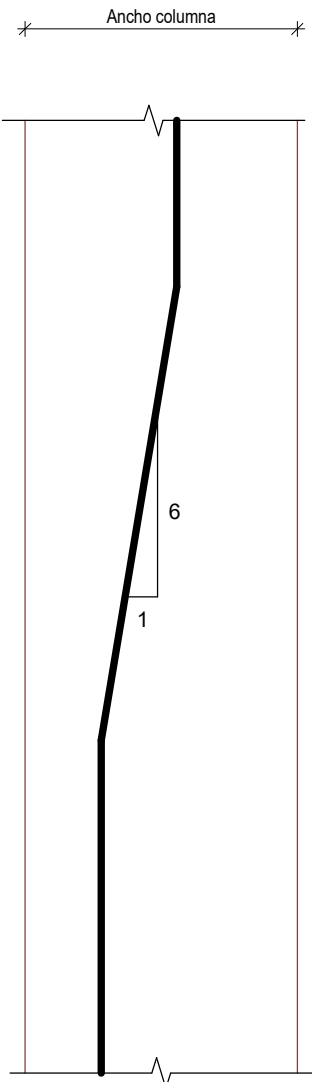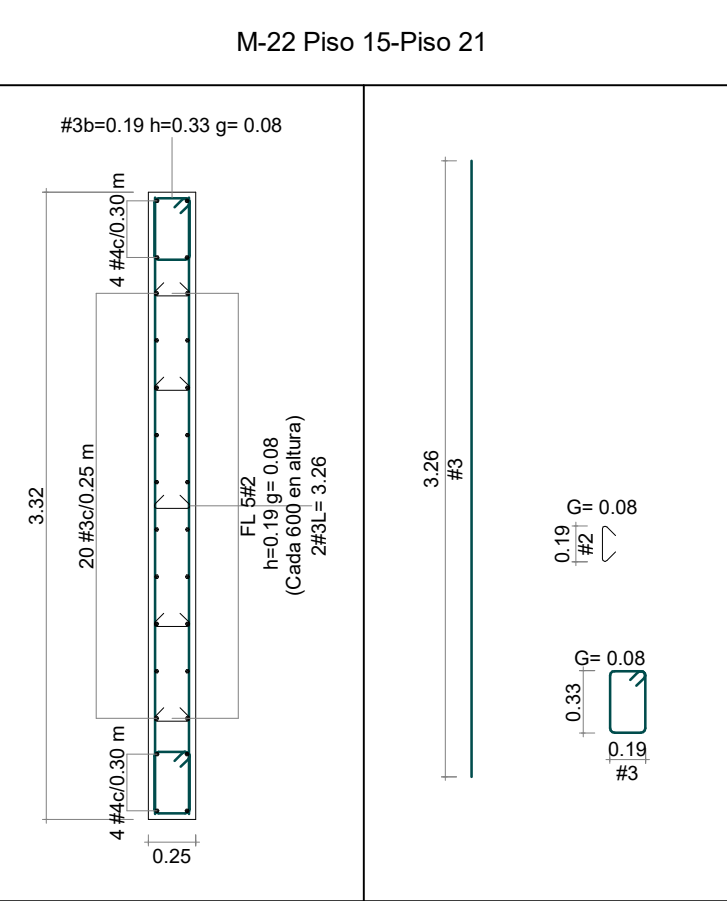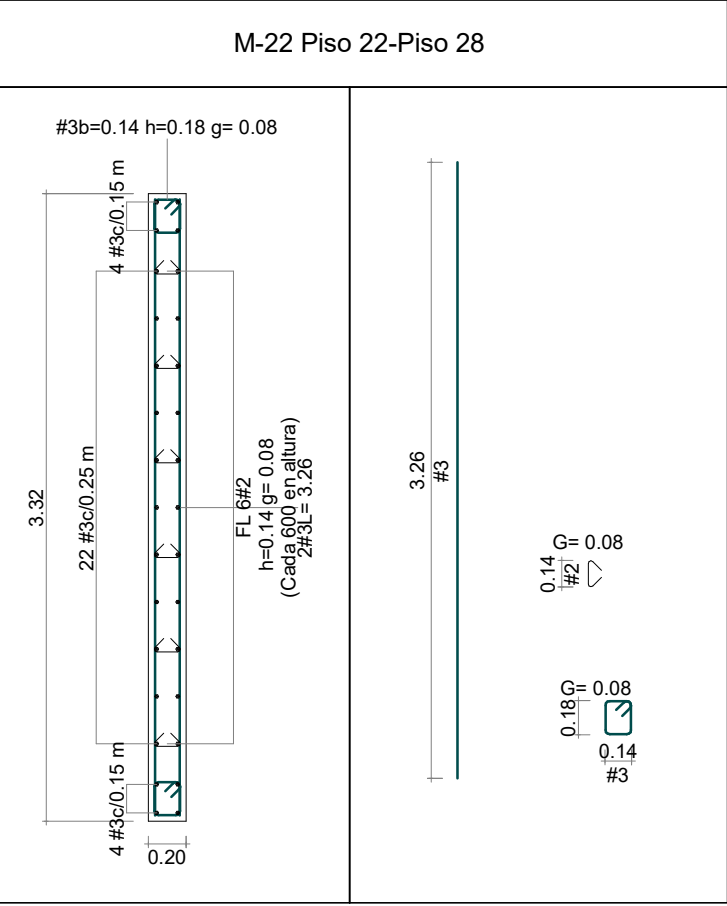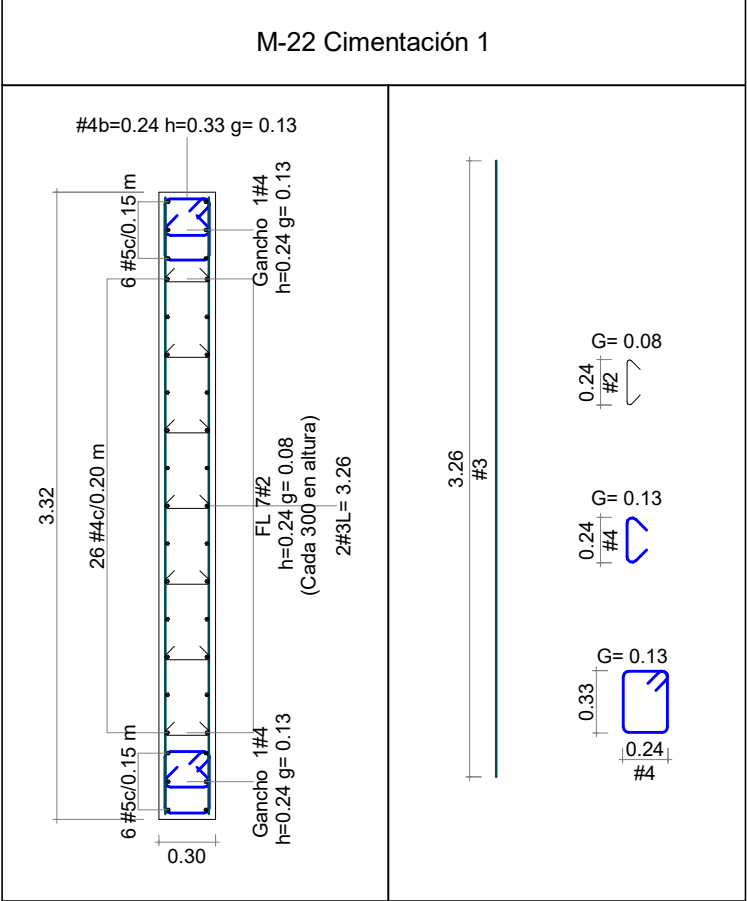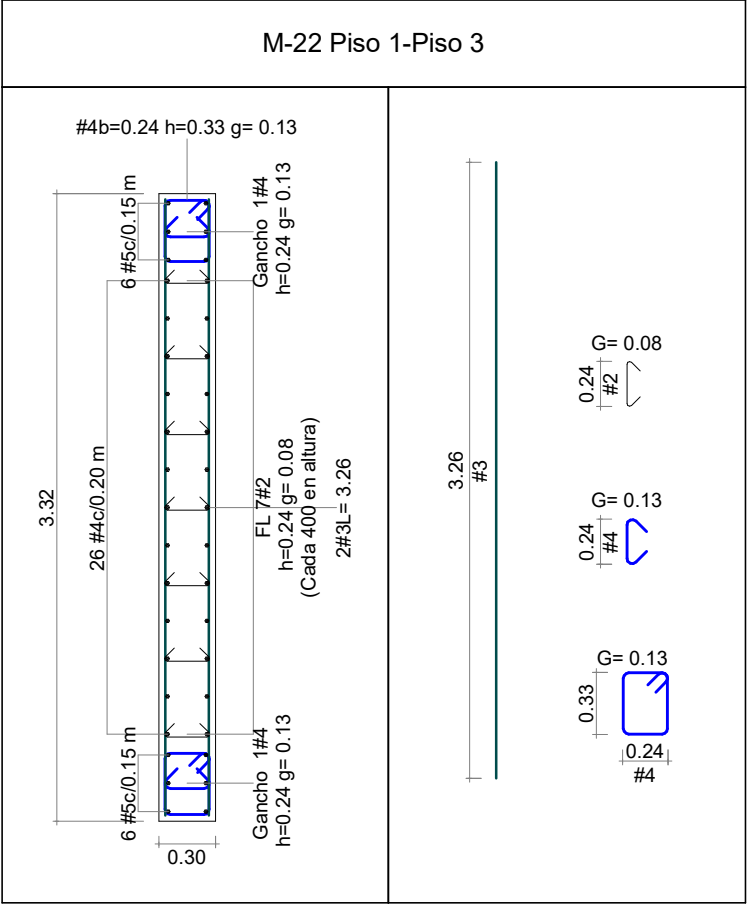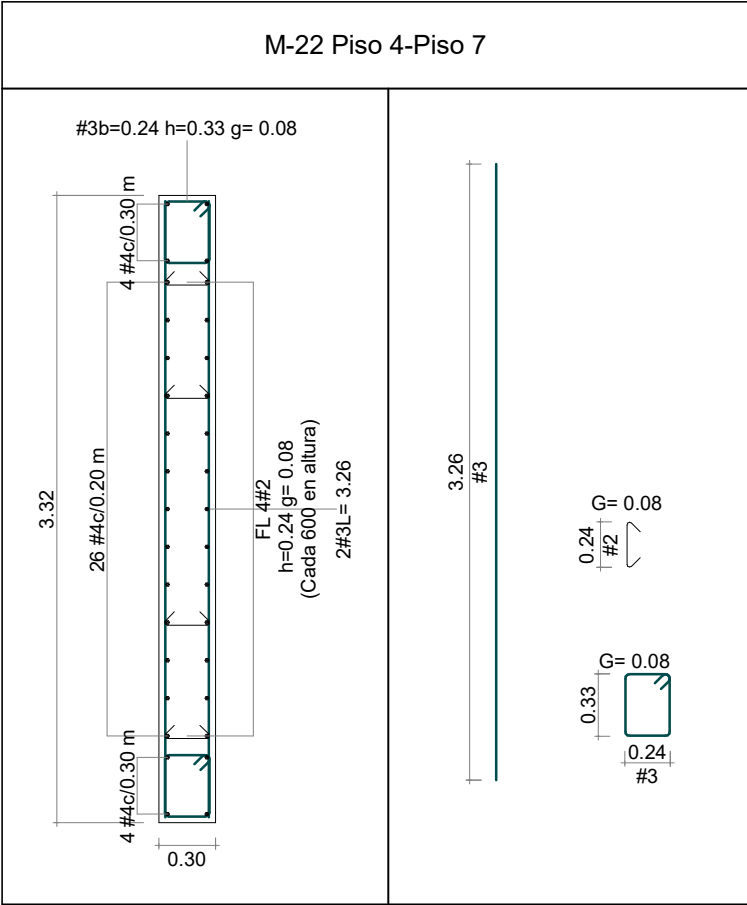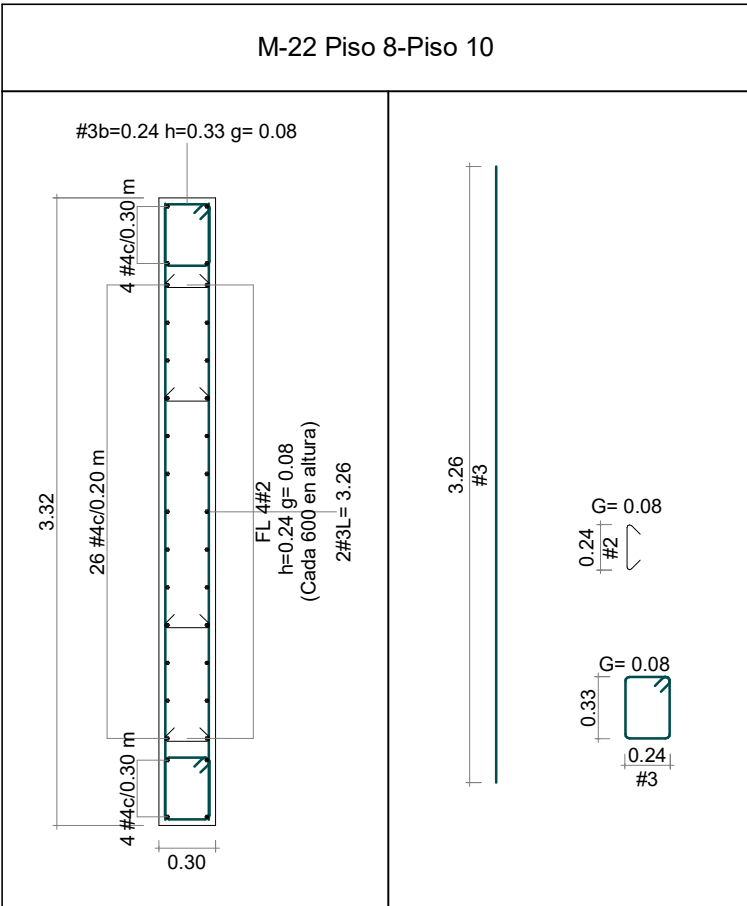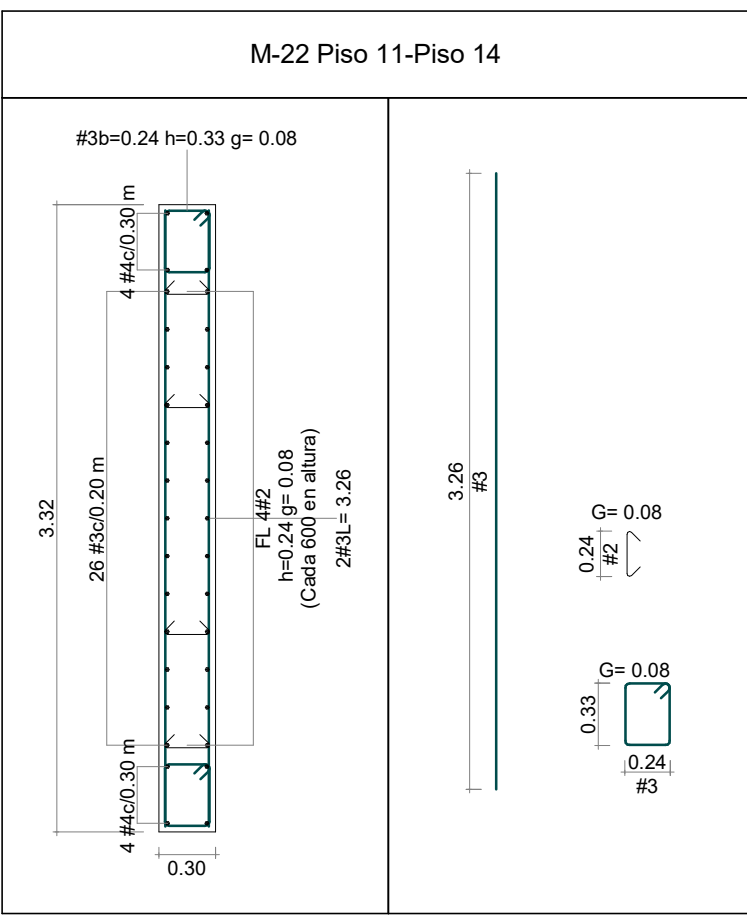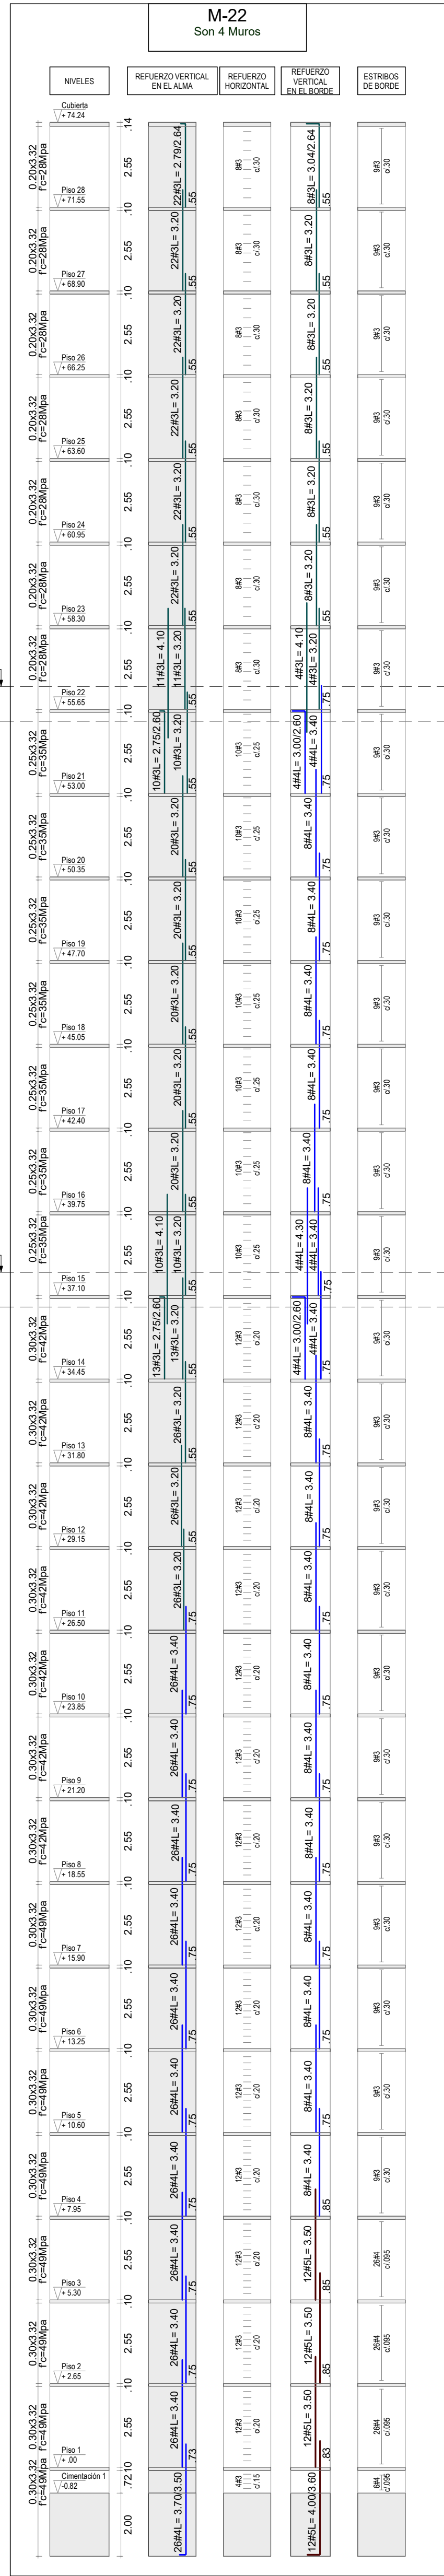

DETALLE DOBLEZ
Escala 1 : 10

NOTAS:
1. Ver detalles generales en el PL.N° 01.02
2. Ver detalles de muros en el PL.N° 11.20
3. Ver plantas de localización e identificación de muros en los PL. N°03.00-04.00-05.00-06.00-07.00-08.00 y 09.00

ESCALA 1:125

VERSIÓN :

3

PLANO N°

11.15



GERENTE DE PROYECTO
ROBERTO AYCARDI F.
MAT. 2520257258 CND

INGENIERO
CARLOS ANDRÉS WILCHES C.

MODELADOR
DANIEL CASTELLANOS

MODIFICACIONES	FECHA
Emisión Inicial	28-02-2025
Ajuste longitudes refuerzos y se incluye detalle sobre ancho muro	03-10-2025
Ajuste refuerzo muros	26-02-2026



LA SCALA

LA SCALA_EST_TOR-1

TORRE 1

CALLE 170 CON AV. BOYACA

DESPIECE DE MUROS

LA SCALA_EST_TOR-1_11.15_MUR-D16

REVISOR ESTRUCTURAL
RAMÓN ANDRÉS ALVAREZ MANTILLA
MAT. 25202-34654 CND.

PLANO N°

11.15

VERSIÓN :

3