
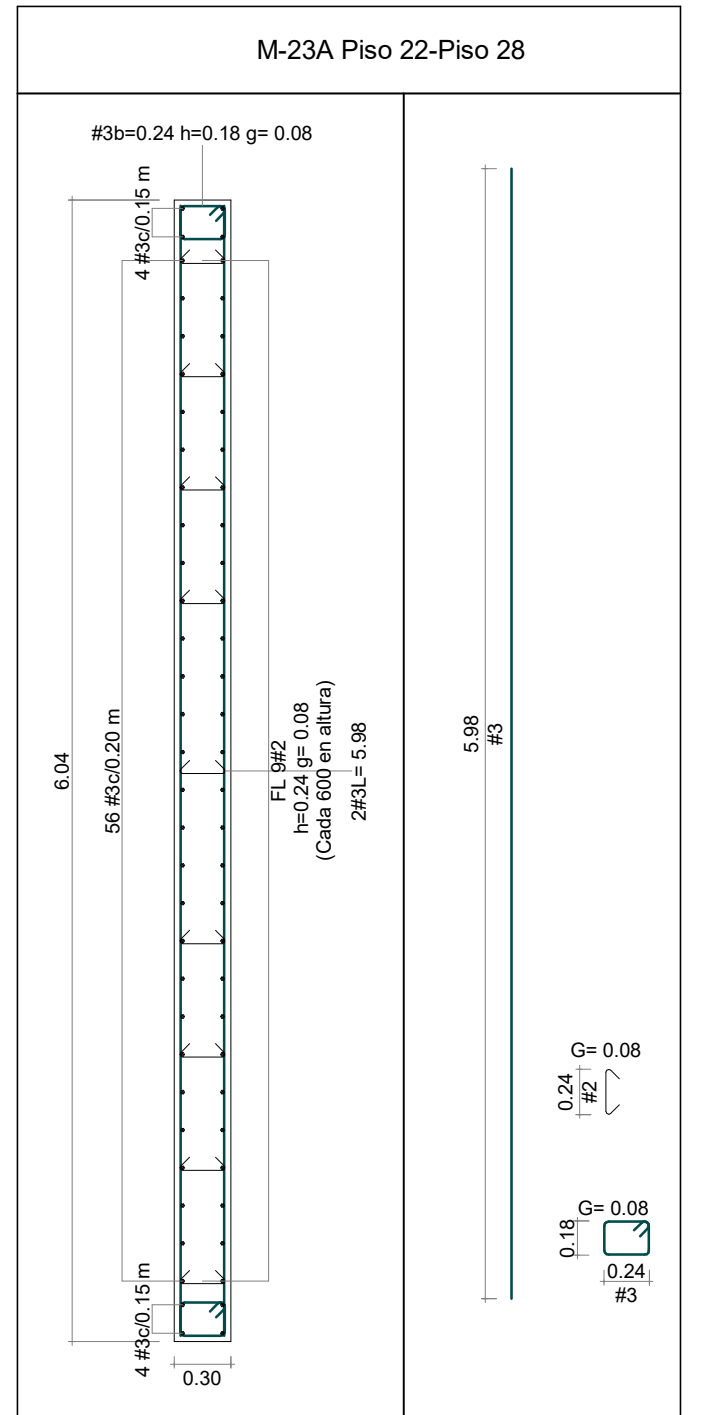
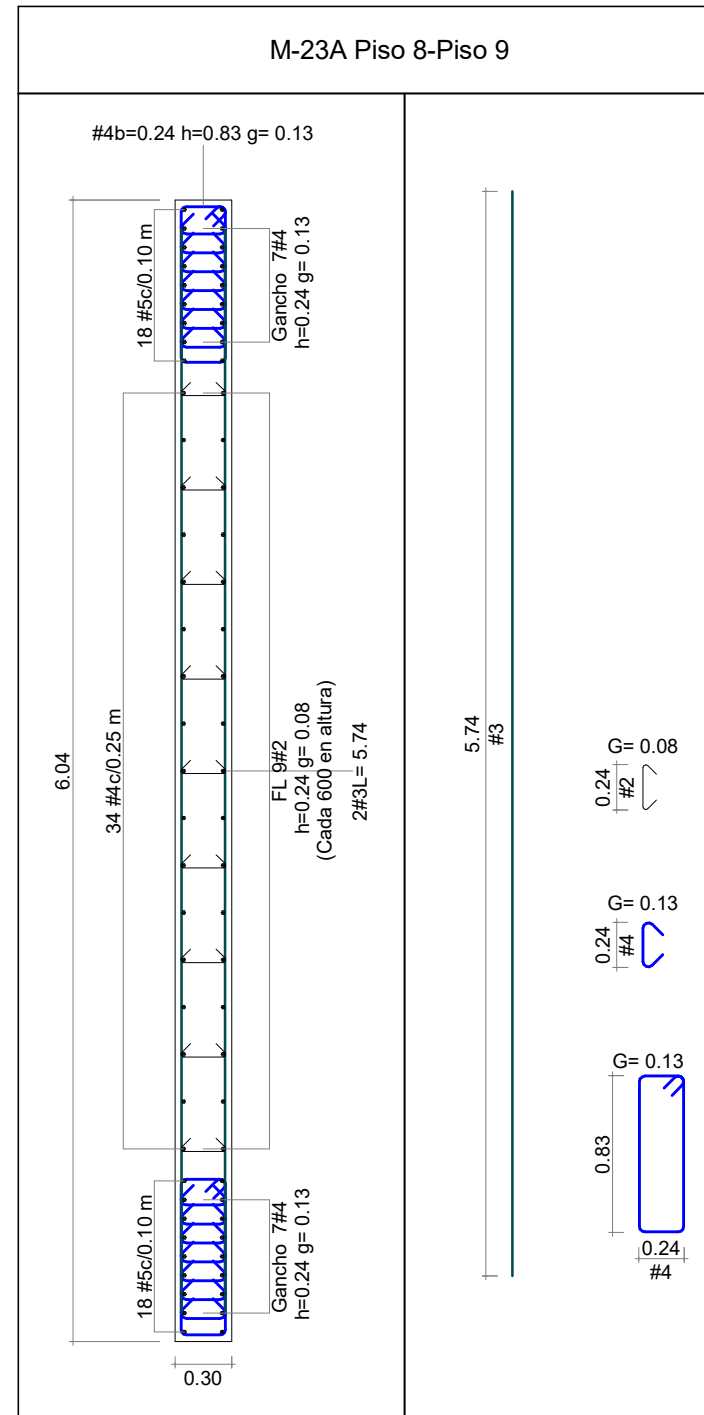
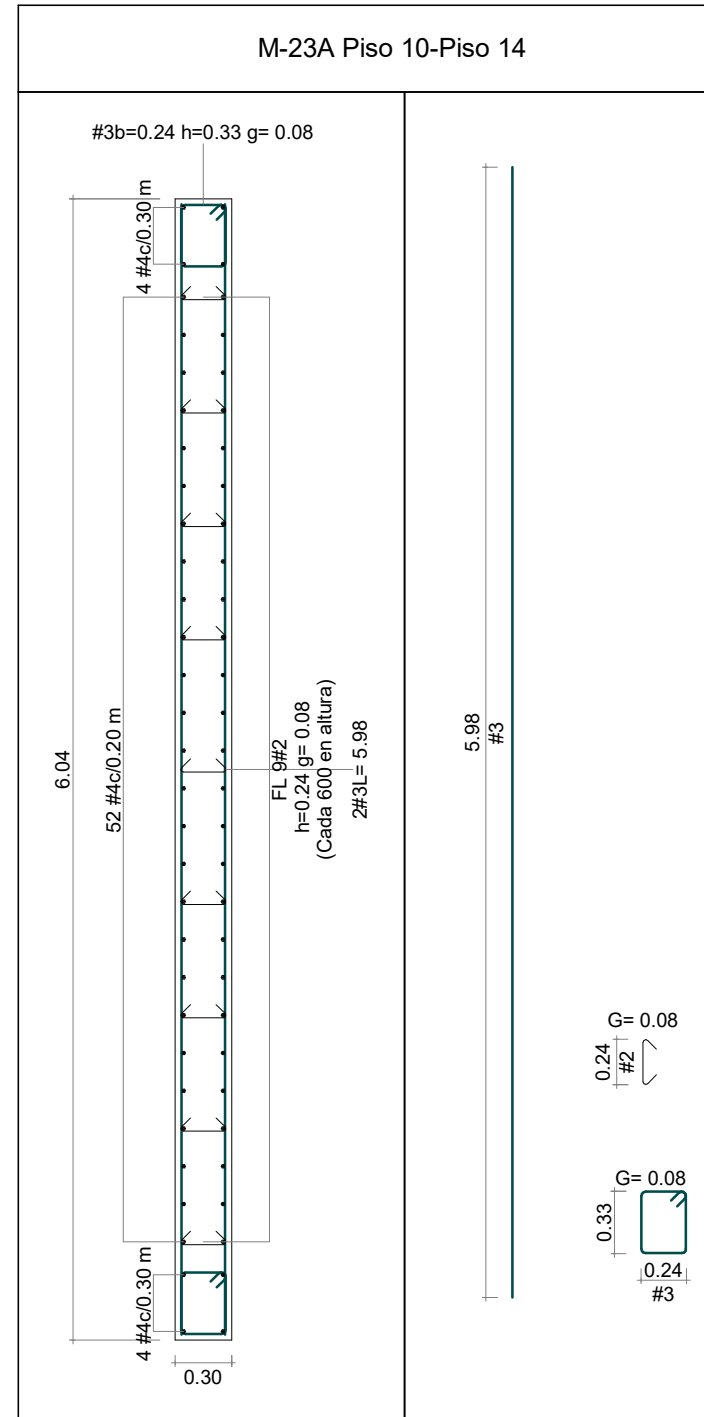
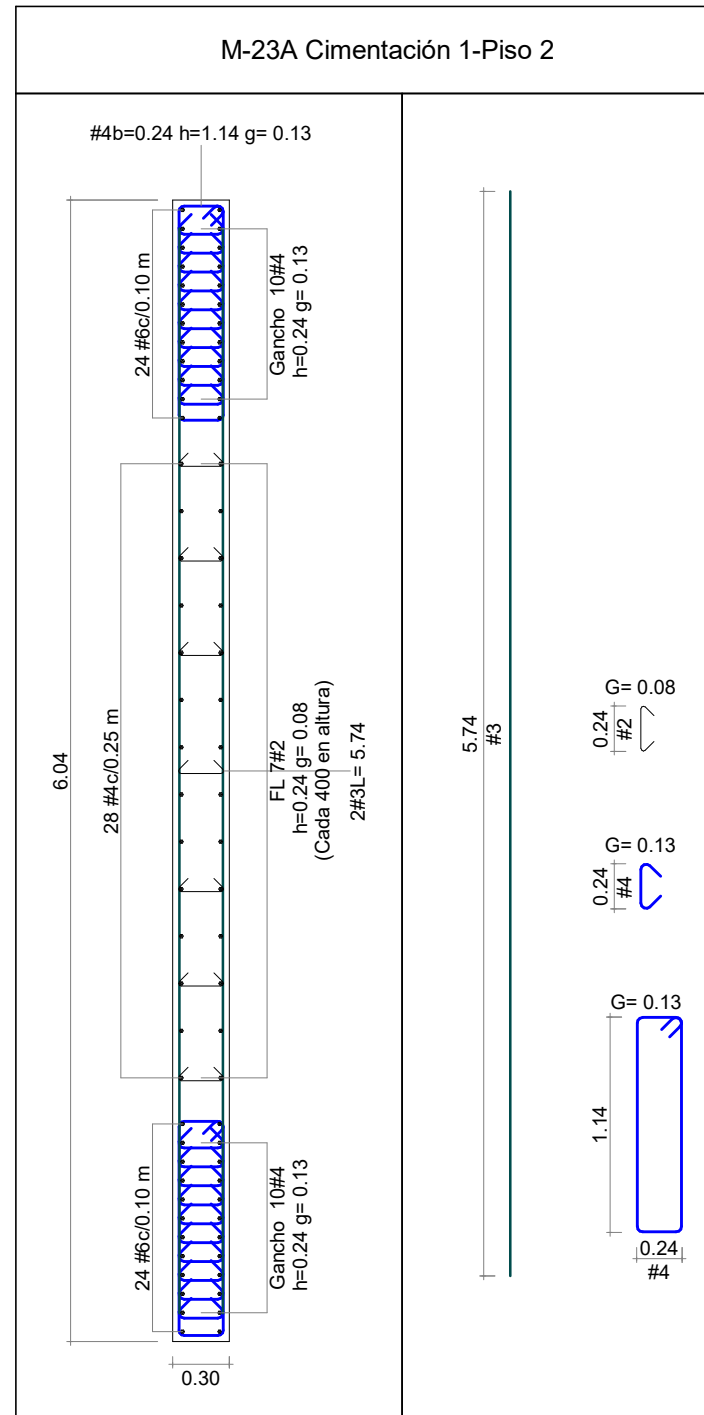
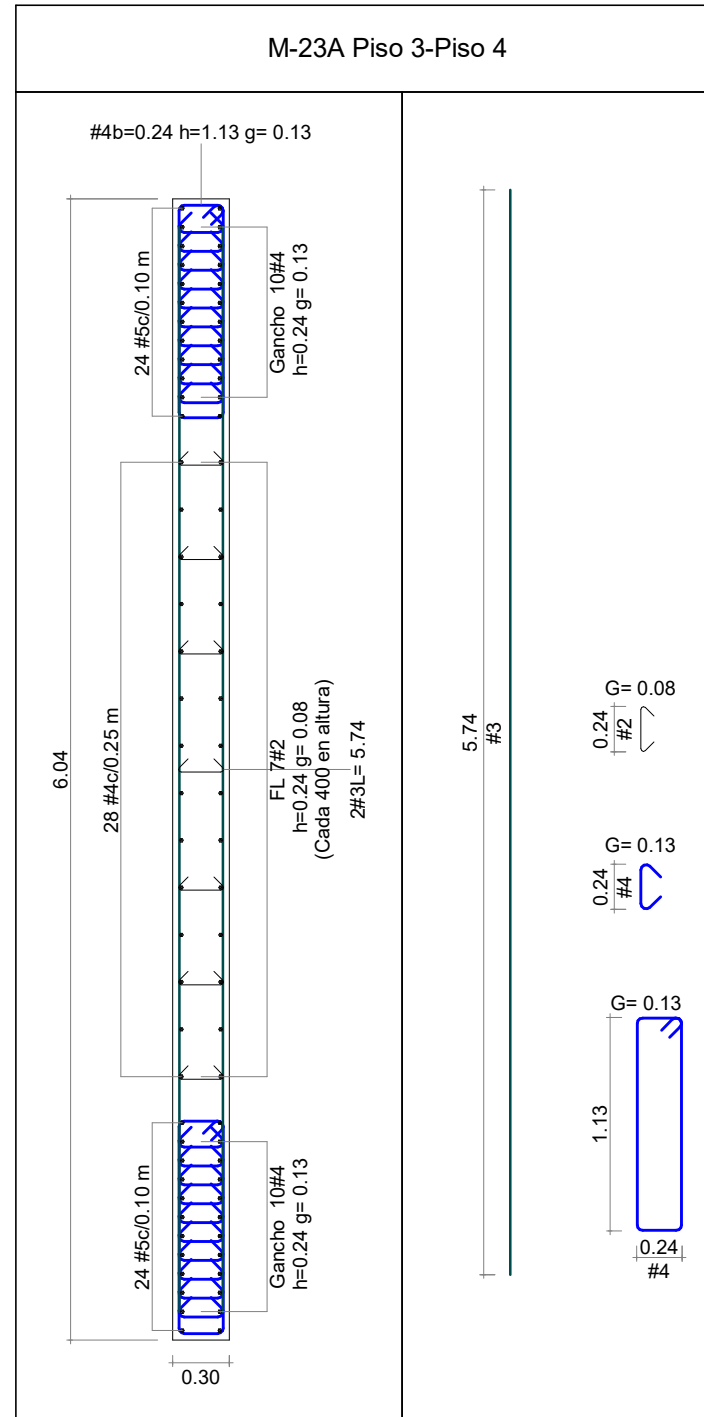
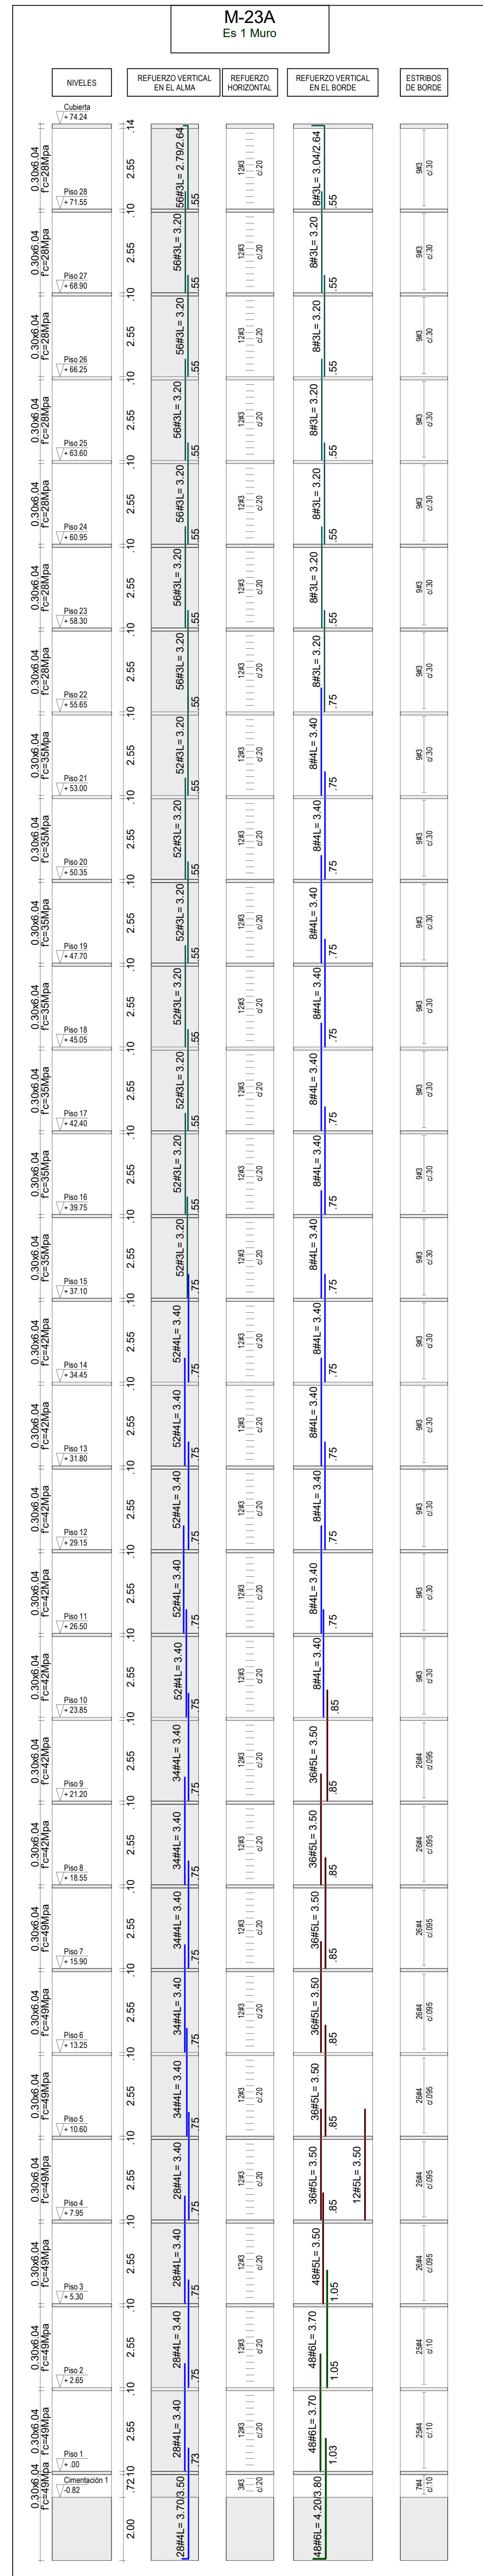
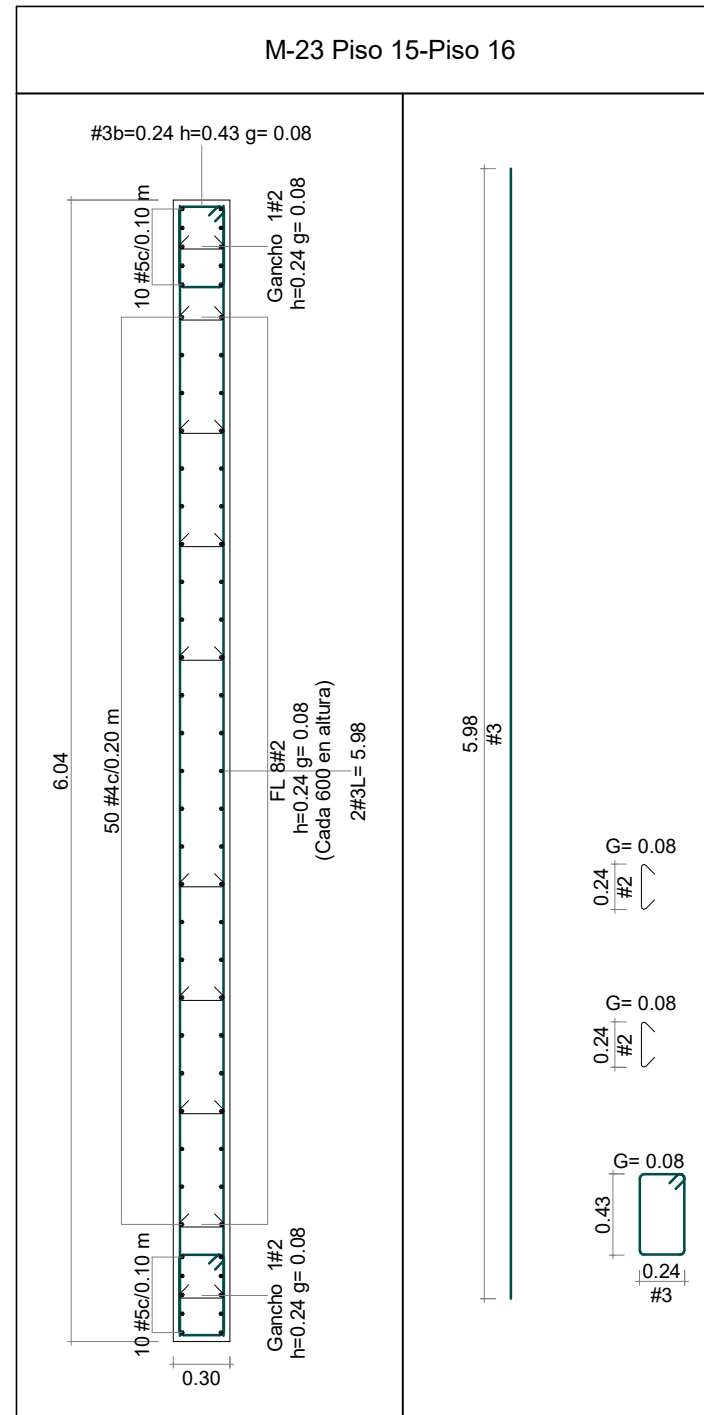
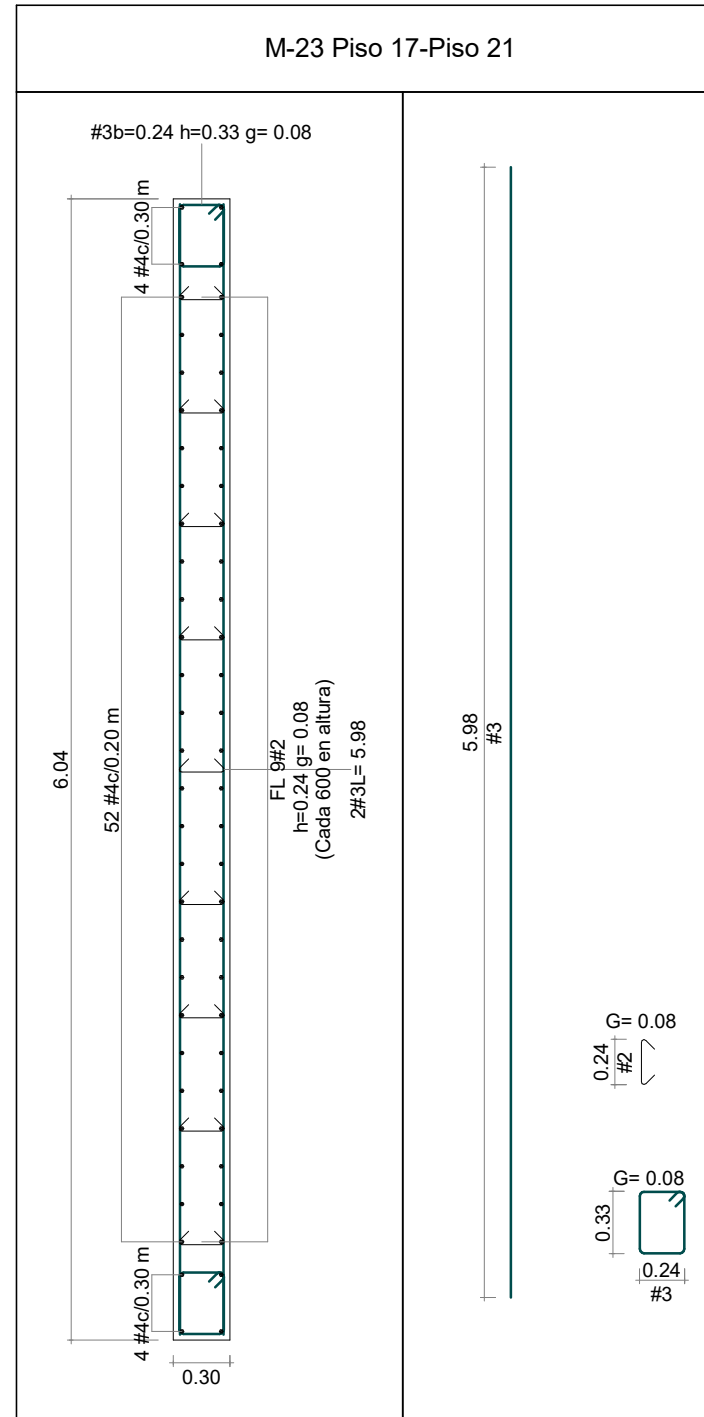
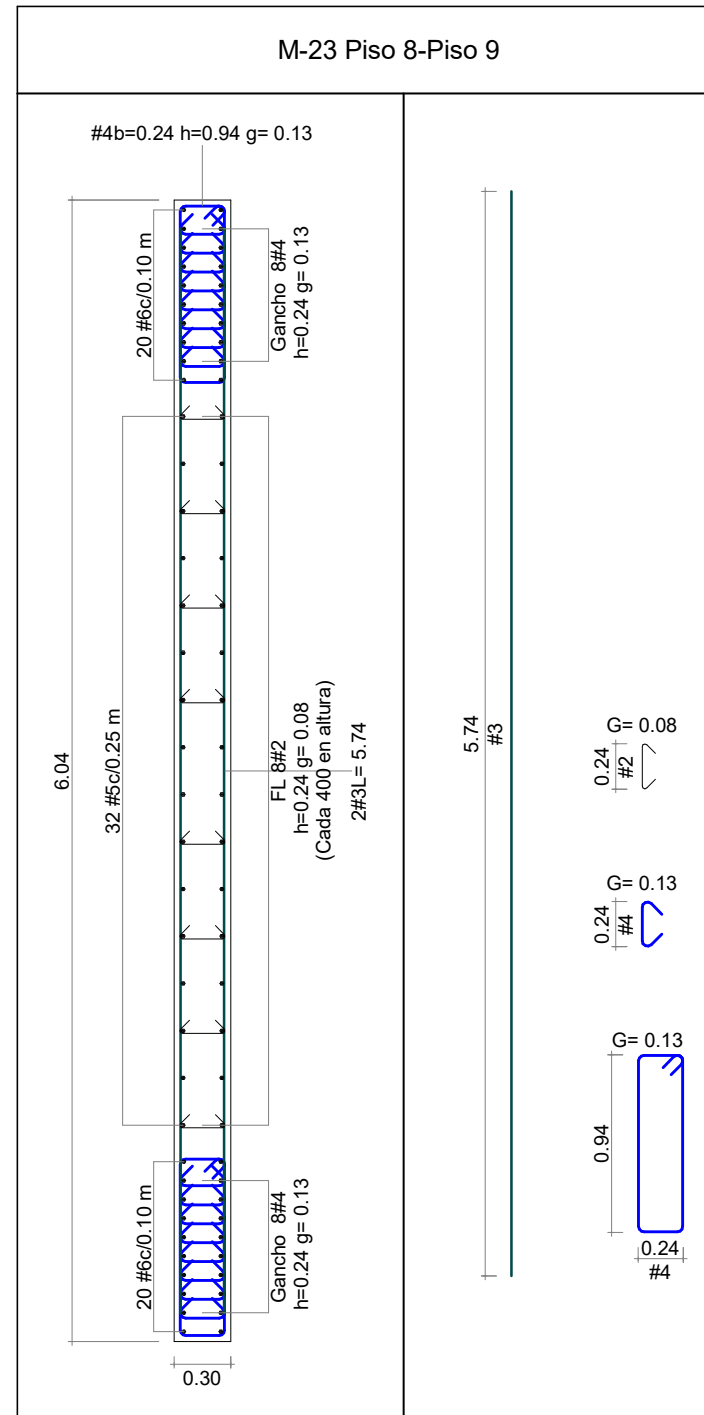
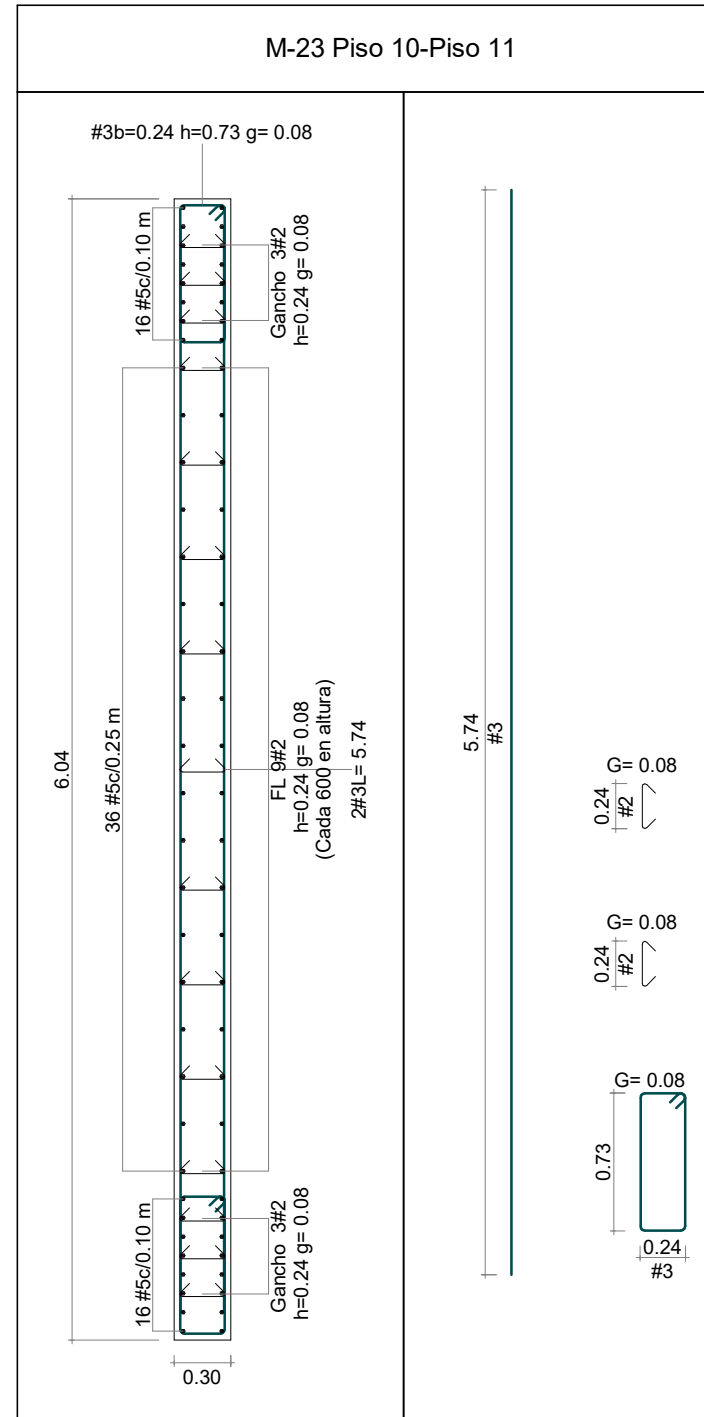
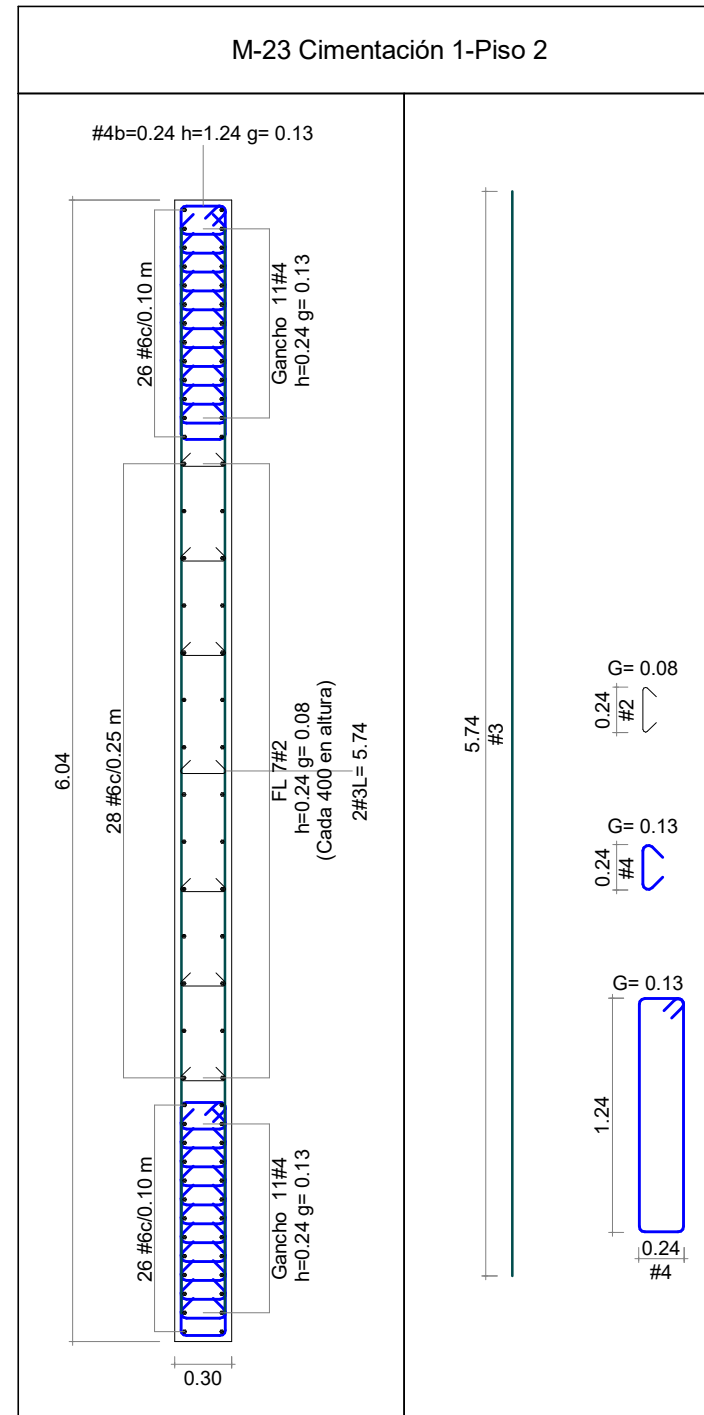
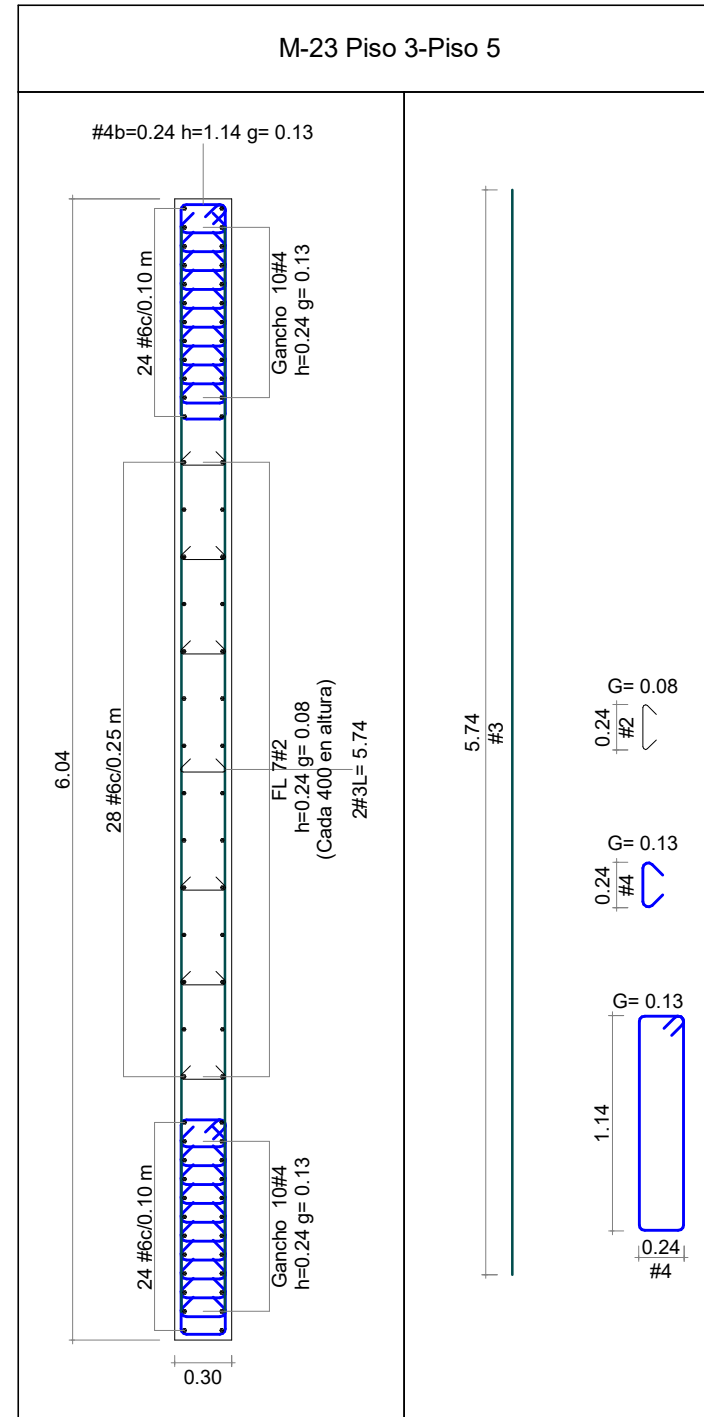


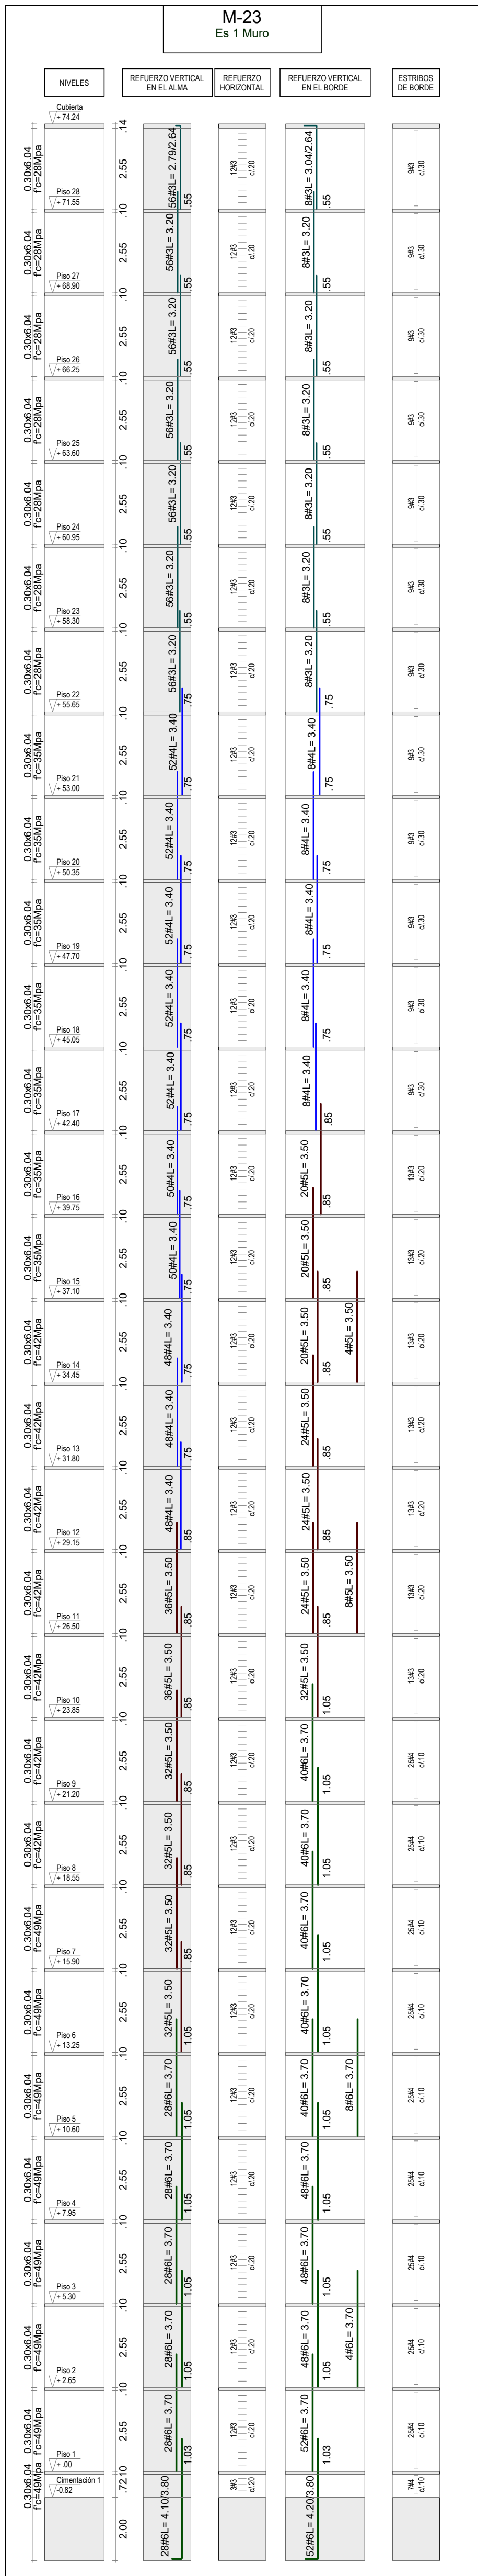

ESCALA 1:125

# 11.16

Aycardi  
Estructural

**INGENIERO**  
**CARLOS ANDRÉS WILCHES C.**

| MODIFICACIONES    | FECHA      |
|-------------------|------------|
| Inicial           | 28-02-2025 |
| Alturas refuerzos | 03-10-2025 |
| Trazo muros       | 26-02-2026 |
|                   |            |
|                   |            |



ALLE 170 CON AV. BOYACA

LA SCALA\_EST\_TOR-1\_11.16\_MUR-D17

Nº VERSIÓN :

## 11.16

3