


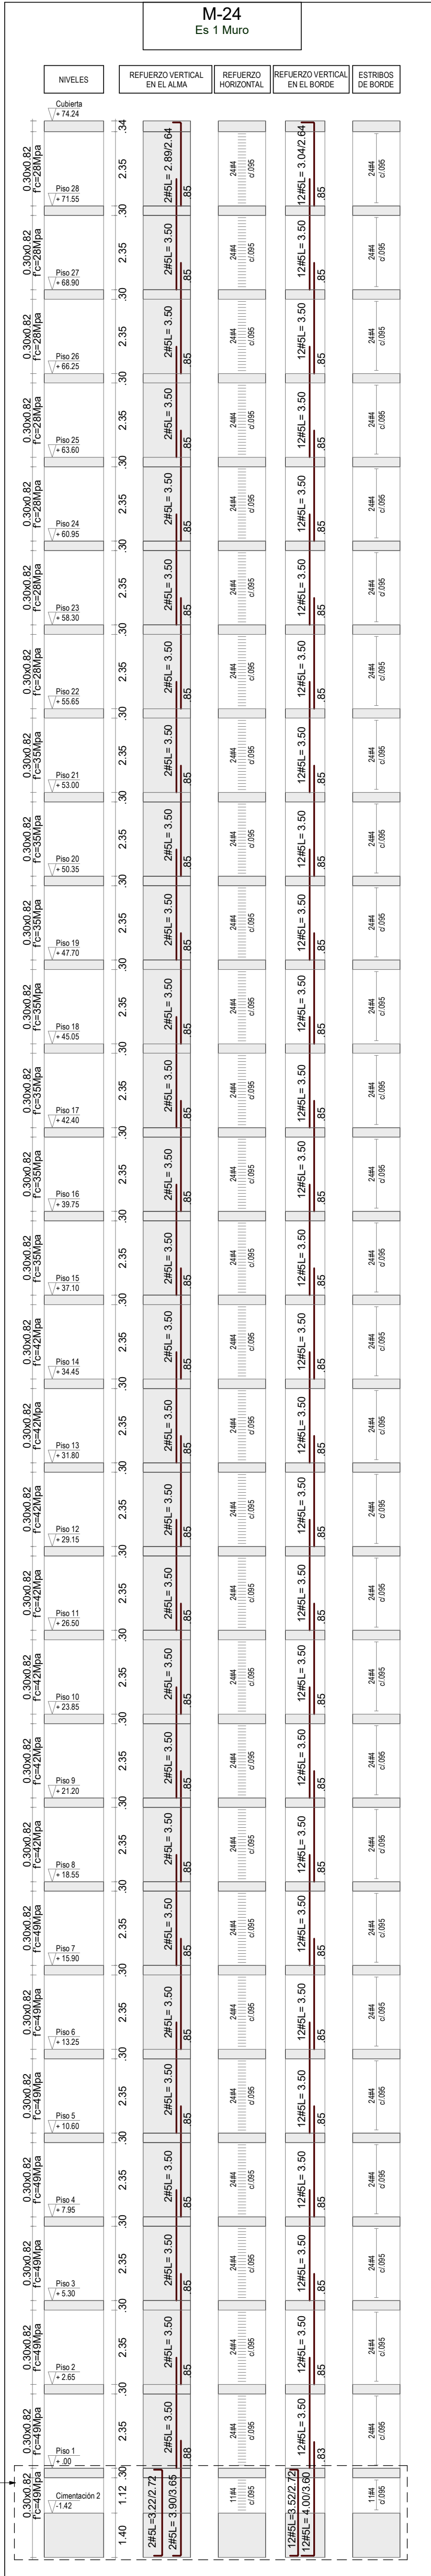
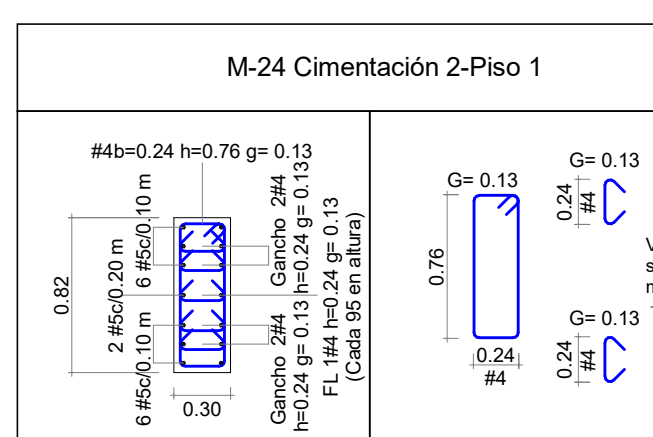
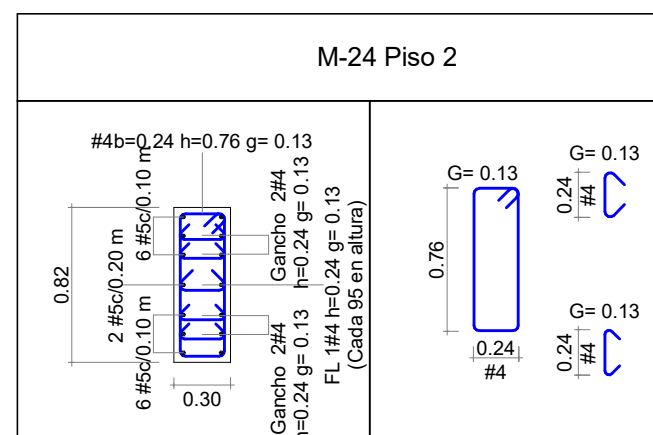
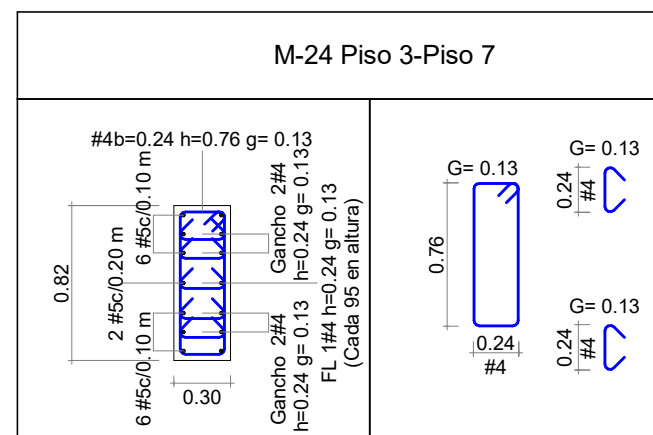


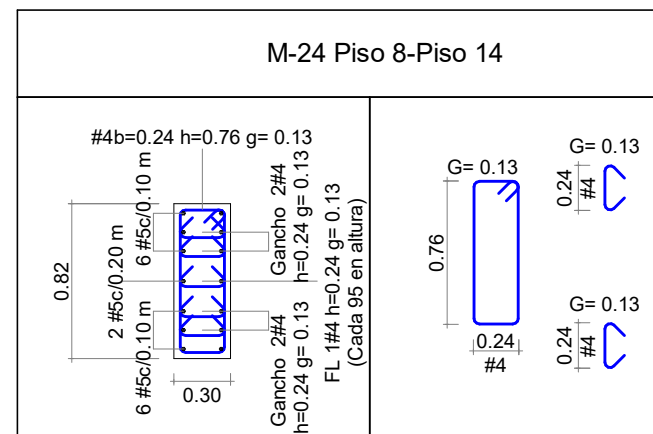


Ver detalle de sobre
ancho muro

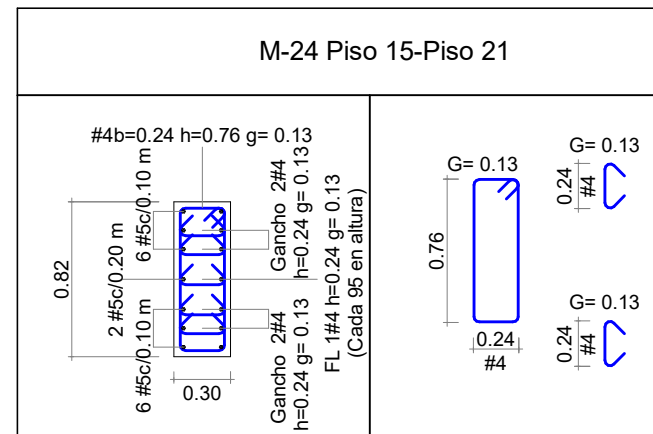





DETALLE SOBRE ANCHO EN MURO M-24
Escala 1 : 25

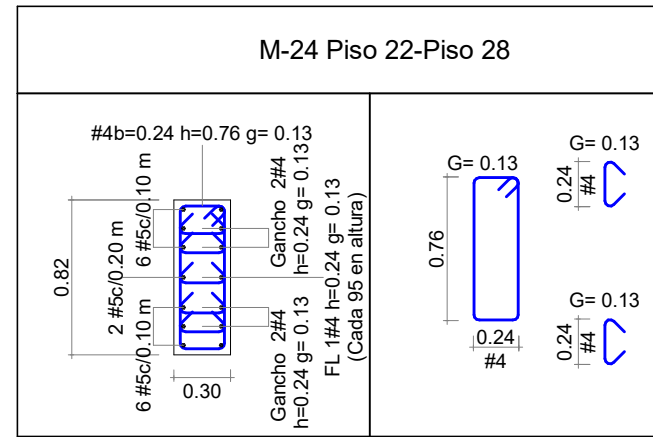












Ver detalle de
sobre ancho
muro

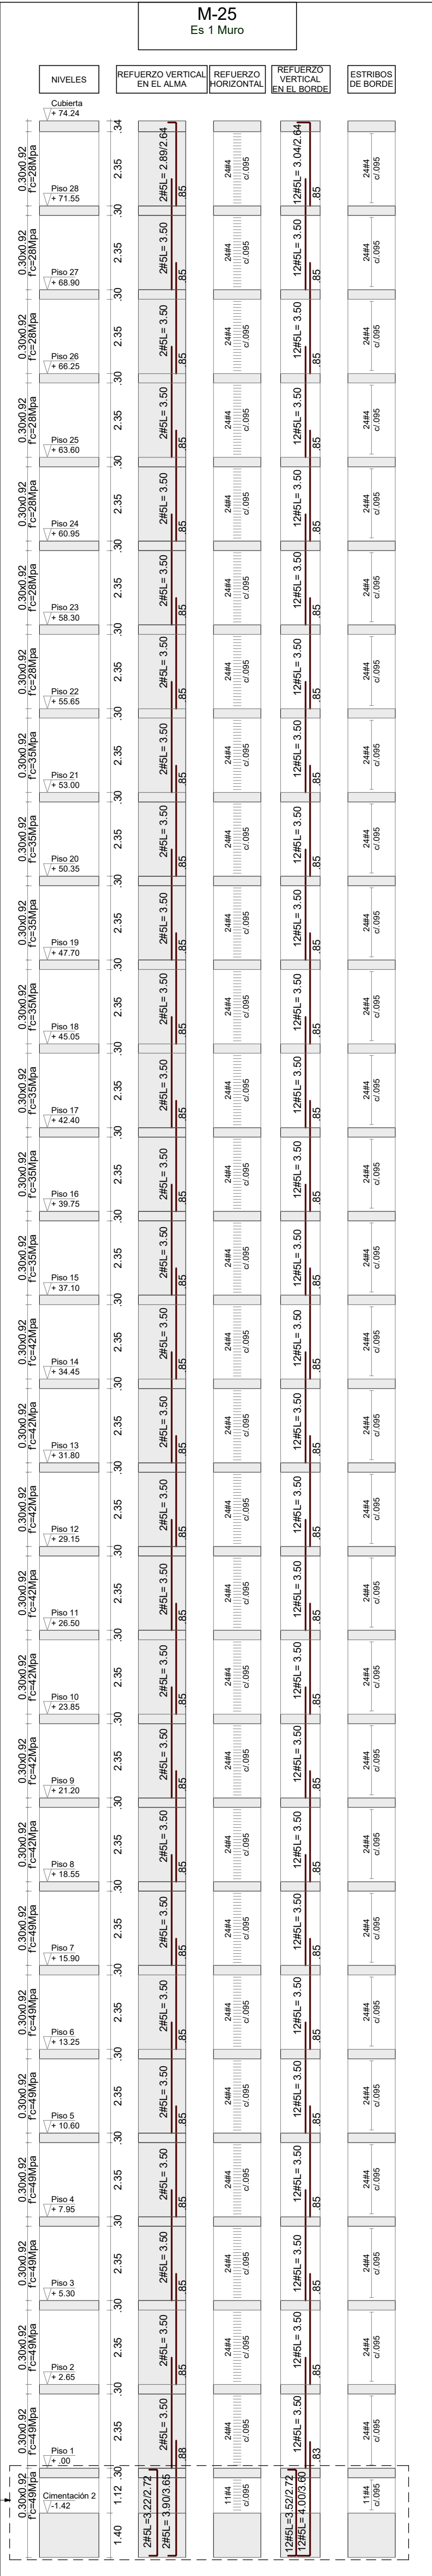


DETALLE SOBRE ANCHO EN MURO M-25
Escala 1 : 25

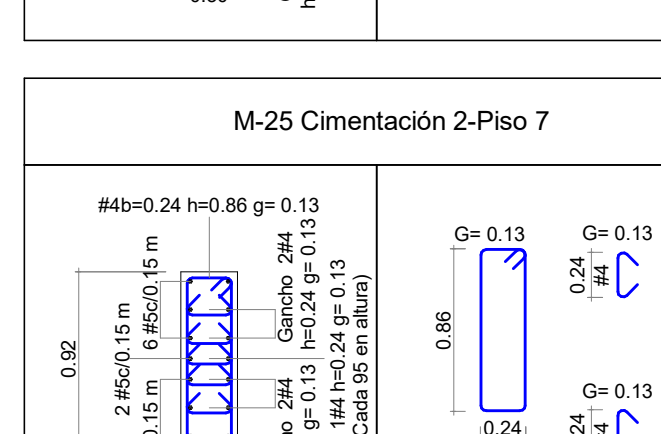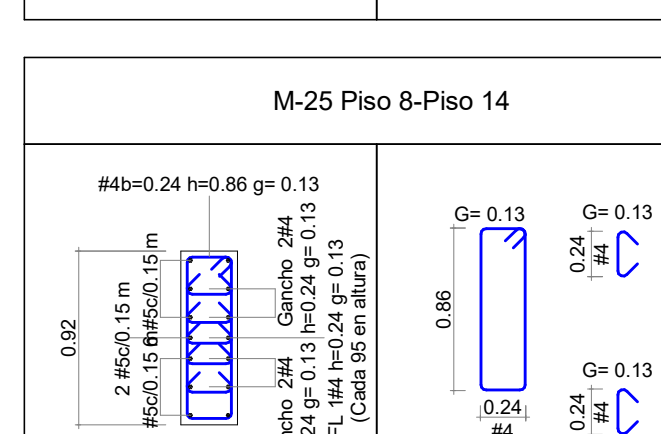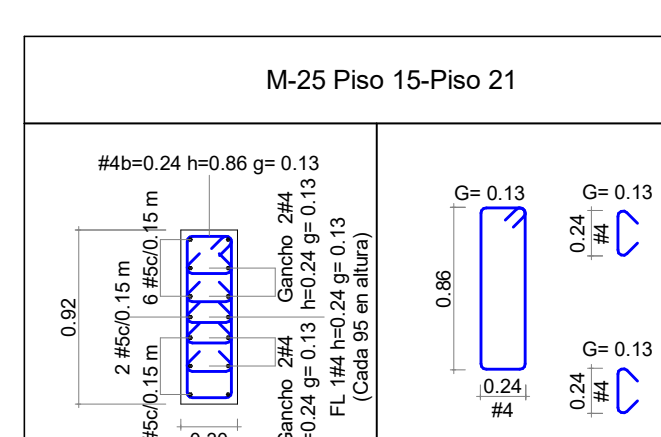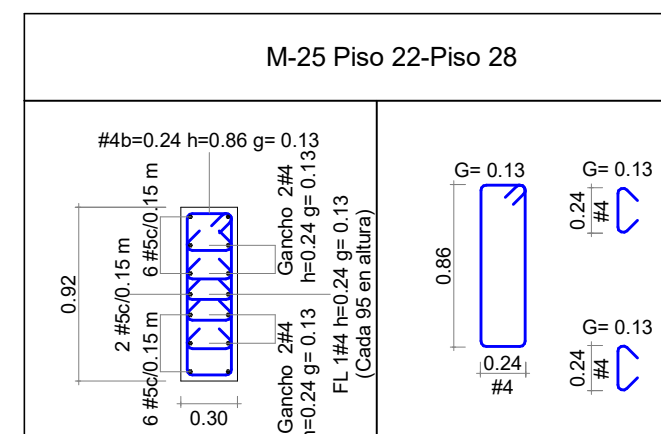

Ver detalle de
sobre ancho
muro

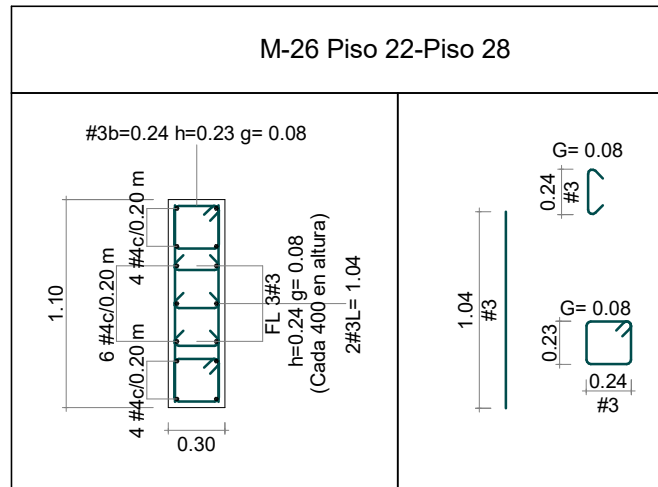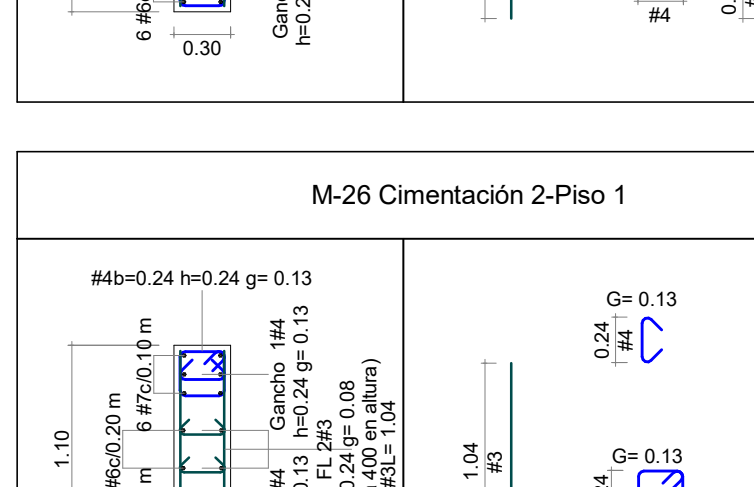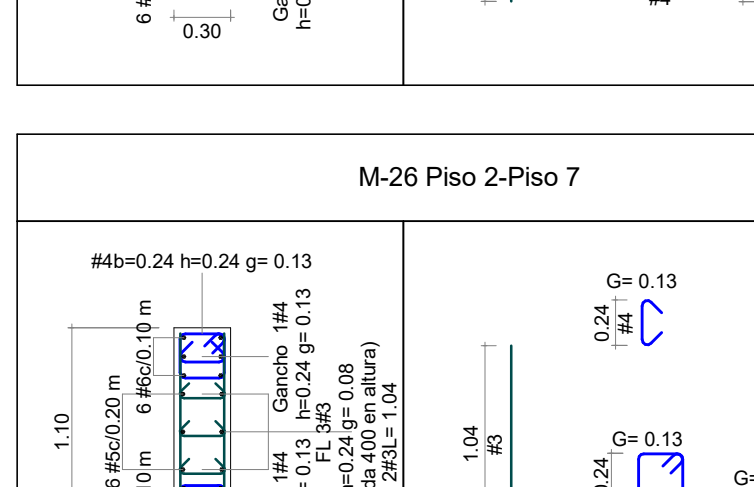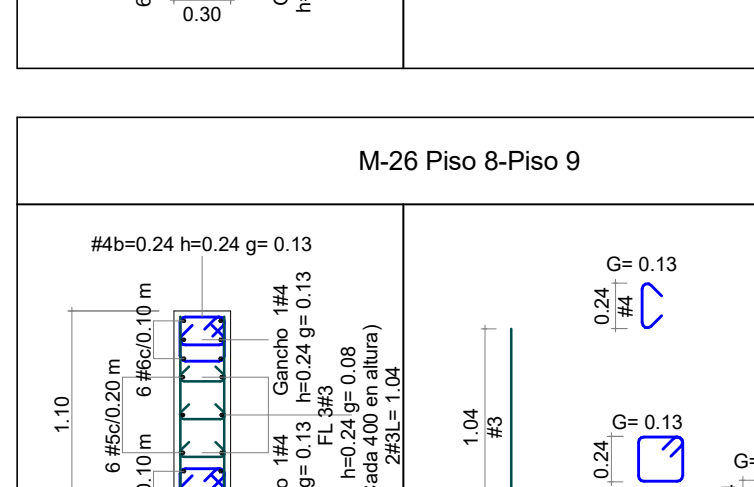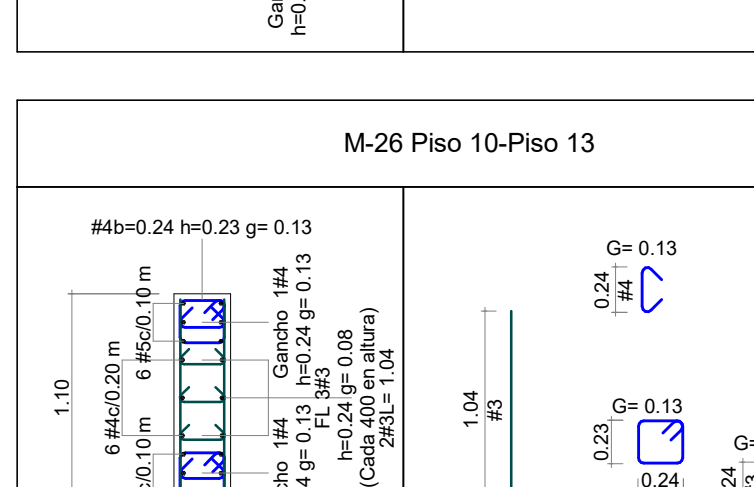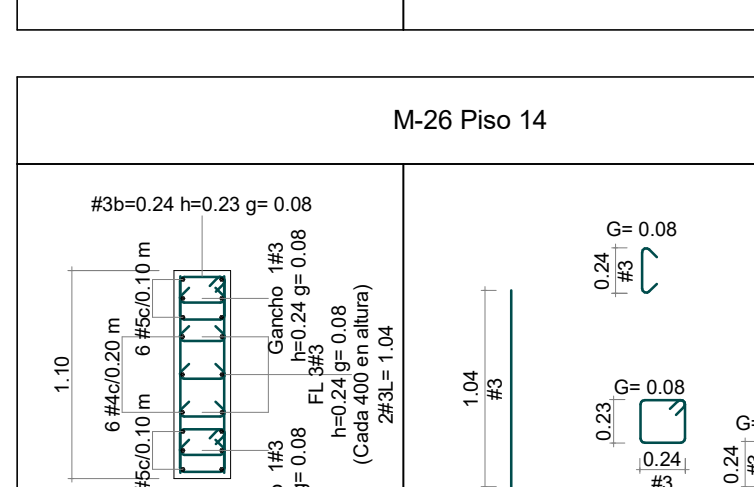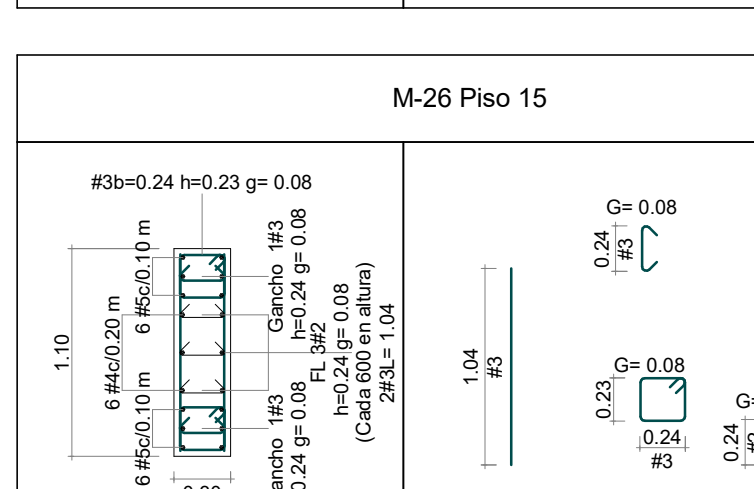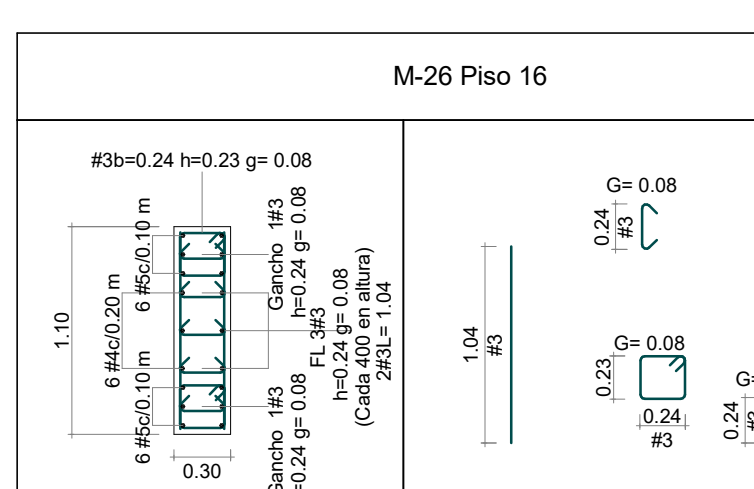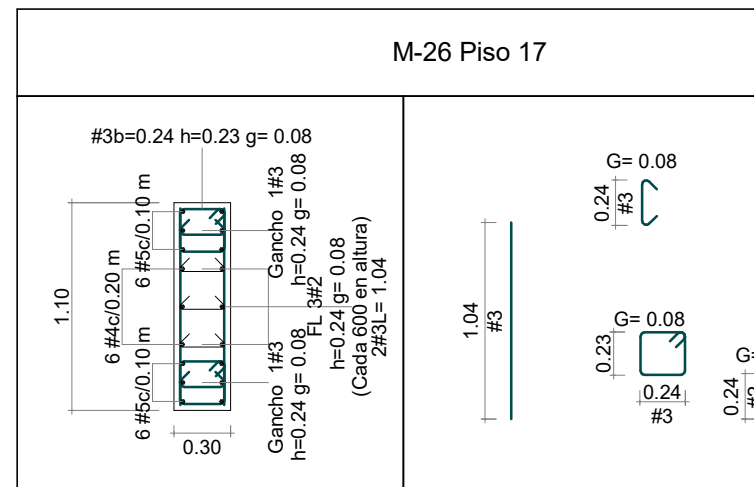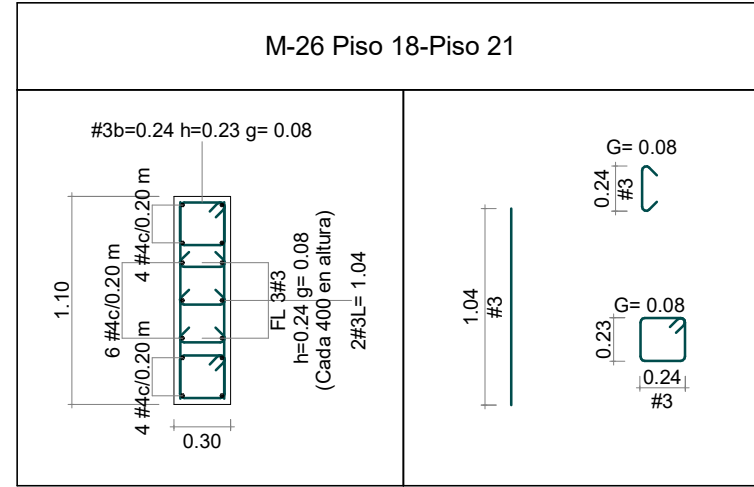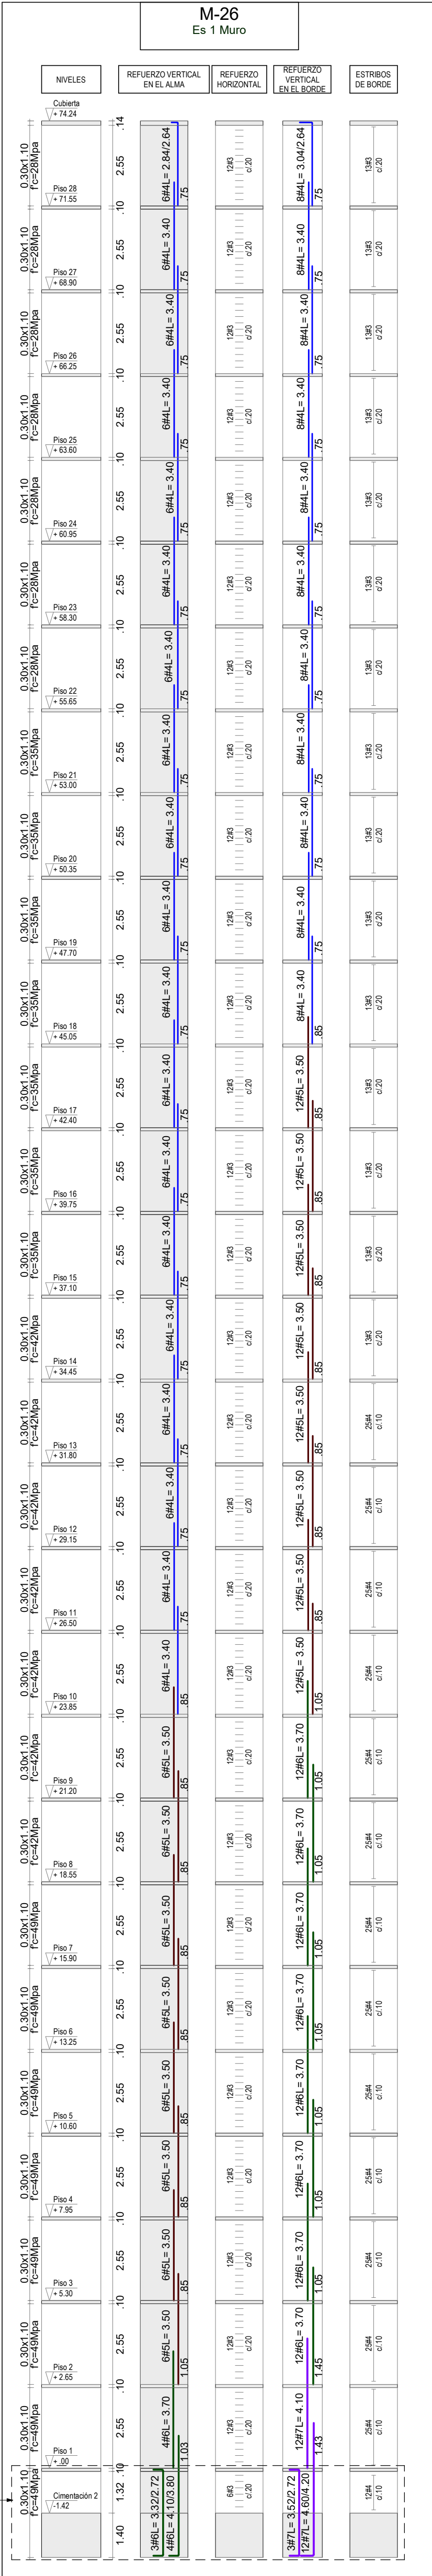

DETALLE SOBRE ANCHO EN MURO M-26
Escala 1 : 25

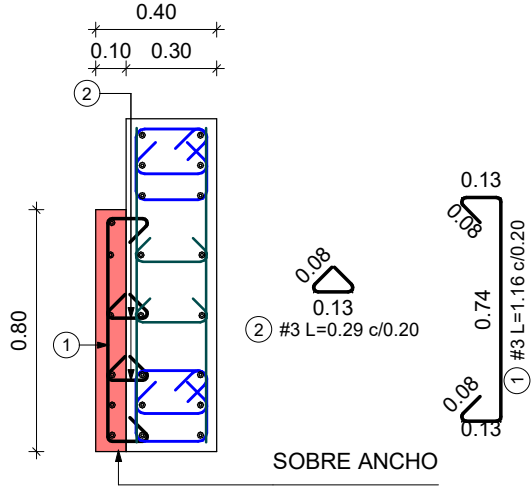

- NOTAS:
1. Ver detalles generales en el PLN° 01.02
 2. Ver detalle de muros en el PLN° 11.20
 3. Ver plantas de localización e identificación de muros en los PL. N°03.00-04.00-05.00-06.00-07.00-08.00 y 09.00

ESCALA 1:125

PLANO N° 11.17

VERSIÓN : 3



GERENTE DE PROYECTO
ROBERTO AYCARDI F.
MAT. 2520257258 CND

INGENIERO
CARLOS ANDRÉS WILCHES C.

MODELADOR
DANIEL CASTELLANOS

MODIFICACIONES	FECHA
Emisión Inicial	28-02-2025
Ajuste longitudes refuerzos y se incluye detalle sobre ancho muro	03-10-2025
Ajuste refuerzo muros	26-02-2026



LA SCALA

LA SCALA_EST_TOR-1

TORRE 1

CALLE 170 CON AV. BOYACA

DESPIECE DE MUROS

LA SCALA_EST_TOR-1_11.17_MUR-D18

REVISOR ESTRUCTURAL

RAMÓN ANDRÉS ALVAREZ MANTILLA
MAT. 25202-346546 CND.

PLANO N°

11.17

VERSIÓN :

3