

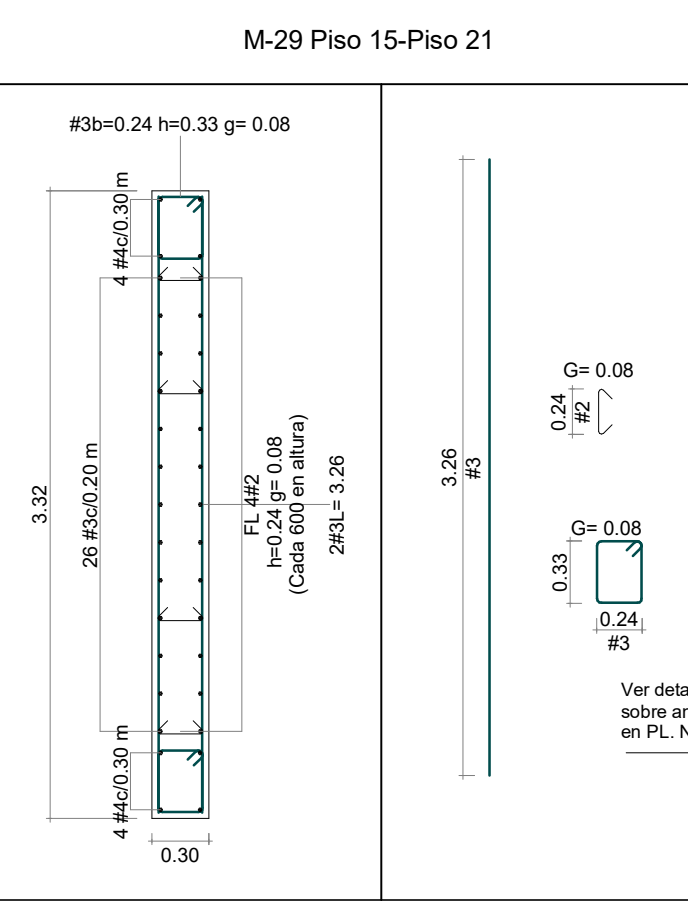
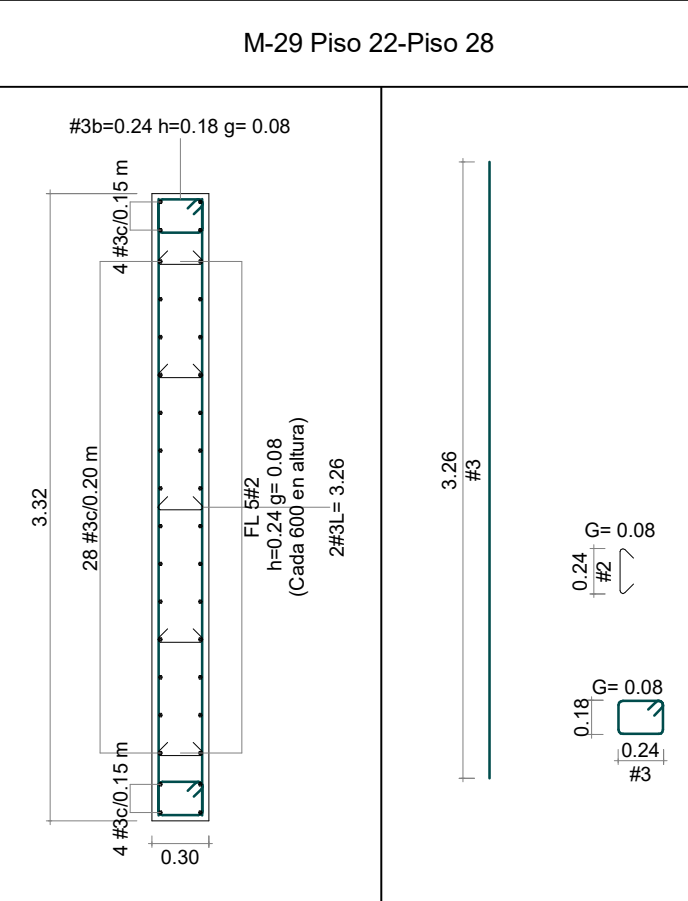
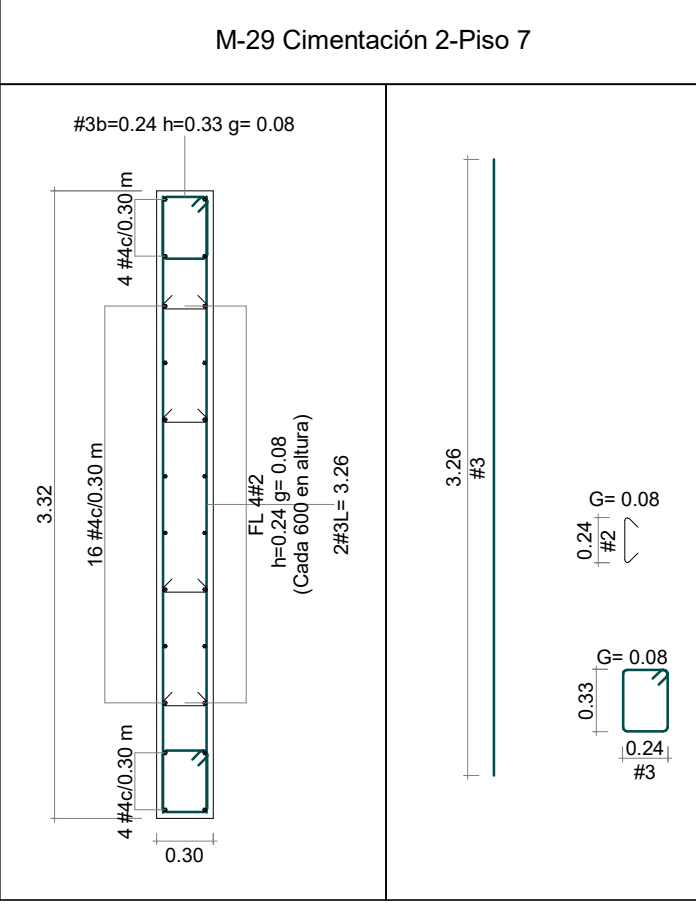
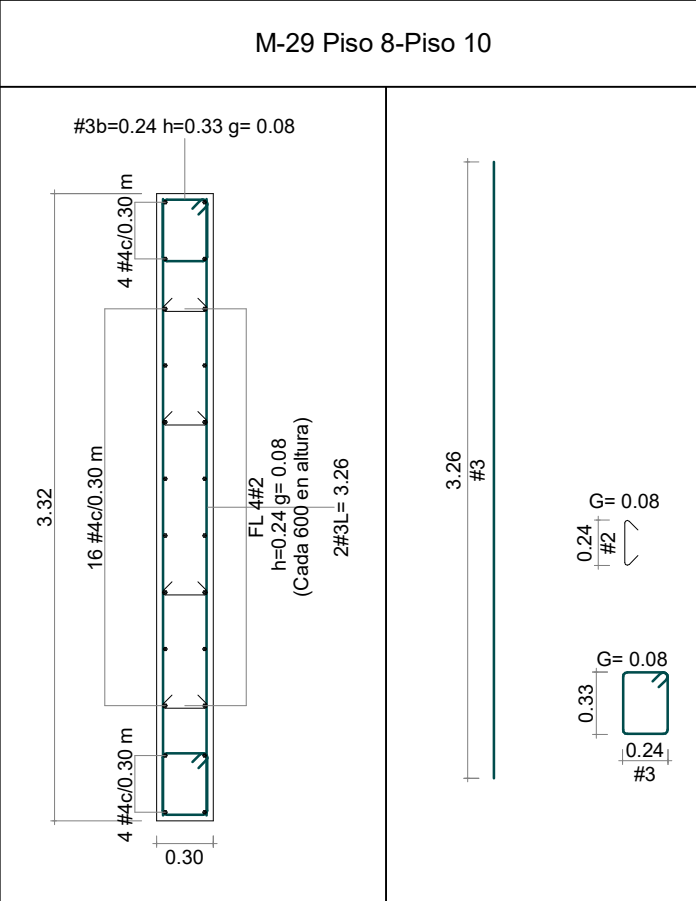
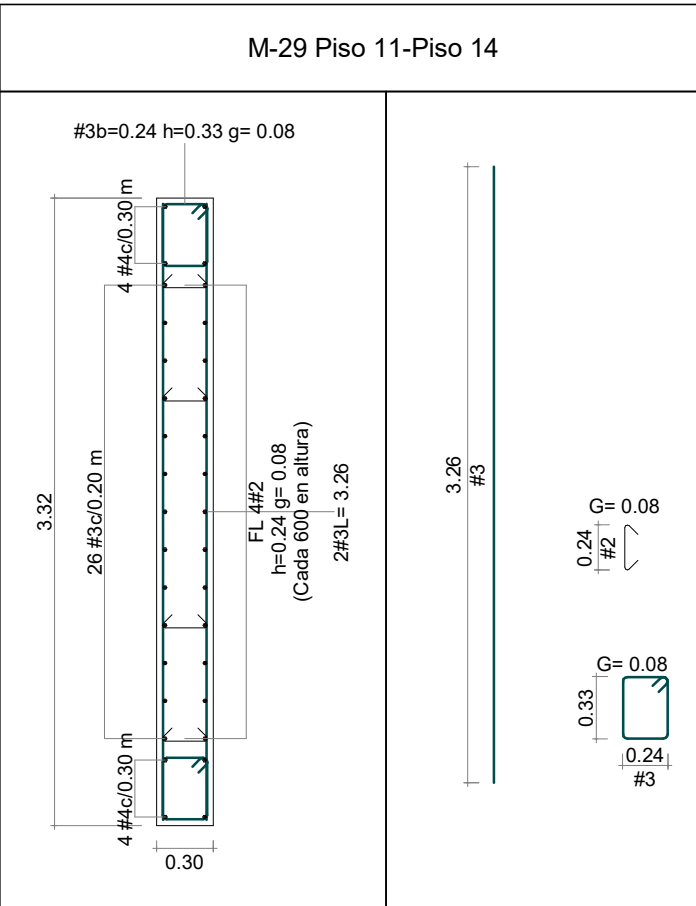
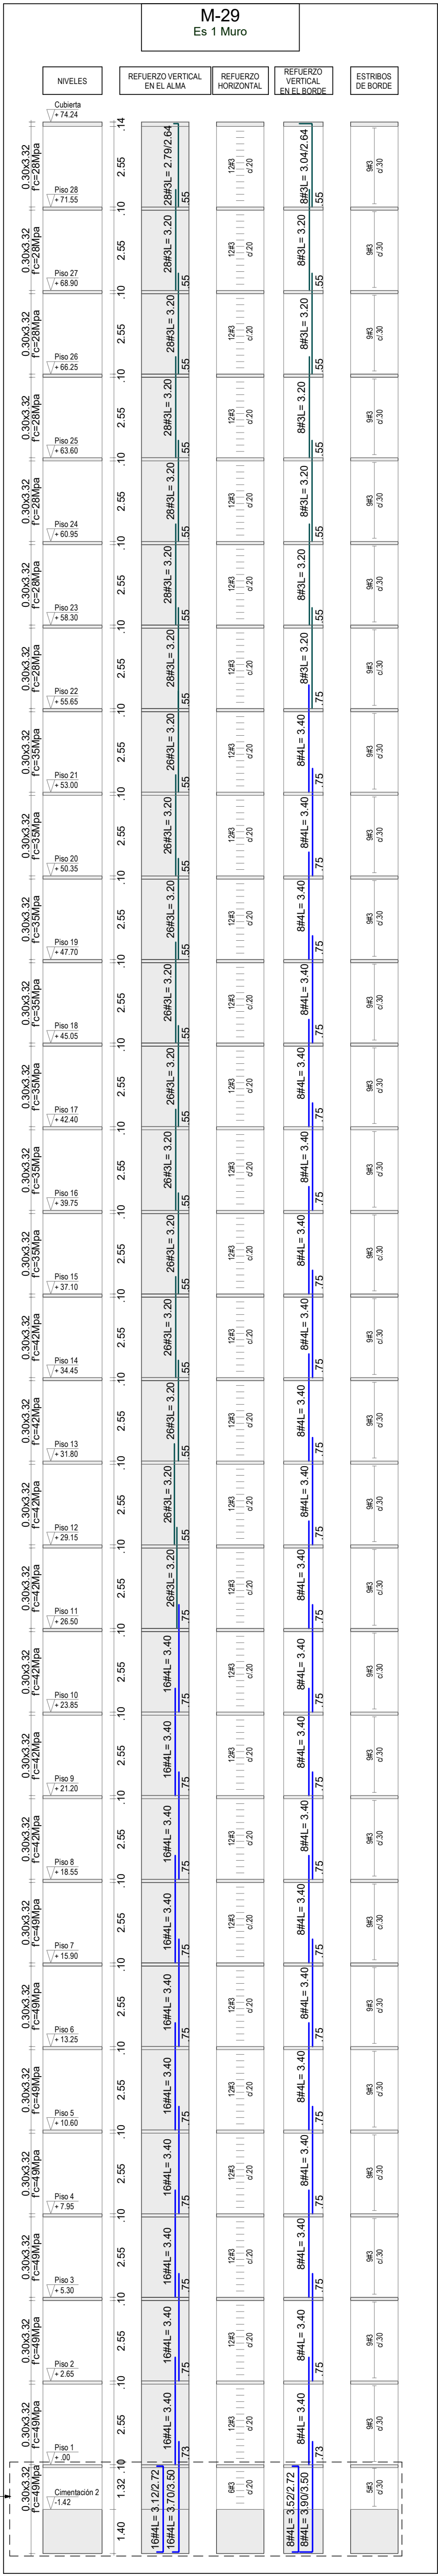
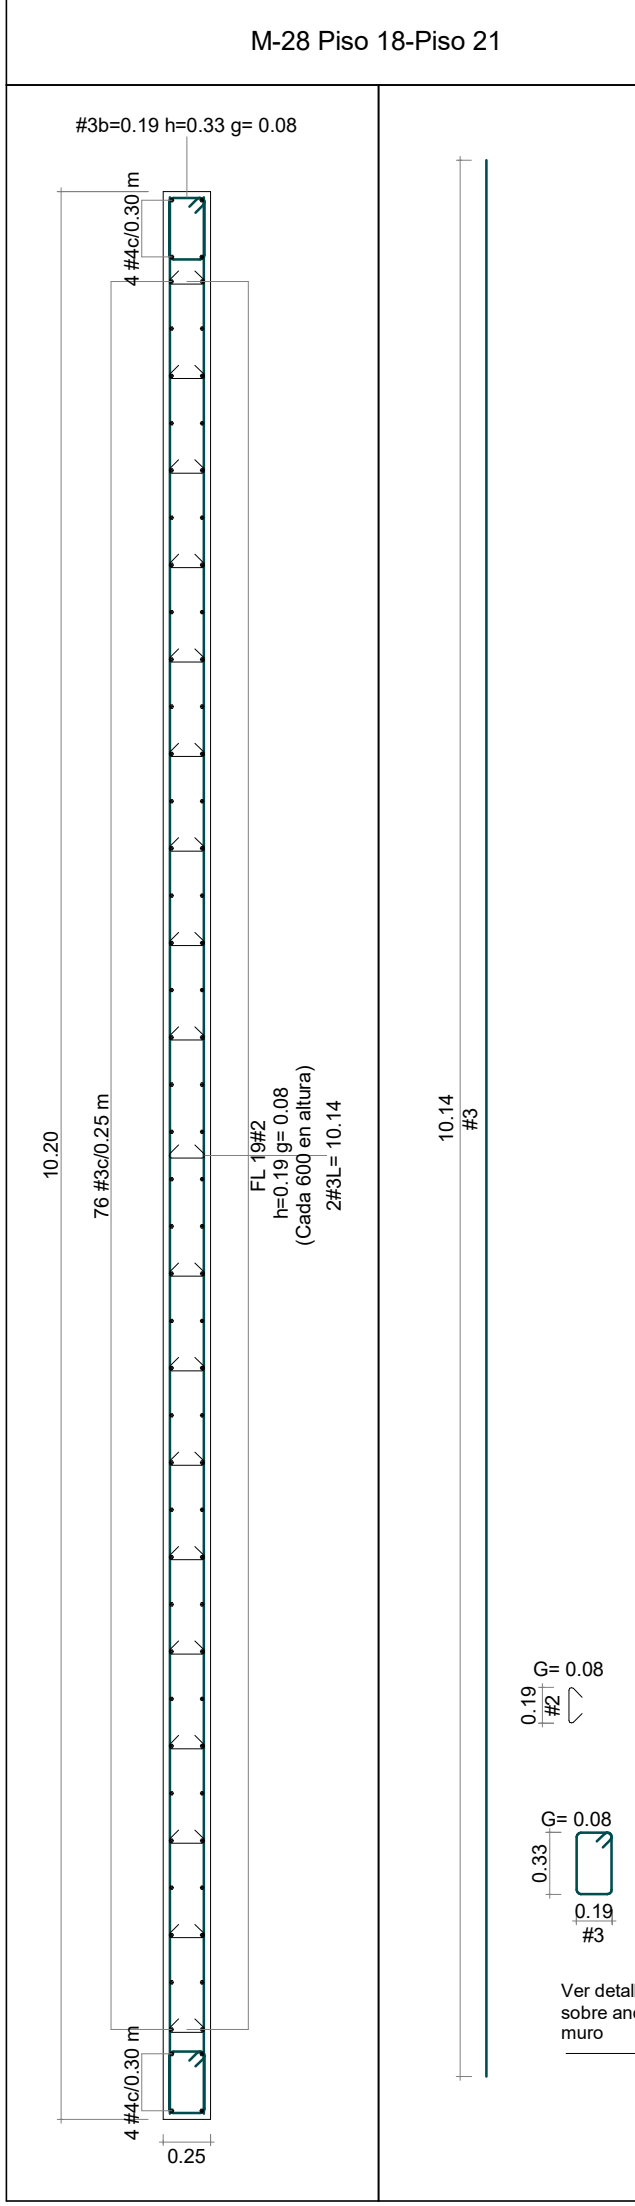
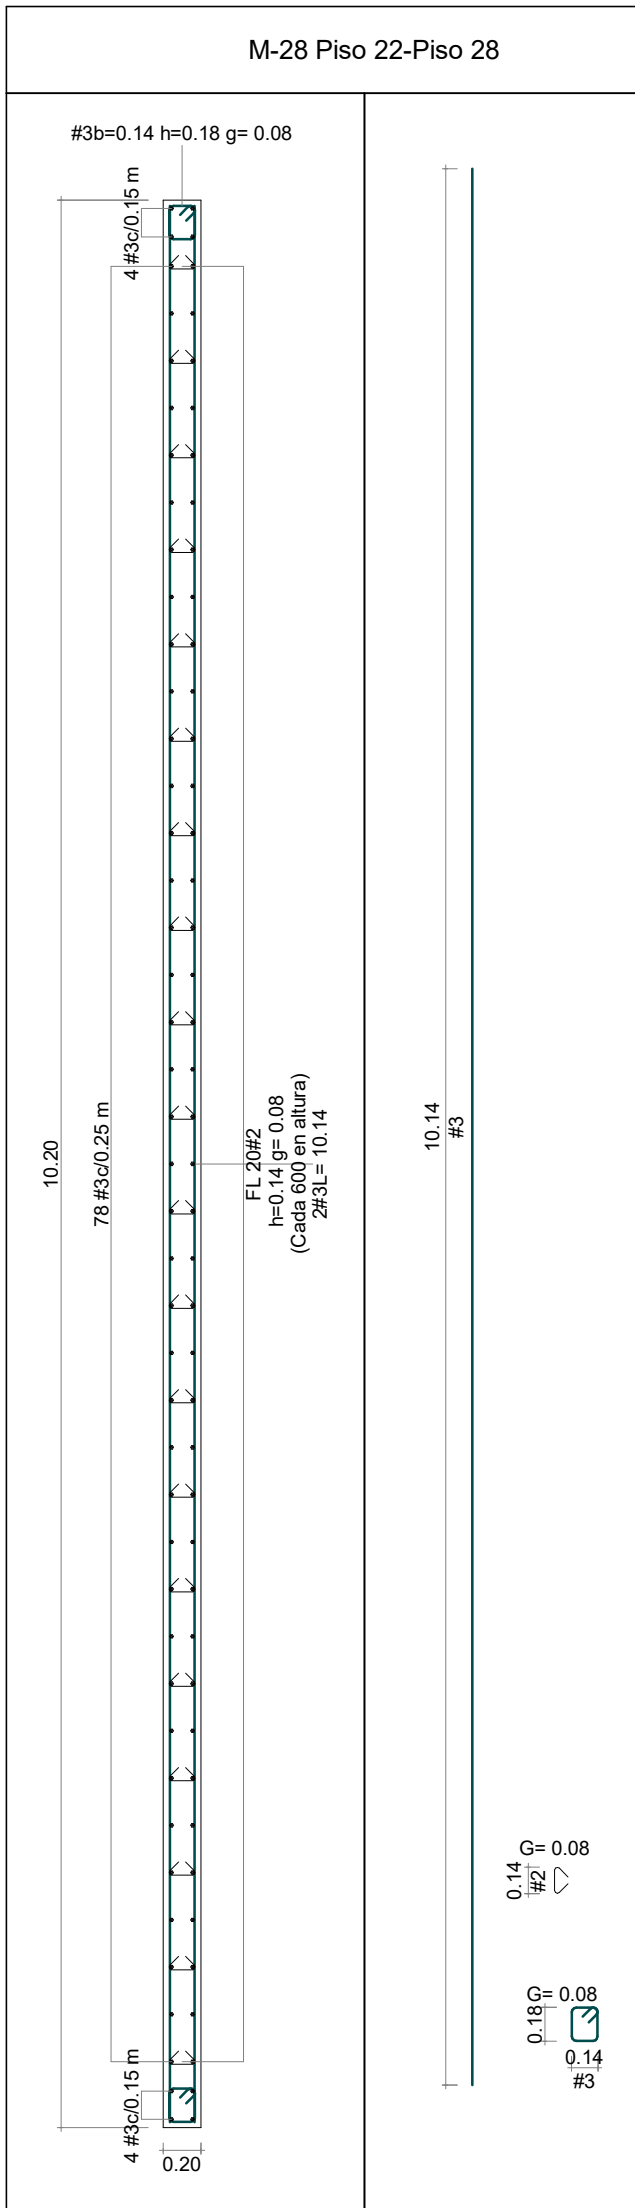
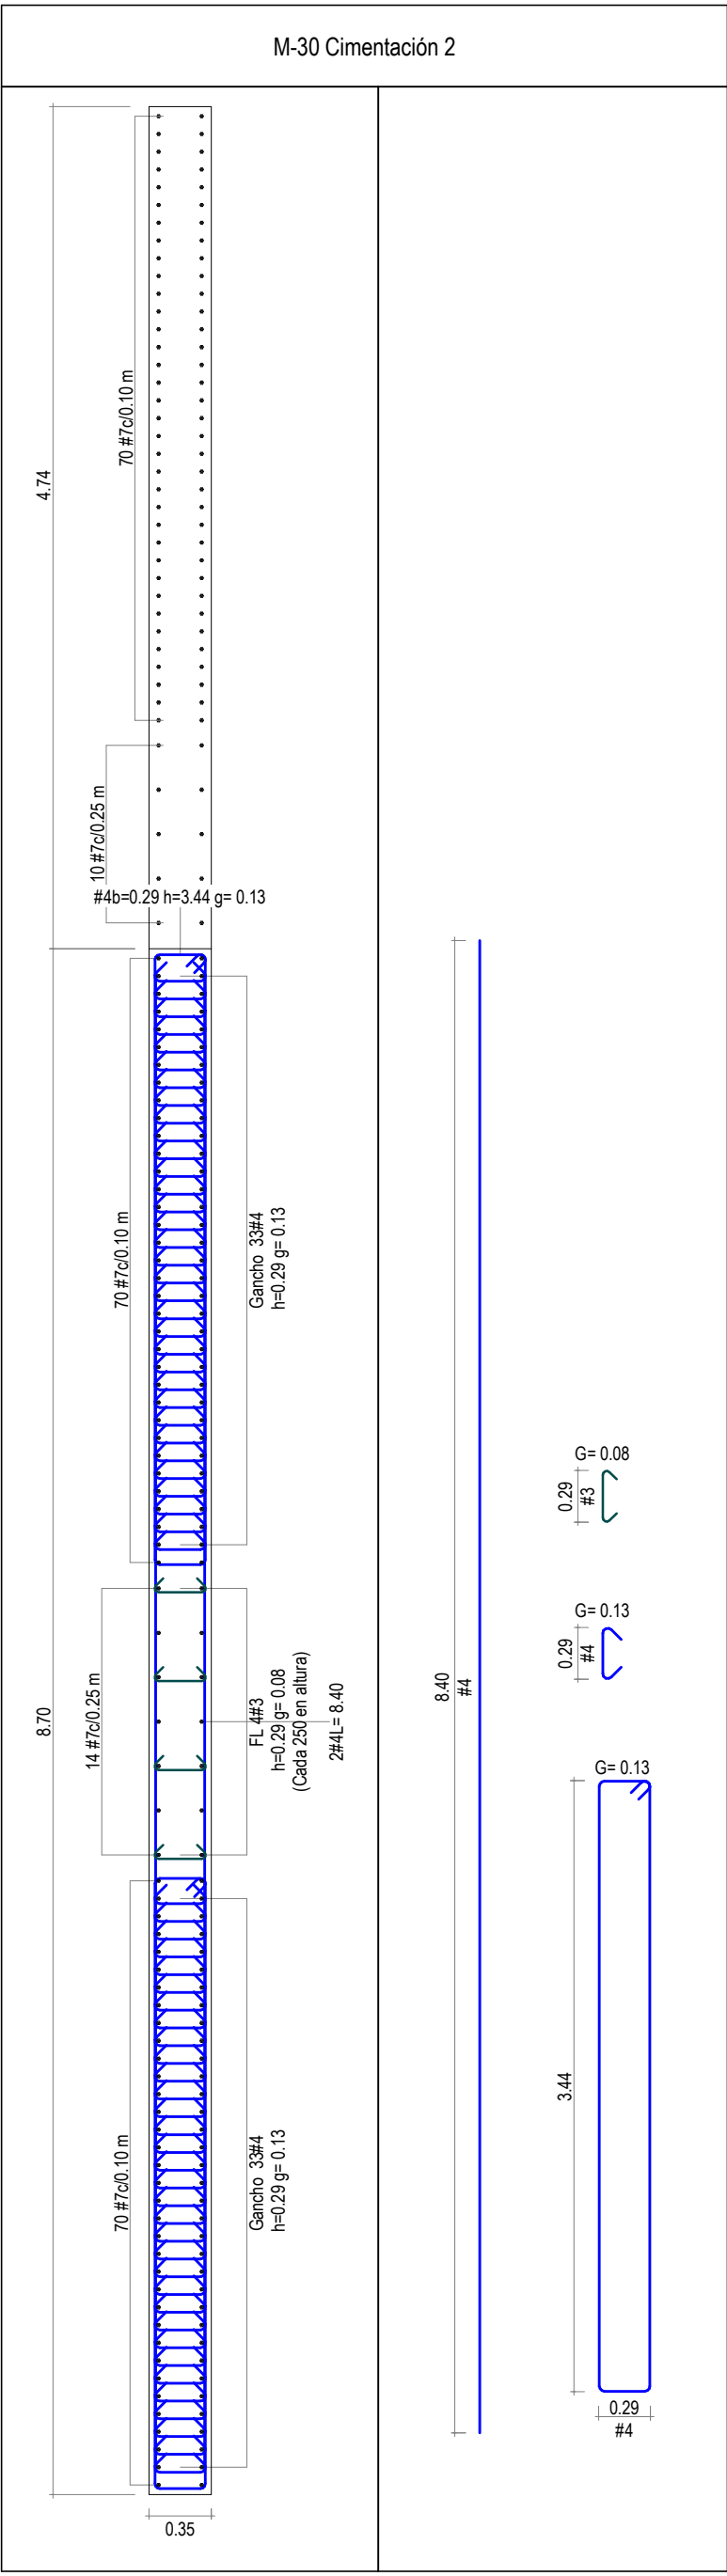


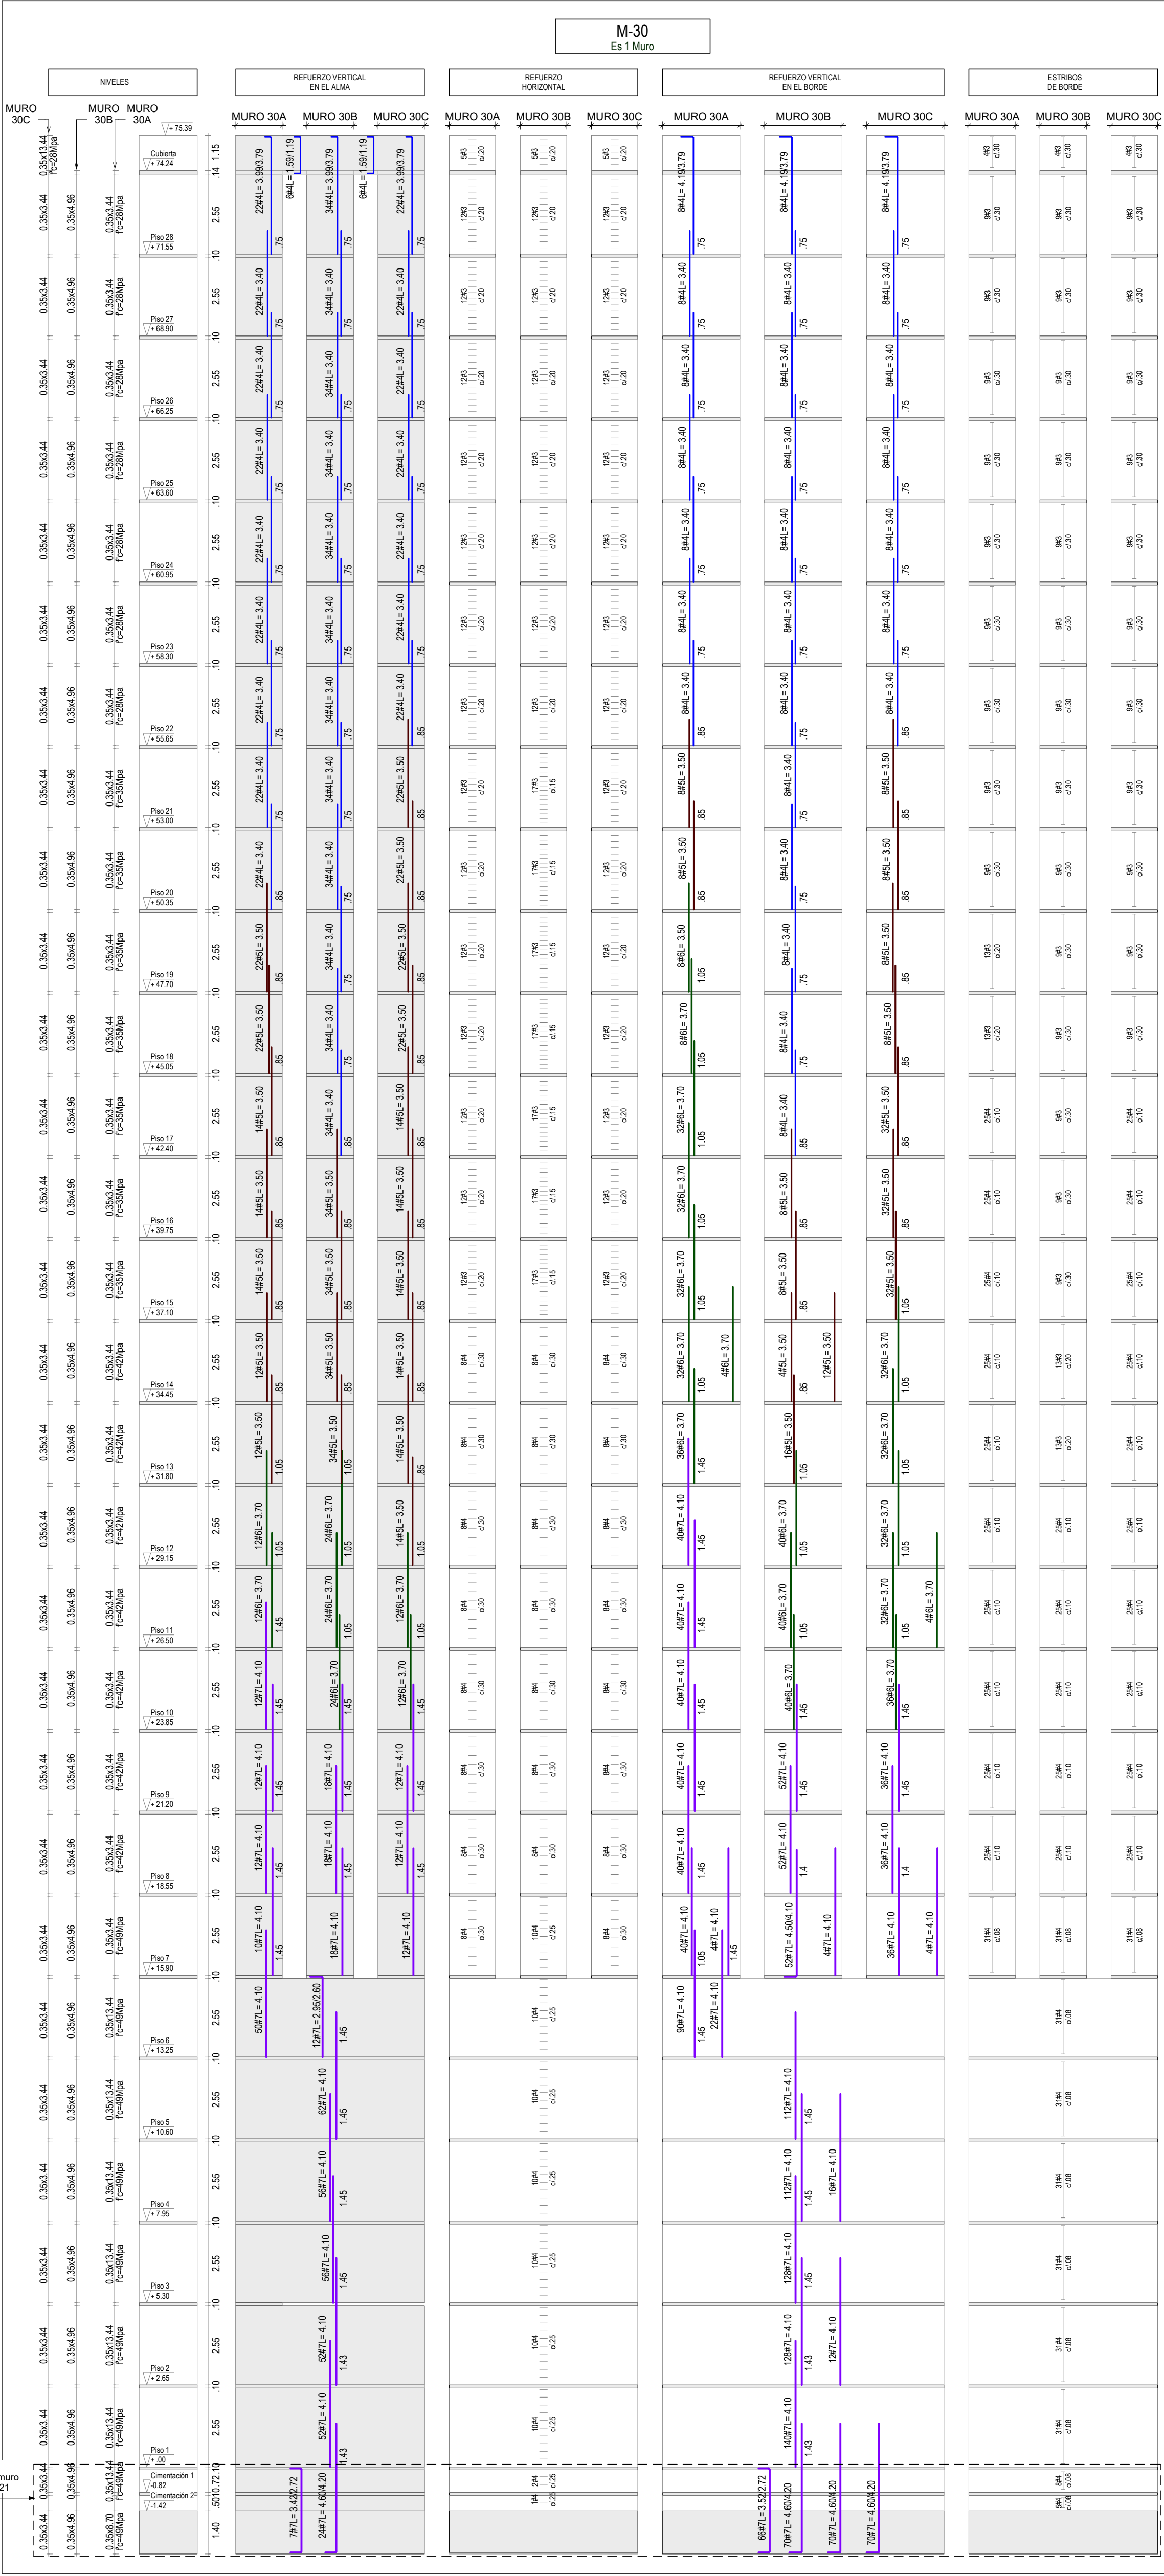

DETALLE SOBRE ANCHO EN MURO M-29

Escala 1 : 25

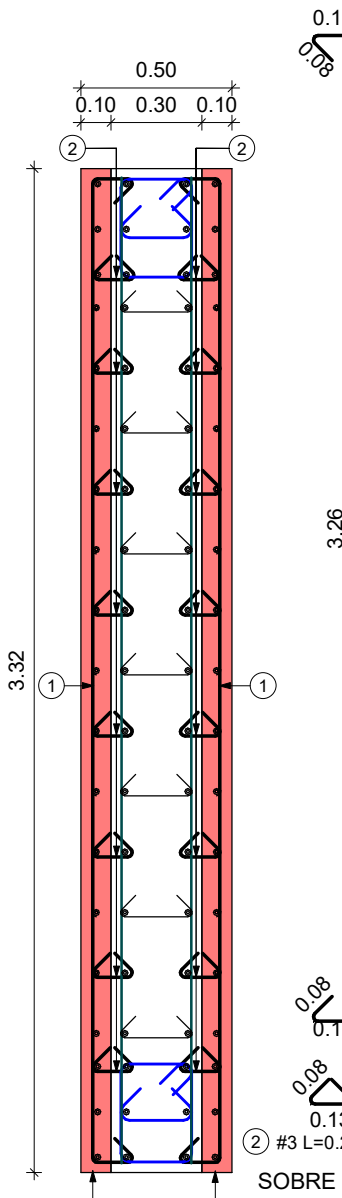

NOTAS:

- Ver detalles generales en el PL.N° 01.02
- Ver detalle de muros en el PL.N° 11.20
- Ver plantas de localización e identificación de muros en los PL. N°03.00-04.00-05.00-06.00-07.00-08.00 y 09.00

MODIFICACIONES	FECHA
Emisión Inicial	28-02-2025
Ajuste longitudes refuerzos y se incluye detalle sobre ancho muro	03-10-2025
Ajuste refuerzo muros	26-02-2026



LA SCALA

LA SCALA_EST_TOR-1

TORRE 1

CALLE 170 CON AV. BOYACA

DESPIECE DE MUROS

LA SCALA_EST_TOR-1_11.19_MUR-D20

REVISOR ESTRUCTURAL
RAMÓN ANDRÉS ALVAREZ MANTILLA
MAT. 25202-346546 CND.