


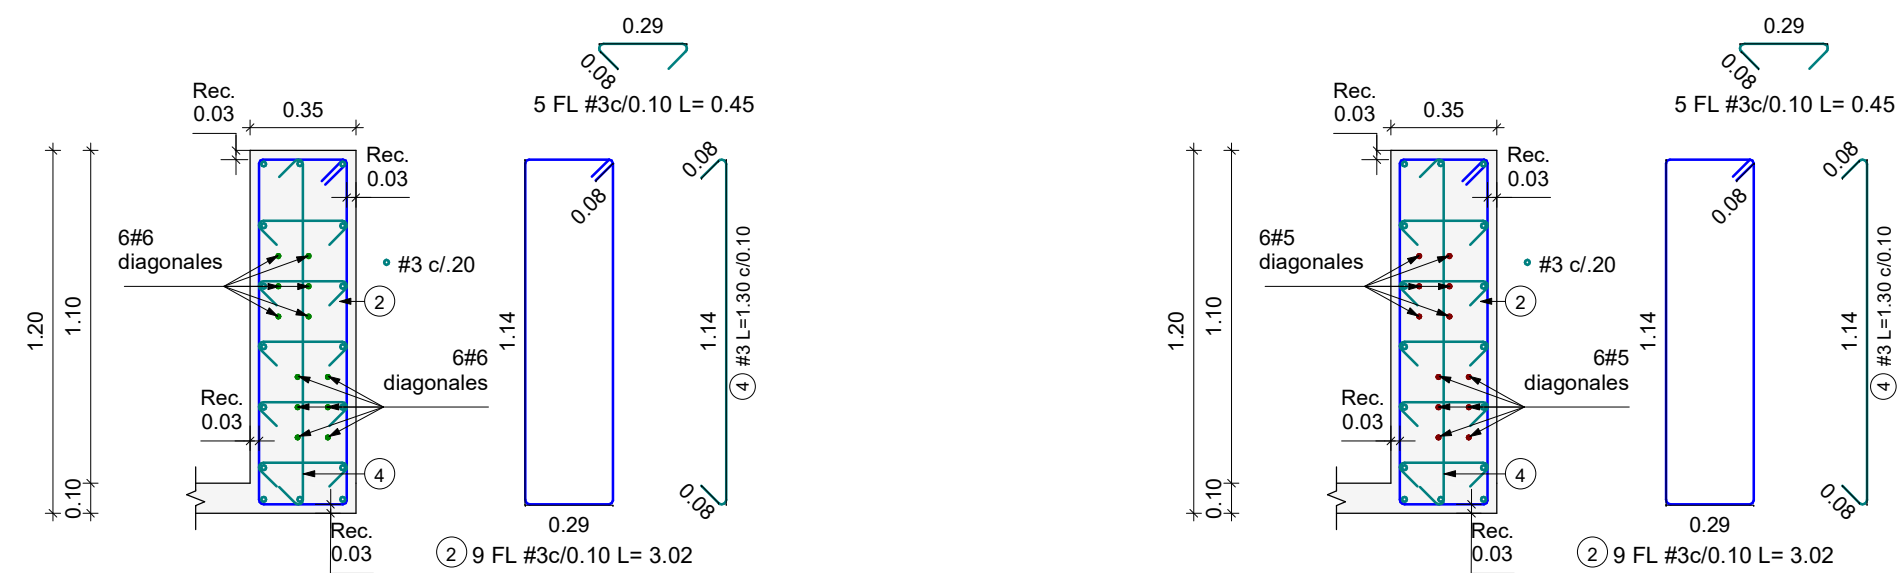

CORTE 1 - 1 VIGA DE ACOPLE TIPO 2 $e=0.35$
Escala 1 : 25



ESCALA 1:125

Aycardi
Estructural

INGENIERO
CARLOS ANDRÉS WILCHES C.

MODIFICACIONES	FECHA
Inicial	28-02-2025
Longitudes refuerzos	03-10-2025
Fuerzo muros	26-02-2026

MODIFICACIONES	FECHA
Emisión Inicial	28-02-2025
Ajuste longitudes refuerzos	03-10-2025
Ajuste refuerzo muros	26-02-2026



DESPIECE DE MUROS

LA SCALA_EST_TOR-1_11.20_MUR-D21

PLANO N°	VERSIÓN :
----------	-----------

3

