


1. Ver detalles generales en el PL.Nº 01.02
2. Ver detalle de muros en el PL.Nº 11.20
3. Ver plantas de localización e identificación de muros en los PL. Nº03.00-04.00-05.00-06.00-07.00-08.00 y 09.00

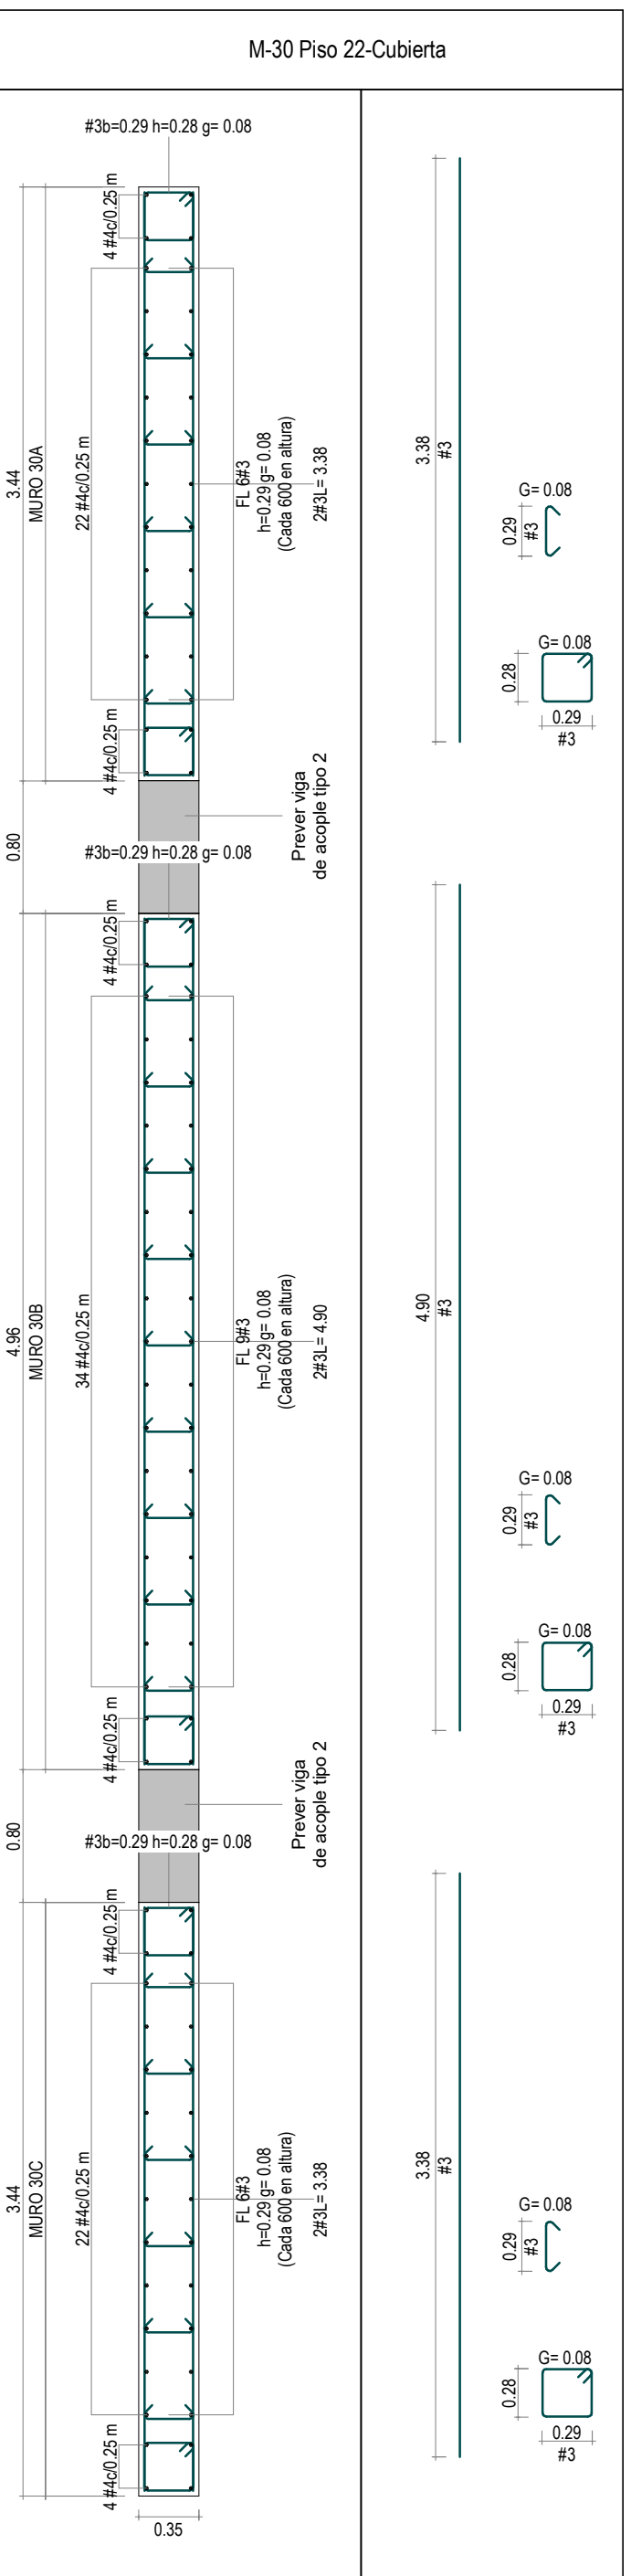

M-31 Piso 22-Cubierta	
	2.42 18 #4@0.30 m 0.15 F5: 500 x 100 cm (Caja 600 en altura) 295kN = 2.36 2.36 #3 0.08 G= 0.08 #2 0.08 0.08
M-31 Piso 15-Piso 21	
	2.42 18 #4@0.30 m 0.15 F5: 500 x 100 cm (Caja 600 en altura) 295kN = 2.36 2.36 #3 0.08 G= 0.08 #2 0.08 0.08
M-31 Piso 11-Piso 14	
	2.42 18 #4@0.30 m 0.15 F5: 500 x 100 cm (Caja 600 en altura) 295kN = 2.36 2.36 #3 0.08 G= 0.08 #2 0.08 0.08
M-31 Piso 8-Piso 10	
	2.42 18 #4@0.30 m 0.15 F5: 500 x 100 cm (Caja 600 en altura) 295kN = 2.36 2.36 #3 0.08 G= 0.08 #2 0.08 0.08
M-31 Cimentación 2-Piso 7	
	2.42 18 #4@0.30 m 0.15 F5: 500 x 100 cm (Caja 600 en altura) 295kN = 2.36 2.36 #3 0.08 G= 0.08 #2 0.08 0.08

Aycardi
Estructural

ROBERTO AYCARDI F
MAT. 2520257258 CNI

MODELADOR
EL CASTELLANOS

MODIFICACIONES	FECHA
Emisión Inicial	28-02-2025
Ajuste longitudes refuerzos y se incluye detalle sobre ancho muro	03-10-2025
Ajuste refuerzo muros	26-02-2026



CALLE 170 CON AV. BOYACA

LA SCALA_EST_TOR-1_11.21_MUR-D22

RAMÓN ÁNDRES ALVAREZ MANTILLA
MAT. 25202-346546 CND.

VERSIÓN

3