


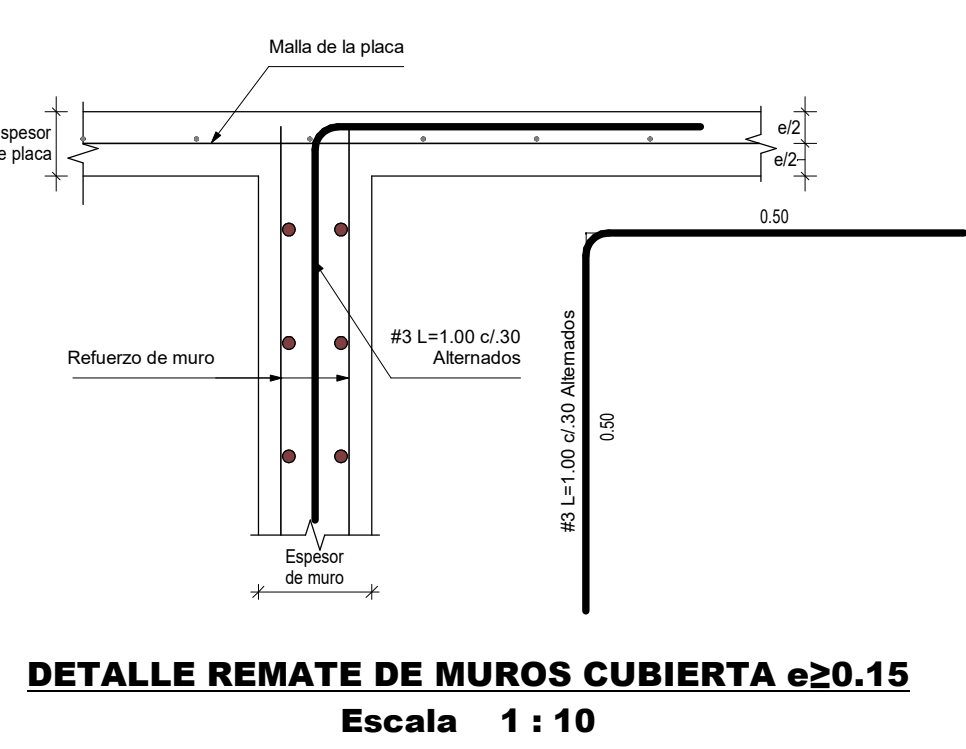


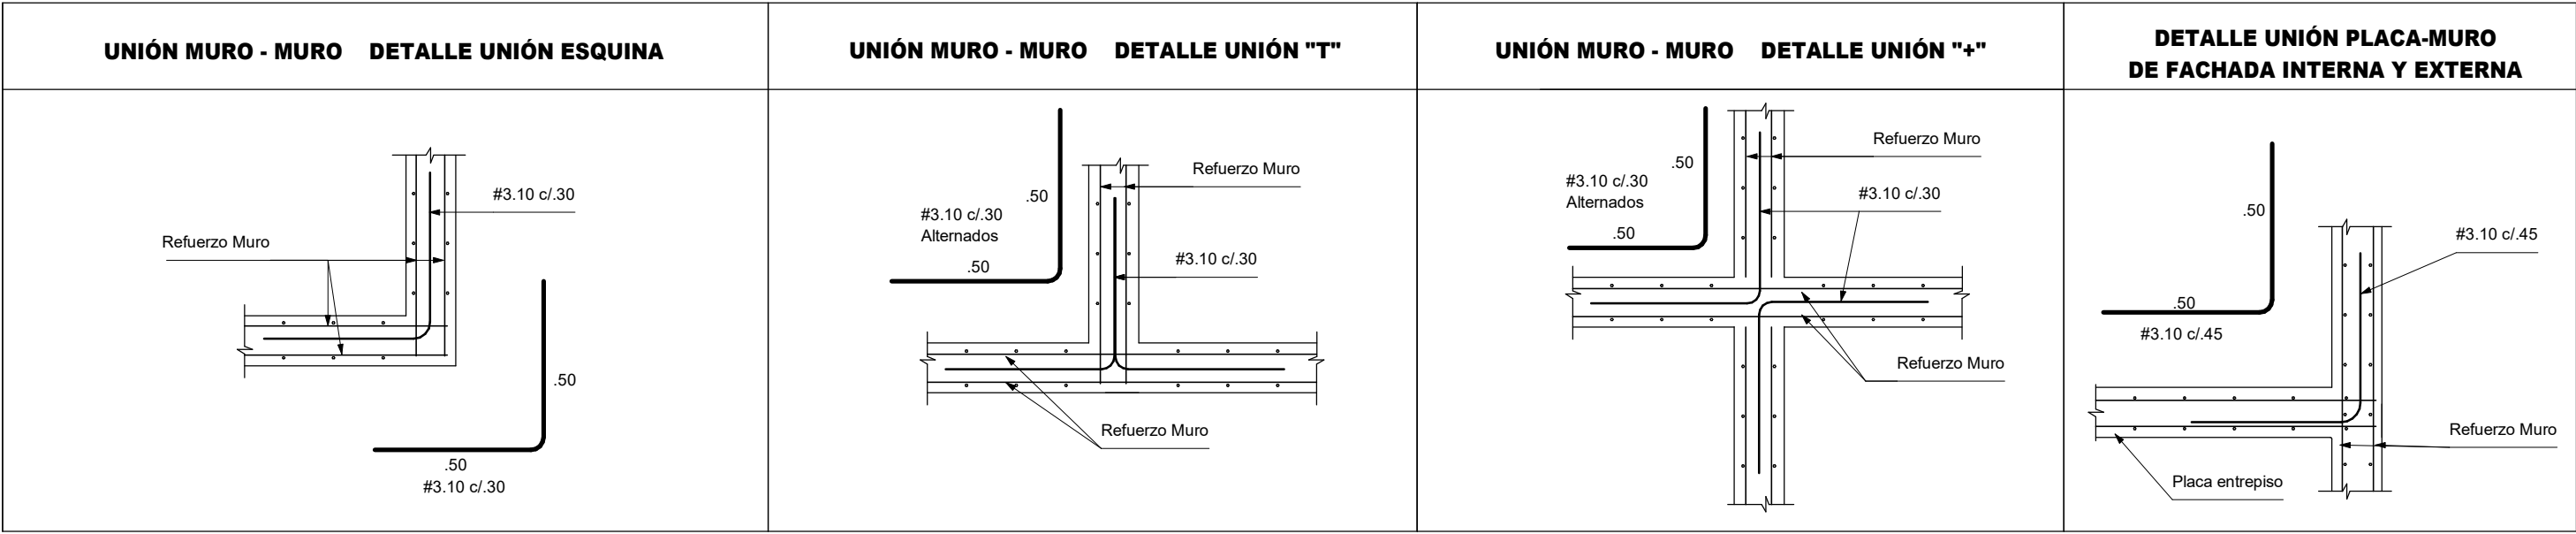


DETALLE REMATE DE MUROS CUBIERTA e≥0.15
Escala 1 : 10

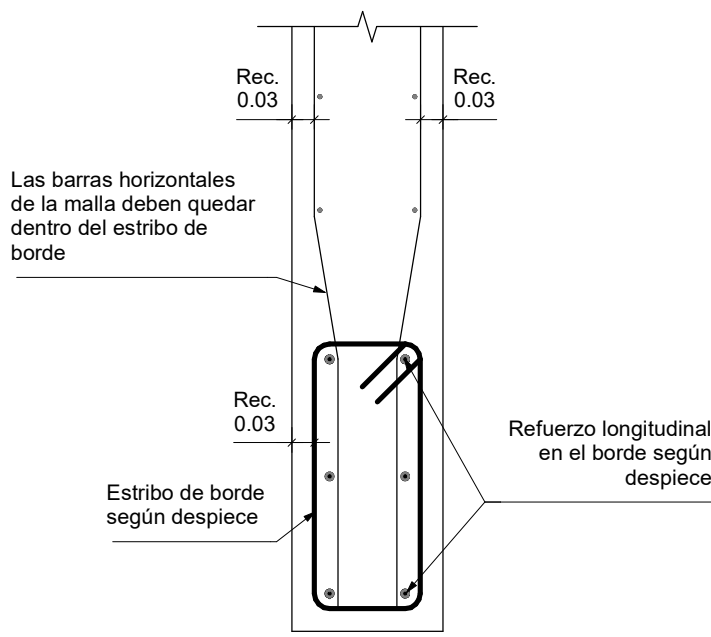


DETALLE ELEMENTO DE BORDE
Escala 1 : 10

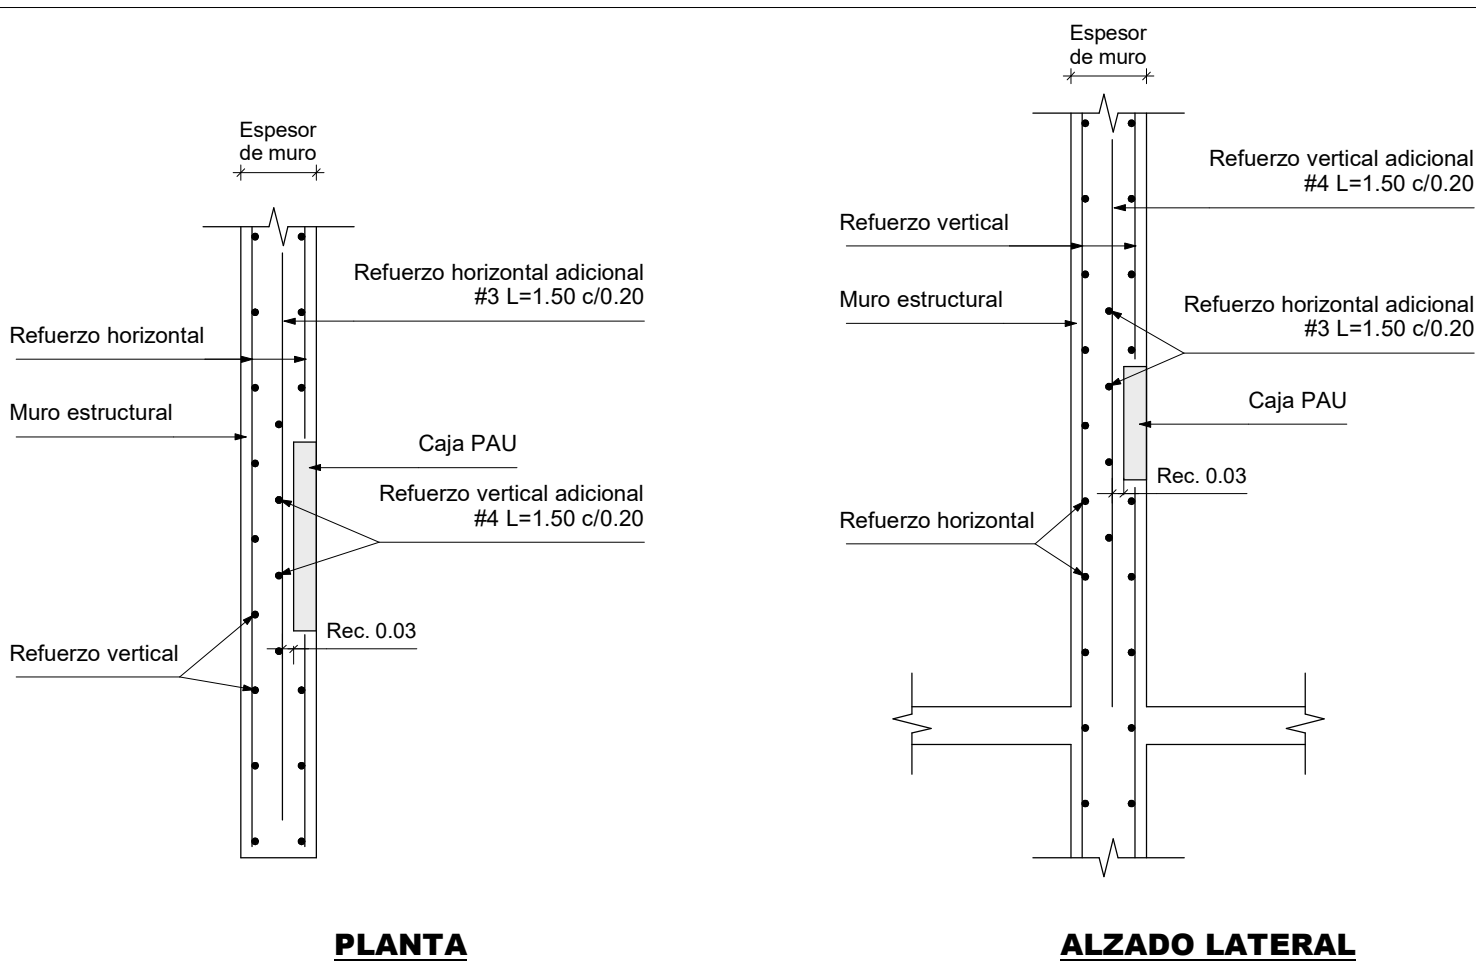


DETALLE REFUERZO ADICIONAL MUROS CON CAJAS PAU
Escala 1 : 20

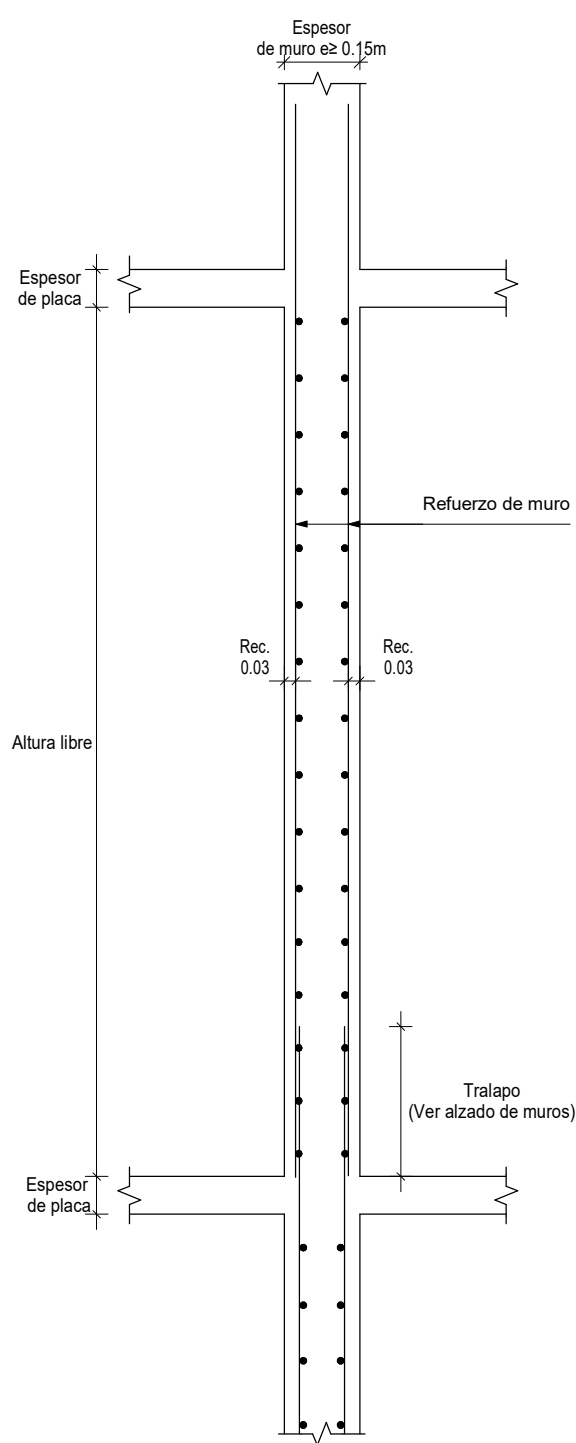


CORTE TRANSVERSAL MUROS e≥0.15m
Escala 1 : 20

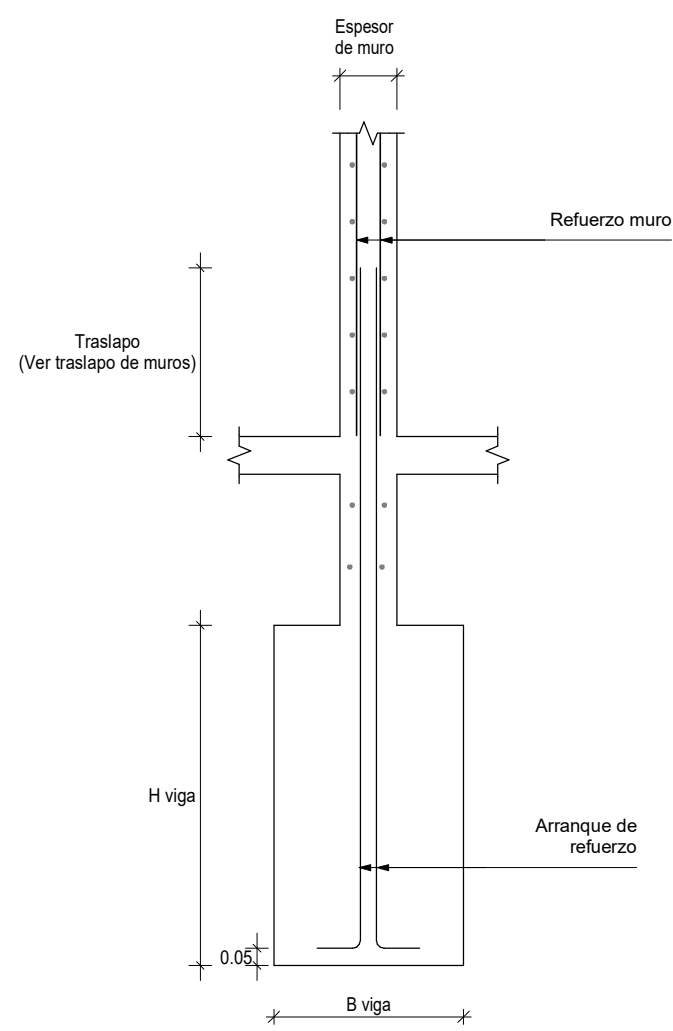

DETALLE ARRANQUE DE VARILLAS
MUROS e≥0.15m
Escala 1 : 20

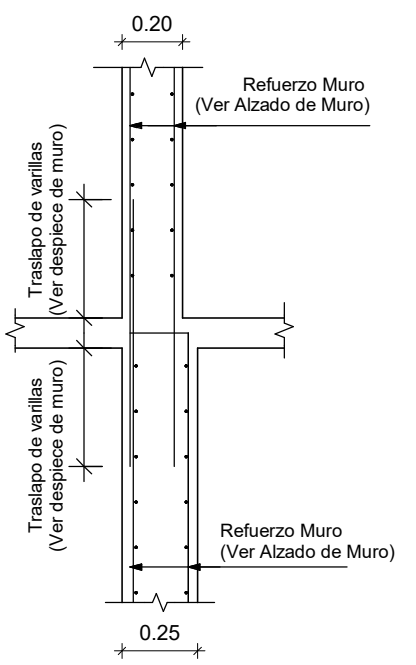


DETALLE 1
Escala 1 : 25

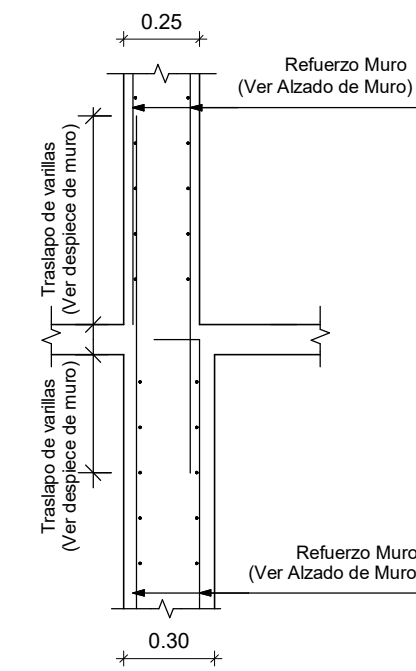


DETALLE 2
Escala 1 : 25

DETALLES CAMBIO DE
ESPESORES DE MUROS

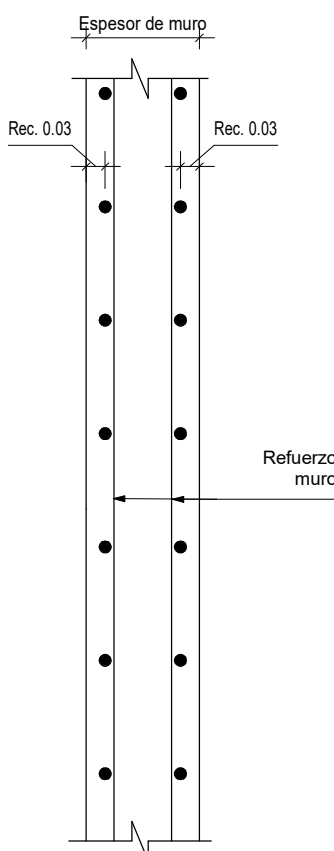

DETALLE RECUBRIMIENTO
EN MUROS e≥0.15m

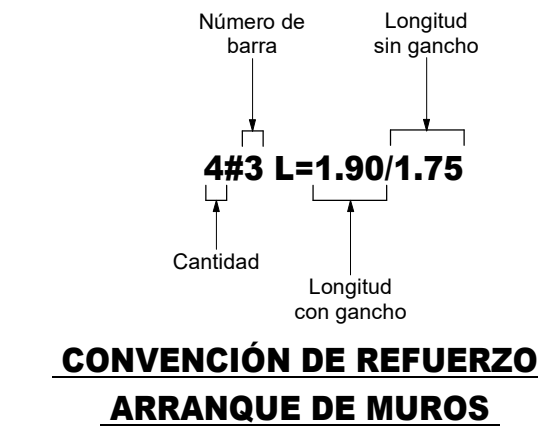

CONVENCIÓN DE REFUERZO
ARRANQUE DE MUROS



LA SCALA

LA SCALA_EST_TOR-1

TORRE 1

CALLE 170 CON AV. BOYACA

DETALLES DE MUROS

LA SCALA_EST_TOR-1_11.22_DT-MUR

REVISOR ESTRUCTURAL
RAMÓN ÁNDRES ALVAREZ MANTILLA
MAT. 25202-346546 CND.

PLANO N° VERSIÓN :

11.22

1

PLANO N° VERSIÓN :
11.22 1

GERENTE DE PROYECTO
ROBERTO AYCARDI F.
MAT. 2520257258 CND

INGENIERO
CARLOS ANDRÉS WILCHES C.

MODELADOR
DANIEL CASTELLANOS

MODIFICACIONES	FECHA
Emisión Inicial	21-02-2025

